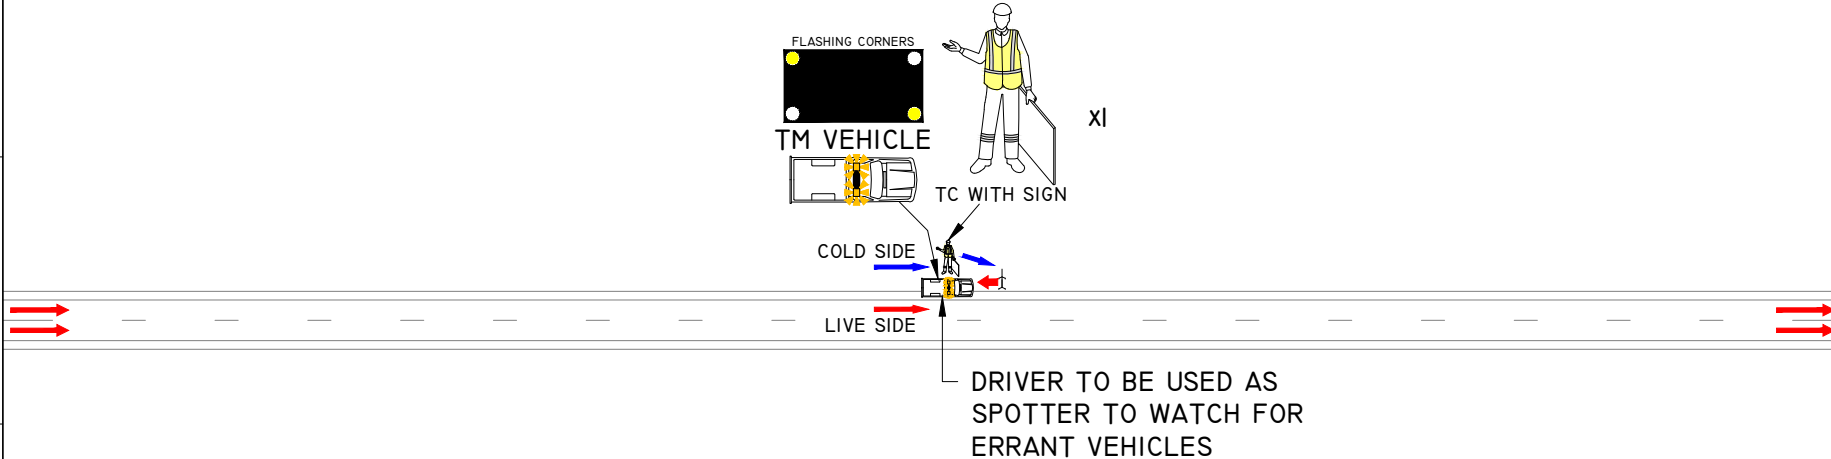
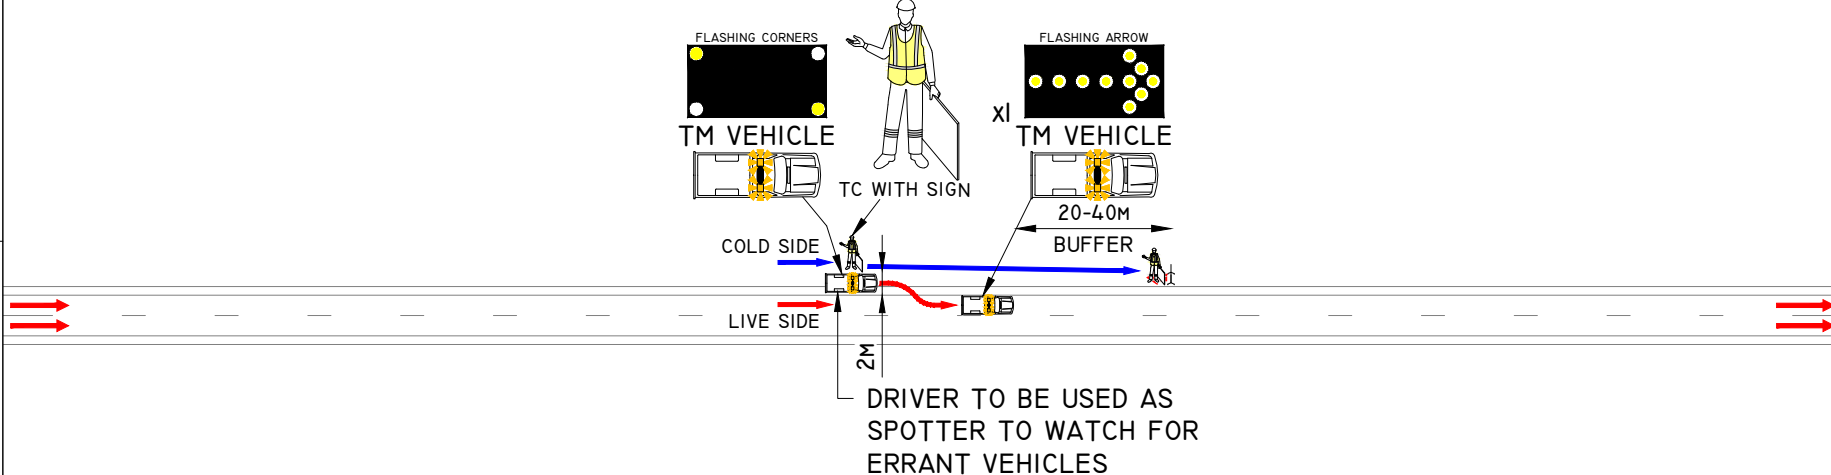
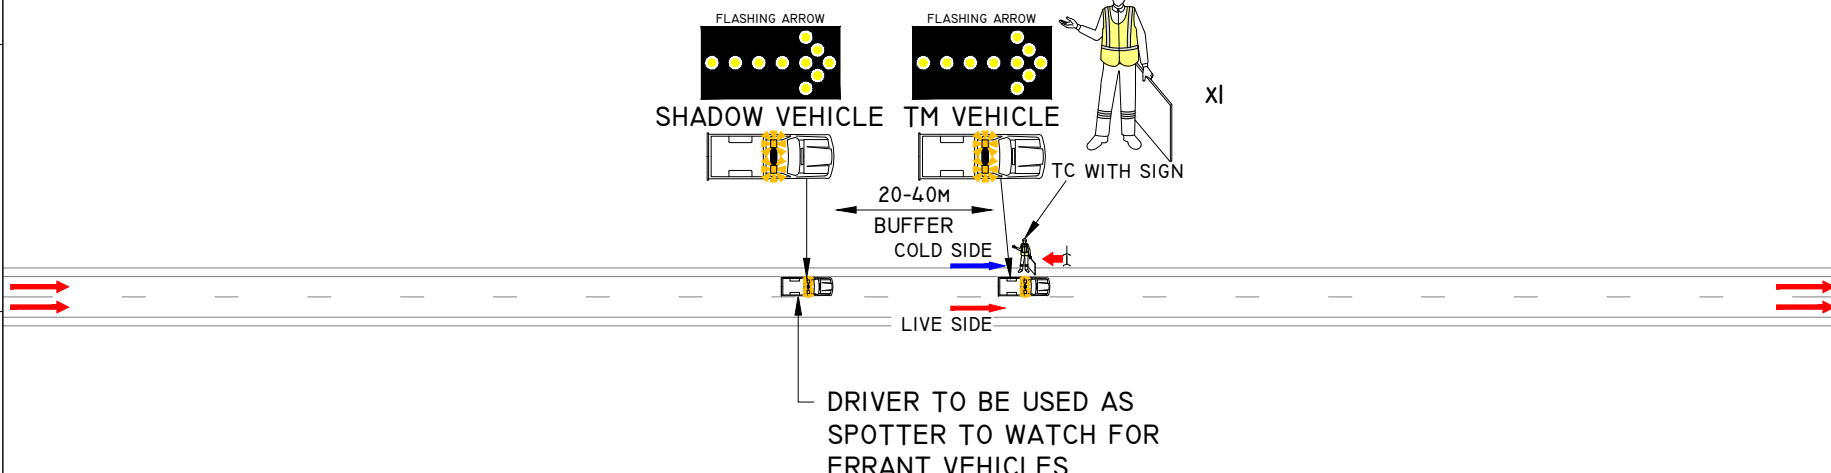


A		B		C		D		E		F		G		H																		
SCENARIO 1:												IMPLEMENTATION PROCEDURES		NOTES																		
												SCENARIO 1: 1. THIS SCENARIO IS TO BE USED ON ROADS WITH A POSTED SPEED LESS THAN 80KM/H. 2. A SHADOW VEHICLE MAY NOT BE REQUIRED SUBJECT TO A ON SITE RISK ASSESSMENT. WHERE A HAZARD IS IDENTIFIED WHICH REQUIRES THE USE OF A SHADOW VEHICLE, THE BELOW SCENARIOS MUST BE USED. 3. TC RETRIEVING SIGNS MUST DO SO FROM THE COLD SIDE OF THE VEHICLE. THE VEHICLE MUST BE PARKED OFF THE ROAD AT ALL TIMES. 4. DRIVER OF TM VEHICLE MUST ACT AS SPOTTER TO WARN OF ERRANT VEHICLES. 5. MUST NOT BE USED WHERE A TMA IS REQUIRED TO SHADOW THE WORKS OPERATION, REFER TO SCENARIO 3.		DOCUMENTATION ON-SITE VARIATIONS MUST BE APPROVED BY THE TRAFFIC MANAGEMENT SUPERVISOR, THAN AN ON-SITE VARIATION MADE AND CHANGES RECORDED IN THE DAILY DAIRY. FOR MORE INFORMATION REFER TO SECTION 9.3 OF THE TMP. 1. TM VEHICLE SHALL BE ANY OF THE FOLLOWING: 1.1. TRAFFIC MANAGEMENT UTE 1.2. UTE WITH ARROW BOARD 1.3. CONE TRUCK 1.4. MR TRUCK 1.5. HR TRUCK 1.6. TRUCK MOUNTED ATTENUATOR 2. THIS DRAWING IS FOR IMPLEMENTATION ONLY AND MUST BE USED IN CONJUNCTION WITH AN APPROVED TRAFFIC MANAGEMENT LAYOUT TGS. 3. THIS DRAWING IS TO BE USED AS A GUIDELINE FOR THE TYPICAL SIGNAGE INSTALLATION AND MAY CHANGE DEPENDING SITE REQUIREMENTS.																		
SCENARIO 2:												SCENARIO 2:		FOR IMPLEMENTATION ONLY LEGEND — EXISTING ROAD → TC MOVEMENTS → TM VEHICLE MOVEMENTS																		
												SCENARIO 2: 1. THIS SCENARIO IS TO BE USED ON ROADS WITH A POSTED SPEED 80KM/H OR GREATER AND A VERGE/SHOULDER WIDE ENOUGH WHERE THE TCs UNLOADING SIGNS CAN MAINTAIN 2M FROM LIVE TRAFFIC LANES. WHERE THIS CANNOT BE MAINTAINED REFER TO THE SCENARIO BELOW. 2. TC RETRIEVING SIGNS MUST DO SO FROM THE COLD SIDE OF THE VEHICLE. THE VEHICLE MUST BE PARKED OFF THE ROAD WHILE THE SINGS ARE UNLOADED. 3. ONCE THE SIGN IS UNLOADED FROM THE VEHICLE, TC TO POSITION 20-40M AHEAD OF VEHICLE AS IT PULLS INTO THE LANE. 4. TM VEHICLE TO BE USED AS SHADOW VEHICLE DURING THE SIGNAGE INSTALLATION. ARROW BOARD ON TM VEHICLE TO BE SWITCHED TO FLASHING ARROW PRIOR TO ENTERING LANE. 5. DRIVER OF TM VEHICLE MUST ACT AS SPOTTER TO WARN OF ERRANT VEHICLES. 6. MUST NOT BE USED WHERE A TMA IS REQUIRED TO SHADOW THE WORKS OPERATION, REFER TO SCENARIO 3.																				
SCENARIO 3:												SCENARIO 3: 1. THIS SCENARIO IS TO BE USED WHERE THE TM VEHICLE MUST PARK IN THE LANE DUE TO A ROAD SIDE HAZARD OR SHALLOW VERGE. 2. TC AND TM VEHICLE TO MAINTAIN 20-40M FROM SHADOW VEHICLE AT ALL TIMES. 3. DRIVER OF SHADOW VEHICLE MUST ACT AS SPOTTER TO WARN OF ERRANT VEHICLES. 4. SHADOW VEHICLE MUST BE REPLACED WITH A TMA ON HIGH SPEED/VOLUME ROADS AND FREEWAYS. REFER TO THE TMP OR MAIN ROADS REQUIREMENTS FOR THE USE OF TRUCK MOUNTED ATTENUATOR POLICY FOR MORE INFORMATION.																				
														 METROPOLITAN REGIONS TRAFFIC MANAGEMENT BRANCH WATERLOO CRESCENT TELEPHONE (08) 138 138 EAST PERTH 6004 <table><tr><td>DATE OF DRAWING 2025 JULY</td><td>SCALE -</td></tr><tr><td>LOCAL GOVERNMENT AUTHORITY -</td><td>POSTED SPEED -</td></tr><tr><td>ROAD AUTHORITY MAIN ROADS WA</td><td>WORKSITE SPEED -</td></tr><tr><td>CHECKED BY TYLER HARTLEY</td><td>SIGNATURE </td></tr><tr><td>ACCREDITATION RTM-0066</td><td rowspan="2">SIGNATURE </td></tr><tr><td>DESIGNED BY MICHAEL REED</td></tr><tr><td>ACCREDITATION AWTM-23-11536-02</td><td></td></tr><tr><td colspan="2">GENERIC TRAFFIC GUIDANCE SCHEME IMPLEMENTATION WORK SETUPS SIGNAGE IMPLEMENTATION MULTI LANE ROAD</td></tr><tr><td>DRAWING NO 0922-01531-IW-002</td><td>REVISION 6</td></tr></table>		DATE OF DRAWING 2025 JULY	SCALE -	LOCAL GOVERNMENT AUTHORITY -	POSTED SPEED -	ROAD AUTHORITY MAIN ROADS WA	WORKSITE SPEED -	CHECKED BY TYLER HARTLEY	SIGNATURE 	ACCREDITATION RTM-0066	SIGNATURE 	DESIGNED BY MICHAEL REED	ACCREDITATION AWTM-23-11536-02		GENERIC TRAFFIC GUIDANCE SCHEME IMPLEMENTATION WORK SETUPS SIGNAGE IMPLEMENTATION MULTI LANE ROAD		DRAWING NO 0922-01531-IW-002	REVISION 6
DATE OF DRAWING 2025 JULY	SCALE -																															
LOCAL GOVERNMENT AUTHORITY -	POSTED SPEED -																															
ROAD AUTHORITY MAIN ROADS WA	WORKSITE SPEED -																															
CHECKED BY TYLER HARTLEY	SIGNATURE 																															
ACCREDITATION RTM-0066	SIGNATURE 																															
DESIGNED BY MICHAEL REED																																
ACCREDITATION AWTM-23-11536-02																																
GENERIC TRAFFIC GUIDANCE SCHEME IMPLEMENTATION WORK SETUPS SIGNAGE IMPLEMENTATION MULTI LANE ROAD																																
DRAWING NO 0922-01531-IW-002	REVISION 6																															
A		B		C		D		E		F		G		H																		