STAGE 1:

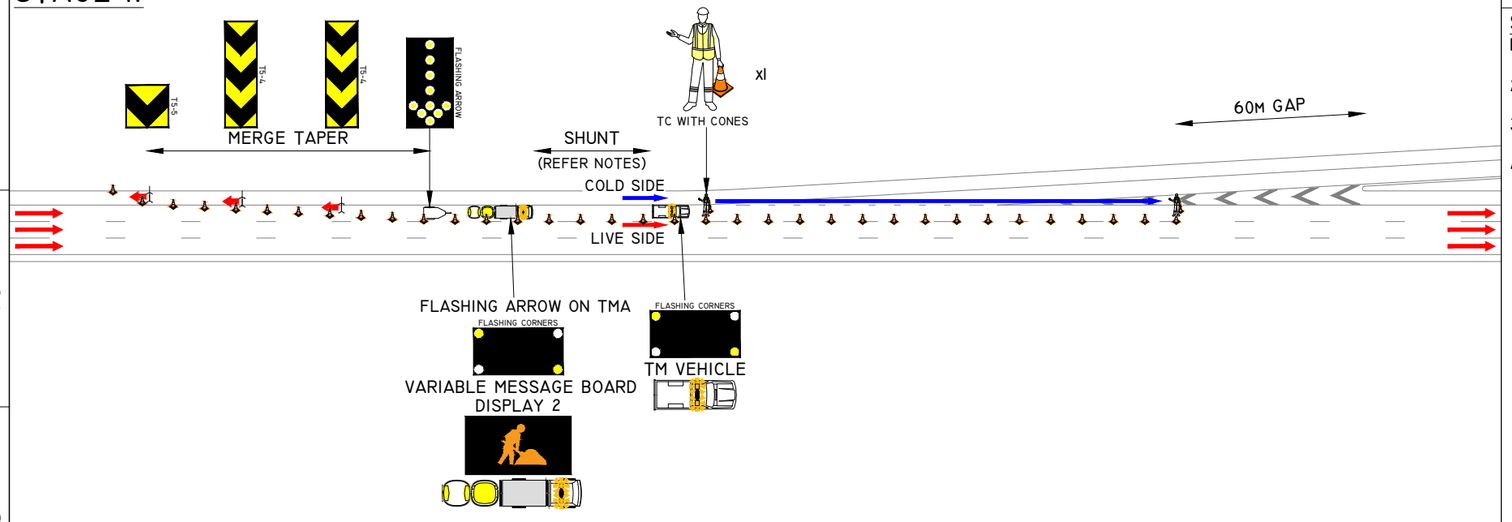

STAGE 2:

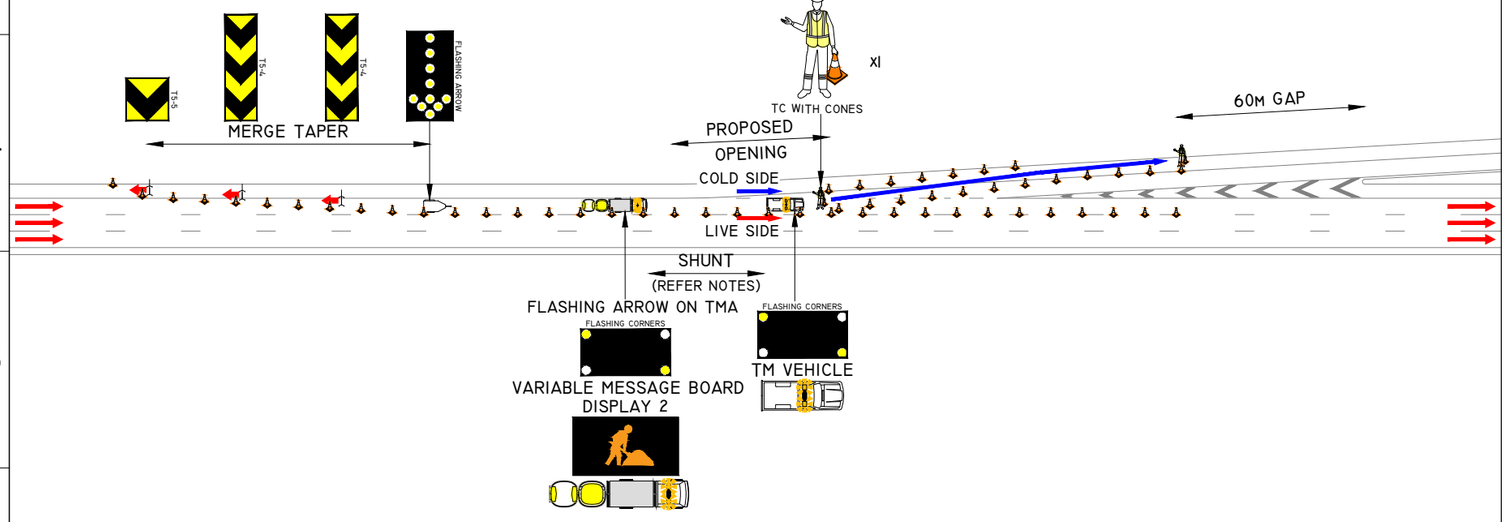

STAGE 3:

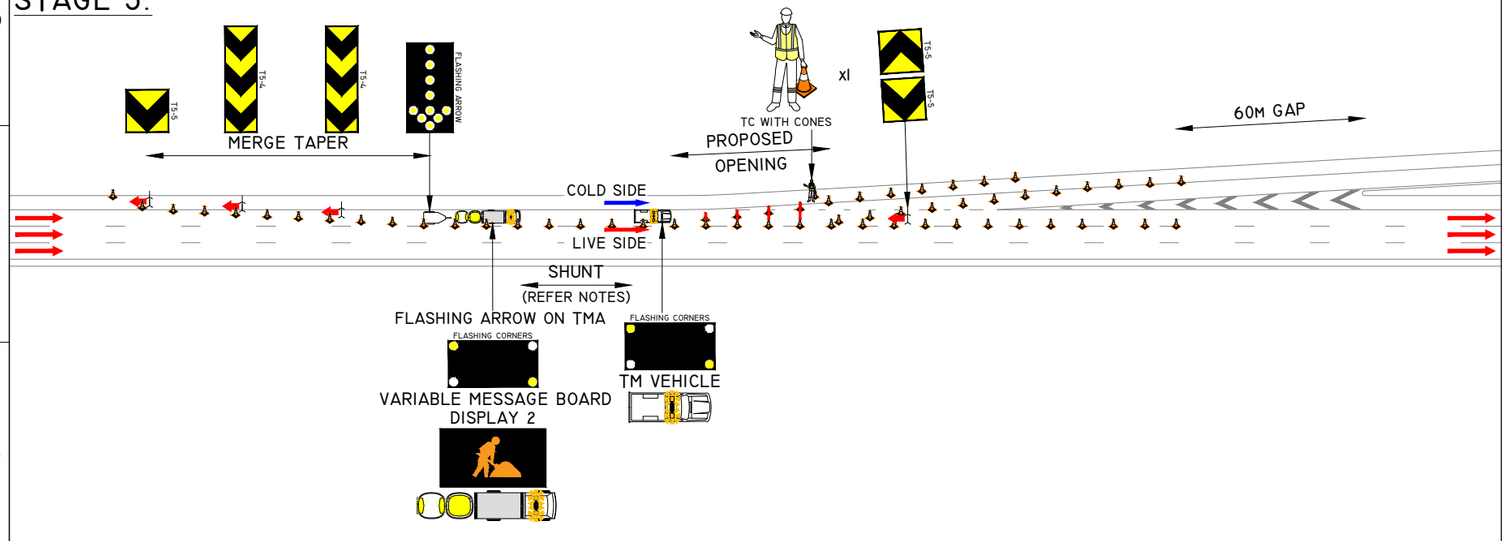

IMPLEMENTATION PROCEDURES

STAGE 1:

1. APPROACH & TERMINATION SIGNAGE AND MERGE TAPER TO BE INSTALLED.
2. WORKS CONVOY TO ENTER INTO LANE CLOSURE TO EXTEND CONES.
3. CONES TO BE EXTENDED PAST RAMP OPENING. WORKS CONVOY TO RESET FOR STAGE 2.
4. TO MAINTAIN AT MINIMUM 60M GAP FROM START OF BULL NOSE TO MAINTAIN ACCESS TO OFF RAMP.

STAGE 2:

1. TC AND TM VEHICLE SHADOWED BY TMA AS REQUIRED TO START LAYING CONES WITHIN CLOSURE FOR RAMP DELINEATION AND LATERAL SHIFT.
2. CONE TO BE INSTALLED TO EXTENT OF MAIN ALIGNMENT DELINEATION.
3. RETAIN 60M GAP PRIOR TO BULL NOSE OF OFF RAMP UNTIL OPENING IS IMPLEMENTED.

STAGE 3:

1. TM VEHICLE TO POSITION AT START OF CHICANE OPENING SHADOWED BY TMA AS REQUIRED.
2. TC INSTALLS SHIFT MARKERS FOR CHICANE OPENING.
3. TC STEPS BACK CONES WITHIN PROPOSED OPENING AREA STARTING FURTHEST FROM WORK CONVOY TOWARDS DIRECTION OF TRAFFIC.

NOTES

DOCUMENTATION

ON-SITE VARIATIONS MUST BE APPROVED BY THE TRAFFIC MANAGEMENT SUPERVISOR, THAN AN ON-SITE VARIATION MADE AND CHANGES RECORDED IN THE DAILY DAIRY. FOR MORE INFORMATION REFER TO SECTION 9.3 OF THE TMP.

1. TM VEHICLE SHALL BE ANY OF THE FOLLOWING:
   - 1.1. TRAFFIC MANAGEMENT UTE
   - 1.2. UTE WITH ARROW BOARD
   - 1.3. CONE TRUCK
   - 1.4. MR TRUCK
   - 1.5. HR TRUCK
   - 1.6. TRUCK MOUNTED ATTENUATOR
2. THIS DRAWING IS FOR IMPLEMENTATION ONLY AND MUST BE USED IN CONJUNCTION WITH AN APPROVED TRAFFIC MANAGEMENT LAYOUT TGS.
3. THIS DRAWING IS TO BE USED AS A GUIDELINE FOR THE TYPICAL FREEWAY CHICANE INSTALLATION AND MAY CHANGE DEPENDING SITE REQUIREMENTS.
4. TMA TO BE USED AS PER THE REQUIREMENTS SET OUT IN THE MAIN ROADS CODE OF PRACTICE AND THE 'MAIN ROADS WA - REQUIREMENTS FOR THE USE OF TRUCK MOUNTED ATTNUATORS (TMAs) IN WA'.
5. REFER TO MANUFACTURING ADVICE FOR SHUNT DISTANCES ON TRUCK MOUNTED ATTENUATORS.
6. APPROACH SIGNAGE IS INDICATIVE OF A GENERIC FREEWAY CHICANE SETUP AND MAY CHANGE ACCORDING TO SPECIFIC PLAN.

FOR IMPLEMENTATION ONLY

LEGEND

- EXISTING ROAD
- PROPOSED CONES
- TC MOVEMENTS

mainroads WESTERN AUSTRALIA

METROPOLITAN REGIONS
TRAFFIC MANAGEMENT BRANCH
WATERLOO CRESCENT EAST PERTH 6004
TELEPHONE (08) 138 138

DATE OF DRAWING: 2025 JULY	SCALE: -
LOCAL GOVERNMENT AUTHORITY: -	POSTED SPEED: -
ROAD AUTHORITY: MAIN ROADS WA	WORKSITE SPEED: -
CHECKED BY: TYLER HARTLEY	SIGNATURE: Tyler Hartley
ACCREDITATION: RTM-0066	
DESIGNED BY: MICHAEL REED	SIGNATURE: MRed
ACCREDITATION: AWTM-23-11536-02	

GENERIC TRAFFIC GUIDANCE SCHEME
IMPLEMENTATION WORK SETUPS
CONTROL OF ACCESS CHICANE
IMPLEMENTATION (1/2)

DRAWING NO: 0922-01531-IW-005	REVISION: 6