


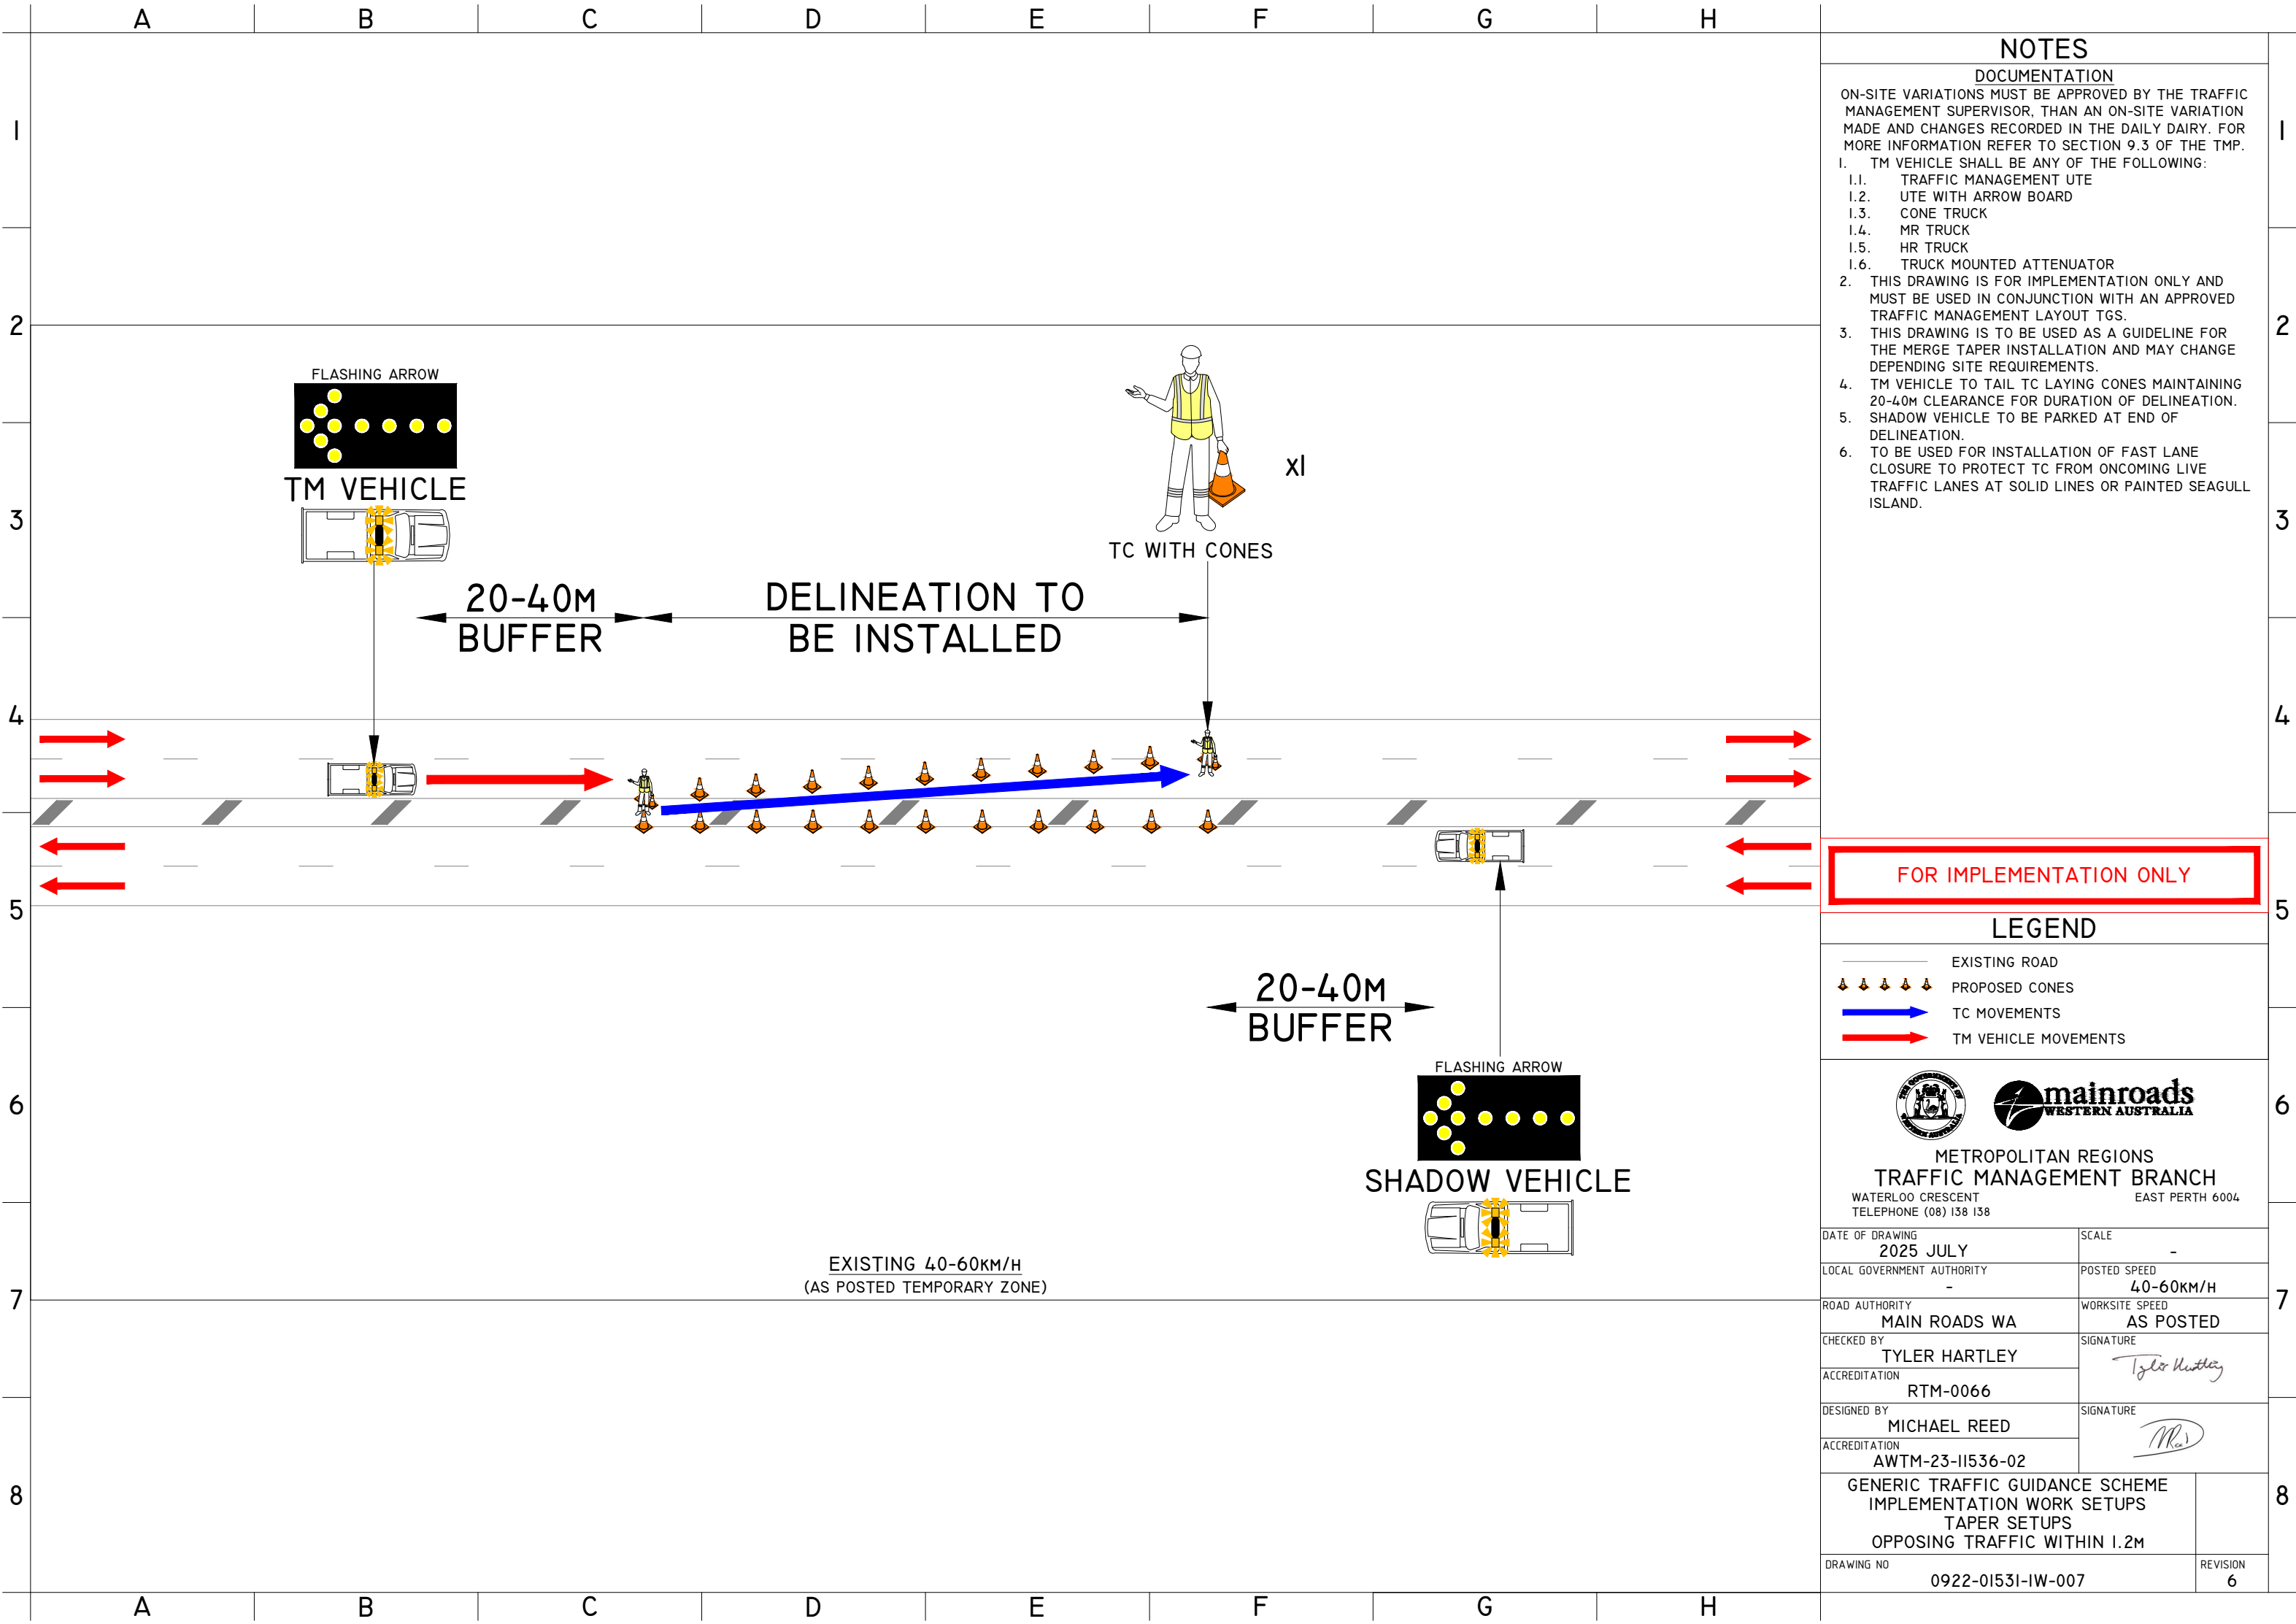

NOTES

DOCUMENTATION

ON-SITE VARIATIONS MUST BE APPROVED BY THE TRAFFIC MANAGEMENT SUPERVISOR, THAN AN ON-SITE VARIATION MADE AND CHANGES RECORDED IN THE DAILY DAIRY. FOR MORE INFORMATION REFER TO SECTION 9.3 OF THE TMP.

1. TM VEHICLE SHALL BE ANY OF THE FOLLOWING:

- 1.1. TRAFFIC MANAGEMENT UTE
- 1.2. UTE WITH ARROW BOARD
- 1.3. CONE TRUCK
- 1.4. MR TRUCK
- 1.5. HR TRUCK
- 1.6. TRUCK MOUNTED ATTENUATOR

2. THIS DRAWING IS FOR IMPLEMENTATION ONLY AND MUST BE USED IN CONJUNCTION WITH AN APPROVED TRAFFIC MANAGEMENT LAYOUT TGS.

3. THIS DRAWING IS TO BE USED AS A GUIDELINE FOR THE MERGE TAPER INSTALLATION AND MAY CHANGE DEPENDING SITE REQUIREMENTS.

4. TM VEHICLE TO TAIL TC LAYING CONES MAINTAINING 20-40M CLEARANCE FOR DURATION OF DELINEATION.

5. SHADOW VEHICLE TO BE PARKED AT END OF DELINEATION.

6. TO BE USED FOR INSTALLATION OF FAST LANE CLOSURE TO PROTECT TC FROM ONCOMING LIVE TRAFFIC LANES AT SOLID LINES OR PAINTED SEAGULL ISLAND.

FOR IMPLEMENTATION ONLY

LEGEND

- EXISTING ROAD
- PROPOSED CONES
- TC MOVEMENTS
- TM VEHICLE MOVEMENTS

METROPOLITAN REGIONS
TRAFFIC MANAGEMENT BRANCH
WATERLOO CRESCENT
TELEPHONE (08) 138 138
EAST PERTH 6004

DATE OF DRAWING 2025 JULY	SCALE -
LOCAL GOVERNMENT AUTHORITY -	POSTED SPEED 40-60KM/H
ROAD AUTHORITY MAIN ROADS WA	WORKSITE SPEED AS POSTED
CHECKED BY TYLER HARTLEY	SIGNATURE
ACCREDITATION RTM-0066	
DESIGNED BY MICHAEL REED	SIGNATURE
ACCREDITATION AWTM-23-11536-02	

GENERIC TRAFFIC GUIDANCE SCHEME
IMPLEMENTATION WORK SETUPS
TAPER SETUPS
OPPOSING TRAFFIC WITHIN 1.2M

DRAWING NO
0922-01531-IW-007

REVISION
6