


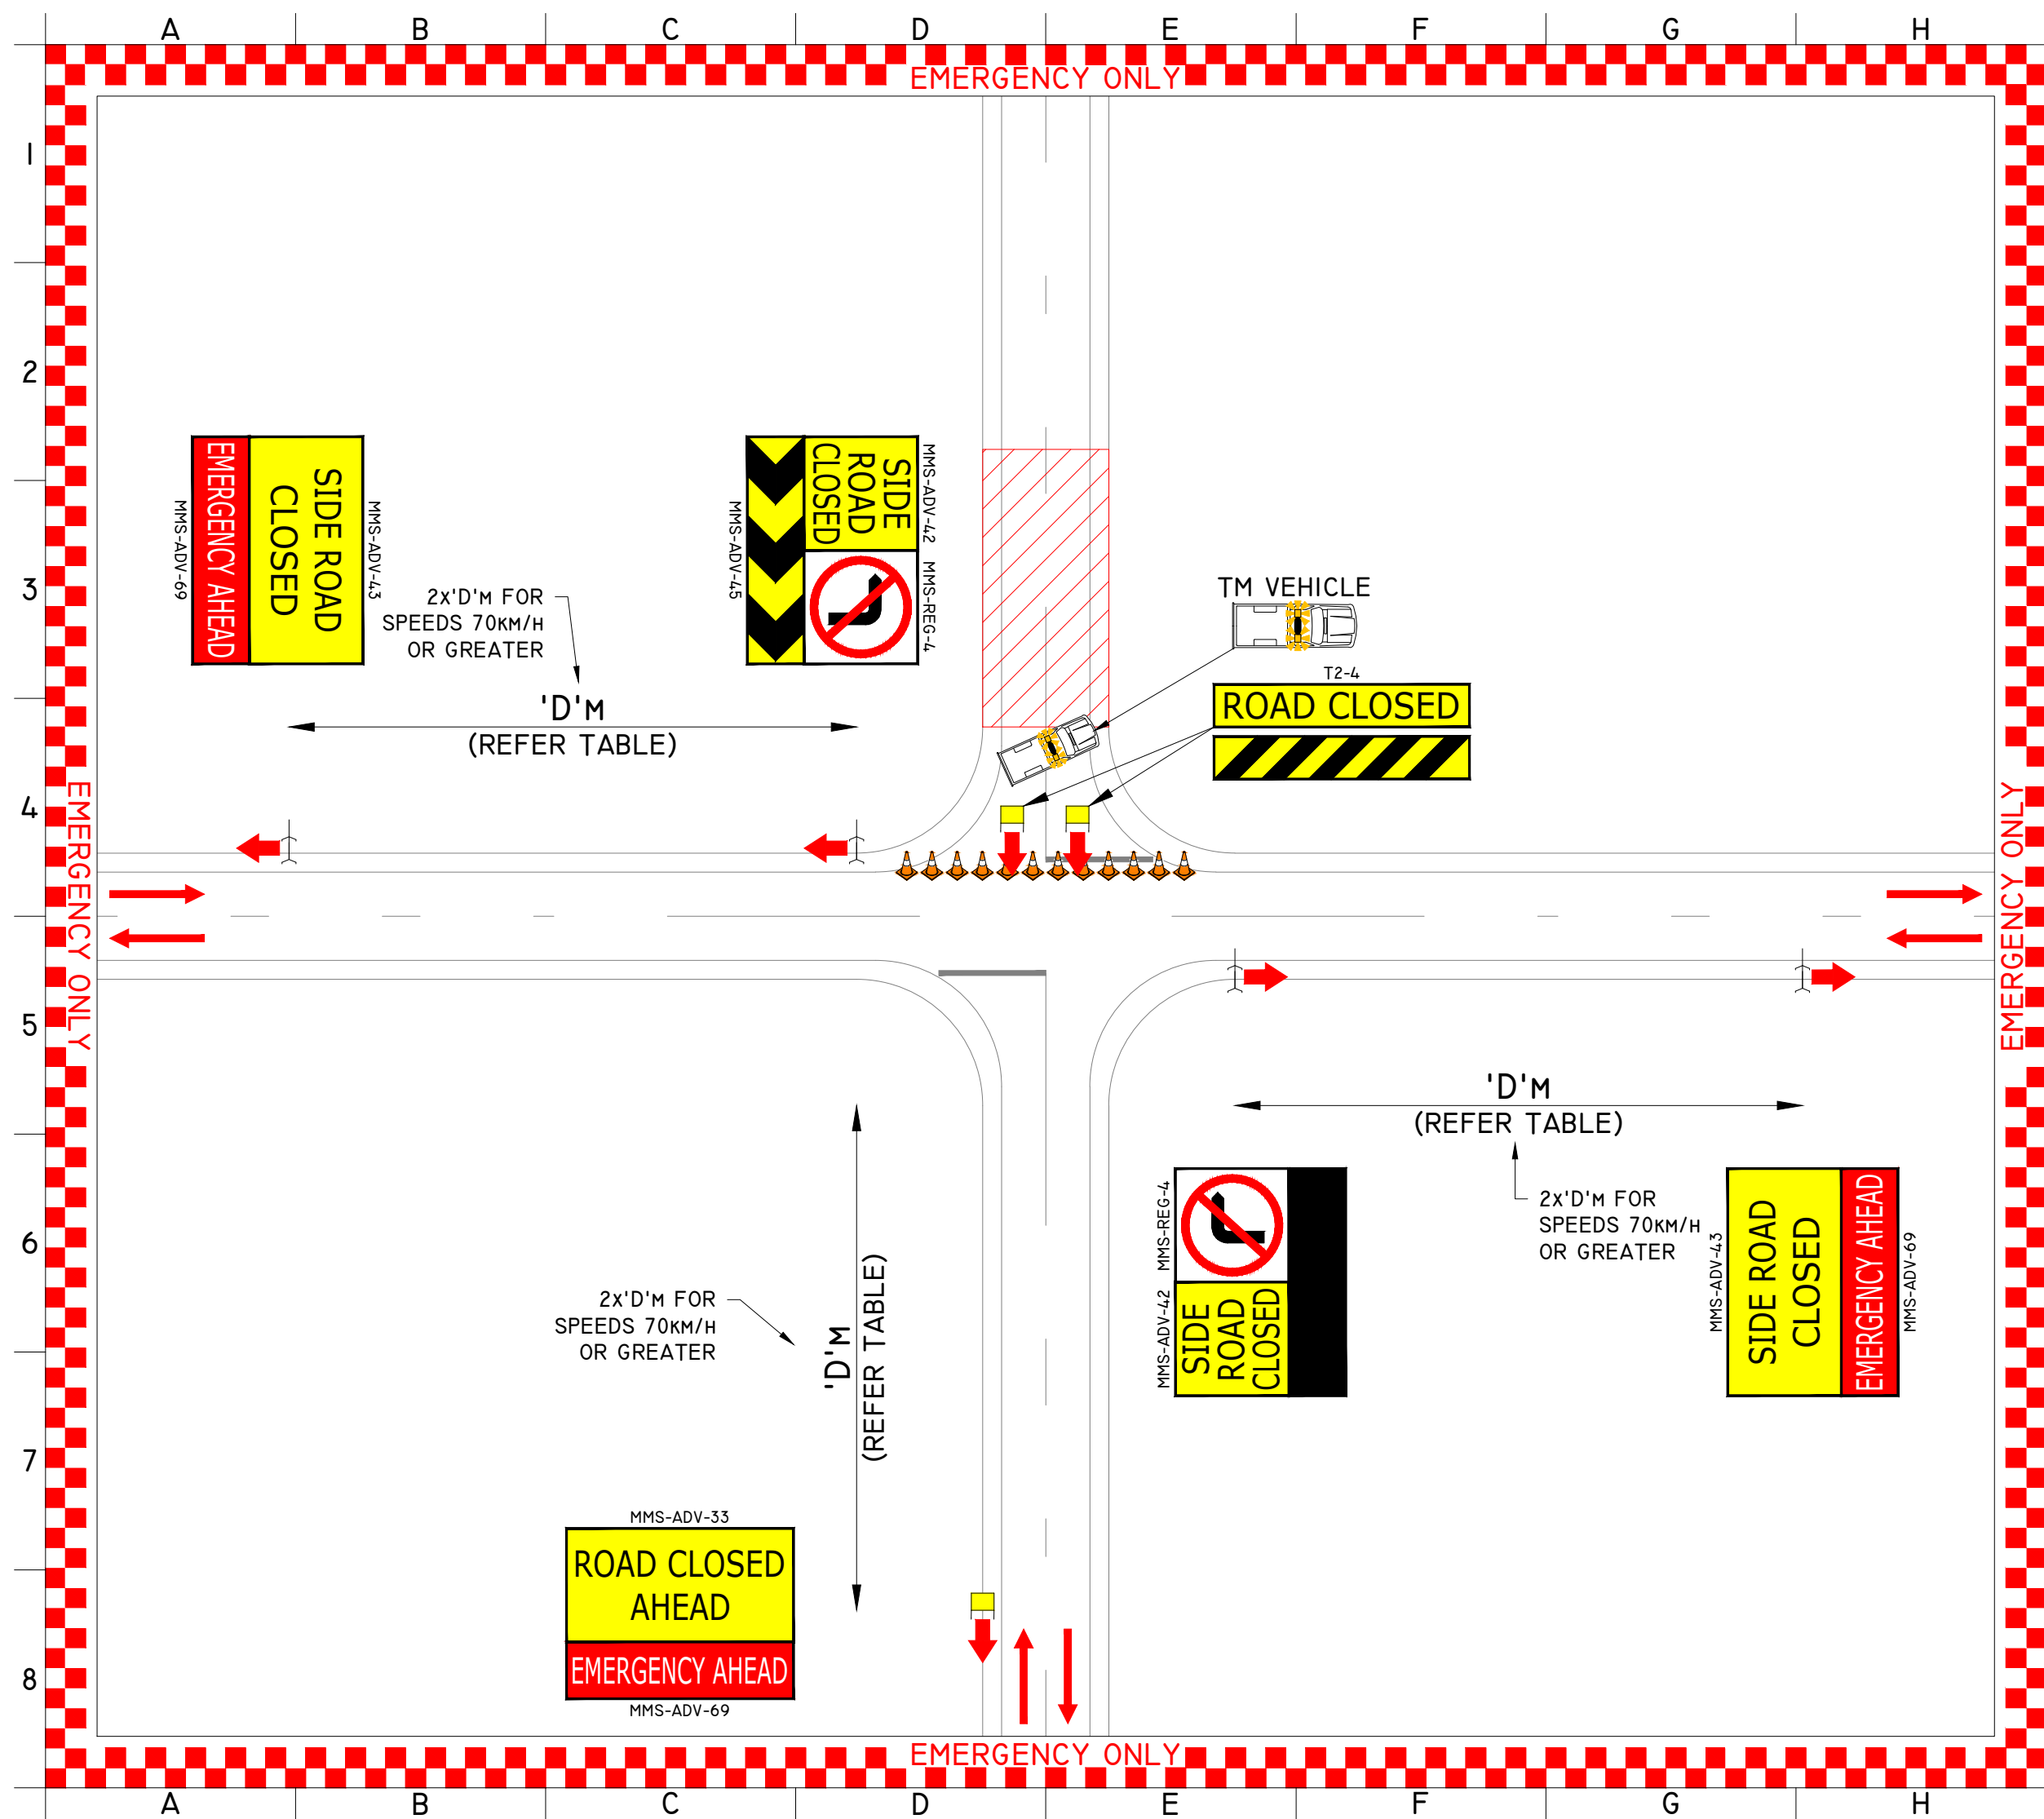

| <b>NOTES</b><br>TOLERANCES:<br>POSITION OF SIGNS:<br>MINIMUM 10% LESS THAN THE DISTANCE OR LENGTHS GIVEN.<br>MAXIMUM 25% MORE THAN THE DISTANCES OR LENGTHS GIVEN.<br>SPACING OF DELINEATING DEVICES:<br>MAXIMUM 10% MORE THAN THE SPACING GIVEN.<br>NO MINIMUM.<br>AGTTM PART 6 SECTION 6.8.<br>DOCUMENTATION<br>ON-SITE VARIATIONS MUST BE APPROVED BY THE TRAFFIC MANAGEMENT SUPERVISOR, THAN AN ON-SITE VARIATION MADE AND CHANGES RECORDED IN THE DAILY DAIRY. FOR MORE INFORMATION REFER TO SECTION 9.3 OF THE TMP.<br>1. PLAN TO BE USED FOR EMERGENCY WORKS ONLY.<br>2. ONE TM VEHICLE WILL BE REQUIRED FOR EVERY CLOSURE POINT AROUND EMERGENCY.<br>3. THIS PLAN MAY BE USED IN CONJUNCTION WITH OTHER EMERGENCY PLANS TO FORM A SAFE BARRIER AROUND THE HAZARD. |   |                    |                                     |                   |                        |                     |                             |   |                           |   |                             |                                   |  |  |
|---|---|--------------------|-------------------------------------|-------------------|------------------------|---------------------|-----------------------------|---|---------------------------|---|-----------------------------|-----------------------------------|--|--|
| <b>TABLES</b><br><b>SIGN SPACING</b><br>AGTTM PART 3 - TABLE 2.2   |   |                    |                                     |                   |                        |                     |                             |   |                           |   |                             |                                   |  |  |
| <table><tr><th>SPEED LIMIT (km/h)</th><th>DISTANCE ('D') (m)</th></tr><tr><td>55 OR LESS</td><td>15</td></tr><tr><td>56 TO 65</td><td>45</td></tr><tr><td>GREATER THAN 65</td><td>EQUAL TO SPEED OF TRAFFIC IN km/h</td></tr></table>   | SPEED LIMIT (km/h)                                                                                 | DISTANCE ('D') (m) | 55 OR LESS                          | 15                | 56 TO 65               | 45                  | GREATER THAN 65             | EQUAL TO SPEED OF TRAFFIC IN km/h                                                                  |                           |   |                             |                                   |  |  |
| SPEED LIMIT (km/h)   | DISTANCE ('D') (m)                                                                                 |                    |                                     |                   |                        |                     |                             |   |                           |   |                             |                                   |  |  |
| 55 OR LESS   | 15                                                                                                 |                    |                                     |                   |                        |                     |                             |   |                           |   |                             |                                   |  |  |
| 56 TO 65   | 45                                                                                                 |                    |                                     |                   |                        |                     |                             |   |                           |   |                             |                                   |  |  |
| GREATER THAN 65   | EQUAL TO SPEED OF TRAFFIC IN km/h                                                                  |                    |                                     |                   |                        |                     |                             |   |                           |   |                             |                                   |  |  |
| <b>LEGEND</b><br>— EXISTING ROAD<br>🚧 PROPOSED CONES<br>HAZARD   |   |                    |                                     |                   |                        |                     |                             |   |                           |   |                             |                                   |  |  |
|  <br>METROPOLITAN REGIONS<br>TRAFFIC MANAGEMENT BRANCH<br>WATERLOO CRESCENT<br>TELEPHONE (08) 138 138<br>EAST PERTH 6004   |   |                    |                                     |                   |                        |                     |                             |   |                           |   |                             |                                   |  |  |
| <table><tr><td>DATE OF DRAWING<br/>2025 JULY</td><td>SCALE<br/>-</td></tr><tr><td>STRAIGHT LINE KILOMETERS (SLK)<br/>-</td><td>POSTED SPEED<br/>-</td></tr><tr><td>ROAD AUTHORITY<br/>MRWA</td><td>WORKSITE SPEED<br/>-</td></tr><tr><td>CHECKED BY<br/>TYLER HARTLEY</td><td>SIGNATURE<br/></td></tr><tr><td>ACCREDITATION<br/>RTM-0066</td><td rowspan="2">SIGNATURE<br/></td></tr><tr><td>DESIGNED BY<br/>MICHAEL REED</td></tr><tr><td>ACCREDITATION<br/>AWTM-23-11536-02</td><td></td></tr></table>                                                                                        | DATE OF DRAWING<br>2025 JULY                                                                       | SCALE<br>-         | STRAIGHT LINE KILOMETERS (SLK)<br>- | POSTED SPEED<br>- | ROAD AUTHORITY<br>MRWA | WORKSITE SPEED<br>- | CHECKED BY<br>TYLER HARTLEY | SIGNATURE<br> | ACCREDITATION<br>RTM-0066 | SIGNATURE<br> | DESIGNED BY<br>MICHAEL REED | ACCREDITATION<br>AWTM-23-11536-02 |  |  |
| DATE OF DRAWING<br>2025 JULY   | SCALE<br>-                                                                                         |                    |                                     |                   |                        |                     |                             |   |                           |   |                             |                                   |  |  |
| STRAIGHT LINE KILOMETERS (SLK)<br>-   | POSTED SPEED<br>-                                                                                  |                    |                                     |                   |                        |                     |                             |   |                           |   |                             |                                   |  |  |
| ROAD AUTHORITY<br>MRWA   | WORKSITE SPEED<br>-                                                                                |                    |                                     |                   |                        |                     |                             |   |                           |   |                             |                                   |  |  |
| CHECKED BY<br>TYLER HARTLEY   | SIGNATURE<br> |                    |                                     |                   |                        |                     |                             |   |                           |   |                             |                                   |  |  |
| ACCREDITATION<br>RTM-0066   | SIGNATURE<br> |                    |                                     |                   |                        |                     |                             |   |                           |   |                             |                                   |  |  |
| DESIGNED BY<br>MICHAEL REED   |   |                    |                                     |                   |                        |                     |                             |   |                           |   |                             |                                   |  |  |
| ACCREDITATION<br>AWTM-23-11536-02   |   |                    |                                     |                   |                        |                     |                             |   |                           |   |                             |                                   |  |  |
| GENERIC TRAFFIC GUIDANCE SCHEME<br>EMERGENCY WORK SCENARIOS<br>MINOR 4-WAY INTERSECTION<br>ROAD CLOSURE POINT   |   |                    |                                     |                   |                        |                     |                             |   |                           |   |                             |                                   |  |  |
| DRAWING NO<br>0922-01531-EW-001   | REVISION<br>6                                                                                      |                    |                                     |                   |                        |                     |                             |   |                           |   |                             |                                   |  |  |