


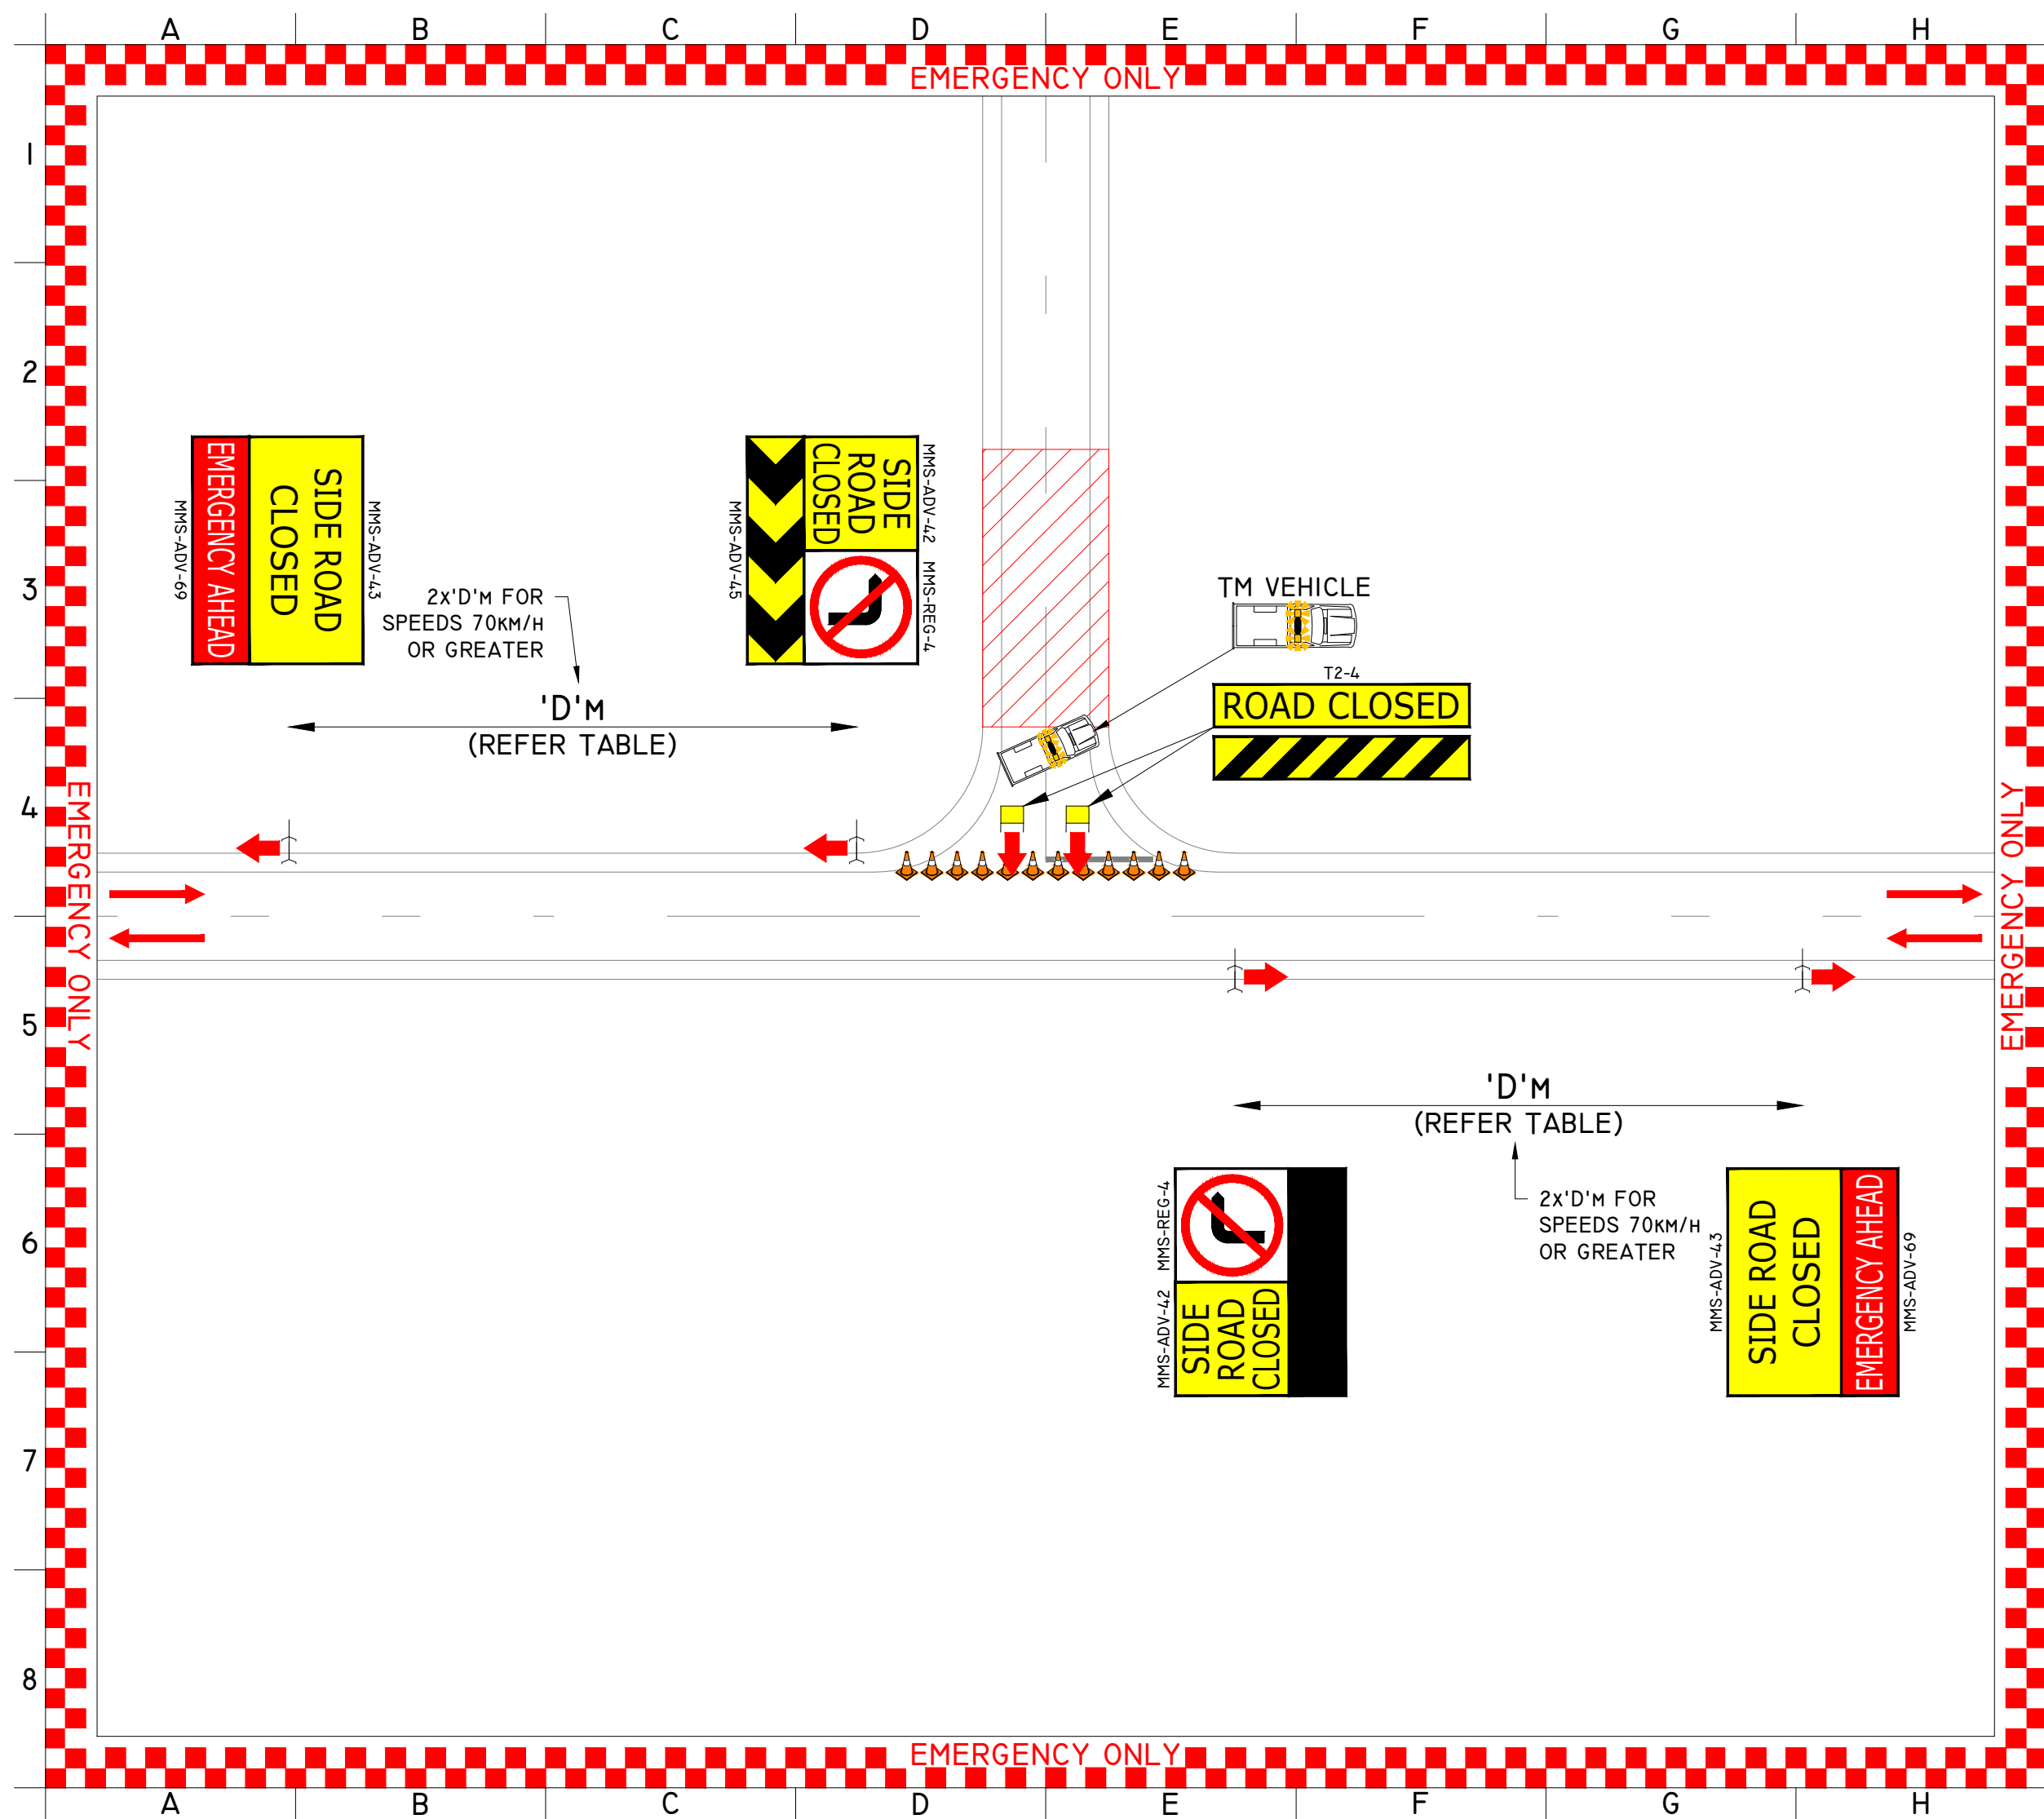

NOTES TOLERANCES: POSITION OF SIGNS: MINIMUM 10% LESS THAN THE DISTANCE OR LENGTHS GIVEN. MAXIMUM 25% MORE THAN THE DISTANCES OR LENGTHS GIVEN. SPACING OF DELINEATING DEVICES: MAXIMUM 10% MORE THAN THE SPACING GIVEN. NO MINIMUM. AGTTM PART 6 SECTION 6.8. DOCUMENTATION ON-SITE VARIATIONS MUST BE APPROVED BY THE TRAFFIC MANAGEMENT SUPERVISOR, THAN AN ON-SITE VARIATION MADE AND CHANGES RECORDED IN THE DAILY DAIRY. FOR MORE INFORMATION REFER TO SECTION 9.3 OF THE TMP. 1. PLAN TO BE USED FOR EMERGENCY WORKS ONLY. 2. ONE TM VEHICLE WILL BE REQUIRED FOR EVERY CLOSURE POINT AROUND EMERGENCY. 3. THIS PLAN MAY BE USED IN CONJUNCTION WITH OTHER EMERGENCY PLANS TO FORM A SAFE BARRIER AROUND THE HAZARD.														
TABLES SIGN SPACING AGTTM PART 3 - TABLE 2.2														
<table><tr><th>SPEED LIMIT (KM/H)</th><th>DISTANCE ('D') (M)</th></tr><tr><td>55 OR LESS</td><td>15</td></tr><tr><td>56 TO 65</td><td>45</td></tr><tr><td>GREATER THAN 65</td><td>EQUAL TO SPEED OF TRAFFIC IN KM/H</td></tr></table>	SPEED LIMIT (KM/H)	DISTANCE ('D') (M)	55 OR LESS	15	56 TO 65	45	GREATER THAN 65	EQUAL TO SPEED OF TRAFFIC IN KM/H						
SPEED LIMIT (KM/H)	DISTANCE ('D') (M)													
55 OR LESS	15													
56 TO 65	45													
GREATER THAN 65	EQUAL TO SPEED OF TRAFFIC IN KM/H													
LEGEND — EXISTING ROAD 🚧 PROPOSED CONES HAZARD														
 METROPOLITAN REGIONS TRAFFIC MANAGEMENT BRANCH WATERLOO CRESCENT TELEPHONE (08) 138 138 EAST PERTH 6004														
<table><tr><td>DATE OF DRAWING 2025 JULY</td><td>SCALE -</td></tr><tr><td>STRAIGHT LINE KILOMETERS (SLK) -</td><td>POSTED SPEED -</td></tr><tr><td>ROAD AUTHORITY MRWA</td><td>WORKSITE SPEED -</td></tr><tr><td>CHECKED BY TYLER HARTLEY</td><td>SIGNATURE </td></tr><tr><td>ACCREDITATION RTM-0066</td><td rowspan="2">SIGNATURE </td></tr><tr><td>DESIGNED BY MICHAEL REED</td></tr><tr><td>ACCREDITATION AWTM-23-11536-02</td><td></td></tr></table>	DATE OF DRAWING 2025 JULY	SCALE -	STRAIGHT LINE KILOMETERS (SLK) -	POSTED SPEED -	ROAD AUTHORITY MRWA	WORKSITE SPEED -	CHECKED BY TYLER HARTLEY	SIGNATURE 	ACCREDITATION RTM-0066	SIGNATURE 	DESIGNED BY MICHAEL REED	ACCREDITATION AWTM-23-11536-02		
DATE OF DRAWING 2025 JULY	SCALE -													
STRAIGHT LINE KILOMETERS (SLK) -	POSTED SPEED -													
ROAD AUTHORITY MRWA	WORKSITE SPEED -													
CHECKED BY TYLER HARTLEY	SIGNATURE 													
ACCREDITATION RTM-0066	SIGNATURE 													
DESIGNED BY MICHAEL REED														
ACCREDITATION AWTM-23-11536-02														
GENERIC TRAFFIC GUIDANCE SCHEME EMERGENCY WORK SCENARIOS MINOR 3-WAY INTERSECTION ROAD CLOSURE POINT														
DRAWING NO 0922-01531-EW-002	REVISION 6													