


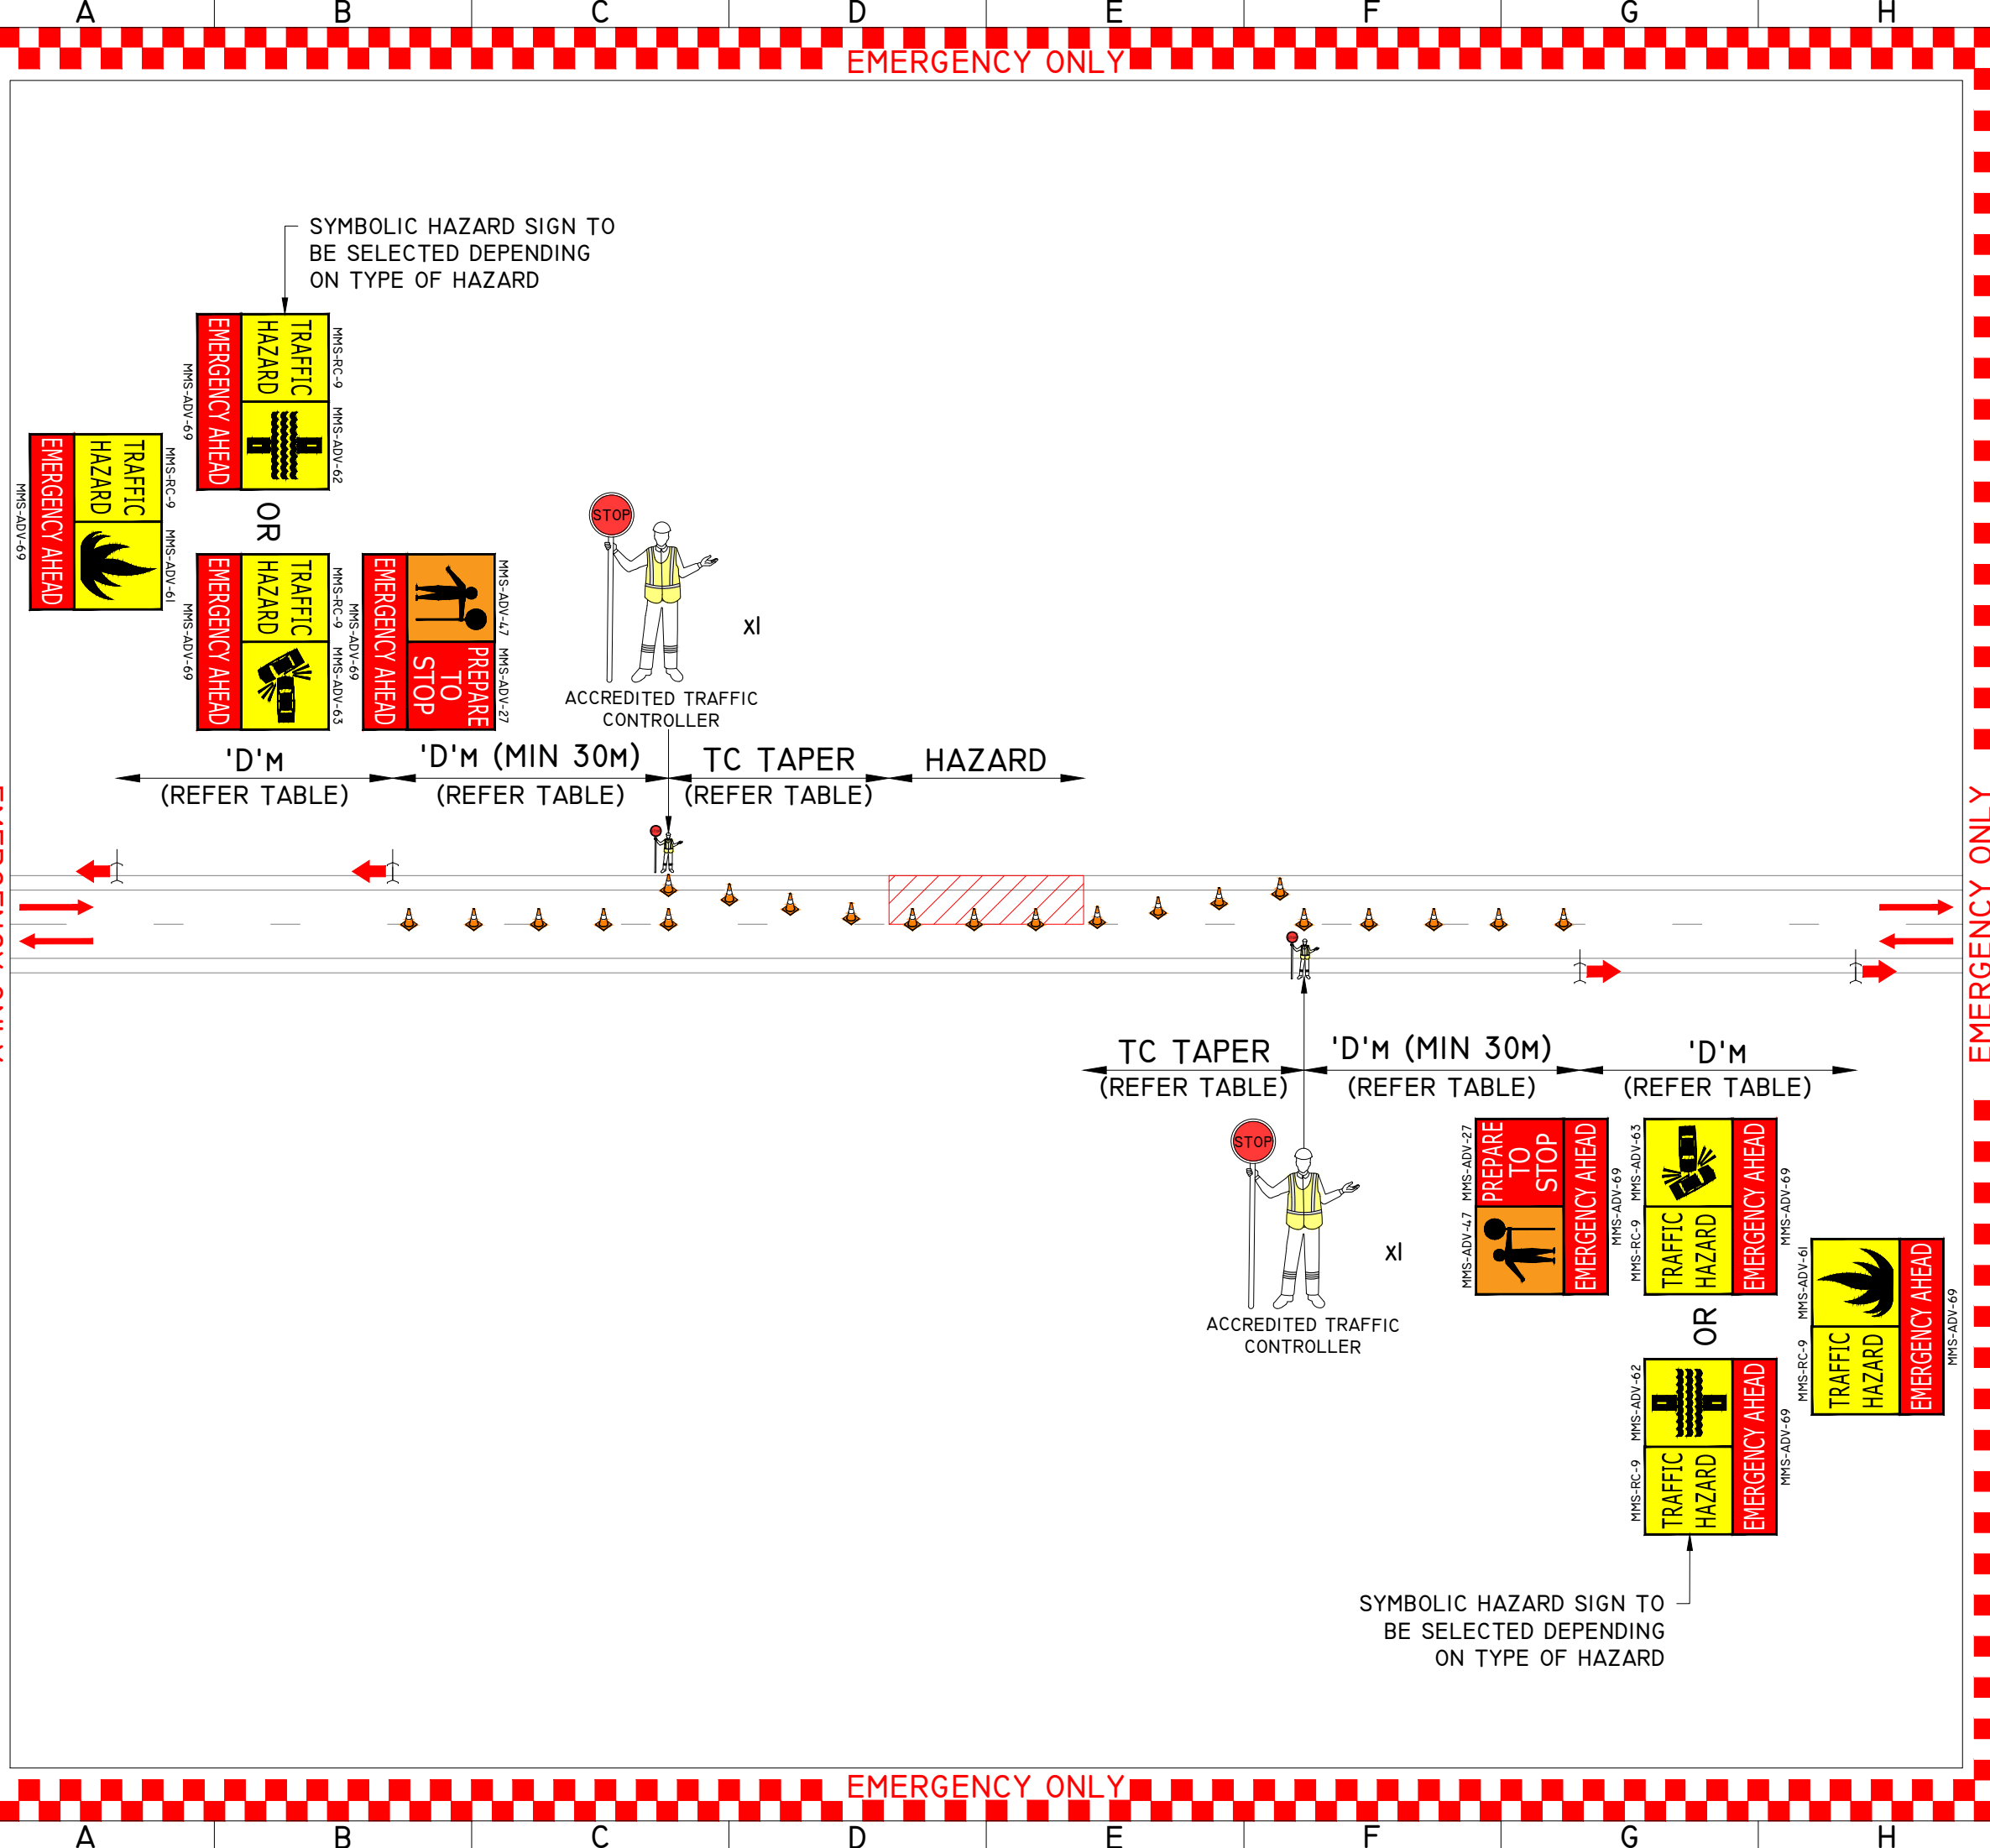

NOTES

TOLERANCES:
POSITION OF SIGNS:
MINIMUM 10% LESS THAN THE DISTANCE OR LENGTHS GIVEN.
MAXIMUM 25% MORE THAN THE DISTANCES OR LENGTHS GIVEN.
SPACING OF DELINEATING DEVICES:
MAXIMUM 10% MORE THAN THE SPACING GIVEN.
NO MINIMUM.
AGTTM PART 6 SECTION 6.8.

DOCUMENTATION
ON-SITE VARIATIONS MUST BE APPROVED BY THE TRAFFIC MANAGEMENT SUPERVISOR, THAN AN ON-SITE VARIATION MADE AND CHANGES RECORDED IN THE DAILY DAIRY. FOR MORE INFORMATION REFER TO SECTION 9.3 OF THE TMP.

1. PLAN TO BE USED FOR EMERGENCY WORKS ONLY.
2. ADDITIONAL CONES MAY BE DELIVERED TO SITE DEPENDING ON LENGTH OF EMERGENCY SETUP.
3. 'STOP HERE WHEN DIRECTED' SIGNAGE TO BE INSTALLED IF AVAILABLE ON SITE.

TABLES

SIGN SPACING
AGTTM PART 3 - TABLE 2.2

SPEED LIMIT (KM/H)	DISTANCE ('D') (M)
55 OR LESS	15
56 TO 65	45
GREATER THAN 65	EQUAL TO SPEED OF TRAFFIC IN KM/H

TAPER LENGTHS
AGTTM PART 3 - TABLE 5.7

SPEED LIMIT (KM/H)	TRAFFIC CONTROL TAPER (M)
45 OR LESS	15
46 TO 55	15
56 TO 65	30
66 TO 75*	N/A
76 TO 85*	
86 TO 95*	
96 TO 105*	
GREATER THAN 105*	

*TAPER LENGTHS ARE BASED ON A:


- 3.5m WIDTH OF THE LANE TO BE CLOSED
- LATERAL SHIFT TAPER LENGTH EQUAL TO 1.0m/s
- MEDIAN SPEED FOR EACH RANGE (I.E 76 - 85 = 80km/h)

LEGEND

- EXISTING ROAD
- PROPOSED CONES
- HAZARD



**METROPOLITAN REGIONS
TRAFFIC MANAGEMENT BRANCH**
WATERLOO CRESCENT
TELEPHONE (08) 138 138
EAST PERTH 6004

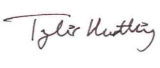DATE OF DRAWING 2025 JULY	SCALE -
STRAIGHT LINE KILOMETERS (SLK) -	POSTED SPEED -
ROAD AUTHORITY MRWA	WORKSITE SPEED -
CHECKED BY TYLER HARTLEY	SIGNATURE 
ACCREDITATION RTM-0066	SIGNATURE 
DESIGNED BY MICHAEL REED	
ACCREDITATION AWTM-23-11536-02	
GENERIC TRAFFIC GUIDANCE SCHEME EMERGENCY WORK SCENARIOS REVERSIBLE FLOW TWO WAY ROAD	
DRAWING NO 0922-01531-EW-005	REVISION 6