


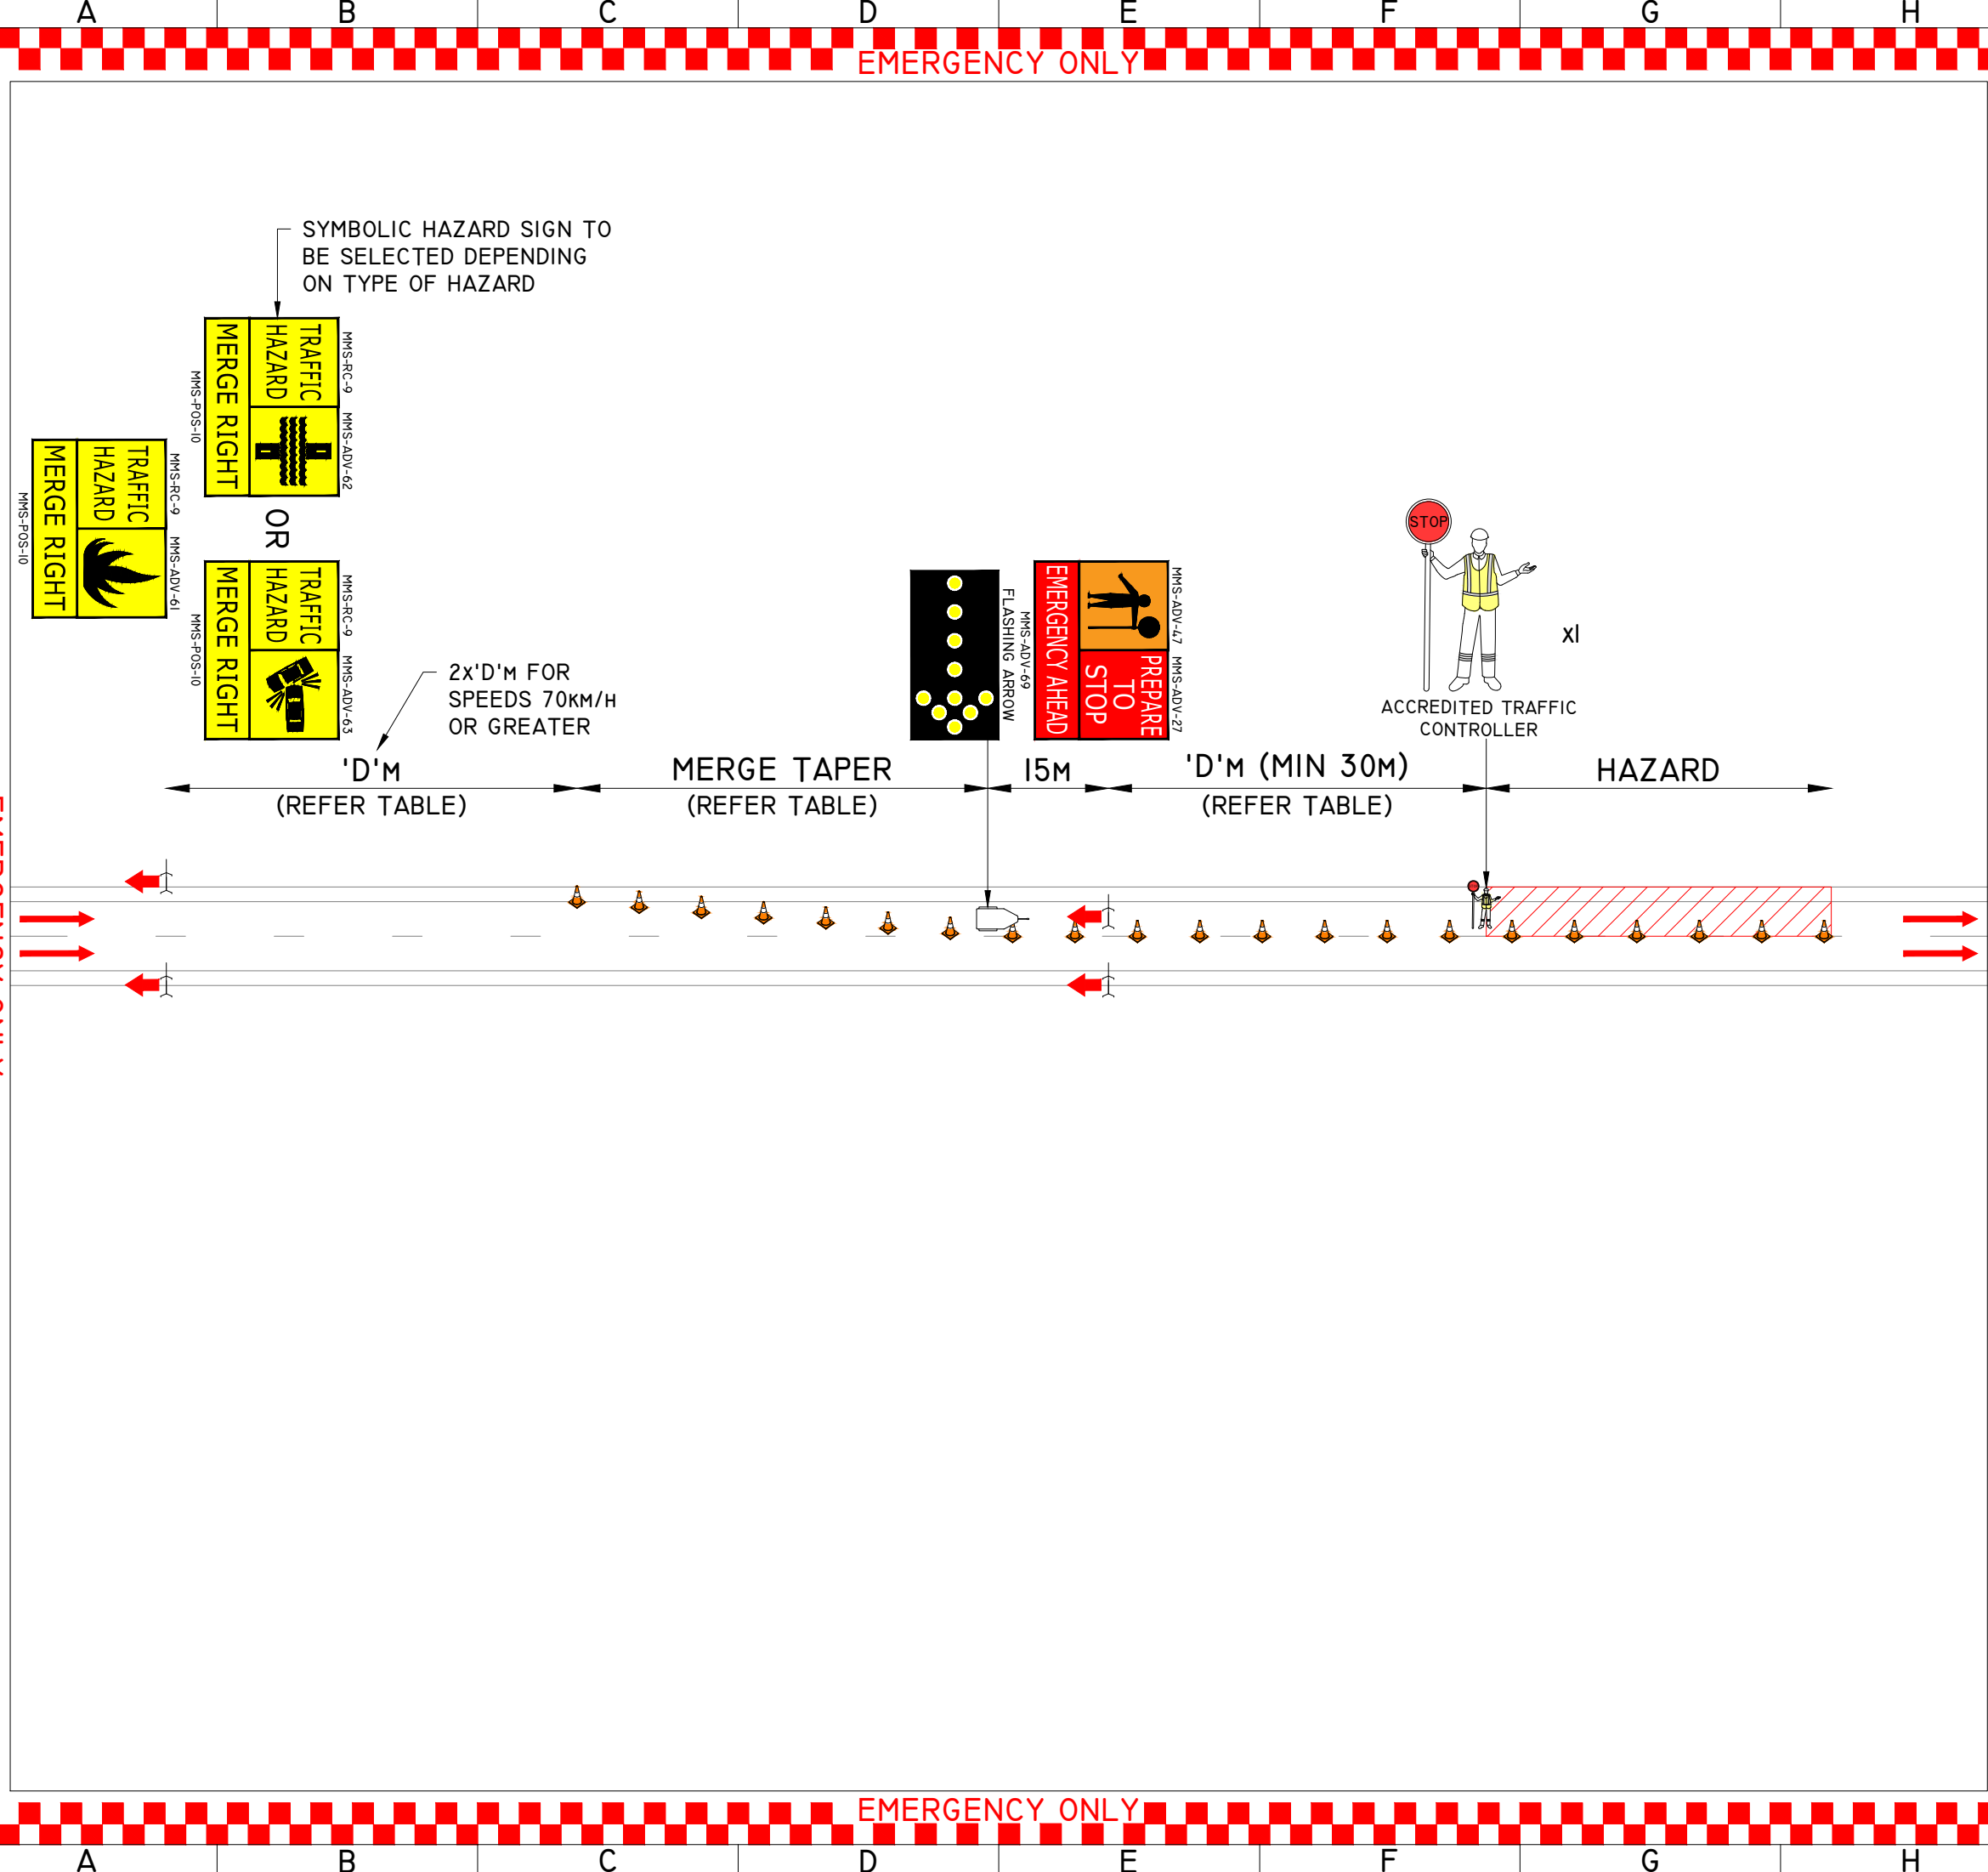

NOTES

TOLERANCES:  
POSITION OF SIGNS:  
MINIMUM 10% LESS THAN THE DISTANCE OR LENGTHS GIVEN.  
MAXIMUM 25% MORE THAN THE DISTANCES OR LENGTHS GIVEN.  
SPACING OF DELINEATING DEVICES:  
MAXIMUM 10% MORE THAN THE SPACING GIVEN.  
NO MINIMUM.  
AGTTM PART 6 SECTION 6.8.  
DOCUMENTATION  
ON-SITE VARIATIONS MUST BE APPROVED BY THE TRAFFIC MANAGEMENT SUPERVISOR, THAN AN ON-SITE VARIATION MADE AND CHANGES RECORDED IN THE DAILY DAIRY. FOR MORE INFORMATION REFER TO SECTION 9.3 OF THE TMP.  
1. PLAN TO BE USED FOR EMERGENCY WORKS ONLY.  
2. TCs MAY BE USED ON SITE WHERE HAZARD ENCROACHES INTO LIVE LANES.  
3. ONE TM VEHICLE REQUIRED PER DIRECTION OF AFFECTED TRAFFIC.  
4. ADDITIONAL CONES MAY BE DELIVERED TO SITE DEPENDING ON LENGTH OF EMERGENCY SETUP.  
5. 'STOP HERE WHEN DIRECTED' SIGNAGE INSTALLED AS REQUIRED.

TABLES

SIGN SPACING

AGTTM PART 3 - TABLE 2.2

| SPEED LIMIT (KM/H) | DISTANCE ('D') (M)                |
|--------------------|-----------------------------------|
| 55 OR LESS         | 15                                |
| 56 TO 65           | 45                                |
| GREATER THAN 65    | EQUAL TO SPEED OF TRAFFIC IN KM/H |

TAPER LENGTHS

AGTTM PART 3 - TABLE 5.7

| SPEED LIMIT (KM/H) | MERGE TAPER (M) |
|--------------------|-----------------|
| 45 OR LESS         | 15              |
| 46 TO 55           | 30              |
| 56 TO 65           | 60              |
| 66 TO 75*          | 115             |
| 76 TO 85*          | 130             |
| 86 TO 95*          | 145             |
| 96 TO 105*         | 160             |
| GREATER THAN 105*  | 180             |

- \*TAPER LENGTHS ARE BASED ON A:  
• 3.5m WIDTH OF THE LANE TO BE CLOSED  
• MERGE TAPER LENGTH EQUAL TO 0.6M/S  
• MEDIAN SPEED FOR EACH RANGE (I.E 76 - 85 = 80KM/H

LEGEND

- EXISTING ROAD  
PROPOSED CONES  
HAZARD



METROPOLITAN REGIONS  
TRAFFIC MANAGEMENT BRANCH  
WATERLOO CRESCENT  
TELEPHONE (08) 138 138  
EAST PERTH 6004

|                                     |                                   |
|-------------------------------------|-----------------------------------|
| DATE OF DRAWING<br>2025 JULY        | SCALE<br>-                        |
| STRAIGHT LINE KILOMETERS (SLK)<br>- | POSTED SPEED<br>-                 |
| ROAD AUTHORITY<br>MRWA              | WORKSITE SPEED<br>-               |
| CHECKED BY<br>TYLER HARTLEY         | SIGNATURE<br><i>Tyler Hartley</i> |
| ACCREDITATION<br>RTM-0066           |                                   |
| DESIGNED BY<br>MICHAEL REED         | SIGNATURE<br><i>Michael Reed</i>  |
| ACCREDITATION<br>AWTM-23-11536-02   |                                   |

GENERIC TRAFFIC GUIDANCE SCHEME  
EMERGENCY WORK SCENARIOS  
LANE CLOSURE  
DUAL LANE ROAD

|                                 |               |
|---------------------------------|---------------|
| DRAWING NO<br>0922-01531-EW-006 | REVISION<br>6 |
|---------------------------------|---------------|