


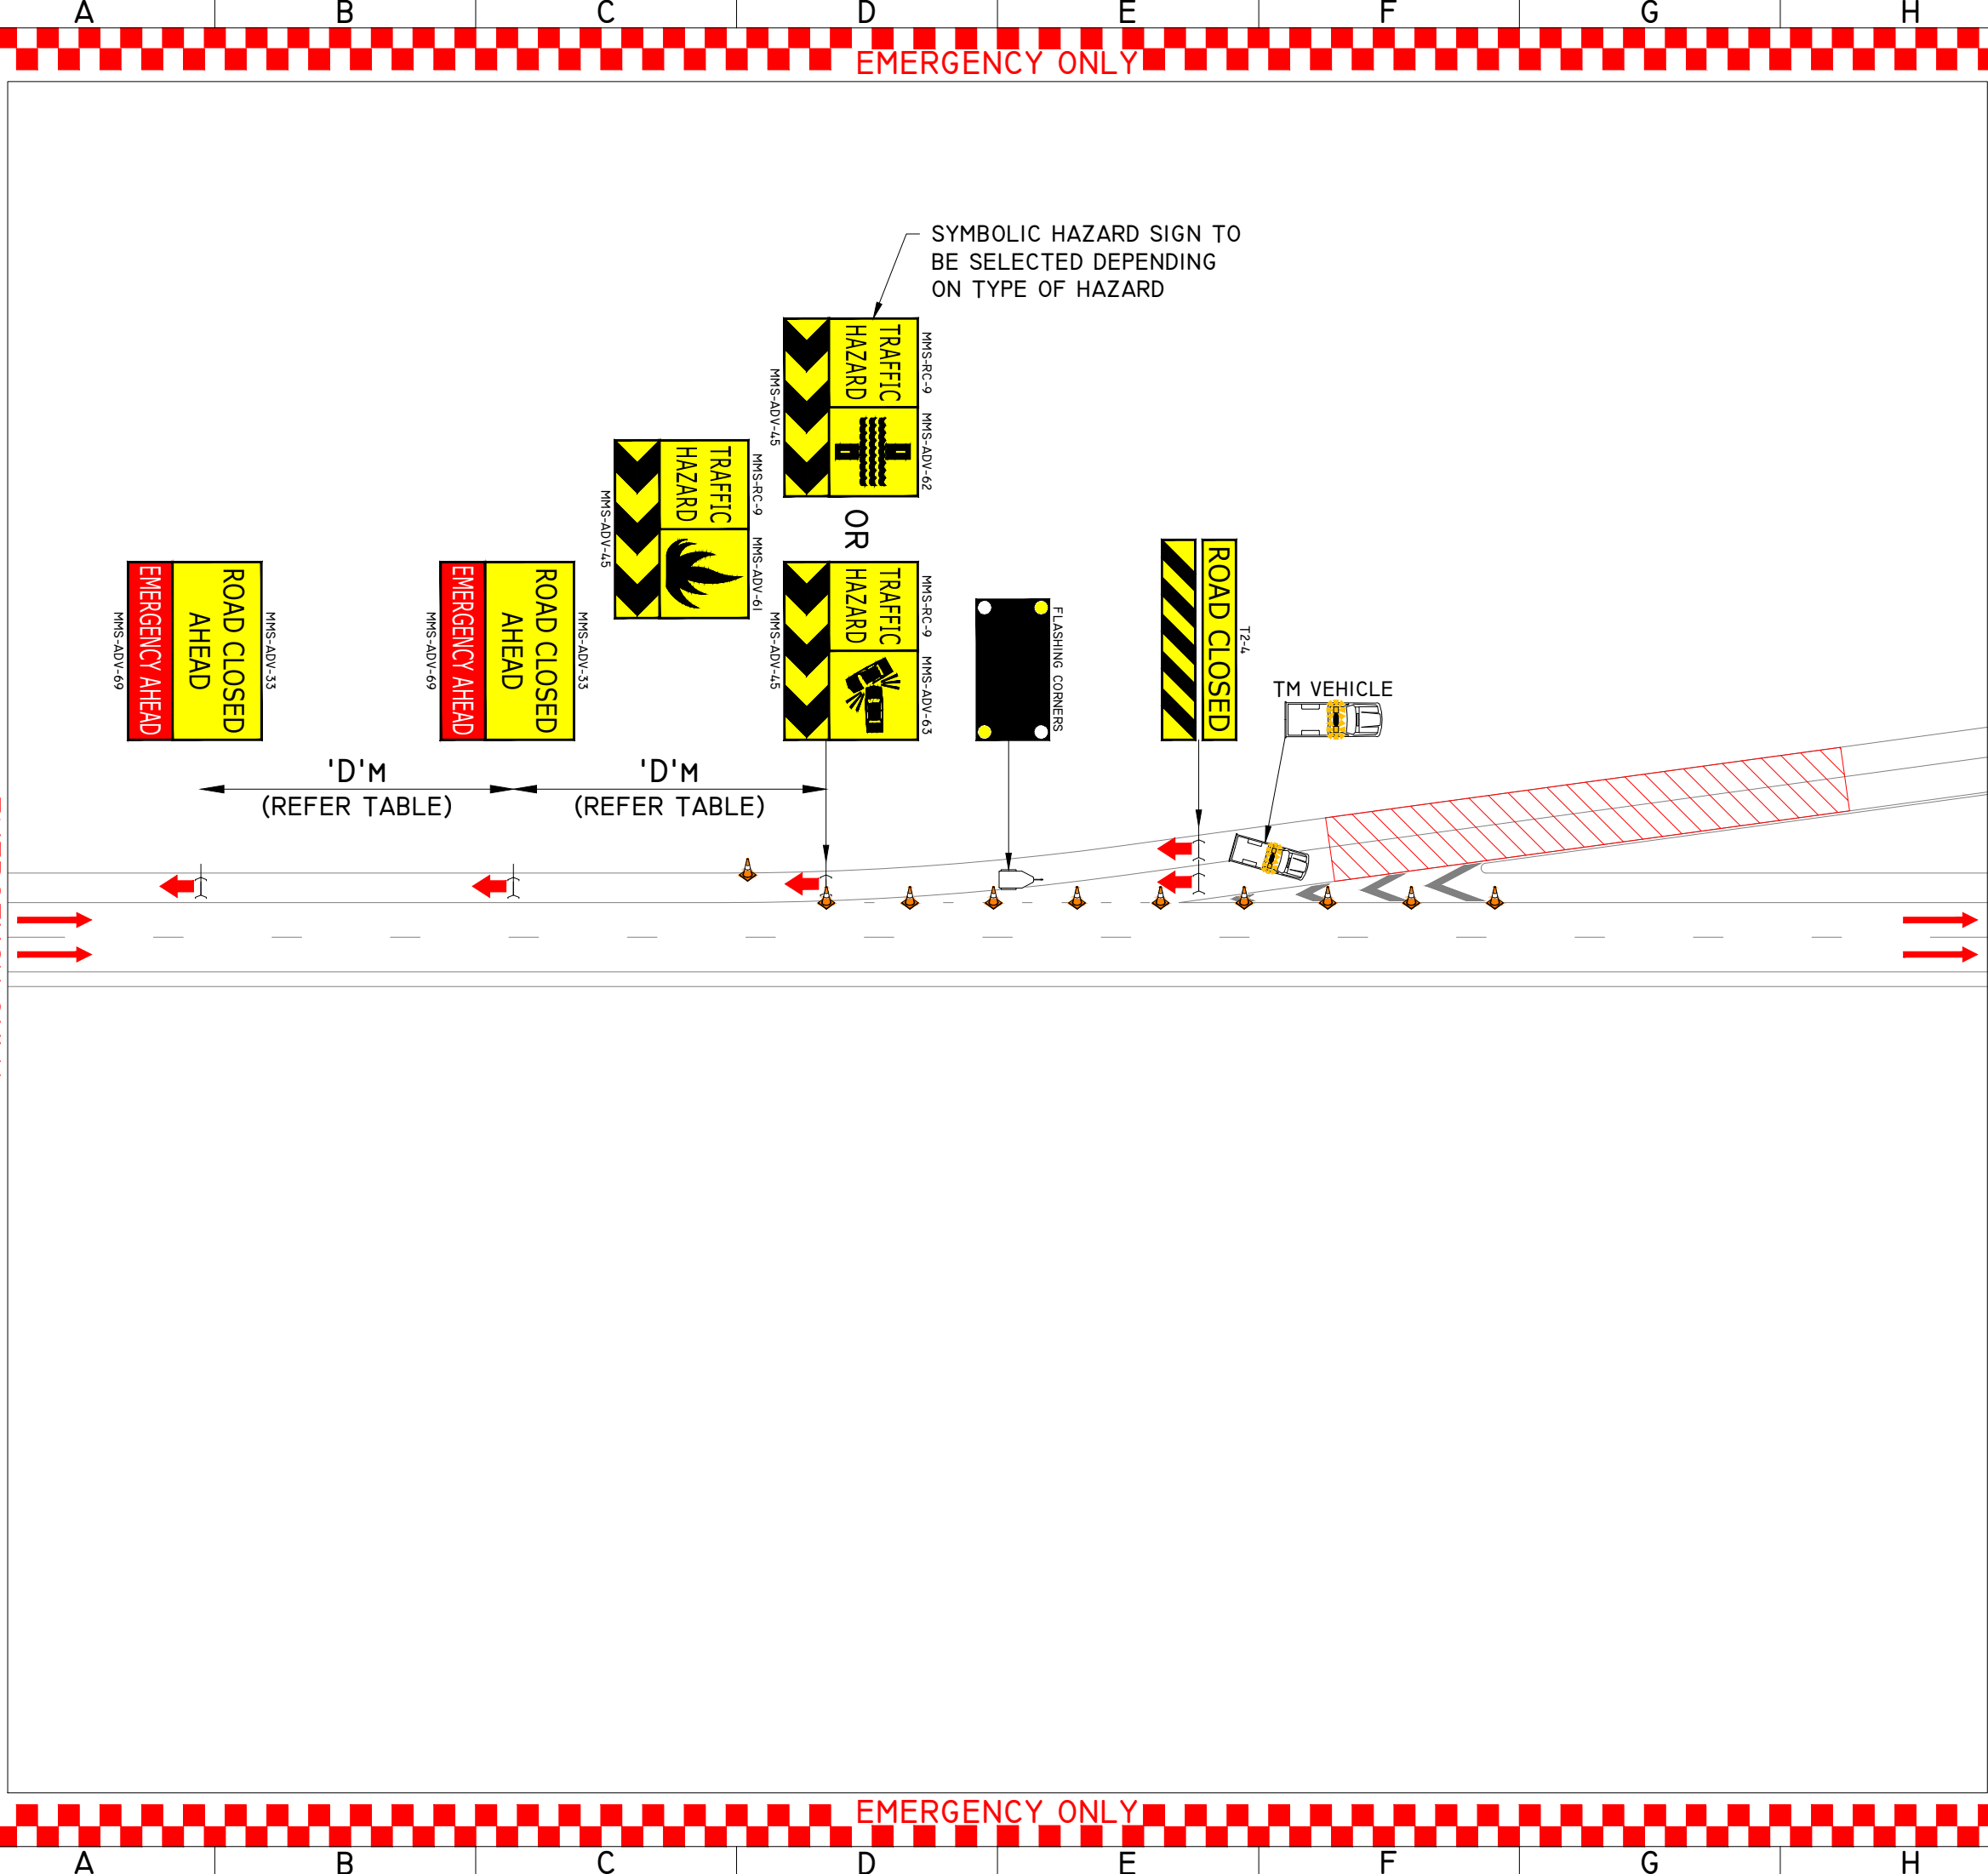

SYMBOLIC HAZARD SIGN TO
BE SELECTED DEPENDING
ON TYPE OF HAZARD

NOTES

TOLERANCES:
POSITION OF SIGNS:
MINIMUM 10% LESS THAN THE DISTANCE OR LENGTHS GIVEN.
MAXIMUM 25% MORE THAN THE DISTANCES OR LENGTHS GIVEN.
SPACING OF DELINEATING DEVICES:
MAXIMUM 10% MORE THAN THE SPACING GIVEN.
NO MINIMUM.
AGTTM PART 6 SECTION 6.8.

DOCUMENTATION
ON-SITE VARIATIONS MUST BE APPROVED BY THE TRAFFIC
MANAGEMENT SUPERVISOR, THAN AN ON-SITE VARIATION MADE
AND CHANGES RECORDED IN THE DAILY DAIRY. FOR MORE
INFORMATION REFER TO SECTION 9.3 OF THE TMP.

1. PLAN TO BE USED FOR EMERGENCY WORKS ONLY.
2. ONE TM VEHICLE WILL BE REQUIRED FOR EVERY CLOSURE
POINT AROUND EMERGENCY.
3. THIS PLAN MAY BE USED IN CONJUNCTION WITH OTHER
EMERGENCY PLANS TO FORM A SAFE BARRIER AROUND
THE HAZARD.

TABLES

SIGN SPACING
AGTTM PART 3 - TABLE 2.2

SPEED LIMIT (KM/H)	DISTANCE ('D') (M)
55 OR LESS	15
56 TO 65	45
GREATER THAN 65	EQUAL TO SPEED OF TRAFFIC IN KM/H

LEGEND

	EXISTING ROAD
	PROPOSED CONES
	HAZARD

**METROPOLITAN REGIONS
TRAFFIC MANAGEMENT BRANCH**
WATERLOO CRESCENT
TELEPHONE (08) 138 138
EAST PERTH 6004

DATE OF DRAWING 2025 JULY	SCALE -
STRAIGHT LINE KILOMETERS (SLK) -	POSTED SPEED -
ROAD AUTHORITY MRWA	WORKSITE SPEED -
CHECKED BY TYLER HARTLEY	SIGNATURE
ACCREDITATION RTM-0066	SIGNATURE
DESIGNED BY MICHAEL REED	
ACCREDITATION AWTM-23-11536-02	

GENERIC TRAFFIC GUIDANCE SCHEME
EMERGENCY WORK SCENARIOS
OFF RAMP
CLOSURE POINT

DRAWING NO
0922-01531-EW-010

REVISION
6