

EMERGENCY ONLY

NOTES

TOLERANCES:
POSITION OF SIGNS:
MINIMUM 10% LESS THAN THE DISTANCE OR LENGTHS GIVEN.
MAXIMUM 25% MORE THAN THE DISTANCES OR LENGTHS GIVEN.
SPACING OF DELINEATING DEVICES:
MAXIMUM 10% MORE THAN THE SPACING GIVEN.
NO MINIMUM.

AGTTM PART 6 SECTION 6.8.

DOCUMENTATION

ON-SITE VARIATIONS MUST BE APPROVED BY THE TRAFFIC MANAGEMENT SUPERVISOR, THAN AN ON-SITE VARIATION MADE AND CHANGES RECORDED IN THE DAILY DAIRY. FOR MORE INFORMATION REFER TO SECTION 9.3 OF THE TMP.

1. PLAN TO BE USED FOR EMERGENCY WORKS ONLY.
2. ONE TM VEHICLE WILL BE REQUIRED FOR EVERY CLOSURE POINT AT EMERGENCY.
3. THIS PLAN MAY BE USED IN CONJUNCTION WITH OTHER EMERGENCY PLANS TO FORM A SAFE BARRIER AROUND THE HAZARD.
4. APPROPRIATE DETOUR PATH TO BE DECIDED PRIOR TO IMPLEMENTATION ONSITE

TABLES

SIGN SPACING

AGTTM PART 3 - TABLE 2.2

SPEED LIMIT (km/h)	DISTANCE ('D') (m)
55 OR LESS	15
56 TO 65	45
GREATER THAN 65	EQUAL TO SPEED OF TRAFFIC IN km/h

LEGEND

- EXISTING ROAD
- PROPOSED CONES
- HAZARD




METROPOLITAN REGIONS
TRAFFIC MANAGEMENT BRANCH
WATERLOO CRESCENT
TELEPHONE (08) 138 138
EAST PERTH 6004

DATE OF DRAWING	2025 JULY	SCALE	-
STRAIGHT LINE KILOMETERS (SLK)	-	POSTED SPEED	-
ROAD AUTHORITY	MRWA	WORKSITE SPEED	-
CHECKED BY	TYLER HARTLEY	SIGNATURE	<i>Tyler Hartley</i>
ACCREDITATION	RTM-0066	SIGNATURE	<i>Michael Reed</i>
DESIGNED BY	MICHAEL REED	SIGNATURE	<i>Michael Reed</i>
ACCREDITATION	AWTM-23-11536-02	SIGNATURE	<i>Michael Reed</i>

GENERIC TRAFFIC GUIDANCE SCHEME
EMERGENCY WORK SCENARIOS
ROAD CLOSURE WITH DETOUR
TWO WAY ROAD

DRAWING NO	0922-01531-EW-019	REVISION	6
------------	-------------------	----------	---

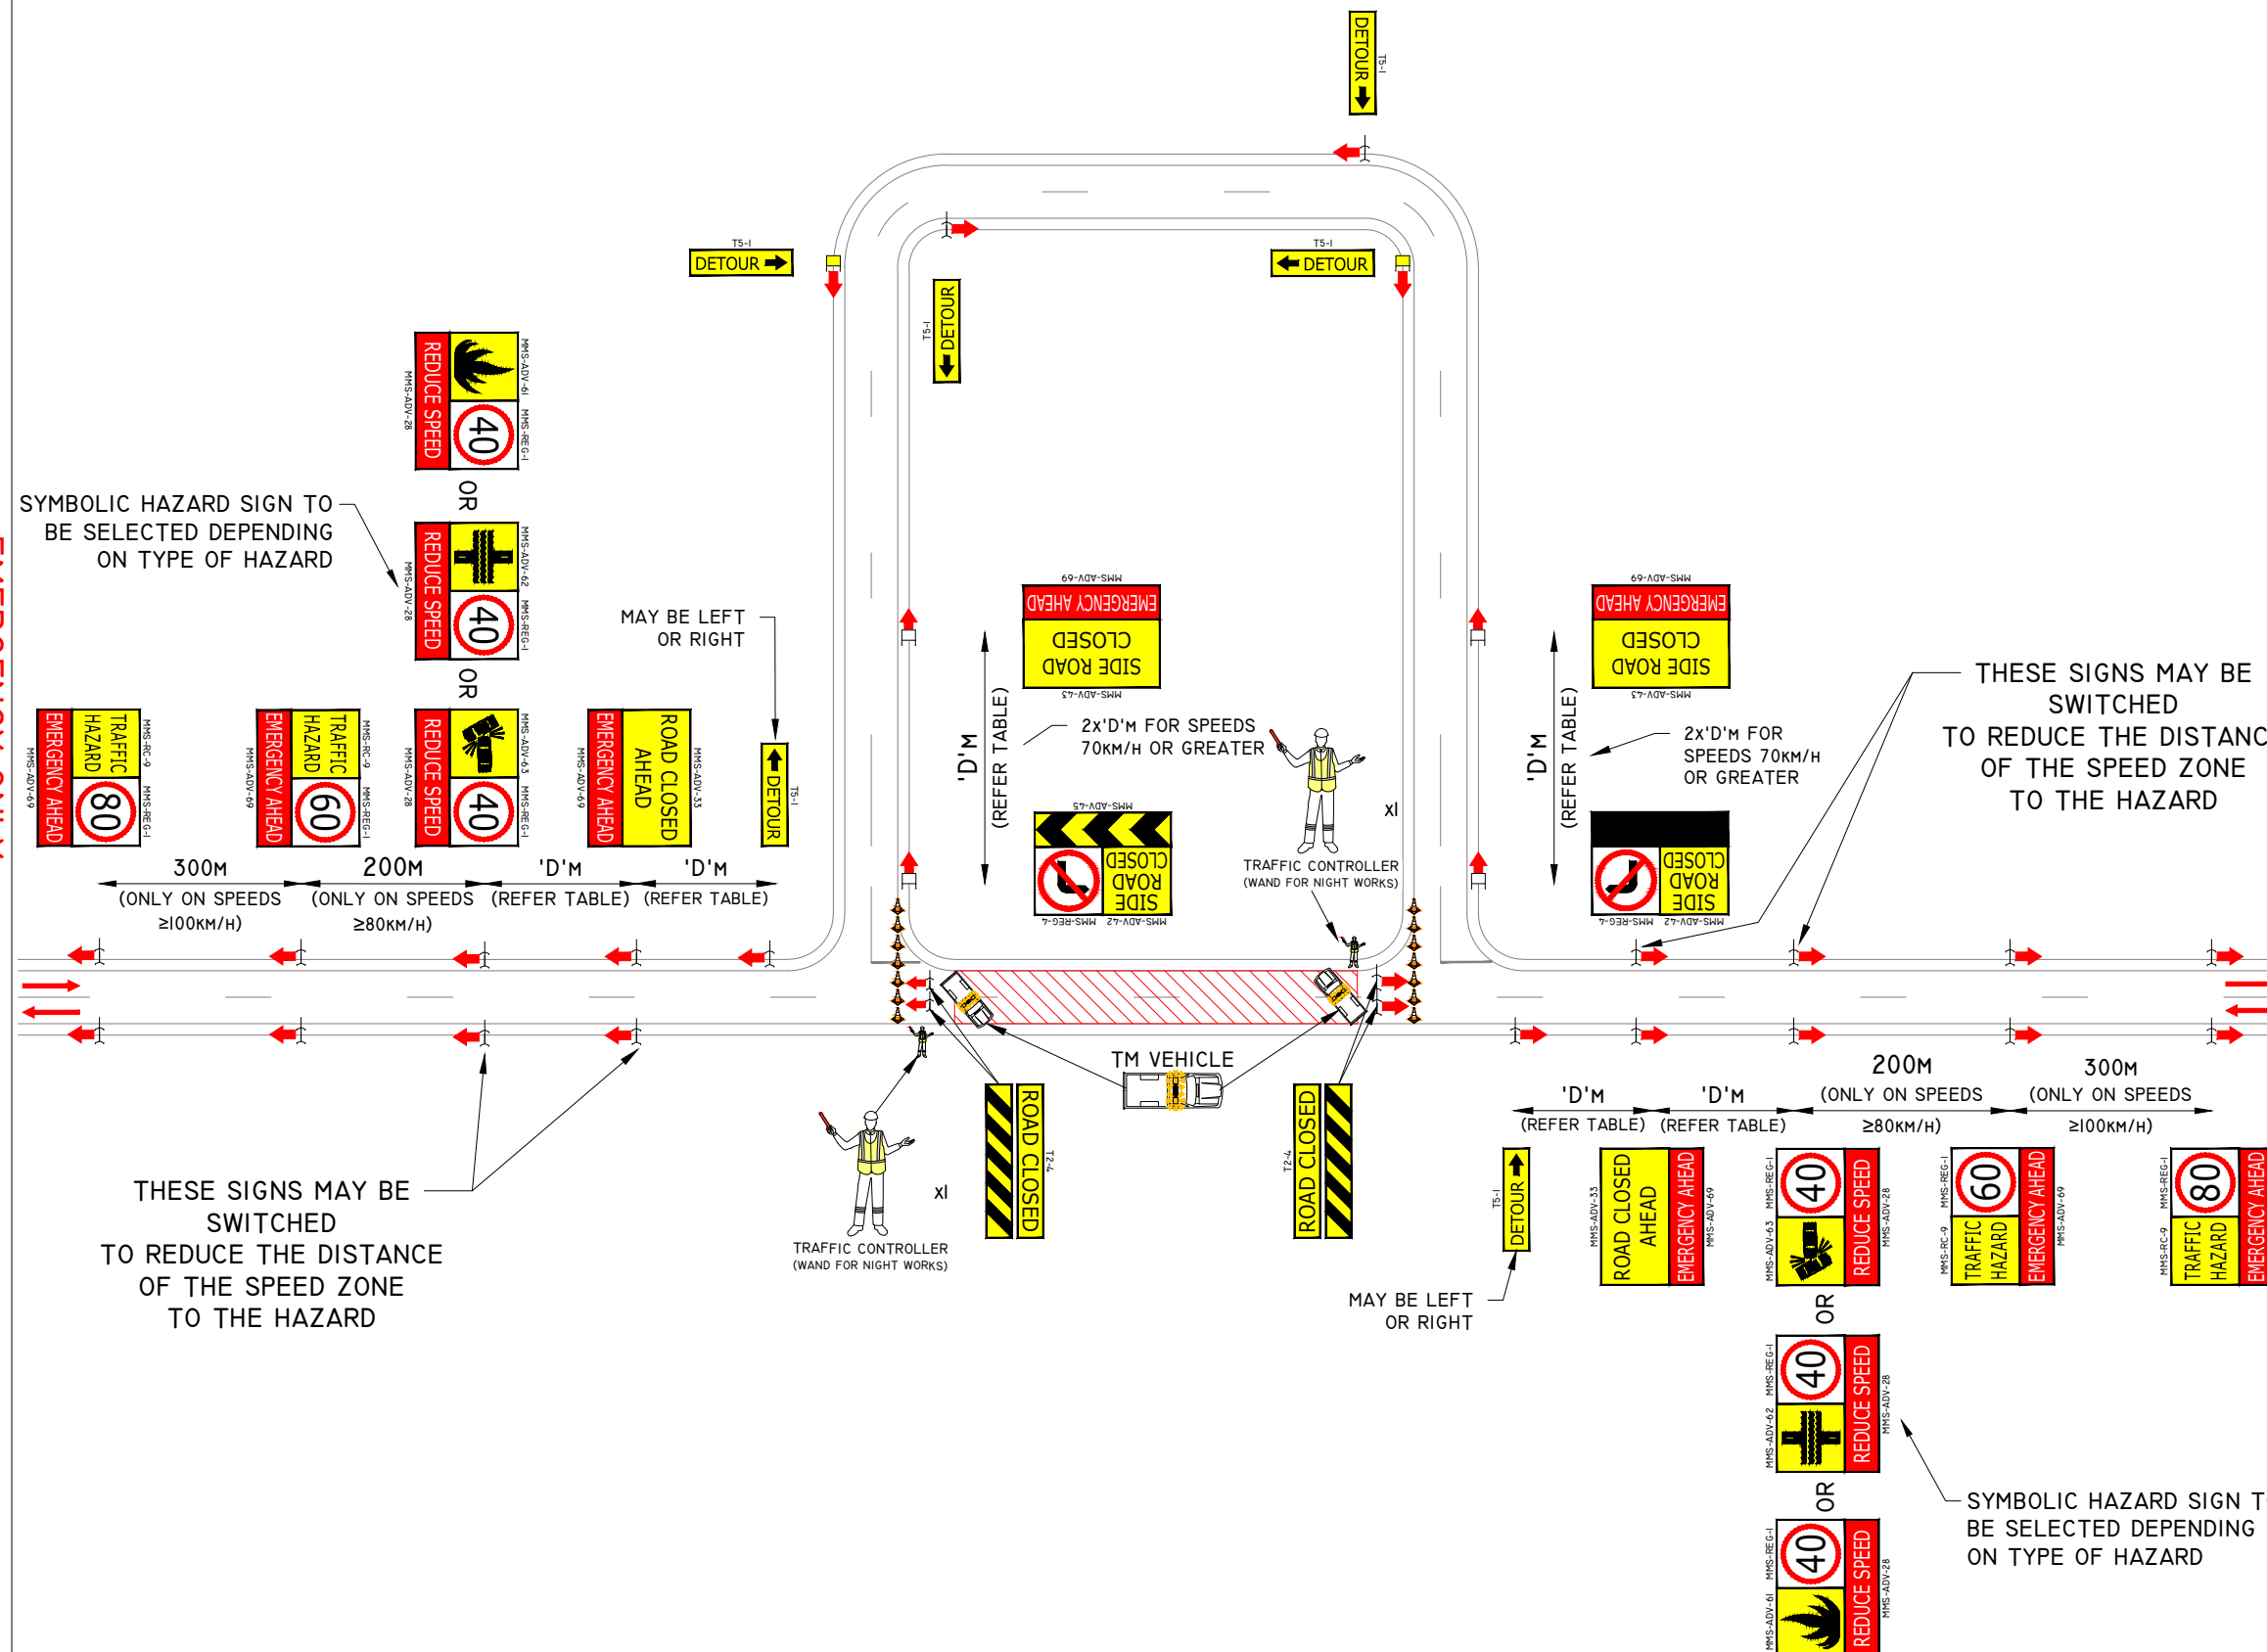

EMERGENCY ONLY