
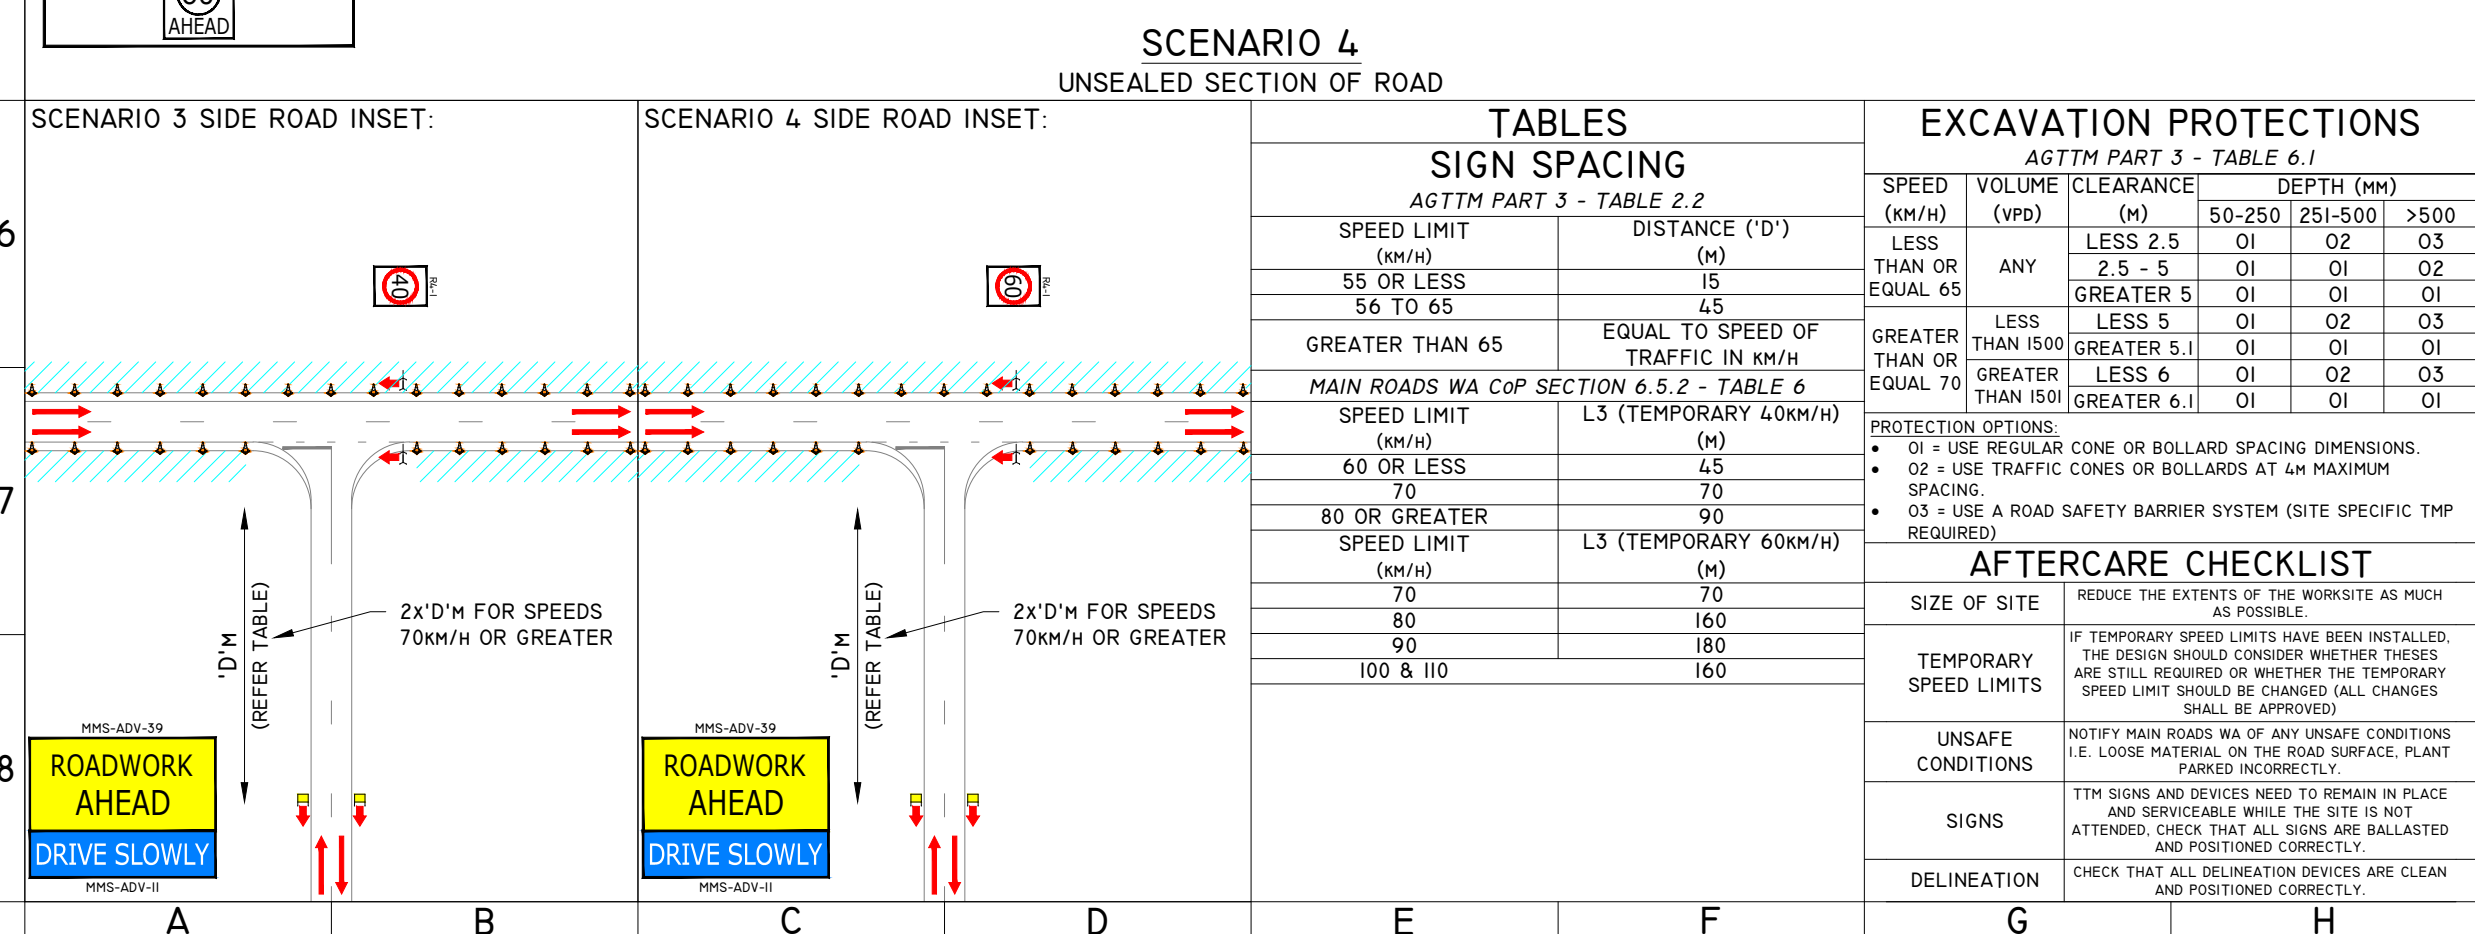
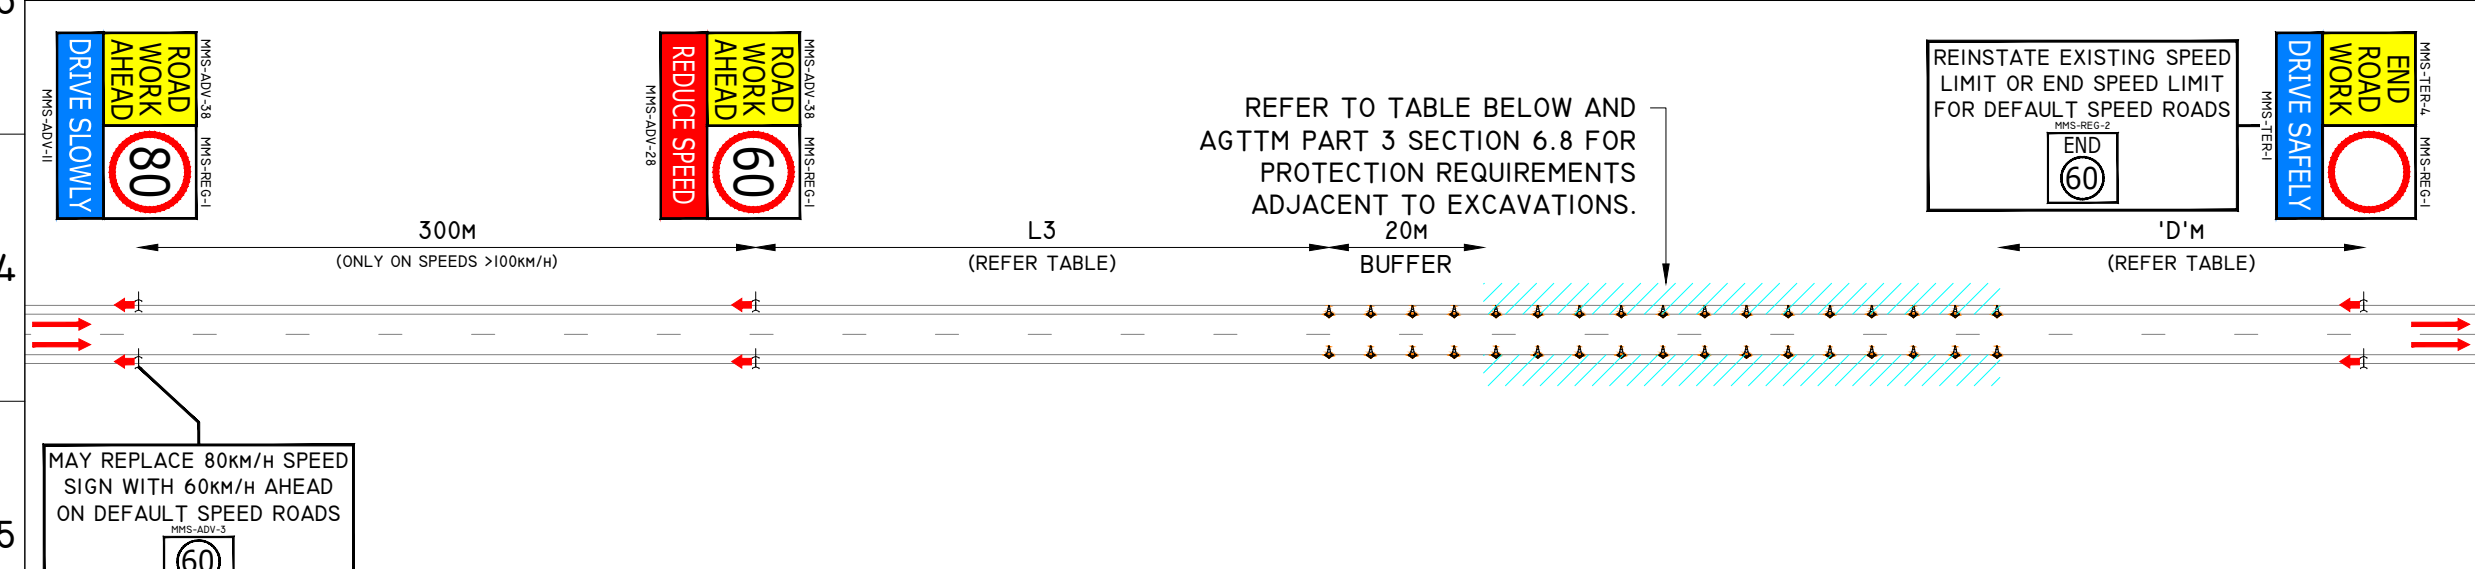


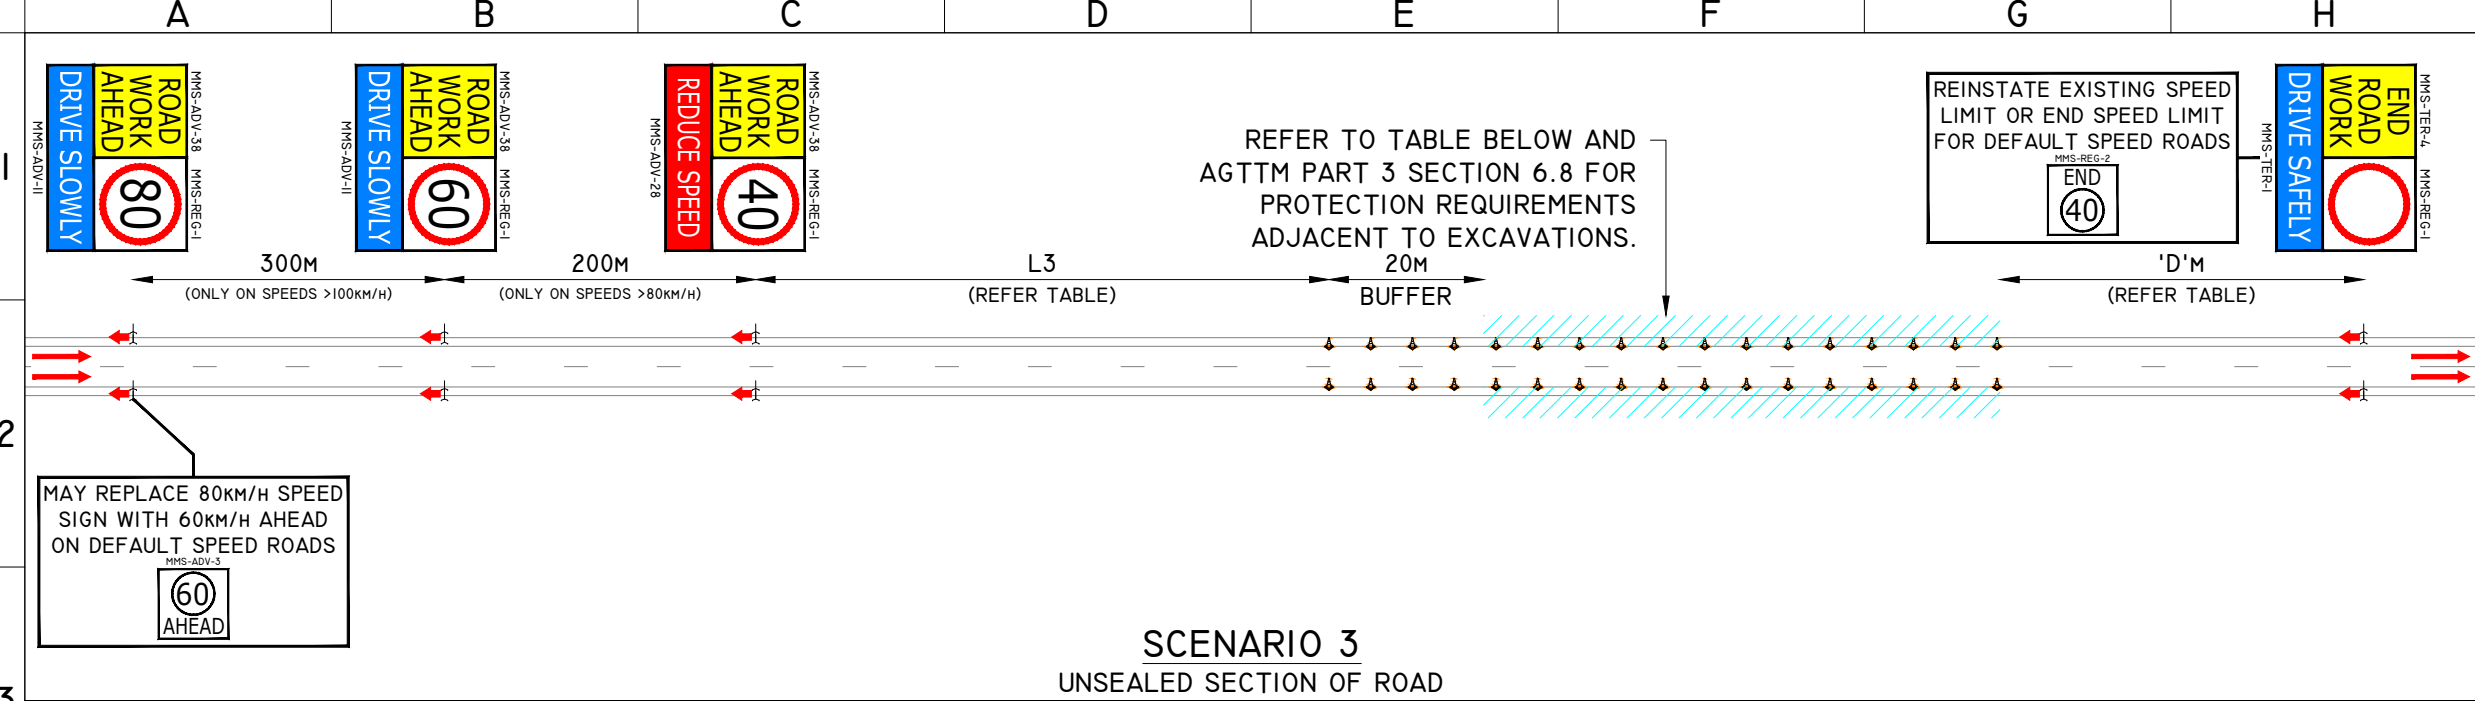

SCENARIO 3:

- 40km/h SPEED REDUCTION FOR AN UNSAFE EXCAVATION ADJACENT TO THE ROAD.

SCENARIO 4:

- 60km/h SPEED REDUCTION FOR AN UNSAFE EXCAVATION ADJACENT TO THE ROAD.

NOTES

TOLERANCES

POSITION OF SIGNS:
MINIMUM 10% LESS THAN THE DISTANCE OR LENGTHS GIVEN.
MAXIMUM 25% MORE THAN THE DISTANCES OR LENGTHS GIVEN.

SPACING OF DELINEATING DEVICES:
MAXIMUM 10% MORE THAN THE SPACING GIVEN.
NO MINIMUM.

AGTTM PART 6 SECTION 6.8.

DOCUMENTATION

ON-SITE VARIATIONS MUST BE APPROVED BY THE TRAFFIC MANAGEMENT SUPERVISOR, THAN AN ON-SITE VARIATION MADE AND CHANGES RECORDED IN THE DAILY DAIRY. FOR MORE INFORMATION REFER TO SECTION 9.3 OF THE TMP.

- ALL SIGN LOCATIONS ARE TO BE CHECKED ON SITE PRIOR TO SETOUT AND POSITIONS ADJUSTED AS PER THE 'TOLERANCES'.
- WHERE TEMPORARY SPEED REDUCTIONS ARE IMPLEMENTED, THEY SHOULD BE NO MORE THAN 20km/h LESS THAN THE POSTED SPEED LIMIT.
- WHERE TEMPORARY SPEED REDUCTIONS GREATER THAN 20km/h ARE REQUIRED AN ON-SITE RISK ASSESSMENT SHALL BE COMPLETED.
- PERIODIC INSPECTIONS OF THE SITE SHALL BE CONDUCTED AS PER AGTTM PART 6 SECTION 7.4 AFTERCARE - WORKSITE ARRANGEMENTS OUTSIDE WORKING HOURS. FOR BOX EDGED SIGN ALTERNATIVES, CONSULT AWTM PRIOR TO IMPLEMENTATION.
- PEDESTRIAN MANAGEMENT


- 'PEDESTRIAN WATCH YOUR STEP' SIGN TO BE INSTALLED ON EACH APPROACH WHERE WORKS MAY ENCROACH ONTO OR ADJACENT TO EXISTING FOOTPATH FACILITIES.
- TM PERSONNEL TO MONITOR AND ESCORT PEDESTRIANS THROUGH THE WORK AREA AS REQUIRED.
- PEDESTRIANS MAY BE HELD ON EITHER END OF THE WORKSITE UNTIL IT IS SAFE TO PASS AS REQUIRED.

LEGEND

- EXISTING ROAD
- PROPOSED CONES
- WORKSITE



**METROPOLITAN REGIONS
TRAFFIC MANAGEMENT BRANCH**
WATERLOO CRESCENT
TELEPHONE (08) 138 138
EAST PERTH 6004

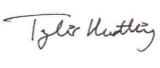DATE OF DRAWING 2025 JULY	SCALE -
LOCAL GOVERNMENT AUTHORITY -	POSTED SPEED -
ROAD AUTHORITY MAIN ROADS WA	WORKSITE SPEED -
CHECKED BY TYLER HARTLEY	SIGNATURE 
ACCREDITATION RTM-0066	SIGNATURE 
DESIGNED BY MICHAEL REED	
ACCREDITATION AWTM-23-11536-02	

GENERIC TRAFFIC GUIDANCE SCHEME
AFTERCARE MANAGEMENT
UNSEALED ROAD - ONE WAY ROAD
AND TEMPORARY SPEED ZONES (2/2)

DRAWING NO
0922-01531-AC-006B

REVISION
6