


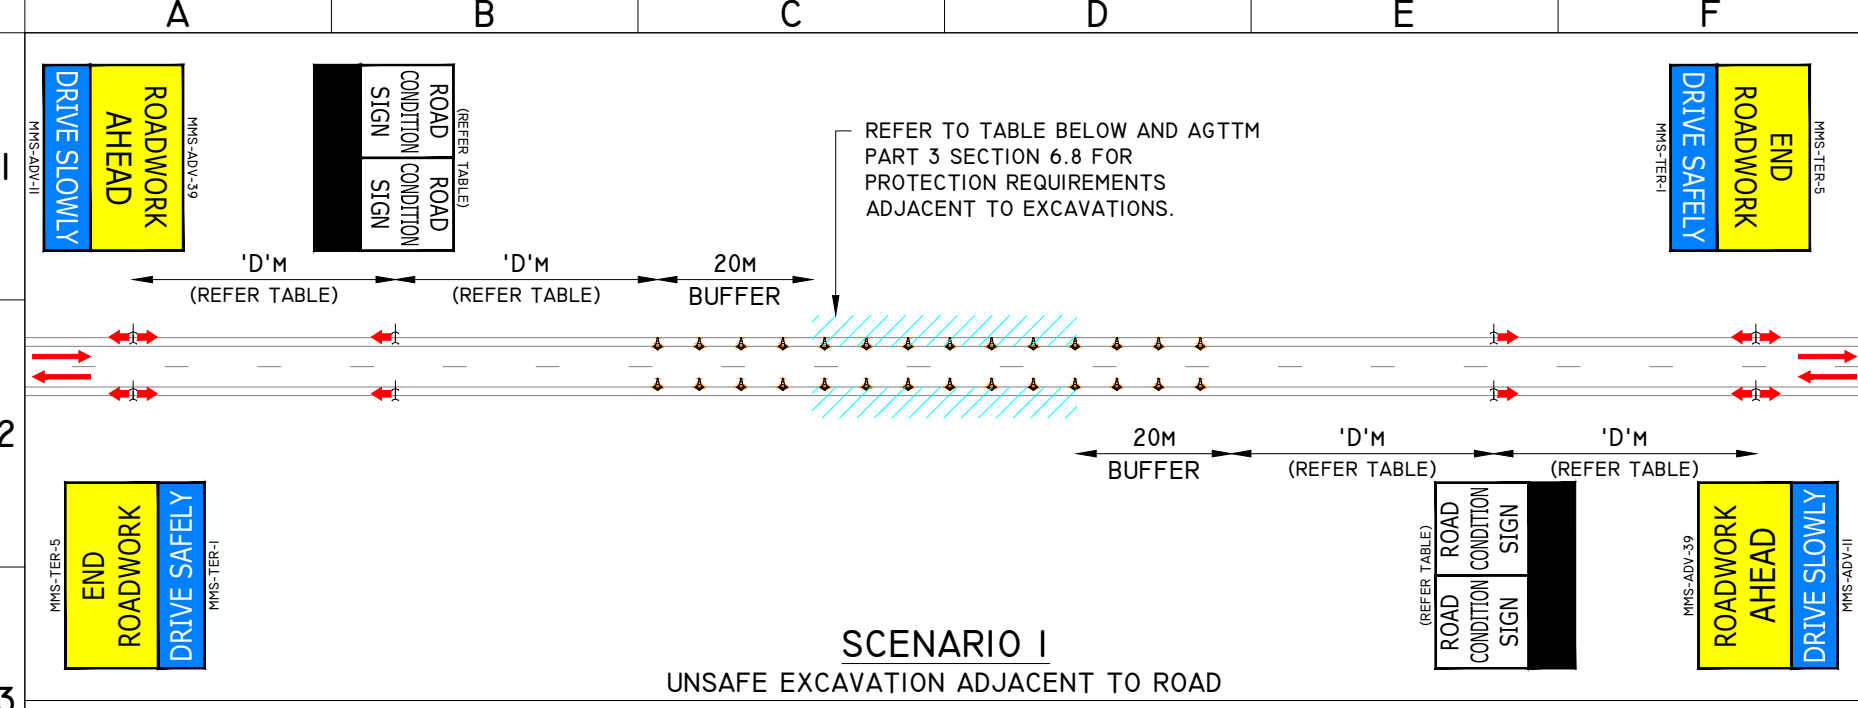
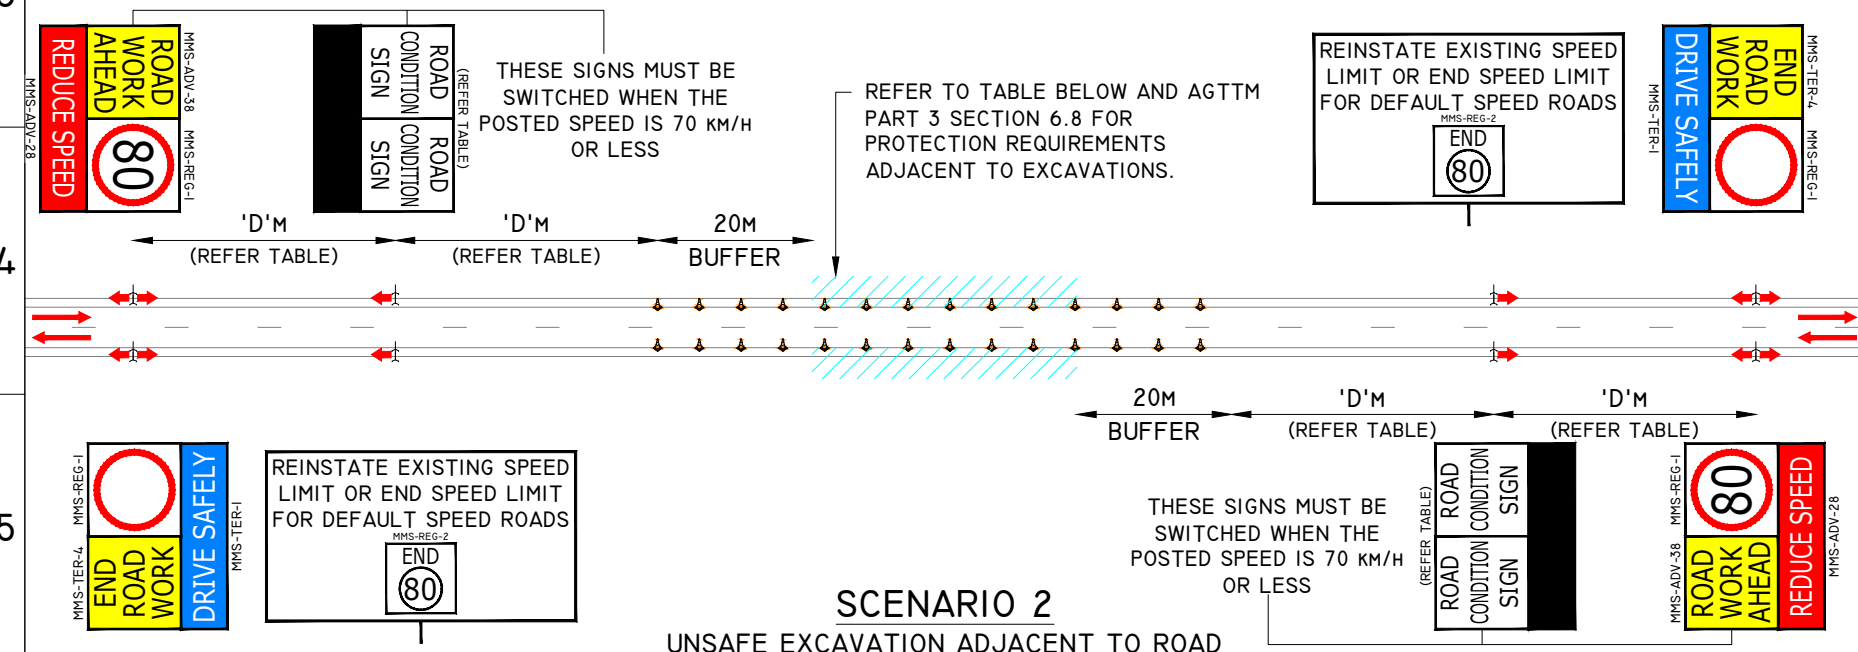


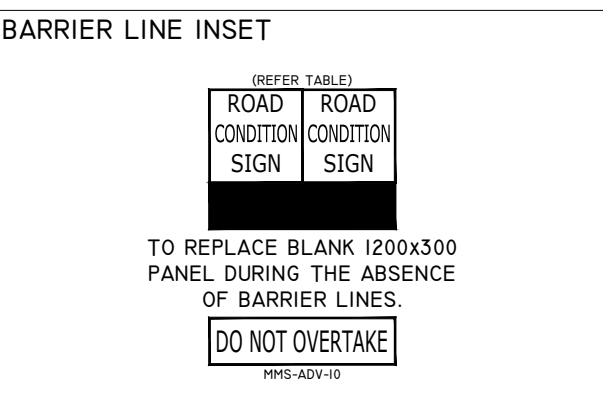

SCENARIO 1
UNSAFE EXCAVATION ADJACENT TO ROAD

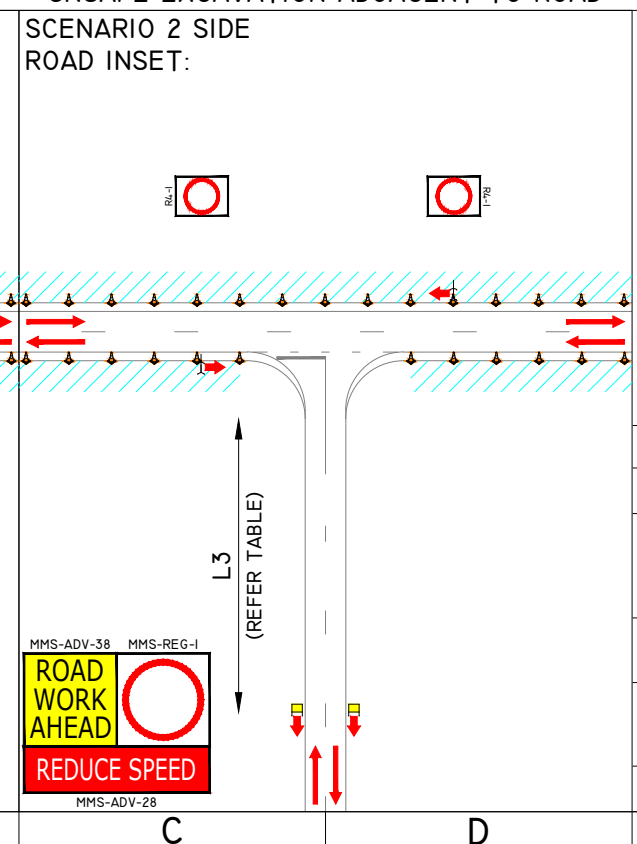

SCENARIO 2
UNSAFE EXCAVATION ADJACENT TO ROAD

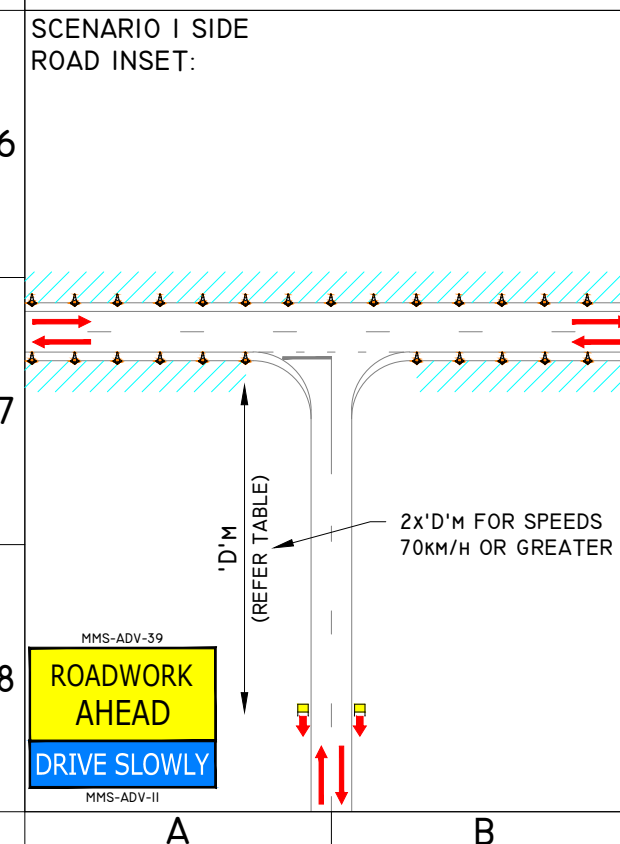

AFTERCARE CHECKLIST	
SIZE OF SITE	REDUCE THE EXTENTS OF THE WORKSITE AS MUCH AS POSSIBLE.
TEMPORARY SPEED LIMITS	IF TEMPORARY SPEED LIMITS HAVE BEEN INSTALLED, THE DESIGN SHOULD CONSIDER WHETHER THESE ARE STILL REQUIRED OR WHETHER THE TEMPORARY SPEED LIMIT SHOULD BE CHANGED (ALL CHANGES SHALL BE APPROVED)
UNSAFE CONDITIONS	NOTIFY MAIN ROADS WA OF ANY UNSAFE CONDITIONS I.E. LOOSE MATERIAL ON THE ROAD SURFACE, PLANT PARKED INCORRECTLY.
SIGNS	TTM SIGNS AND DEVICES NEED TO REMAIN IN PLACE AND SERVICEABLE WHILE THE SITE IS NOT ATTENDED, CHECK THAT ALL SIGNS ARE BALLASTED AND POSITIONED CORRECTLY.
DELINEATION	CHECK THAT ALL DELINEATION DEVICES ARE CLEAN AND POSITIONED CORRECTLY.

G		H			
TABLES					
SIGN SPACING					
AGTTM PART 3 - TABLE 2.2					
SPEED LIMIT (KM/H)		DISTANCE ('D') (M)			
55 OR LESS		15			
56 TO 65		45			
GREATER THAN 65		EQUAL TO SPEED OF TRAFFIC IN KM/H			
MAIN ROADS WA CoP SECTION 6.5.2 - TABLE 6					
SPEED LIMIT (KM/H)		L3 (M)			
90		180			
100		200			
110		220			
ROAD CONDITION SIGNS					
PLACEMENT ON EITHER SIDE OF FRAME					
(A) MMS-RC-8	(B) MMS-RC-4	(C) MMS-RC-9	(D) MMS-RC-10		
SOFT EDGES	NO LINES	TRAFFIC HAZARD	WATER OVER ROAD		
PLACEMENT ON RIGHT SIDE OF FRAME					
(E) MMS-RC-1	(F) MMS-RC-6	(G) MMS-RC-13			
					
PLACEMENT ON LEFT SIDE OF FRAME					
(H) MMS-RC-2	(I) MMS-RC-5	(J) MMS-RC-12			
LOOSE SURFACE	ROUGH SURFACE	WET BITUMEN			
EXCAVATION PROTECTIONS					
AGTTM PART 3 - TABLE 6.1					
SPEED (KM/H)	VOLUME (VPD)	CLEARANCE (M)	DEPTH (MM)		
			50-250	251-500	>500
LESS THAN OR EQUAL 65	ANY	LESS 2.5	01	02	03
		2.5 - 5	01	01	02
		GREATER 5	01	01	01
GREATER THAN OR EQUAL 70	LESS THAN 1500	LESS 5	01	02	03
	GREATER THAN 1501	GREATER 5.1	01	01	01
		LESS 6	01	02	03
		GREATER 6.1	01	01	01
PROTECTION OPTIONS:					

SCENARIO 1:

- NO SPEED REDUCTIONS REQUIRED WITH UNSAFE EXCAVATIONS ADJACENT TO ROAD.

SCENARIO 2:

- 80KM/H SPEED REDUCTION ON AN UNSEALED SECTION OF ROAD.

NOTES

TOLERANCES

POSITION OF SIGNS:
MINIMUM 10% LESS THAN THE DISTANCE OR LENGTHS GIVEN.
MAXIMUM 25% MORE THAN THE DISTANCES OR LENGTHS GIVEN.

SPACING OF DELINEATING DEVICES:
MAXIMUM 10% MORE THAN THE SPACING GIVEN.
NO MINIMUM.

AGTTM PART 6 SECTION 6.8.

DOCUMENTATION

ON-SITE VARIATIONS MUST BE APPROVED BY THE TRAFFIC MANAGEMENT SUPERVISOR, THAN AN ON-SITE VARIATION MADE AND CHANGES RECORDED IN THE DAILY DAIRY. FOR MORE INFORMATION REFER TO SECTION 9.3 OF THE TMP.

- ALL SIGN LOCATIONS ARE TO BE CHECKED ON SITE PRIOR TO SETOUT AND POSITIONS ADJUSTED AS PER THE 'TOLERANCES'.
- WHERE TEMPORARY SPEED REDUCTIONS ARE IMPLEMENTED, THEY MUST BE NO MORE THAN 20km/h LESS THAN THE POSTED SPEED LIMIT.
- PERIODIC INSPECTIONS OF THE SITE SHALL BE CONDUCTED AS PER AGTTM PART 6 SECTION 7.4 AFTERCARE - WORKSITE ARRANGEMENTS OUTSIDE WORKING HOURS. FOR BOX EDGED SIGN ALTERNATIVES, CONSULT AWTM PRIOR TO IMPLEMENTATION.

PEDESTRIAN MANAGEMENT

- 'PEDESTRIAN WATCH YOUR STEP' SIGN TO BE INSTALLED ON EACH APPROACH WHERE WORKS MAY ENCROACH ONTO OR ADJACENT TO EXISTING FOOTPATH FACILITIES.
- TM PERSONNEL TO MONITOR AND ESCORT PEDESTRIANS THROUGH THE WORK AREA AS REQUIRED.
- PEDESTRIANS MAY BE HELD ON EITHER END OF THE WORKSITE UNTIL IT IS SAFE TO PASS AS REQUIRED.

LEGEND

- EXISTING ROAD
- PROPOSED CONES
- WORKSITE

mainroads
WESTERN AUSTRALIA

METROPOLITAN REGIONS
TRAFFIC MANAGEMENT BRANCH

WATERLOO CRESCENT
TELEPHONE (08) 138 138

EAST PERTH 6004

DATE OF DRAWING 2025 JULY	SCALE -
LOCAL GOVERNMENT AUTHORITY -	POSTED SPEED -
ROAD AUTHORITY MAIN ROADS WA	WORKSITE SPEED -
CHECKED BY TYLER HARTLEY	SIGNATURE Tyler Hartley
ACCREDITATION RTM-0066	SIGNATURE Michael Reed
DESIGNED BY MICHAEL REED	SIGNATURE Michael Reed
ACCREDITATION AWTM-23-11536-02	SIGNATURE Michael Reed

GENERIC TRAFFIC GUIDANCE SCHEME
AFTERCARE MANAGEMENT
GENERAL AFTERCARE - TWO WAY ROAD
AND TEMPORARY SPEED ZONES (1/2)

DRAWING NO
0922-01531-AC-007A

REVISION
6