
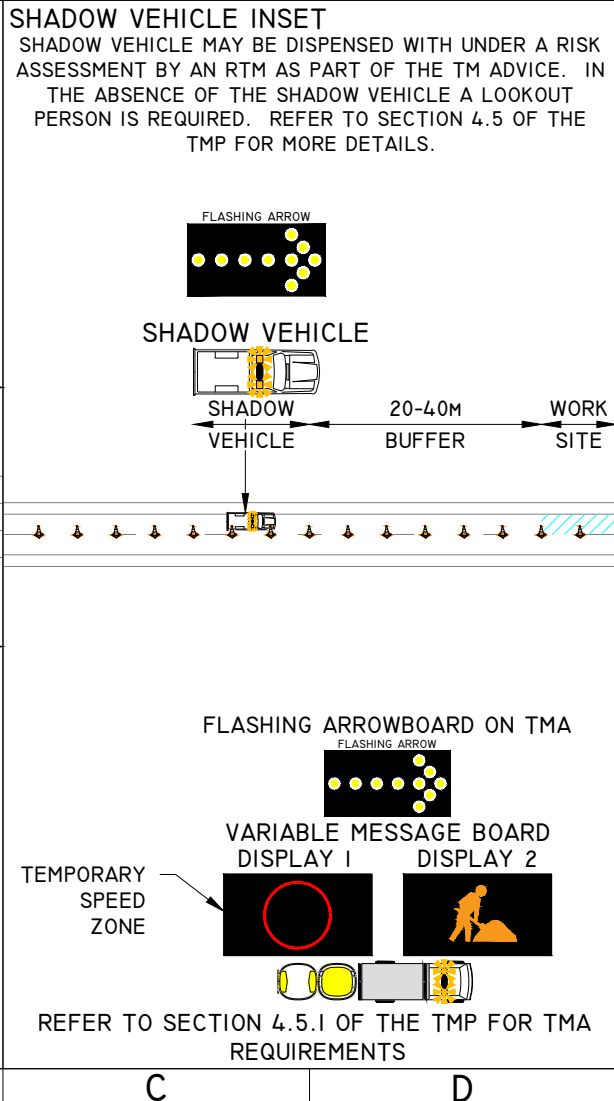
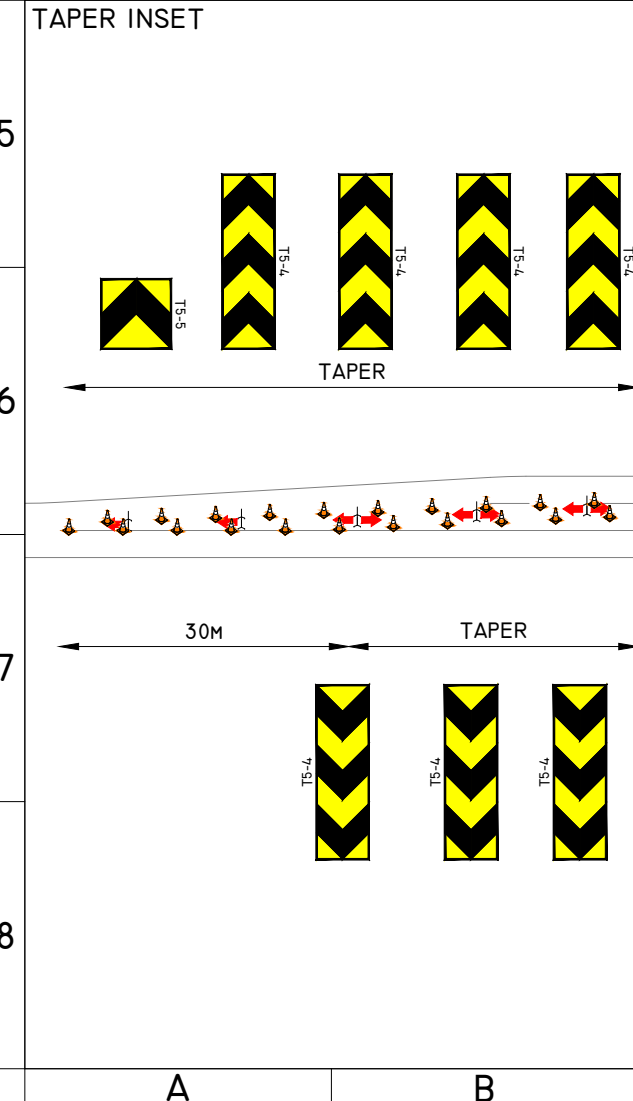


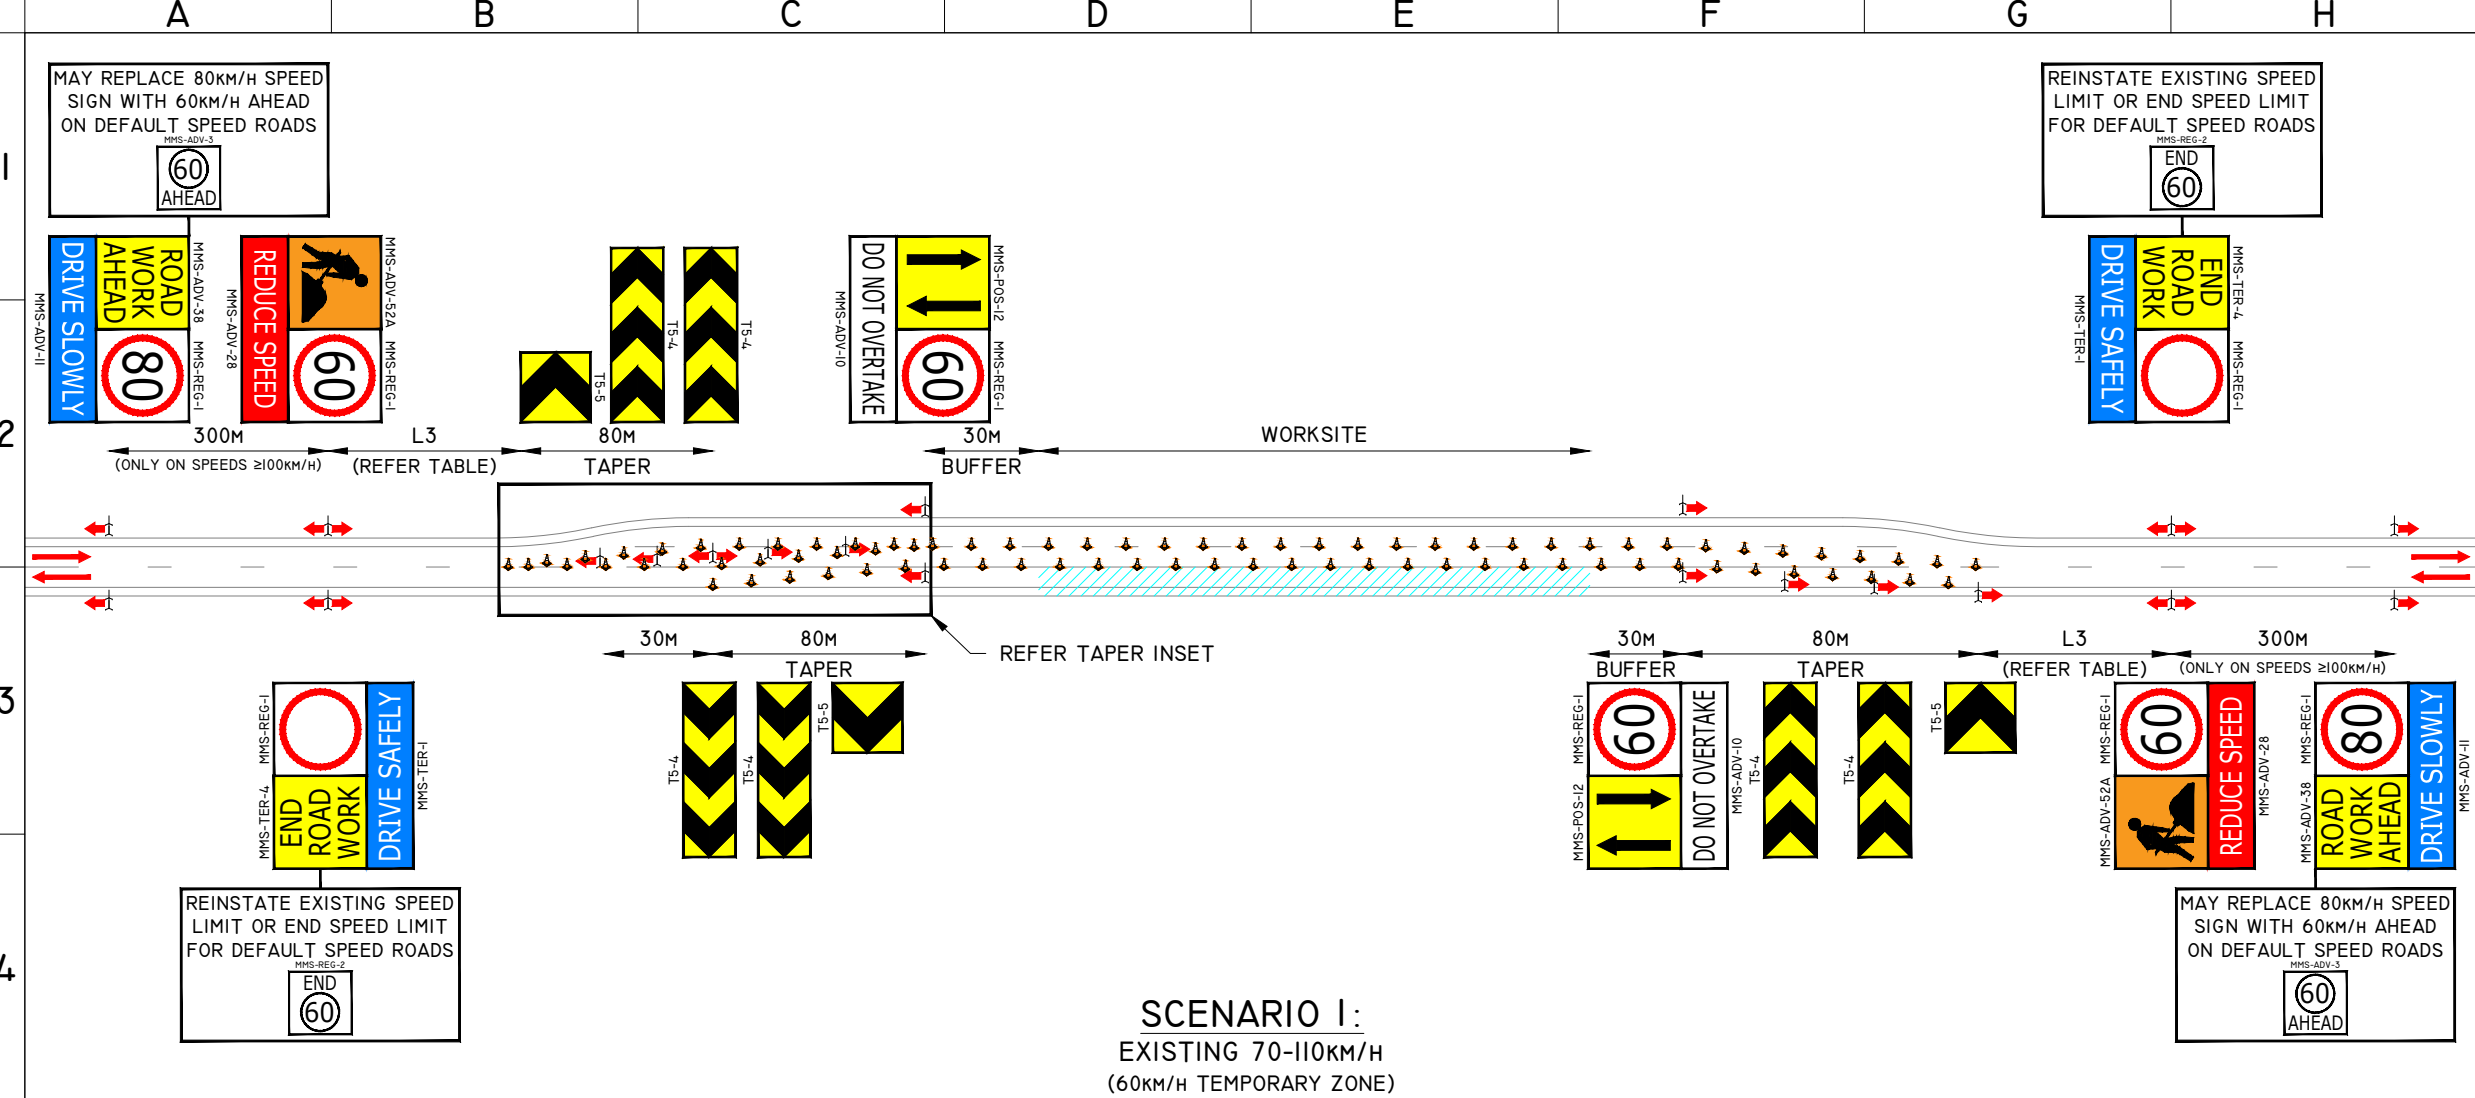

TABLES		
TEMPORARY HAZARD MARKERS		
AGTTM PART 3 - 5.4.2 PAGE 65		
A CONTINUOUS LINE OF T5-4 HAZARD MARKERS MUST BE MADE USING THE FOLLOWING RECOMMENDED NUMBERS.	NUMBER OF SHIFT MARKERS	LENGTH OF TAPER
	2	≤60M
	4	≤115M
	6	≤130M
	8	≤145M
	EVERY 20M	>145M
		WITHIN A CLOSED LANE
SIGN SPACING		
MAIN ROADS WA CoP SECTION 6.5.2 - TABLE 6		
SPEED LIMIT (KM/H)	L3 (M)	
70	70	
80	160	
90	180	
100 & 110	160	

NOTES

TOLERANCES

POSITION OF SIGNS:
MINIMUM 10% LESS THAN THE DISTANCE OR LENGTHS GIVEN.
MAXIMUM 25% MORE THAN THE DISTANCES OR LENGTHS GIVEN.

SPACING OF DELINEATING DEVICES:
MAXIMUM 10% MORE THAN THE SPACING GIVEN.
NO MINIMUM.

AGTTM PART 6 SECTION 6.8.

DOCUMENTATION

ON-SITE VARIATIONS MUST BE APPROVED BY THE TRAFFIC MANAGEMENT SUPERVISOR, THAN AN ON-SITE VARIATION MADE AND CHANGES RECORDED IN THE DAILY DAIRY. FOR MORE INFORMATION REFER TO SECTION 9.3 OF THE TMP.

- A RISK ASSESSMENT MUST BE CARRIED OUT TO DETERMINE THE REQUIREMENTS OF AFTERCARE.
- ALL SIGN LOCATIONS ARE TO BE CHECKED ON SITE PRIOR TO SETOUT AND POSITIONS ADJUSTED AS PER THE 'TOLERANCES'.
- FOR BOX EDGED SIGN ALTERNATIVES, CONSULT AWTM PRIOR TO IMPLEMENTATION.
- ALL CONTRADICTORY SIGNS WITHIN THE TM SETUP TO BE COVERED BY SUITABLY OPAQUE MATERIAL.
- REFER TO MANUFACTURING ADVICE FOR SHUNT DISTANCES ON TRUCK MOUNTED ATTENUATORS.
- REFER TO SECTION 4.1.8 OF THE TMP FOR THE MANDATORY USE OF SPEED FEEDBACK SIGNAGE

PEDESTRIAN MANAGEMENT

- 'PEDESTRIAN WATCH YOUR STEP' SIGN TO BE INSTALLED ON EACH APPROACH WHERE WORKS MAY ENCROACH ONTO OR ADJACENT TO EXISTING FOOTPATH FACILITIES.
- TM PERSONNEL TO MONITOR AND ESCORT PEDESTRIANS THROUGH THE WORK AREA AS REQUIRED.
- PEDESTRIANS MAY BE HELD ON EITHER END OF THE WORKSITE UNTIL IT IS SAFE TO PASS AS REQUIRED.

RECOMMENDED CONE SPACING

AGTTM PART 3 - TABLE 5.3

ALL PURPOSES:
(60 - 70km/h): 12M

PROTECTING FRESHLY PAINTED LINES:
(≤ 70km/h): 24M

RECOMMENDED LANE WIDTHS

MAIN ROADS WA CoP SECTION 6.7 - TABLE 9

RECOMMENDED LANE WIDTHS:
≤ 60km/h: 3.2M

MINIMUM LANE WIDTHS:
≤ 60km/h: 3.0M

LEGEND

EXISTING ROAD

PROPOSED CONES


WORKSITE



**METROPOLITAN REGIONS
TRAFFIC MANAGEMENT BRANCH**

WATERLOO CRESCENT
TELEPHONE (08) 138 138

EAST PERTH 6004

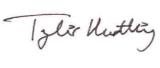DATE OF DRAWING 2025 JULY	SCALE -
LOCAL GOVERNMENT AUTHORITY -	POSTED SPEED 70-110km/h
ROAD AUTHORITY MAIN ROADS WA	WORKSITE SPEED 60km/h
CHECKED BY TYLER HARTLEY	SIGNATURE 
ACCREDITATION RTM-0066	SIGNATURE 
DESIGNED BY MICHAEL REED	
ACCREDITATION AWTM-23-11536-02	

GENERIC TRAFFIC GUIDANCE SCHEME
LANE CLOSURE SETUPS
OVERTAKING LANE CLOSURE
WORKSITE BETWEEN 1.2M AND 3.0M

DRAWING NO
0922-01531-LC-010

REVISION
6