

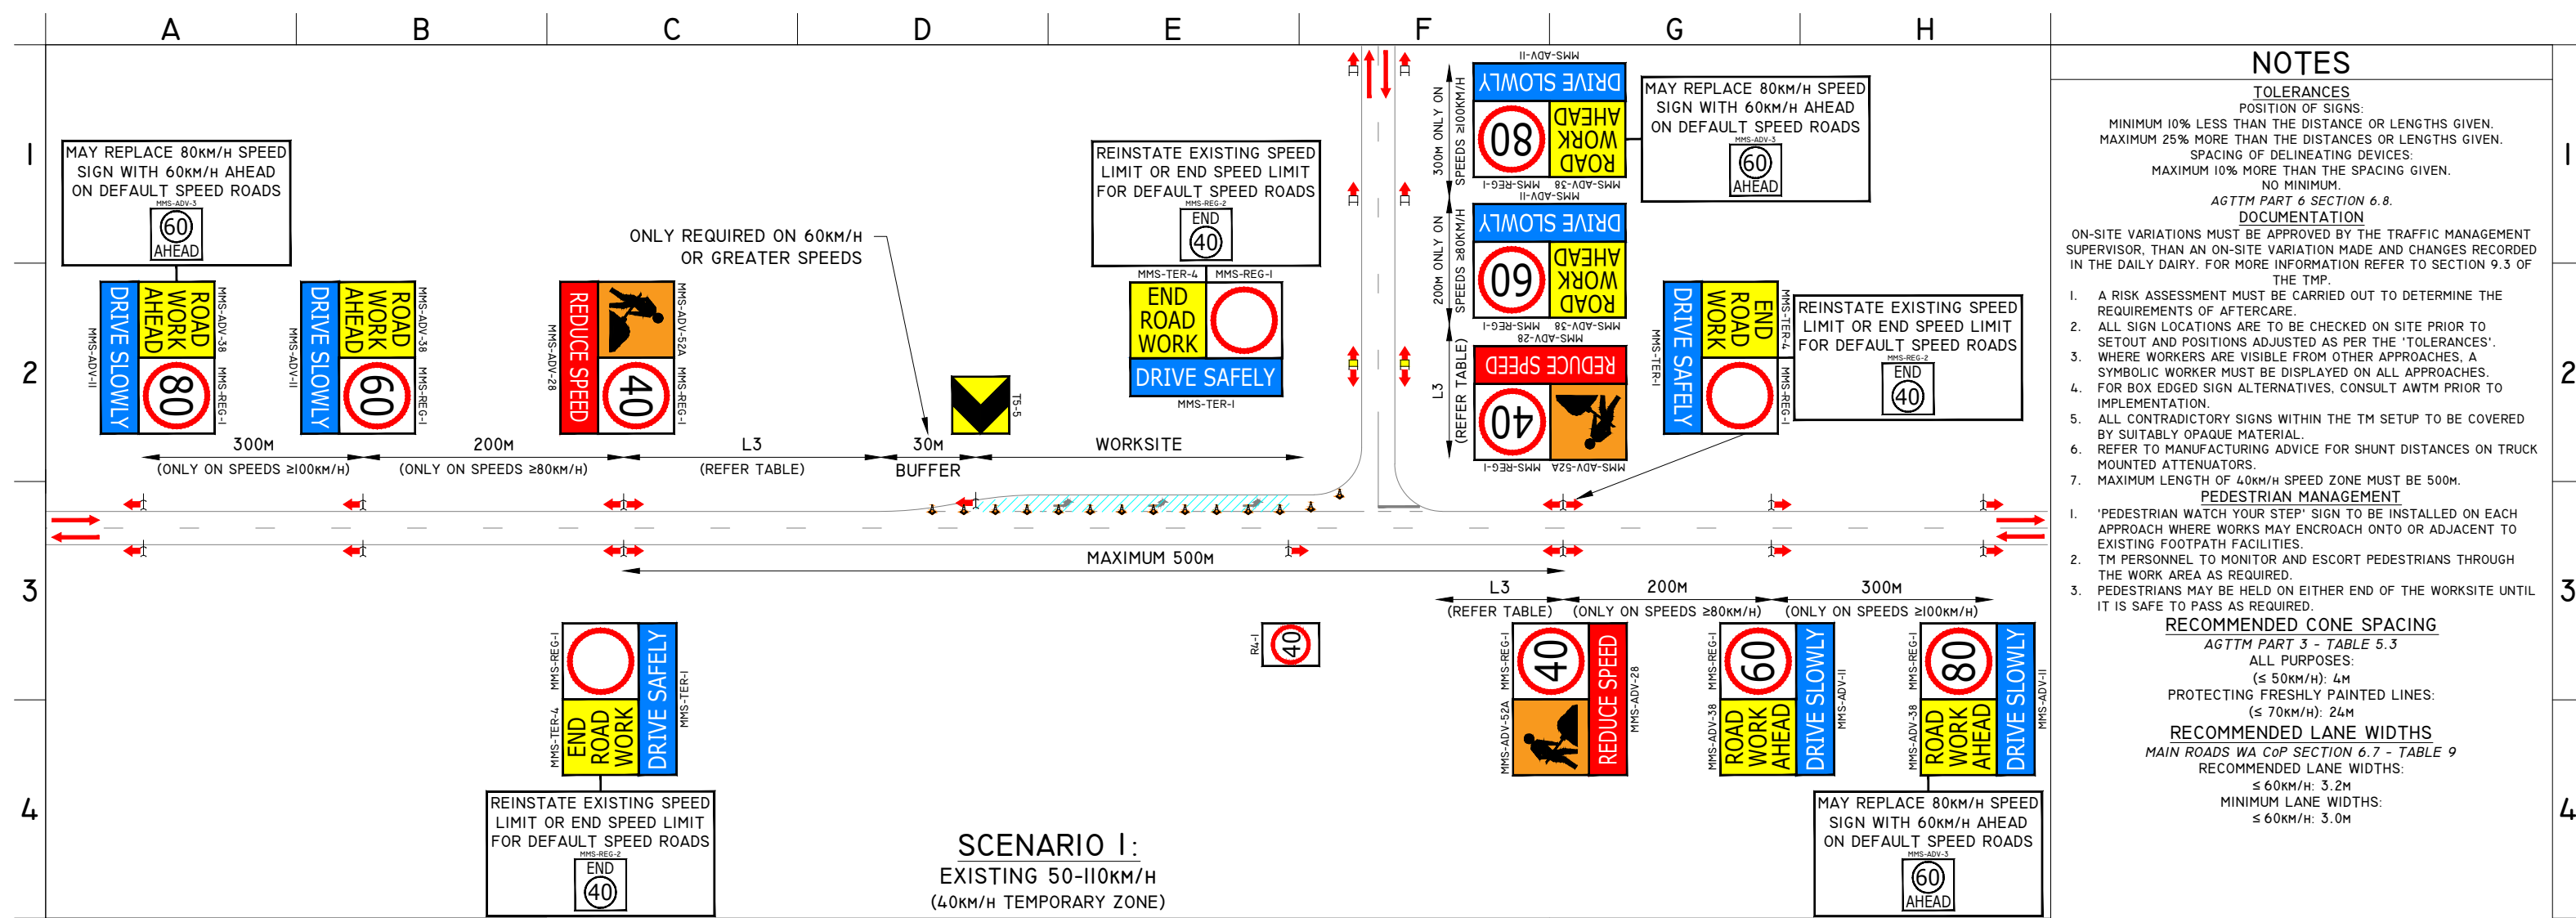


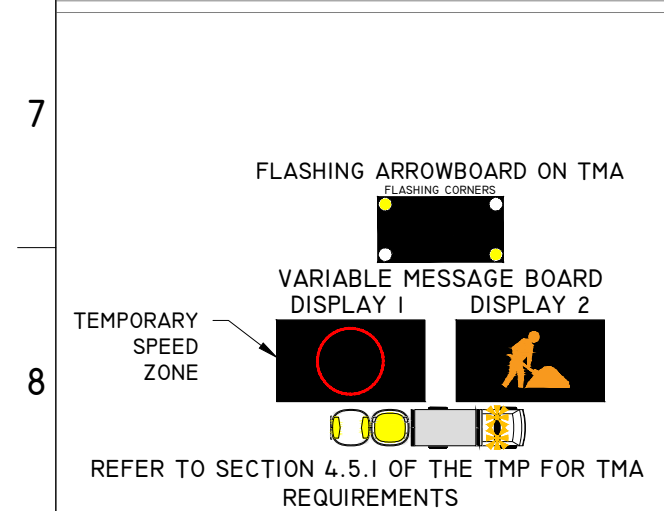


SHADOW VEHICLE INSET
(ONLY REQUIRED ON POSTED SPEEDS 80km/H OR GREATER)
SHADOW VEHICLE MAY BE DISPENSED WITH UNDER RISK
ASSESSMENT UNDERTAKEN BY AN AWTM AS PART OF THE
TM ADVICE OR A WTM ON SITE. IN THE ABSENCE OF
SHADOW VEHICLE A LOOKOUT PERSON IS REQUIRED. REFER
TO SECTION 4.5 OF THE TMP FOR MORE DETAILS.

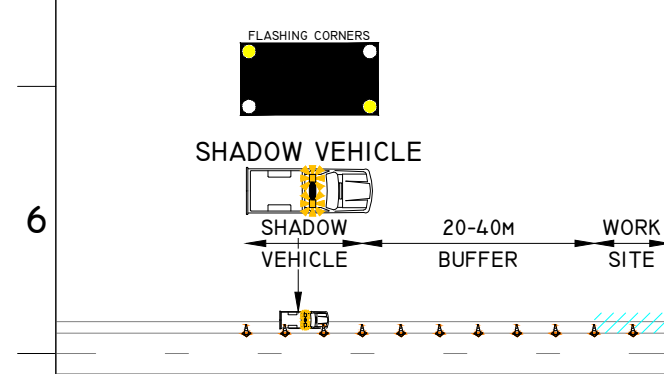

TABLES SIGN SPACING <i>AGTTM PART 3 - TABLE 2.2</i>	
SPEED LIMIT (KM/H)	DISTANCE ('D') (M)
55 OR LESS	15
56 TO 65	45
GREATER THAN 65	EQUAL TO SPEED OF TRAFFIC IN KM/H
<i>MAIN ROADS WA CoP SECTION 6.5.2 - TABLE 6</i>	
SPEED LIMIT (KM/H)	L3 (M)
60 OR LESS	45
70	70
80 OR GREATER	90

LEGEND

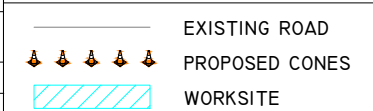

**METROPOLITAN REGIONS
TRAFFIC MANAGEMENT BRANCH**
WATERLOO CRESCENT
TELEPHONE (08) 138 138 EAST PERTH 6004

DATE OF DRAWING 2025 JULY	SCALE -
LOCAL GOVERNMENT AUTHORITY -	POSTED SPEED 50-110KM/H
ROAD AUTHORITY MAIN ROADS WA	WORKSITE SPEED 40KM/H
CHECKED BY TYLER HARTLEY	SIGNATURE 
ACCREDITATION RTM-0066	
DESIGNED BY MICHAEL REED	SIGNATURE 
ACCREDITATION AWTM-23-11536-02	
GENERIC TRAFFIC GUIDANCE SCHEME LANE CLOSURE SETUPS LEFT TURN POCKET CLOSURE WORKSITE WITHIN 1.2M	
DRAWING NO 0922-01531-LC-032	REVISION 6