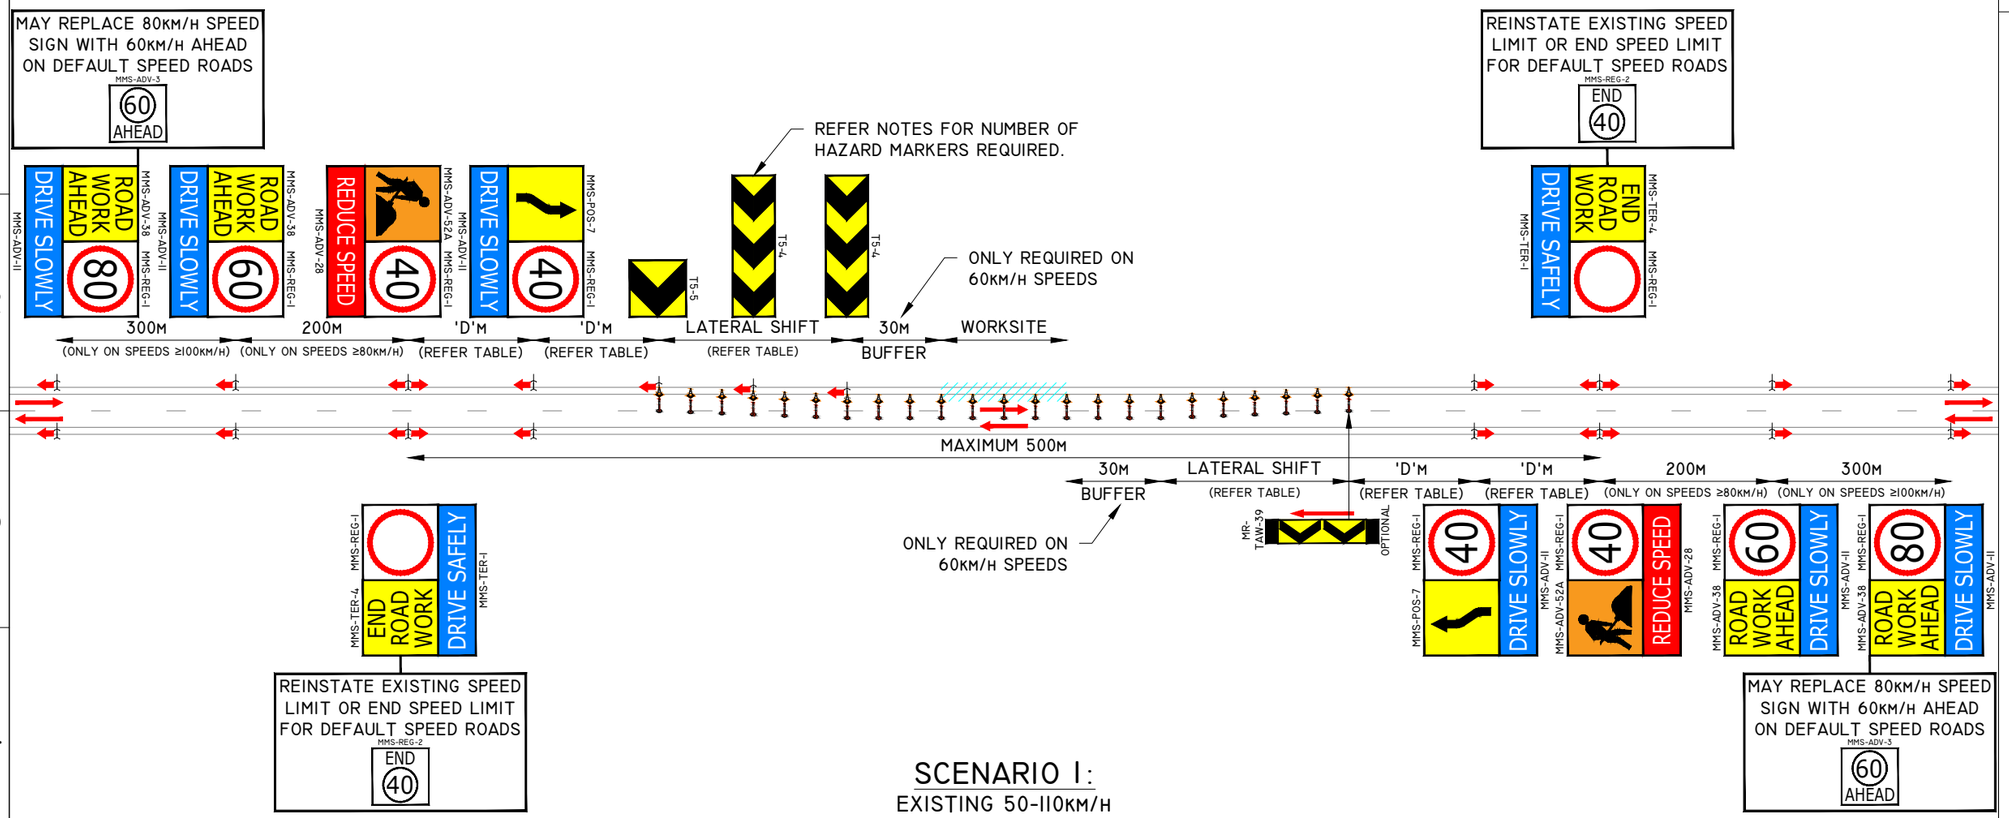

NOTES

TOLERANCES

POSITION OF SIGNS:
MINIMUM 10% LESS THAN THE DISTANCE OR LENGTHS GIVEN.
MAXIMUM 25% MORE THAN THE DISTANCES OR LENGTHS GIVEN.
SPACING OF DELINEATING DEVICES:
MAXIMUM 10% MORE THAN THE SPACING GIVEN.
NO MINIMUM.
AGTTM PART 6 SECTION 6.8.

DOCUMENTATION

ON-SITE VARIATIONS MUST BE APPROVED BY THE TRAFFIC MANAGEMENT SUPERVISOR, THAN AN ON-SITE VARIATION MADE AND CHANGES RECORDED IN THE DAILY DAIRY. FOR MORE INFORMATION REFER TO SECTION 9.3 OF THE TMP.

1. A RISK ASSESSMENT MUST BE CARRIED OUT TO DETERMINE THE REQUIREMENTS OF AFTERCARE.
2. ALL SIGN LOCATIONS ARE TO BE CHECKED ON SITE PRIOR TO SETOUT AND POSITIONS ADJUSTED AS PER THE 'TOLERANCES'.
3. ALL CONTRADICTORY SIGNS WITHIN THE TM SETUP TO BE COVERED BY SUITABLY OPAQUE MATERIAL.
4. FOR BOX EDGED SIGN ALTERNATIVES, CONSULT AWTM PRIOR TO IMPLEMENTATION.
5. MAXIMUM LENGTH OF 40KM/H SPEED ZONE MUST BE 500M.
6. REFER TO SECTION 4.1.8 OF THE TMP FOR THE MANDATORY USE OF SPEED FEEDBACK SIGNAGE

PEDESTRIAN MANAGEMENT

1. 'PEDESTRIAN WATCH YOUR STEP' SIGN TO BE INSTALLED ON EACH APPROACH WHERE WORKS MAY ENCROACH ONTO OR ADJACENT TO EXISTING FOOTPATH FACILITIES.
2. TM PERSONNEL TO MONITOR AND ESCORT PEDESTRIANS THROUGH THE WORK AREA AS REQUIRED.
3. PEDESTRIANS MAY BE HELD ON EITHER END OF THE WORKSITE UNTIL IT IS SAFE TO PASS AS REQUIRED.

RECOMMENDED CONE SPACING

AGTTM PART 3 - TABLE 5.3
ALL PURPOSES:
(≤ 50KM/H): 4M
PROTECTING FRESHLY PAINTED LINES:
(≤ 70KM/H): 24M

RECOMMENDED LANE WIDTHS

MAIN ROADS WA CoP SECTION 6.7 - TABLE 7
RECOMMENDED LANE WIDTHS:
≤ 60KM/H: 3.2M
MINIMUM LANE WIDTHS:
≤ 60KM/H: 3.0M

SHADOW VEHICLE INSET

SHADOW VEHICLE MAY BE DISPENSED WITH UNDER A RISK ASSESSMENT BY AN RTM AS PART OF THE TM ADVICE. IN THE ABSENCE OF THE SHADOW VEHICLE A LOOKOUT PERSON IS REQUIRED. REFER TO SECTION 4.5 OF THE TMP FOR MORE DETAILS.

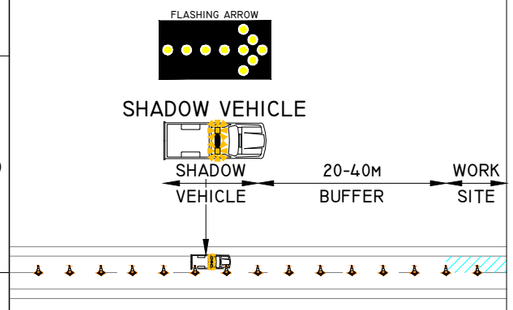

FLASHING ARROWBOARD ON TMA

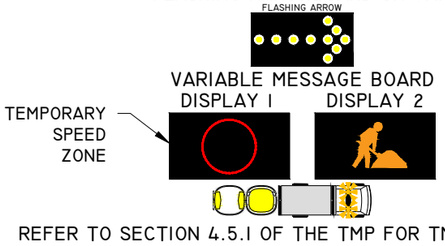

REFER TO SECTION 4.5.1 OF THE TMP FOR TMA REQUIREMENTS

TABLES

TAPER LENGTHS

AGTTM PART 3 - TABLE 5.7

SPEED LIMIT (KM/H)	LATERAL SHIFT TAPER (M)
45 OR LESS	5
46 TO 55	15
56 TO 65	30
66 TO 75*	70
76 TO 85*	80
86 TO 95*	90
96 TO 105*	100
GREATER THAN 105*	110

*TAPER LENGTHS ARE BASED ON A:
- 3.5M WIDTH OF THE LANE TO BE CLOSED
- LATERAL SHIFT TAPER LENGTH EQUAL TO 1.0M/S
- MEDIAN SPEED FOR EACH RANGE (I.E 76 - 85 = 80KM/H

TEMPORARY HAZARD MARKERS

AGTTM PART 3 - 5.4.2 PAGE 65

A CONTINUOUS LINE OF T5-4 HAZARD MARKERS MUST BE MADE USING THE FOLLOWING RECOMMENDED NUMBERS.

T5-4

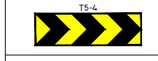

NUMBER OF SHIFT MARKERS	LENGTH OF TAPER
2	≤60M
4	≤115M
6	≤130M
8	≤145M
EVERY 20M	>145M
	WITHIN A CLOSED LANE

SIGN SPACING

AGTTM PART 3 - TABLE 2.2

SPEED LIMIT (KM/H)	DISTANCE ('D') (M)
55 OR LESS	15
56 TO 65	45
GREATER THAN 65	EQUAL TO SPEED OF TRAFFIC IN KM/H

LEGEND

- EXISTING ROAD
- PROPOSED CONES
- PROPOSED TEMPORARY BOLLARDS
- WORKSITE

METROPOLITAN REGIONS
TRAFFIC MANAGEMENT BRANCH
WATERLOO CRESCENT EAST PERTH 6004
TELEPHONE (08) 138 138

DATE OF DRAWING: 2025 JULY	SCALE: -
LOCAL GOVERNMENT AUTHORITY: -	POSTED SPEED: 50-110KM/H
ROAD AUTHORITY: MAIN ROADS WA	WORKSITE SPEED: 40KM/H
CHECKED BY: TYLER HARTLEY	SIGNATURE: Tyler Hartley
ACCREDITATION: RTM-0066	
DESIGNED BY: MICHAEL REED	SIGNATURE: Michael Reed
ACCREDITATION: AWTM-23-11536-02	

GENERIC TRAFFIC GUIDANCE SCHEME
LATERAL SHIFT SETUPS
TWO WAY ROAD LATERAL SHIFT
WORKSITE WITHIN 1.2M

DRAWING NO	REVISION
0922-01531-LS-002	6