
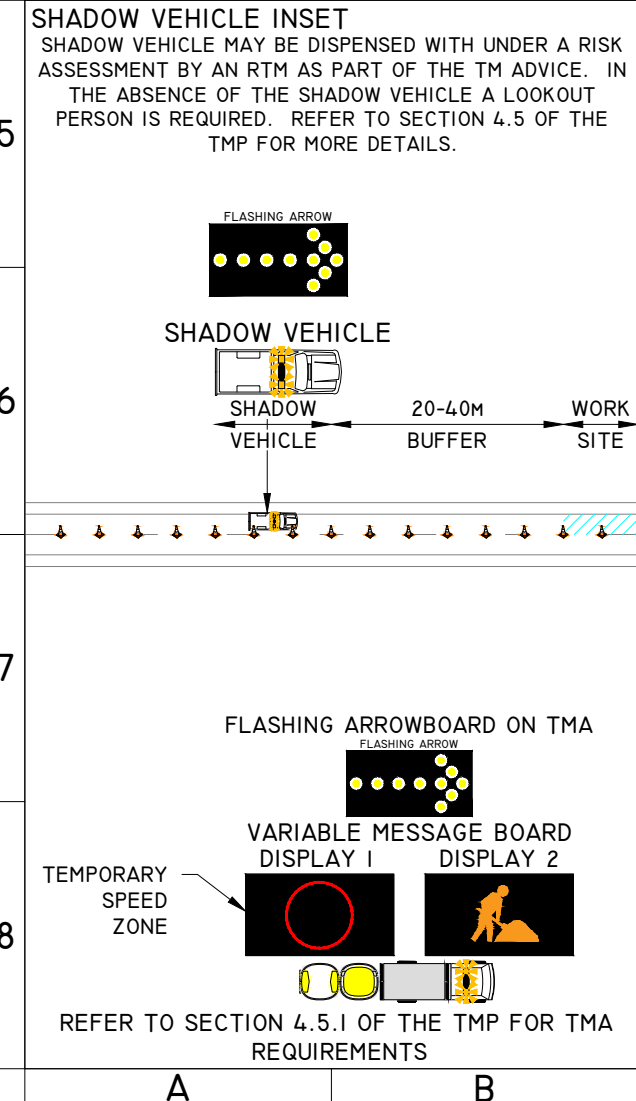


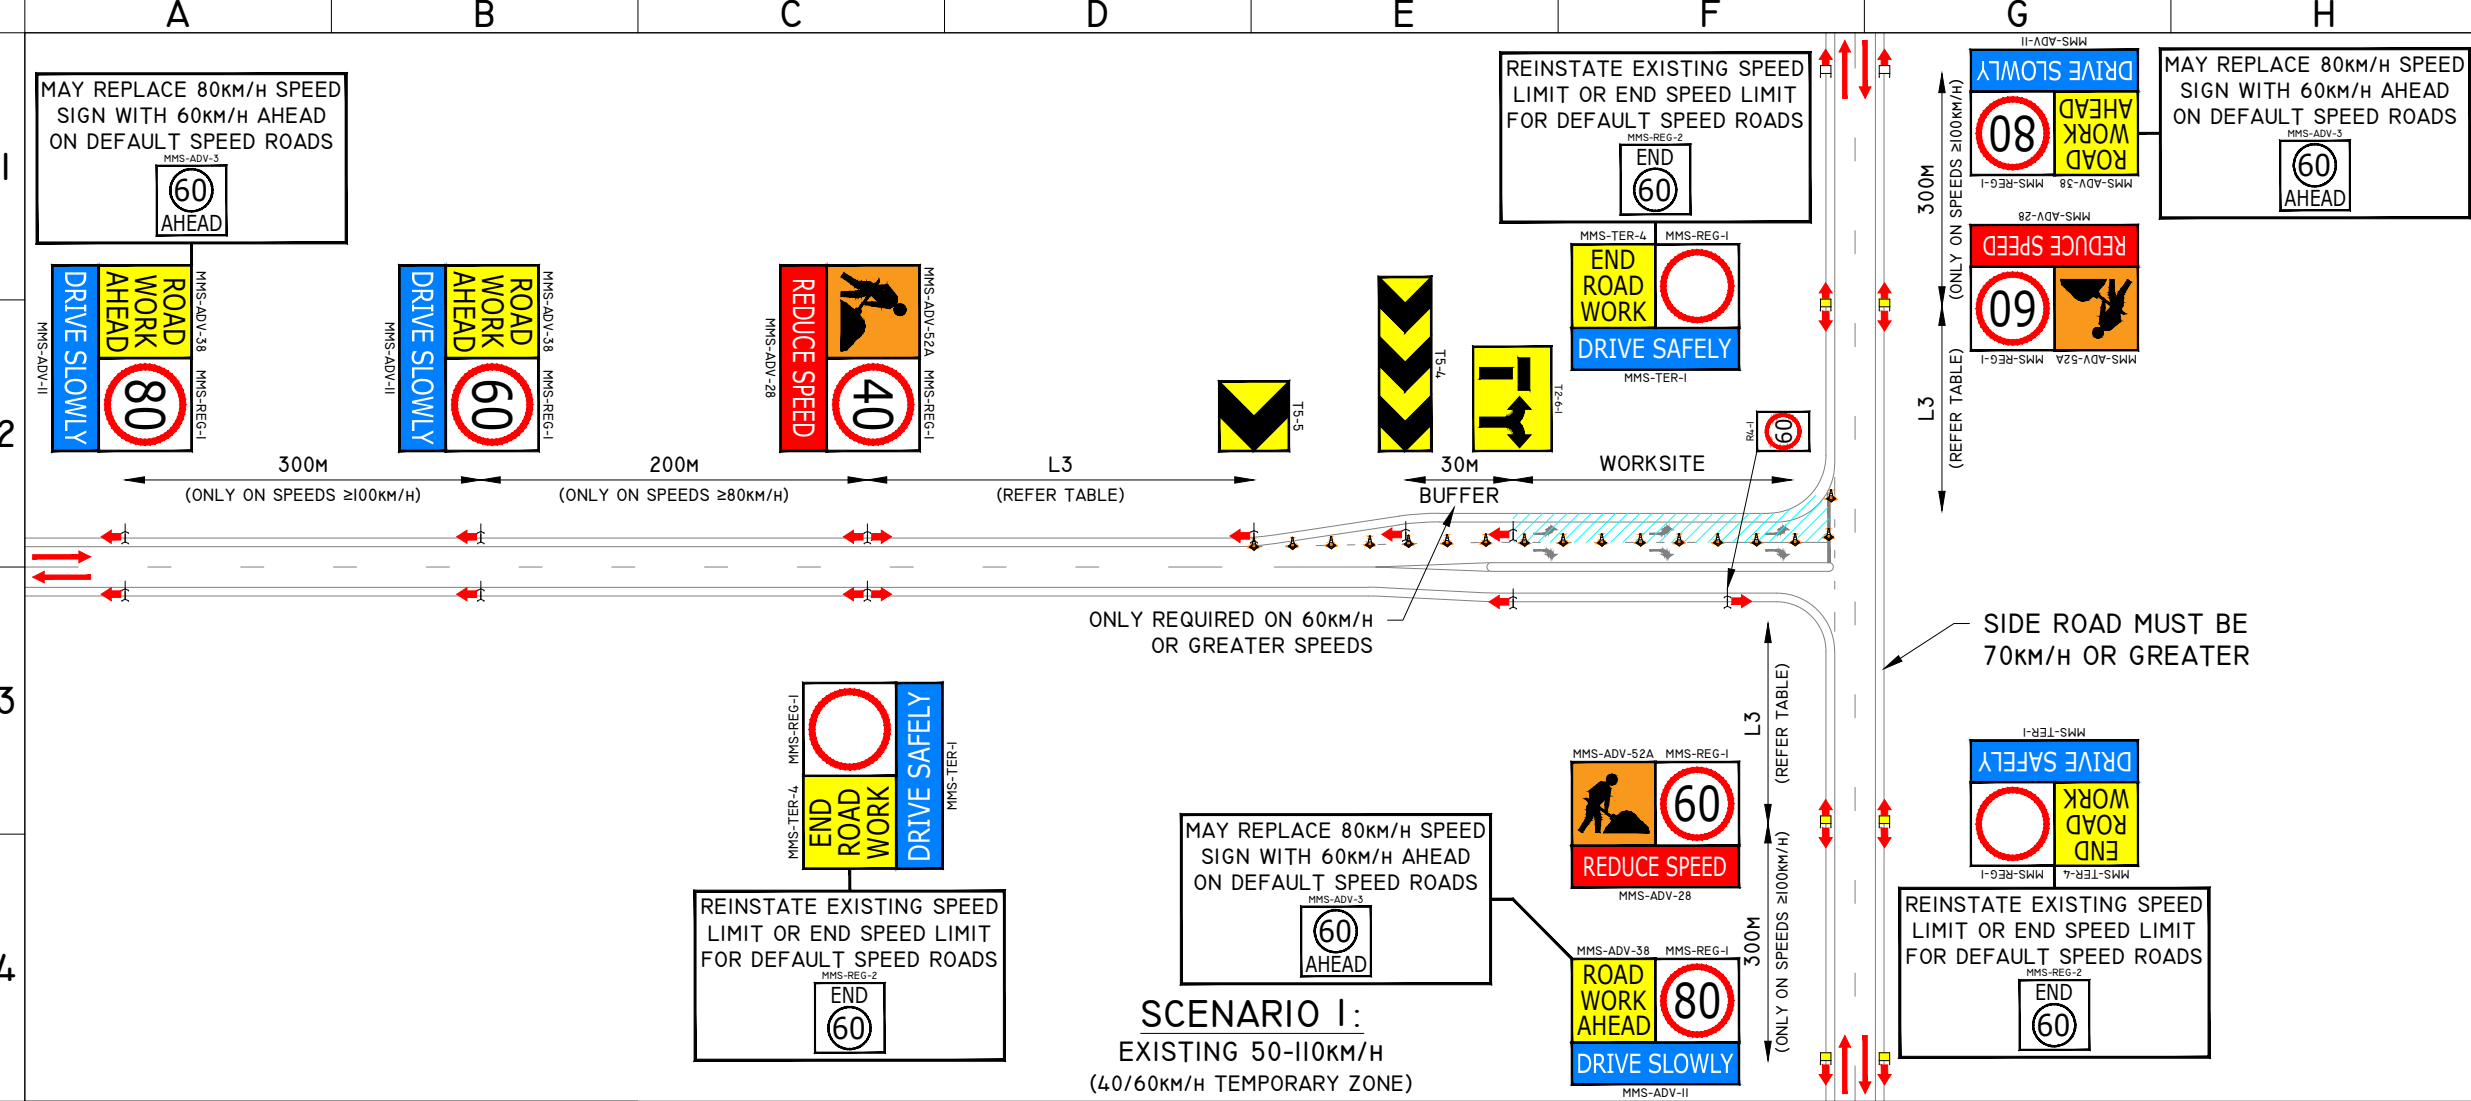

NOTES

TOLERANCES
POSITION OF SIGNS:
MINIMUM 10% LESS THAN THE DISTANCE OR LENGTHS GIVEN.
MAXIMUM 25% MORE THAN THE DISTANCES OR LENGTHS GIVEN.

SPACING OF DELINEATING DEVICES:
MAXIMUM 10% MORE THAN THE SPACING GIVEN.
NO MINIMUM.

AGTTM PART 6 SECTION 6.8.

DOCUMENTATION
ON-SITE VARIATIONS MUST BE APPROVED BY THE TRAFFIC MANAGEMENT SUPERVISOR, THAN AN ON-SITE VARIATION MADE AND CHANGES RECORDED IN THE DAILY DAIRY. FOR MORE INFORMATION REFER TO SECTION 9.3 OF THE TMP.

- A RISK ASSESSMENT MUST BE CARRIED OUT TO DETERMINE THE REQUIREMENTS OF AFTERCARE.
- ALL SIGN LOCATIONS ARE TO BE CHECKED ON SITE PRIOR TO SETOUT AND POSITIONS ADJUSTED AS PER THE 'TOLERANCES'.
- ALL CONTRADICTORY SIGNS WITHIN THE TM SETUP TO BE COVERED BY SUITABLY OPAQUE MATERIAL.
- FOR BOX EDGED SIGN ALTERNATIVES, CONSULT AWTM PRIOR TO IMPLEMENTATION.
- MAXIMUM LENGTH OF 40km/h SPEED ZONE MUST BE 500M.
- REFER TO SECTION 4.1.8 OF THE TMP FOR THE MANDATORY USE OF SPEED FEEDBACK SIGNAGE

PEDESTRIAN MANAGEMENT

- 'PEDESTRIAN WATCH YOUR STEP' SIGN TO BE INSTALLED ON EACH APPROACH WHERE WORKS MAY ENCROACH ONTO OR ADJACENT TO EXISTING FOOTPATH FACILITIES.
- TM PERSONNEL TO MONITOR AND ESCORT PEDESTRIANS THROUGH THE WORK AREA AS REQUIRED.
- PEDESTRIANS MAY BE HELD ON EITHER END OF THE WORKSITE UNTIL IT IS SAFE TO PASS AS REQUIRED.

RECOMMENDED CONE SPACING
AGTTM PART 3 - TABLE 5.3
ALL PURPOSES:
(≤ 50km/h): 4M
(60 - 70km/h): 12M
PROTECTING FRESHLY PAINTED LINES:
(≤ 70km/h): 24M

RECOMMENDED LANE WIDTHS
MAIN ROADS WA CoP SECTION 6.7 - TABLE 7
RECOMMENDED LANE WIDTHS:
≤ 60km/h: 3.2M
MINIMUM LANE WIDTHS:
≤ 60km/h: 3.0M

LEGEND

EXISTING ROAD
PROPOSED CONES
WORKSITE

mainroads
WESTERN AUSTRALIA

METROPOLITAN REGIONS
TRAFFIC MANAGEMENT BRANCH
WATERLOO CRESCENT
TELEPHONE (08) 138 138
EAST PERTH 6004

DATE OF DRAWING 2025 JULY	SCALE -
LOCAL GOVERNMENT AUTHORITY -	POSTED SPEED 50-110km/h
ROAD AUTHORITY MAIN ROADS WA	WORKSITE SPEED 40/60km/h
CHECKED BY TYLER HARTLEY	SIGNATURE
ACCREDITATION RTM-0066	
DESIGNED BY MICHAEL REED	SIGNATURE
ACCREDITATION AWTM-23-11536-02	

GENERIC TRAFFIC GUIDANCE SCHEME
LATERAL SHIFT SETUPS
T-JUNCTION - TURN POCKET CLOSURE
WORKSITE ADJACENT TO LIVE TRAFFIC

DRAWING NO 0922-01531-LS-015	REVISION 6
---------------------------------	---------------

TABLES

SIGN SPACING

MAIN ROADS WA CoP SECTION 6.5.2 - TABLE 6

SPEED LIMIT (KM/H)	L3 (M)
60 OR LESS	45
70	70
80 OR GREATER	90