SCENARIO 1:

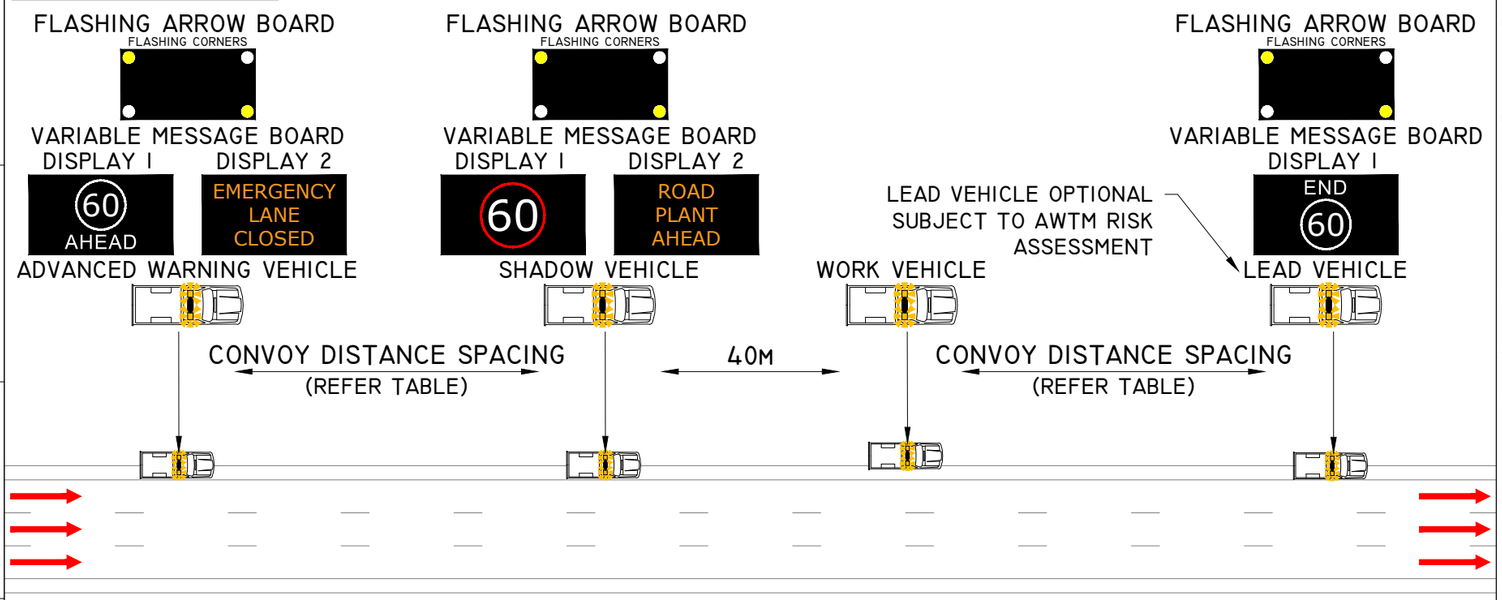

CLASS 2 MOBILE SCENARIO

VEHICLES TRAVELLING GREATER THAN 20KM/H BELOW THE SPEED LIMIT
(NO WORKERS ON FOOT)

SCENARIO 2:

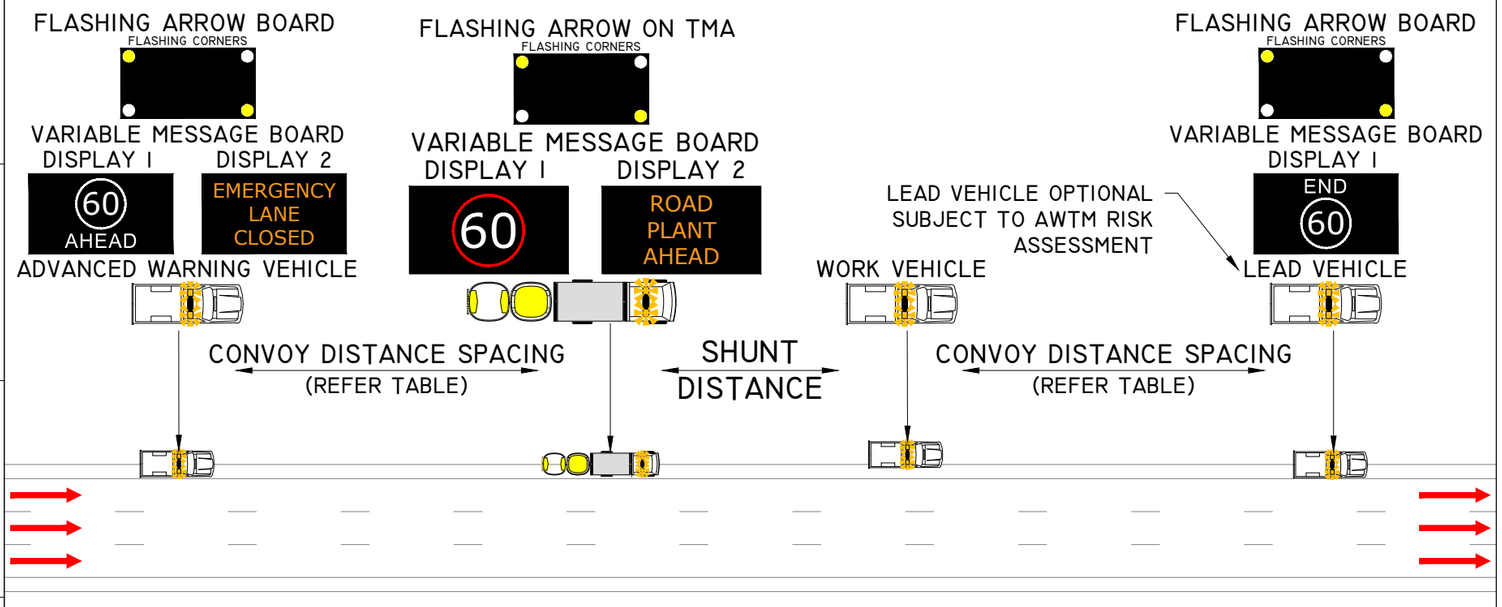

CLASS 2 MOBILE SCENARIO

VEHICLES TRAVELLING GREATER THAN 20KM/H BELOW THE SPEED LIMIT
(NO WORKERS ON FOOT)
TRUCK MOUNTED ATTENUATORS.

SCENARIO 1:

WORKS PROTECTED BY SHADOW VEHICLE

1. A RISK ASSESSMENT MAY BE PROVIDED FOR THE USE OF TRUCK MOUNTED ATTENUATOR IN PLACE OF THE SHADOW VEHICLE.

SCENARIO 2:

WORKS PROTECTED BY TMA

1. REFER TO THE MRWA REQUIREMENTS FOR THE USE OF TRUCK MOUNTED ATTENUATORS IN WA OR SECTION 4.5.1 OF THE TMP.

NOTES

1. WHERE WORKSITE CLEARANCES CANNOT BE ACHIEVED, ANOTHER MOBILE SCENARIO OR A STATIC SETUP MAY BE REQUIRED.
2. THIS DRAWING IS FOR LARGE PLANT ITEMS ONLY AND THERE MUST BE NO WORKERS ON FOOT. THIS SCENARIO IS TO BE USED FOR CLASS 2 MOBILE WORKS, WHERE MOBILE CONVOY TRAVELS GREATER THAN 20KM/H OF TRAFFIC SPEED.
3. WHERE THE CONVOY IS REQUIRED TO STOP FOR AN EXTENDED PERIOD OF TIME, A SHORT TERM LOW IMPACT OR SITE SPECIFIC DRAWING MUST BE USED.
4. PRIOR TO THE IMPLEMENTATION OF ANY MOBILE CONVOYS, A RISK ASSESSMENT IS REQUIRED TO DETERMINE IF THE WORKS CAN BE COMPLETED SAFELY. REFER TO THE TMP FOR RISK CONSIDERATIONS.
5. WHERE THERE IS POOR SIGHT DISTANCE DUE TO CURVE OR CREST IN THE ROAD THE ADVANCED WARNING VEHICLE MUST STOP PRIOR TO THE REDUCED SIGHT DISTANCE LOCATION WHILE THE REST OF THE CONVOY TRAVEL THROUGH. WHERE THERE IS SIGNIFICANT SECTIONS OF POOR SIGHT DISTANCE AN ADDITIONAL SHADOW VEHICLE MAY BE USED.
6. ALL DRIVERS WITHIN MOBILE CONVOY MUST BE ALERT AND AWARE OF APPROACHING VEHICLES AT ALL TIMES.
7. ALL VEHICLES WITHIN MOBILE CONVOY MUST HAVE CLEAR COMMUNICATION METHODS USING TWO-WAY RADIO DEVICES.
8. VEHICLE LOCATIONS MUST CONSIDER THE IMPACT ON VULNERABLE ROAD USERS AND CYCLISTS.
9. REFER TO MANUFACTURING ADVICE FOR SHUNT DISTANCES ON TRUCK MOUNTED ATTENUATORS.
10. WHEN A MOBILE CONVOY CONTAINS MORE THAN ONE WORK VEHICLE, EACH VEHICLE MUST BE 40M APART AS A MAXIMUM. WHERE THIS IS NOT PRACTICABLE, EACH WORK VEHICLE MUST BE TREATED AS A SEPARATE MOBILE OPERATION WITH THEIR OWN WORK CONVOY. EACH WORK VEHICLE MUST ADHERE TO THE CLEARANCES TO LIVE TRAFFIC LANE TABLE.
11. NUMBER OF LANES AND CONFIGURATION OF ROAD ARE INDICATIVE ONLY.
12. WHEN THE SPEED LIMIT IS REDUCED BY MORE THAN 20KM/H, CONSIDER THE USE OF MULTIPLE ADVANCE WARNING VEHICLES TO DECREASE THE SPEED IN STEPS, WHERE THIS IS NOT IMPLEMENTED A RISK ASSESSMENT MUST BE COMPLETED.

DOCUMENTATION

DAILY RECORDS OF THE SITE LAYOUT INCLUDING DEVICES, SIGHT DISTANCE, RISK ASSESSMENTS, SIGNS OR TGS, MUST BE KEPT IN A DIARY OR IN WORK SHEETS (DAILY DIARY). ANY SIGNIFICANT DEPARTURES FROM, OR ADDITIONS TO, THE SIGNS AND DEVICES INCLUDED IN THIS DIAGRAM SHOULD BE NOTED AND APPROVED.

TABLES

DISTANCE BETWEEN VEHICLES IN MOBILE CONVOY - EXCLUDING SHADOW VEHICLE

AGTTM PART 4 - TABLE 3.1

SPEED LIMIT (KM/H)	DISTANCE (M)
≤45	50
46-55	70
56-65	90
66-75	110
76-85	140
86-95	160
96-105	200
>106	230

LEGEND

EXISTING ROAD

METROPOLITAN REGIONS
TRAFFIC MANAGEMENT BRANCH
WATERLOO CRESCENT EAST PERTH 6004
TELEPHONE (08) 138 138

DATE OF DRAWING: 2025 JULY	SCALE: -
LOCAL GOVERNMENT AUTHORITY: -	POSTED SPEED: -
ROAD AUTHORITY: MAIN ROADS WA	WORKSITE SPEED: 60KM/H
CHECKED BY: TYLER HARTLEY	SIGNATURE: Tyler Hartley
ACCREDITATION: RTM-0066	
DESIGNED BY: MICHAEL REED	SIGNATURE:
ACCREDITATION: AWTM-23-11536-02	

GENERIC TRAFFIC GUIDANCE SCHEME
CLASS 2 - MOBILE SCENARIOS
EMERGENCY LANE CONVOY 60KM/H
WORK VEHICLE BETWEEN 1.2M AND 3.0M

DRAWING NO: 0922-01531-MS2-002	REVISION: 6