



SCENARIO I:

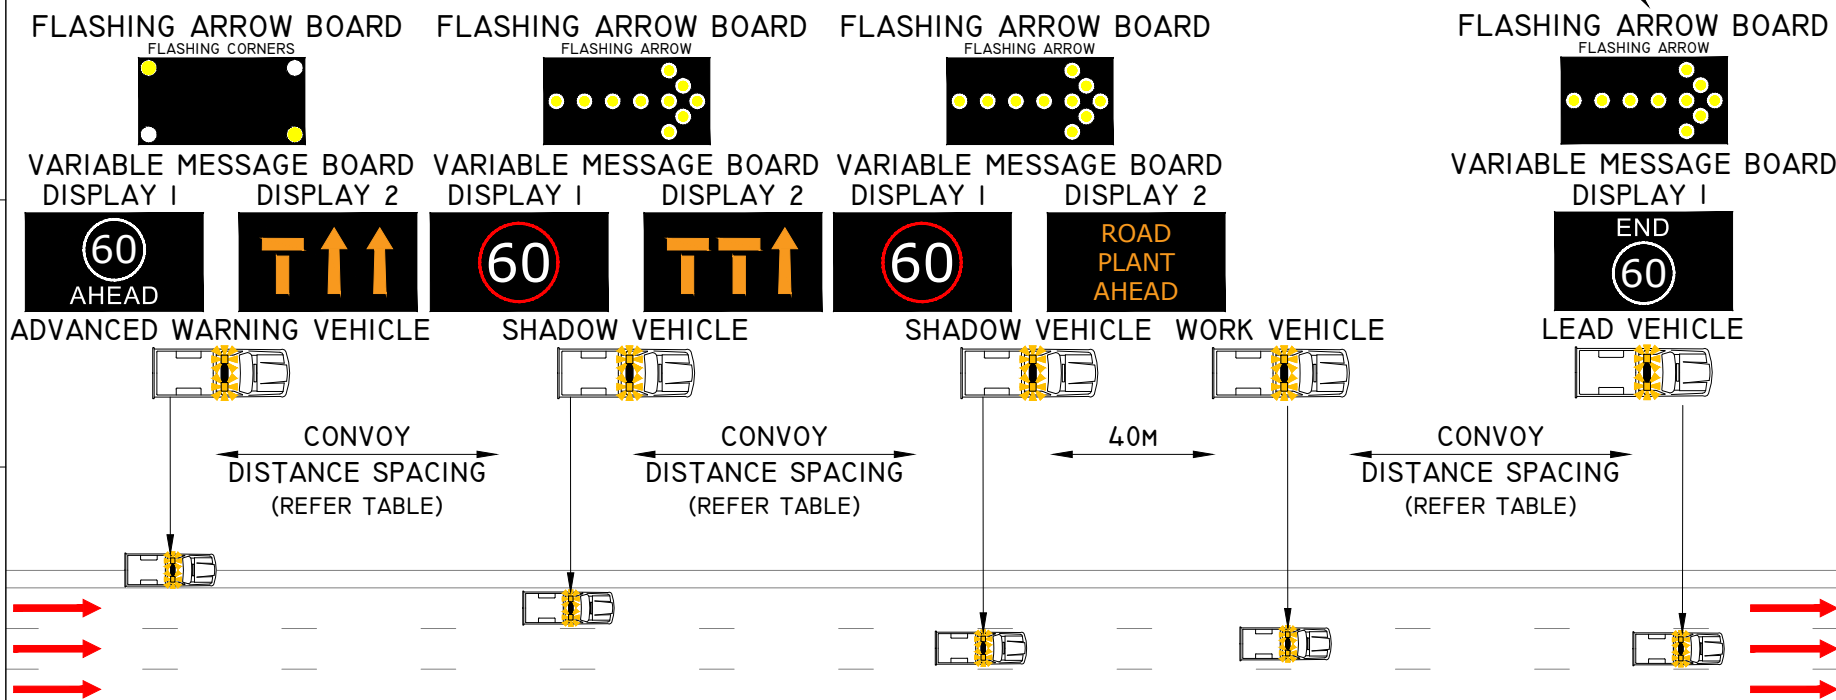

CLASS 2 MOBILE SCENARIO

VEHICLES TRAVELLING GREATER THAN 20KM/H BELOW THE SPEED LIMIT
(NO WORKERS ON FOOT)

SCENARIO 2:

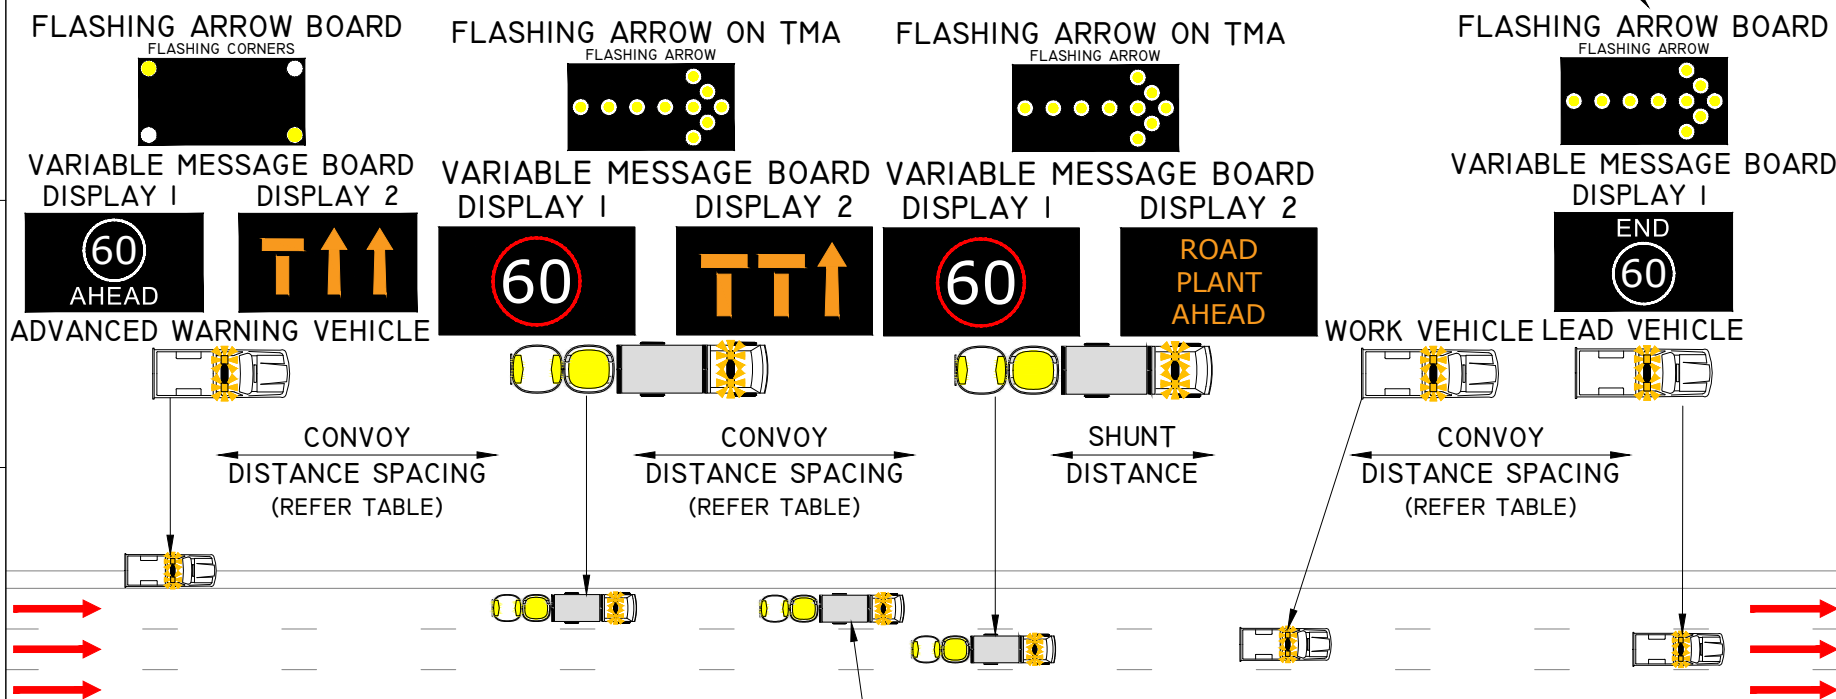

CLASS 2 MOBILE SCENARIO

VEHICLES TRAVELLING GREATER THAN 20km/h BELOW THE SPEED LIMIT (NO
WORKERS ON FOOT)
TRUCK MOUNTED ATTENUATORS.

SCENARIO I:

WORKS PROTECTED BY SHADOW VEHICLE

I. A RISK ASSESSMENT MAY BE PROVIDED FOR THE USE OF TRUCK MOUNTED ATTENUATOR IN PLACE OF THE SHADOW VEHICLE.

SCENARIO 2:

WORKS PROTECTED BY TMA

I. REFER TO THE MRWA REQUIREMENTS FOR THE USE OF TRUCK MOUNTED ATTENUATORS IN WA OR SECTION 4.5.1 OF THE TMP.

NOTES

1. WHERE WORKSITE CLEARANCES CANNOT BE ACHIEVED, ANOTHER MOBILE SCENARIO OR A STATIC SETUP MAY BE REQUIRED.
2. MOBILE CONVOY IS INDICATIVE ONLY AND WORKS CAN BE IN EITHER THE FAR LEFT OR FAR RIGHT LANE AND NUMBER OF LANES MAY VARY. WHERE WORKS ARE IN THE RIGHT LANE, LANE STATUS AND ARROW BOARDS TO BE CHANGED ACCORDINGLY.
3. WHERE THERE IS INSUFFICIENT ROOM IN THE SHOULDER, VERGE OR MEDIAN FOR ADVANCED WARNING VEHICLE REFER TO TGS-TMC-MS2-007.
4. THIS DRAWING IS FOR LARGE PLANT ITEMS ONLY AND THERE MUST BE NO WORKERS ON FOOT. THIS SCENARIO IS TO BE USED FOR CLASS 2 MOBILE WORKS, WHERE MOBILE CONVOY TRAVELS GREATER THAN 20KM/H OF TRAFFIC SPEED.
5. THE VEHICLE CONVOY MUST BE MOBILE AT ALL TIMES AND MUST NOT STOP IF WITHIN LIVE TRAFFIC LANES.
6. PRIOR TO THE IMPLEMENTATION OF ANY MOBILE CONVOYS, A RISK ASSESSMENT IS REQUIRED TO DETERMINE IF THE WORKS CAN BE COMPLETED SAFELY. REFER TO THE TMP FOR RISK CONSIDERATIONS.
7. WHERE THERE IS POOR SIGHT DISTANCE DUE TO CURVE OR CREST IN THE ROAD THE ADVANCED WARNING VEHICLE MUST STOP PRIOR TO THE REDUCED SIGHT DISTANCE LOCATION WHILE THE REST OF THE CONVOY TRAVEL THROUGH. WHERE THERE IS SIGNIFICANT SECTIONS OF POOR SIGHT DISTANCE AN ADDITIONAL SHADOW VEHICLE MAY BE USED.
8. ALL DRIVERS WITHIN MOBILE CONVOY MUST BE ALERT AND AWARE OF APPROACHING VEHICLES AT ALL TIMES.
9. ALL VEHICLES WITHIN MOBILE CONVOY MUST HAVE CLEAR COMMUNICATION METHODS USING TWO-WAY RADIO DEVICES.
10. VEHICLE LOCATIONS MUST CONSIDER THE IMPACT ON VULNERABLE ROAD USERS AND CYCLISTS.
11. FOR WORKS AROUND ON / OFF RAMPS, MAJOR SIDE ROADS OR SIGNALISED INTERSECTIONS A STATIC SETUP SHOULD BE CONSIDERED TO MANAGE VEHICLES PROPERLY. UPON RISK ASSESSMENT, THIS DRAWING MAY BE USED AND SHADOW VEHICLE DISTANCES REDUCED TO PREVENT VEHICLES ENTERING / EXITING THE ROAD IN BETWEEN THE CONVOY VEHICLES.
12. FOR WORKS ON 4 OR 5 LANE ROADS, ADDITIONAL LANE CLOSURES MAY BE IMPLEMENTED FOLLOWING THE PROCEDURES ON THIS DRAWING. LANE STATUS MUST BE INDICATIVE OF THE NUMBER OF LANES ON SITE AND CONVOY DISTANCE BETWEEN CLOSURES MUST BE MAINTAINED. ADDITIONAL TMA IS ONLY REQUIRED ON FREEWAYS, PRIOR TO THE POSITION OF THE LAST SHADOW VEHICLE. A RISK ASSESSMENT MUST BE COMPLETED PRIOR TO THE ADDING OF ADDITIONAL VEHICLES AND LANE CLOSURES TO THE CONVOY.
13. REFER TO MANUFACTURING ADVICE FOR SHUNT DISTANCES ON TRUCK MOUNTED ATTENUATORS.
14. WHEN A MOBILE CONVOY CONTAINS MORE THAN ONE WORK VEHICLE, EACH VEHICLE MUST BE 40m APART AS A MAXIMUM. WHERE THIS IS NOT PRACTICABLE, EACH WORK VEHICLE MUST BE TREATED AS A SEPARATE MOBILE OPERATION WITH THEIR OWN WORK CONVOY. EACH WORK VEHICLE MUST ADHERE TO THE CLEARANCES TO LIVE TRAFFIC LANE TABLE.
15. NUMBER OF LANES AND CONFIGURATION OF ROAD ARE INDICATIVE ONLY. THIS TGS REQUIRES A MINIMUM OF 3 LANES.
16. WHEN THE SPEED LIMIT IS REDUCED BY MORE THAN 20KM/H, CONSIDER THE USE OF MULTIPLE ADVANCE WARNING VEHICLES TO DECREASE THE SPEED IN STEPS, WHERE THIS IS NOT IMPLEMENTED A RISK ASSESSMENT MUST BE COMPLETED.

DOCUMENTATION

DAILY RECORDS OF THE SITE LAYOUT INCLUDING DEVICES, SIGHT DISTANCE, RISK ASSESSMENTS, SIGNS OR TGS, MUST BE KEPT IN A DIARY OR IN WORK SHEETS (DAILY DAIRY). ANY SIGNIFICANT DEPARTURES FROM, OR ADDITIONS TO, THE SIGNS AND DEVICES INCLUDED IN THIS DIAGRAM SHOULD BE NOTED AND APPROVED.

TABLES

DISTANCE BETWEEN VEHICLES IN MOBILE CONVOY - EXCLUDING SHADOW VEHICLE


SPEED LIMIT (км/ч)	DISTANCE (м)
≤45	50
46-55	70
56-65	90
66-75	110
76-85	140
86-95	160
96-105	200
>106	230

LEGEND

EXISTING ROAD



METROPOLITAN REGIONS
TRAFFIC MANAGEMENT BRANCH
WATERLOO CRESCENT
TELEPHONE (08) 138 138 EAST PERTH 6004

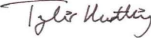DATE OF DRAWING 2025 JULY	SCALE -
LOCAL GOVERNMENT AUTHORITY -	POSTED SPEED -
ROAD AUTHORITY MAIN ROADS WA	WORKSITE SPEED 60KM/H
CHECKED BY TYLER HARTLEY	SIGNATURE 
ACCREDITATION RTM-0066	
DESIGNED BY MICHAEL REED	SIGNATURE 
ACCREDITATION AWTM-23-11536-02	

GENERIC TRAFFIC GUIDANCE SCHEME CLASS 2 - MOBILE SCENARIOS MULTI LANE CLOSURE CONVOY 60KM/H WORK VEHICLE BETWEEN 1.2m AND 3.0m	
---	--

DRAWING NO	0922-01531-MS2-004	REVISION	6
------------	--------------------	----------	---