


SCENARIO I:

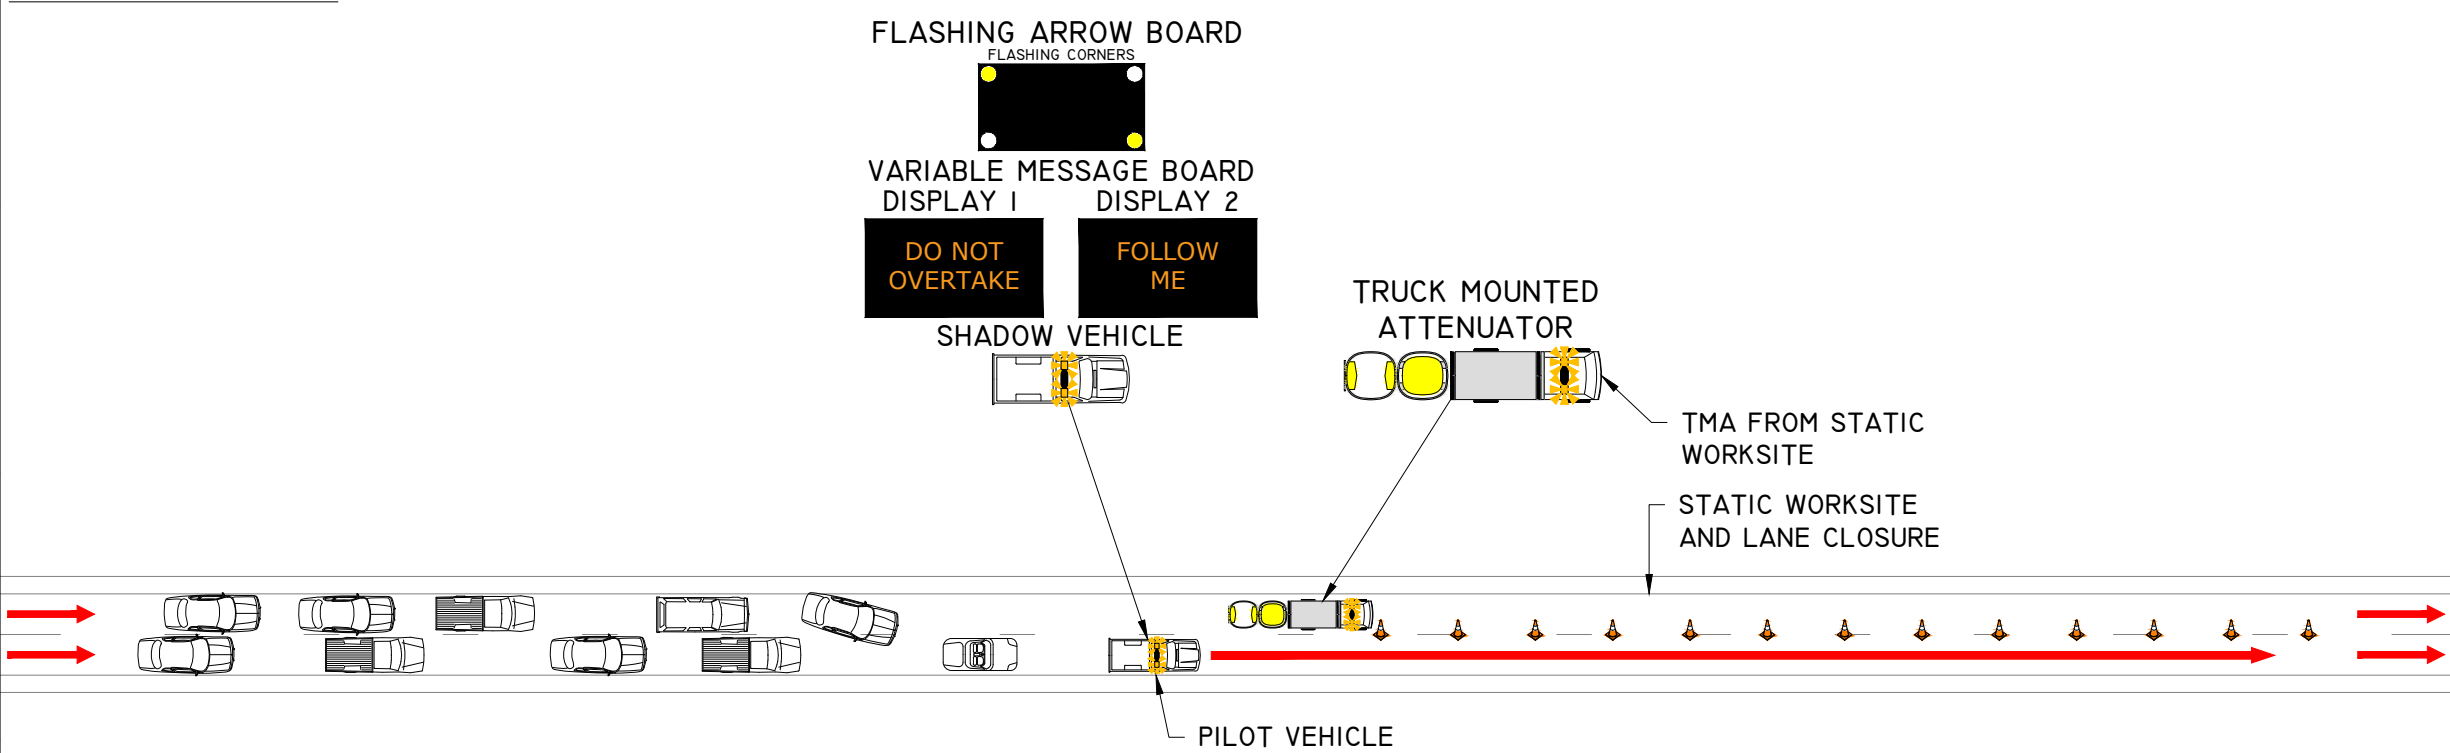

SCENARIO I:
CONTROLLED ROLLING BLOCKS
NOTES

- PRIOR TO THE IMPLEMENTATION OF ANY MOBILE CONVOYS, A RISK ASSESSMENT IS REQUIRED TO DETERMINE IF THE WORKS CAN BE COMPLETED SAFELY. REFER TO THE TMP FOR RISK CONSIDERATIONS.
- ALL DRIVERS WITHIN MOBILE CONVOY MUST BE ALERT AND AWARE OF APPROACHING VEHICLES AT ALL TIMES.
- ALL VEHICLES WITHIN MOBILE CONVOY MUST HAVE CLEAR COMMUNICATION METHODS USING TWO-WAY RADIO DEVICES.
- VEHICLE LOCATIONS MUST CONSIDER THE IMPACT ON VULNERABLE ROAD USERS AND CYCLISTS.
- ROAD AUTHORITY OR RTM APPROVAL IN WRITING TO ACCOMPANY THE USE OF THIS TGS.
- TRAFFIC MANAGEMENT SHOWN IS INDICATIVE ONLY & MUST COMPLIMENT AN APPROVED TGS SHOWING THE FULL TM SETUP.
- SETUP ONLY TO BE USED WHEN ON TRAVEL LANE REMAINS OPENING PASSING THE WORKSITE.
- PILOT VEHICLE (TM VEHICLE) MUST HAVE 2 FLASHING BEACONS ACTIVATED AND VMS BOARD DISPLAYING THE FOLLOWING MESSAGE: "DO NOT OVERTAKE" - "FOLLOW ME".
- ONCE THE PILOT VEHICLE IS IN PARALLEL WITH THE TMA (OR ARROW BOARD AT END OF LANE CLOSURE), THE PILOT VEHICLE CAN TRAVEL BETWEEN 20KM/H TO 40KM/H TO PERFORM ROLLING BLOCK.
- PILOT VEHICLE MUST NOT STOP AT ANY POINT DURING THE ROLLING BLOCK. WHERE THE WORKS CANT BE COMPLETED UNDER A SINGLE ROLLING BLOCK THE TM VEHICLE MUST RESET AND PERFORM A SECONDARY ROLLING BLOCK OR A SEPARATE STATIC SETUP MAY BE REQUIRED.
- AT A DISTANCE OF 60M FROM WORKS IN THE CONVOY TRAVEL PATH OF PILOT VEHICLE - WORKERS/PLANT ON THE ROADWAY ARE TO DEPART INTO CLOSED LANE TO ALLOW UNRESTRICTED PASSAGE OF THE PILOT VEHICLE AND CONVOY.
- PILOT VEHICLE MUST NOT ENTER INTO WORKSITE WHEN CONDUCTION CONVOY, TO PREVENT TRAFFIC BREACHES.
- PILOT VEHICLE OPERATOR TO HAVE RADIO COMMUNICATION WITH TRAFFIC CONTROLLER AT THE LOCATION OF WORKS.
- THE RETENTION OF CONVOY TRAVEL PATH LENGTH SHALL BE PLANNED AND IMPLEMENTED TO SUIT THE EXTENT OF WORKS REQUIRED IN THE CONVOY TRAVEL PATH.
- THIS SETUP CAN BE USED IN ROADS WITHOUT A TMA AS LONG AS SINGLE LANE OPERATION IS MAINTAINED THROUGH A LANE CLOSURE.

DOCUMENTATION

DAILY RECORDS OF THE SITE LAYOUT INCLUDING DEVICES, SIGHT DISTANCE, RISK ASSESSMENTS, SIGNS OR TGS, MUST BE KEPT IN A DIARY OR IN WORK SHEETS (DAILY DAIRY). ANY SIGNIFICANT DEPARTURES FROM, OR ADDITIONS TO, THE SIGNS AND DEVICES INCLUDED IN THIS DIAGRAM SHOULD BE NOTED AND APPROVED.

LEGEND

EXISTING ROAD



METROPOLITAN REGIONS
TRAFFIC MANAGEMENT BRANCH

WATERLOO CRESCENT
TELEPHONE (08) 138 138

EAST PERTH 6004

DATE OF DRAWING 2025 JULY	SCALE -
LOCAL GOVERNMENT AUTHORITY -	POSTED SPEED -
ROAD AUTHORITY MAIN ROADS WA	WORKSITE SPEED -
CHECKED BY TYLER HARTLEY	SIGNATURE
ACCREDITATION RTM-0066	
DESIGNED BY MICHAEL REED	SIGNATURE
ACCREDITATION AWTM-23-II536-02	

GENERIC TRAFFIC GUIDANCE SCHEME
CLASS 2 - MOBILE SCENARIOS
CONTROLLED VEHICLE CONVOY
AT EXISTING WORKSITES

DRAWING NO
0922-01531-MS2-020

REVISION
6