


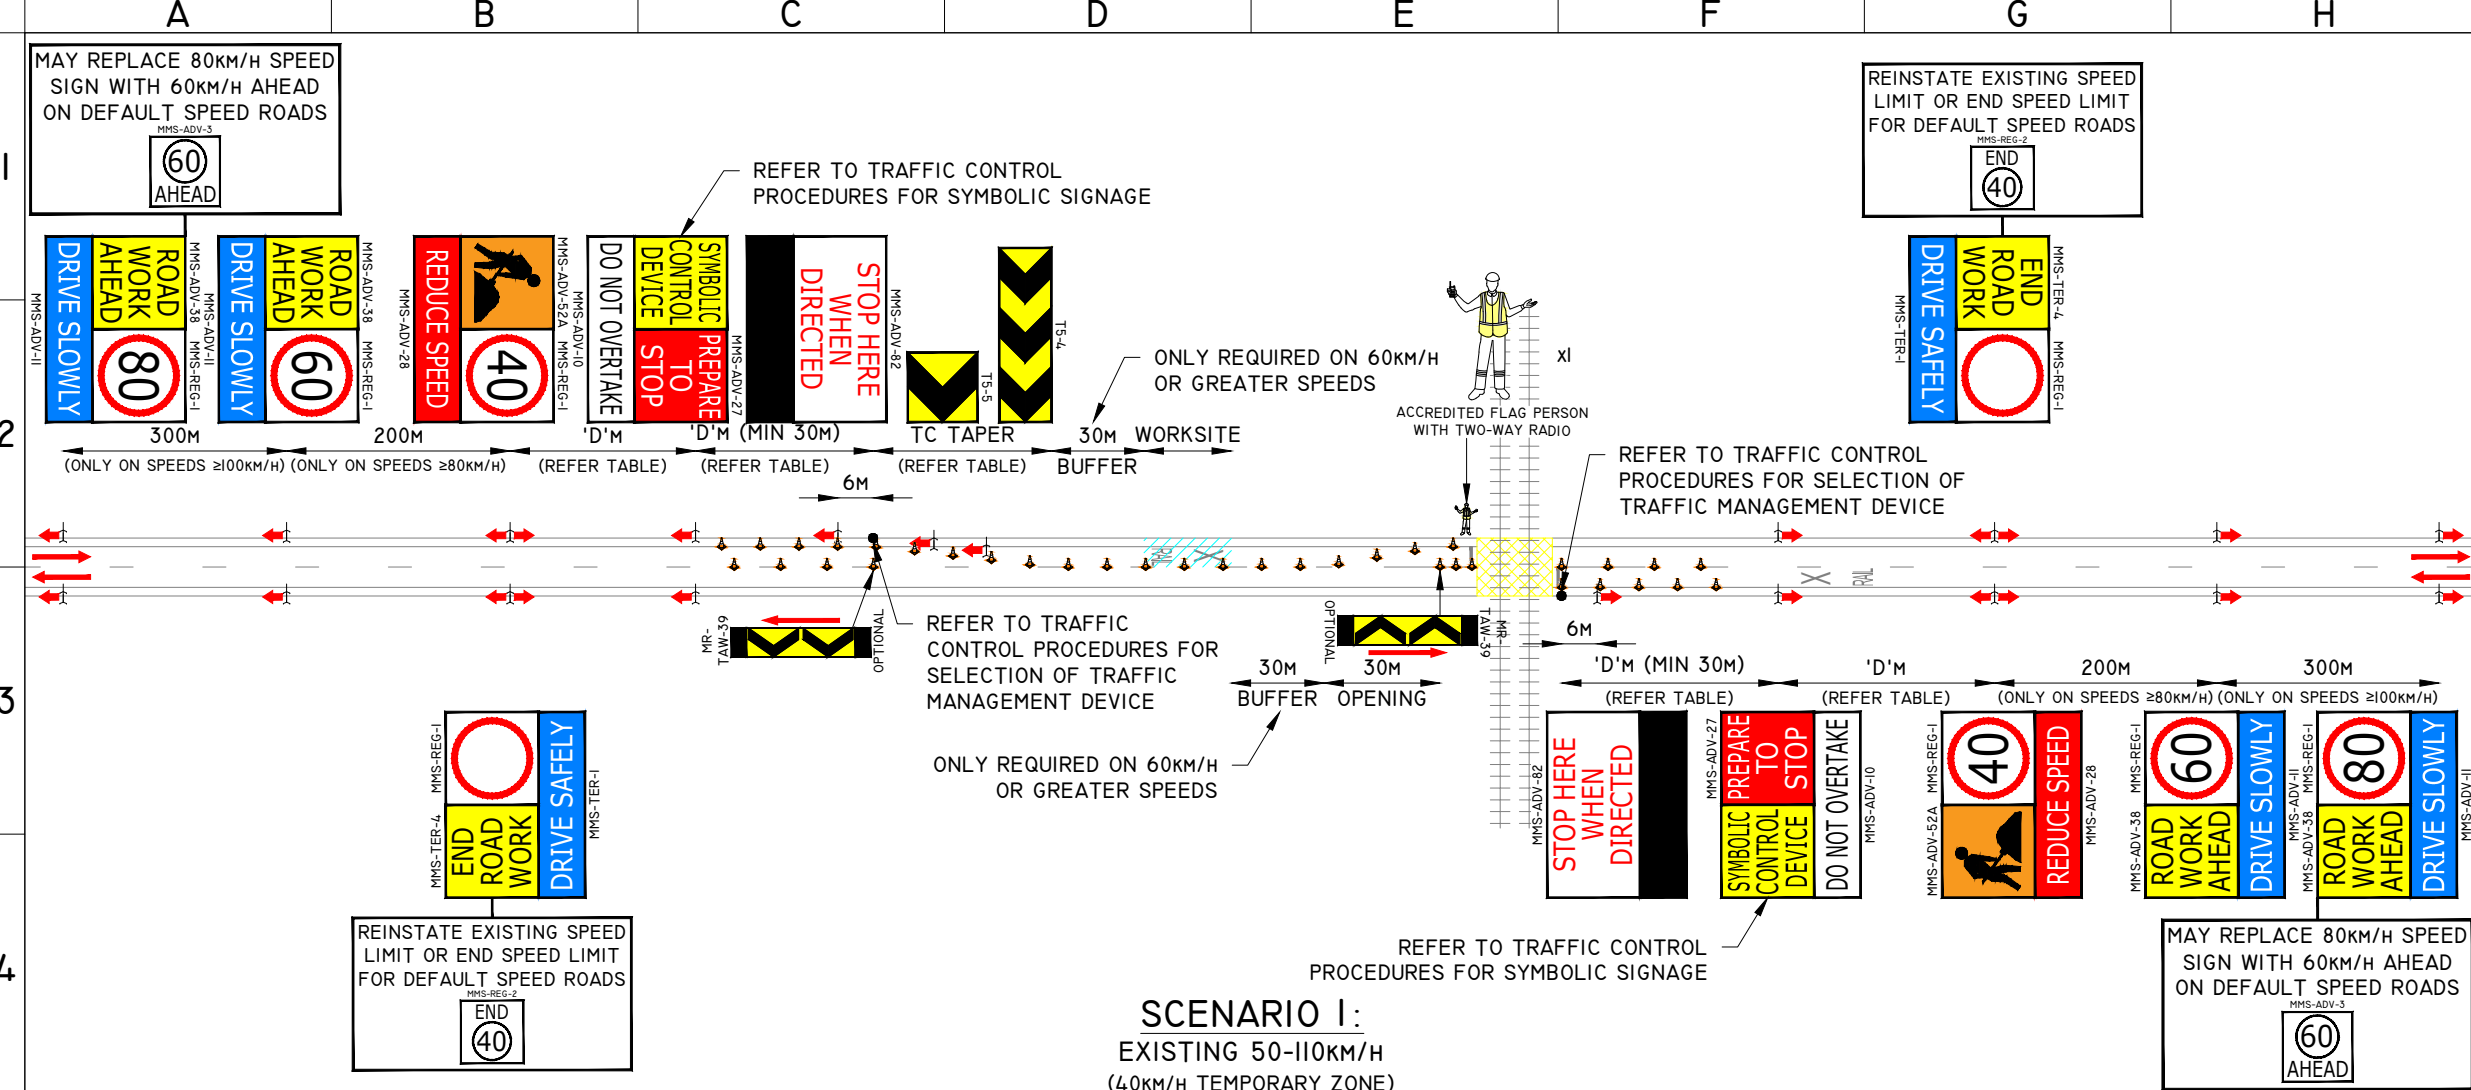

NOTES

TOLERANCES

POSITION OF SIGNS:

MINIMUM 10% LESS THAN THE DISTANCE OR LENGTHS GIVEN.

MAXIMUM 25% MORE THAN THE DISTANCES OR LENGTHS GIVEN.

SPACING OF DELINEATING DEVICES:

MAXIMUM 10% MORE THAN THE SPACING GIVEN.

NO MINIMUM.

AGTTM PART 6 SECTION 6.8.

DOCUMENTATION

ON-SITE VARIATIONS MUST BE APPROVED BY THE TRAFFIC MANAGEMENT SUPERVISOR, THAN AN ON-SITE VARIATION MADE AND CHANGES RECORDED IN THE DAILY DAIRY. FOR MORE INFORMATION REFER TO SECTION 9.3 OF THE TMP.

1. A RISK ASSESSMENT MUST BE CARRIED OUT TO DETERMINE THE REQUIREMENTS OF AFTERCARE.

2. ALL SIGN LOCATIONS ARE TO BE CHECKED ON SITE PRIOR TO SETOUT AND POSITIONS ADJUSTED AS PER THE 'TOLERANCES'.

3. ALL CONTRADICTORY SIGNS WITHIN THE TM SETUP TO BE COVERED BY SUITABLY OPAQUE MATERIAL.

4. FOR BOX EDGED SIGN ALTERNATIVES, CONSULT AWTM PRIOR TO IMPLEMENTATION.

5. WORKERS TO REMAIN 10M CLEAR OF RAILWAY TRACKS AT ALL TIMES.

6. ACCREDITED FLAG PERSON TO MONITOR AND WARN OF INCOMING TRAINS OVER TWO-WAY RADIO. TCS WILL HOLD ALL TRAFFIC TO ALLOW TRAIN TO PASS.

7. TRAFFIC SHALL NEVER BE ALLOWED TO QUEUE/STACK ACROSS THE RAIL CORRIDOR.

8. MAXIMUM LENGTH OF 40km/h TEMPORARY SPEED ZONE MUST BE 500M.

9. REFER TO SECTION 4.1.8 OF THE TMP FOR THE MANDATORY USE OF SPEED FEEDBACK SIGNAGE

PEDESTRIAN MANAGEMENT

1. 'PEDESTRIAN WATCH YOUR STEP' SIGN TO BE INSTALLED ON EACH APPROACH WHERE WORKS MAY ENCR OACH ONTO OR ADJACENT TO EXISTING FOOTPATH FACILITIES.

2. TM PERSONNEL TO MONITOR AND ESCORT PEDESTRIANS THROUGH THE WORK AREA AS REQUIRED.

3. PEDESTRIANS MAY BE HELD ON EITHER END OF THE WORKSITE UNTIL IT IS SAFE TO PASS AS REQUIRED.

RECOMMENDED CONE SPACING

AGTTM PART 3 - TABLE 5.3

ALL PURPOSES:

(≤ 50km/h): 4M

PROTECTING FRESHLY PAINTED LINES:

(≤ 70km/h): 24M

CENTRELINE ON APPROACH TO TC POSITION: 4M

TAPER AT TRAFFIC CONTROL STATION: 4M

RECOMMENDED LANE WIDTHS

MAIN ROADS WA CoP SECTION 6.7 - TABLE 9

SHUTTLE FLOW WITH CONTROL: 3.2M

TRAFFIC CONTROL PROCEDURES

REFER TO TMP SECTION 4.1.7 PORTABLE TRAFFIC CONTROL DEVICES FOR MORE DETAILS

MANUAL TRAFFIC CONTROL

ACCREDITED TRAFFIC CONTROLLER

END OF QUEUE PROTECTION

DEVICE MAY BE A TRAFFIC CONTROLLER, PORTABOOM OR TEMPORARY SIGNAL

END OF QUEUE

2x'D'M (REFER NOTES)

'D'M (MIN 30M)

'D'M (REFER NOTES)

'D'M (MIN)

'D'M (REFER NOTES)

MUST BE IMPLEMENTED ON ALL ROADS WITH A POSTED SPEED OF 80km/h OR GREATER. REFER TO TGS-TMC-RF-022, 023 AND 044 FOR MORE INFORMATION.

MANUAL TRAFFIC CONTROL IS NOT PERMITTED ON THE MAIN ROADS NETWORK WITH THE EXCEPTIONS LISTED UNDER SECTION 4.1.7 (PORTABLE TRAFFIC CONTROL DEVICES) OF THE TMP AND IN THE MAIN ROADS CODE OF PRACTICE.

ON ALL OTHER ROADS, PTCDS MUST BE USED UNDER THE FOLLOWING CONDITIONS:

A PERMANENT SPEED LIMIT OF 90M/H OR MORE AND OVER 2,000VPD; OR

A PERMANENT SPEED LIMIT OF 70km/h OR MORE AND OVER 10,000VPD.

PTCDs SHOULD BE CONSIDERED ON ALL WORKS AND ONLY BE SUPPLEMENTED WITH MANUAL TRAFFIC CONTROL UNDER AN AWTM/WTM RISK ASSESSMENT.

SHADOW VEHICLE INSET

SHADOW VEHICLE MAY BE DISPENSED WITH UNDER A RISK ASSESSMENT BY AN RTM AS PART OF THE TM ADVISE. IN THE ABSENCE OF THE SHADOW VEHICLE A LOOKOUT PERSON IS REQUIRED. REFER TO SECTION 4.5 OF THE TMP FOR MORE DETAILS.

FLASHING ARROW

SHADOW VEHICLE

20-40M

WORK SITE

TABLES

TAPER LENGTHS

AGTTM PART 3 - TABLE 5.7

SPEED LIMIT (KM/H)

TRAFFIC CONTROL TAPER (M)

45 OR LESS

15

46 TO 55

15

56 TO 65

30

66 TO 75*

N/A

76 TO 85*

N/A

86 TO 95*

N/A

96 TO 105*

N/A

GREATER THAN 105*

N/A

*TAPER LENGTHS ARE BASED ON A:

3.5M WIDTH OF THE LANE TO BE CLOSED

LATERAL SHIFT TAPER LENGTH EQUAL TO 1.0M/s

MEDIAN SPEED FOR EACH RANGE (I.E 76 - 85 = 80KM/H)

SIGN SPACING

AGTTM PART 3 - TABLE 2.2

SPEED LIMIT (KM/H)

DISTANCE ('D') (M)

55 OR LESS

15

56 TO 65

45

GREATER THAN 65

EQUAL TO SPEED OF TRAFFIC IN KM/H

MAXIMUM LENGTH OF SHUTTLE FLOW

MAIN ROADS WA CoP SECTION 6.8.6 - TABLE 15

VOLUMES (BOTH DIRECTION) (VPH)

LENGTH (BETWEEN TCS) (M)

RESIDENTIAL STREET

60

701 - 800

70

601 - 700

100

501 - 600

150

401 - 500

250

351 - 400

400

301 - 350

600

251 - 300

800

201 - 250

1200

151 - 200

1600

≤ 150

2200

LEGEND

EXISTING ROAD

EXISTING RAILWAY TRACKS

PROPOSED CONES

WORKSITE

mainroads WESTERN AUSTRALIA

METROPOLITAN REGIONS TRAFFIC MANAGEMENT BRANCH

WATERLOO CRESCENT TELEPHONE (08) 138 138

EAST PERTH 6004

DATE OF DRAWING 2025 JULY

SCALE -

LOCAL GOVERNMENT AUTHORITY -

POSTED SPEED 50-110km/h

ROAD AUTHORITY MAIN ROADS WA

WORKSITE SPEED 40km/h

CHECKED BY TYLER HARTLEY

SIGNATURE Tyler Hartley

ACCREDITATION RTM-0066

SIGNATURE Michael Reed

DESIGNED BY MICHAEL REED

ACCREDITATION AWTM-23-11536-02

GENERIC TRAFFIC GUIDANCE SCHEME RAIL APPROACH SETUPS 'X' AND 'RAIL' REINSTATEMENT WORKSITE WITHIN 1.2M

DRAWING NO 0922-01531-RA-001

REVISION 6