


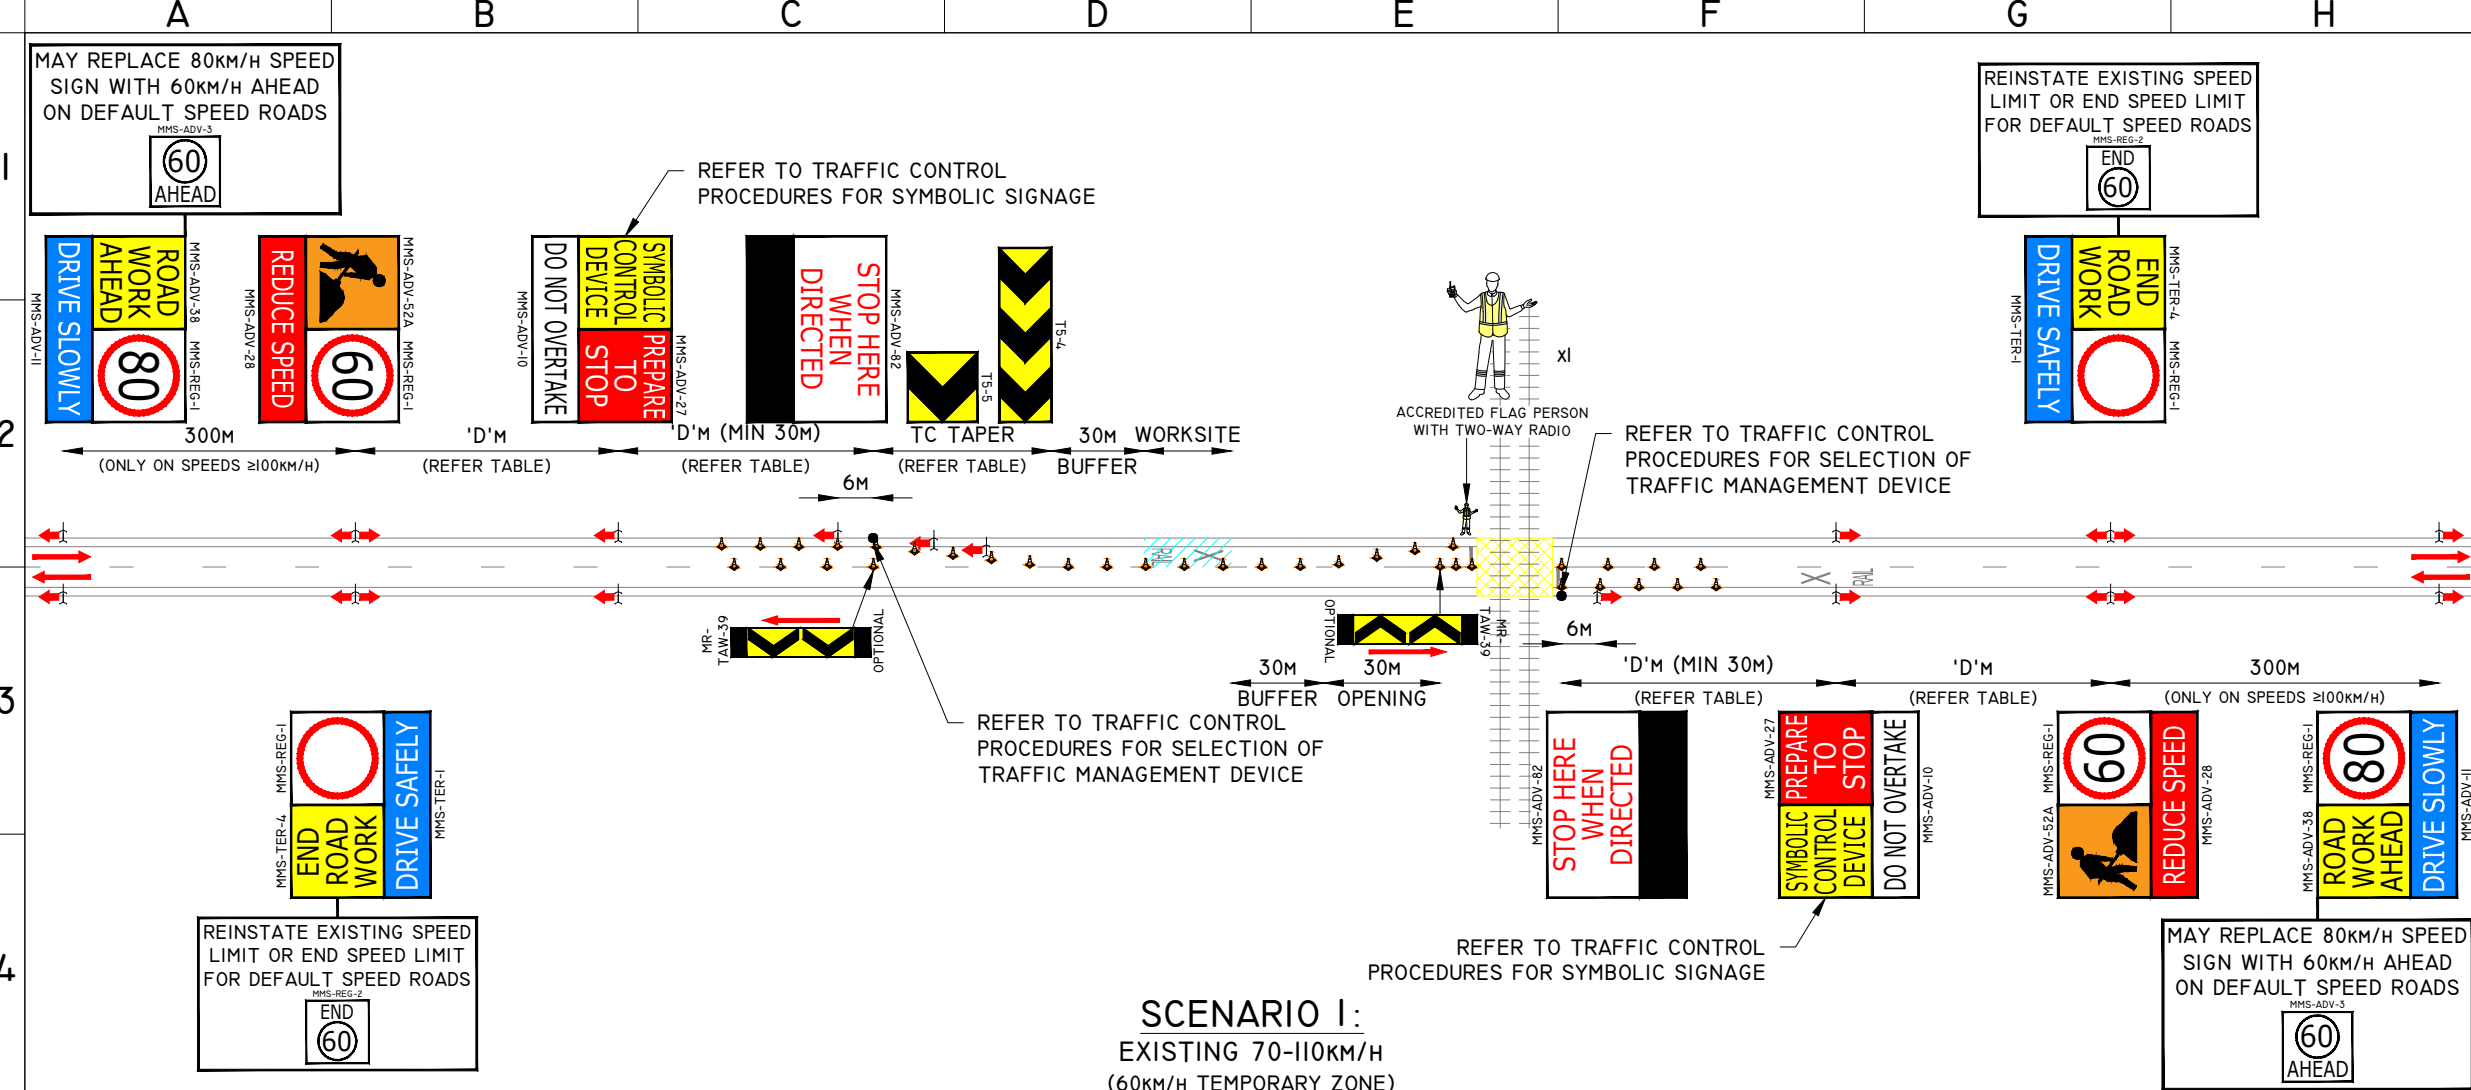

NOTES

TOLERANCES

POSITION OF SIGNS:
MINIMUM 10% LESS THAN THE DISTANCE OR LENGTHS GIVEN.
MAXIMUM 25% MORE THAN THE DISTANCES OR LENGTHS GIVEN.
SPACING OF DELINEATING DEVICES:
MAXIMUM 10% MORE THAN THE SPACING GIVEN.
NO MINIMUM.

AGTTM PART 6 SECTION 6.8. DOCUMENTATION

ON-SITE VARIATIONS MUST BE APPROVED BY THE TRAFFIC MANAGEMENT SUPERVISOR, THAN AN ON-SITE VARIATION MADE AND CHANGES RECORDED IN THE DAILY DAIRY. FOR MORE INFORMATION REFER TO SECTION 9.3 OF THE TMP.

- A RISK ASSESSMENT MUST BE CARRIED OUT TO DETERMINE THE REQUIREMENTS OF AFTERCARE.
- ALL SIGN LOCATIONS ARE TO BE CHECKED ON SITE PRIOR TO SETOUT AND POSITIONS ADJUSTED AS PER THE 'TOLERANCES'.
- ALL CONTRADICTORY SIGNS WITHIN THE TM SETUP TO BE COVERED BY SUITABLY OPAQUE MATERIAL.
- FOR BOX EDGED SIGN ALTERNATIVES, CONSULT AWTM PRIOR TO IMPLEMENTATION.
- WORKERS TO REMAIN 10M CLEAR OF RAILWAY TRACKS AT ALL TIMES.
- ACCREDITED FLAG PERSON TO MONITOR AND WARN OF INCOMING TRAINS OVER TWO-WAY RADIO. TCS WILL HOLD ALL TRAFFIC TO ALLOW TRAIN TO PASS.
- TRAFFIC SHALL NEVER BE ALLOWED TO QUEUE/STACK ACROSS THE RAIL CORRIDOR.
- REFER TO SECTION 4.1.8 OF THE TMP FOR THE MANDATORY USE OF SPEED FEEDBACK SIGNAGE.

PEDESTRIAN MANAGEMENT

- 'PEDESTRIAN WATCH YOUR STEP' SIGN TO BE INSTALLED ON EACH APPROACH WHERE WORKS MAY ENCRONCH ONTO OR ADJACENT TO EXISTING FOOTPATH FACILITIES.
- TM PERSONNEL TO MONITOR AND ESCORT PEDESTRIANS THROUGH THE WORK AREA AS REQUIRED.
- PEDESTRIANS MAY BE HELD ON EITHER END OF THE WORKSITE UNTIL IT IS SAFE TO PASS AS REQUIRED.

RECOMMENDED CONE SPACING

AGTTM PART 3 - TABLE 5.3

ALL PURPOSES:
(60 - 70km/h): 12M

PROTECTING FRESHLY PAINTED LINES:
(≤ 70km/h): 24M

CENTRELINE ON APPROACH TO TC POSITION: 4M
TAPER AT TRAFFIC CONTROL STATION: 4M

RECOMMENDED LANE WIDTHS

MAIN ROADS WA CoP SECTION 6.7 - TABLE 9

SHUTTLE FLOW WITH CONTROL: 3.2M

TRAFFIC CONTROL PROCEDURES

REFER TO TMP SECTION 4.1.7 PORTABLE TRAFFIC CONTROL DEVICES FOR MORE DETAILS

MANUAL TRAFFIC CONTROL

ACCREDITED TRAFFIC CONTROLLER (MMS-ADV-47, MMS-ADV-27, MMS-ADV-82, MMS-ADV-10)

END OF QUEUE PROTECTION

DEVICE MAY BE A TRAFFIC CONTROLLER, PORTABOOM OR TEMPORARY SIGNAL

SHADOW VEHICLE INSET

SHADOW VEHICLE MAY BE DISPENSED WITH UNDER A RISK ASSESSMENT BY AN RTM AS PART OF THE TM ADVICE. IN THE ABSENCE OF THE SHADOW VEHICLE A LOOKOUT PERSON IS REQUIRED. REFER TO SECTION 4.5 OF THE TMP FOR MORE DETAILS.

TABLES

TAPER LENGTHS

AGTTM PART 3 - TABLE 5.7

SPEED LIMIT (KM/H)	TRAFFIC CONTROL TAPER (M)
45 OR LESS	15
46 TO 55	15
56 TO 65	30
66 TO 75*	
76 TO 85*	
86 TO 95*	
96 TO 105*	
GREATER THAN 105*	N/A

*TAPER LENGTHS ARE BASED ON A:
• 3.5M WIDTH OF THE LANE TO BE CLOSED
• LATERAL SHIFT TAPER LENGTH EQUAL TO 1.0m/s
• MEDIAN SPEED FOR EACH RANGE (I.E 76 - 85 = 80km/h)

SIGN SPACING

AGTTM PART 3 - TABLE 2.2

SPEED LIMIT (KM/H)	DISTANCE ('D')
55 OR LESS	15
56 TO 65	45
GREATER THAN 65	EQUAL TO SPEED OF TRAFFIC IN KM/H

MAXIMUM LENGTH OF SHUTTLE FLOW

MAIN ROADS WA CoP SECTION 6.8.6 - TABLE 15

VOLUMES (BOTH DIRECTION) (VPH)	LENGTH (BETWEEN TCS) (M)
RESIDENTIAL STREET	60
701 - 800	70
601 - 700	100
501 - 600	150
401 - 500	250
351 - 400	400
301 - 350	600
251 - 300	800
201 - 250	1200
151 - 200	1600
≤ 150	2200

LEGEND

- EXISTING ROAD
- EXISTING RAILWAY TRACKS
- PROPOSED CONES
- WORKSITE

mainroads WESTERN AUSTRALIA

METROPOLITAN REGIONS TRAFFIC MANAGEMENT BRANCH

WATERLOO CRESCENT
TELEPHONE (08) 138 138

EAST PERTH 6004

DATE OF DRAWING
2025 JULY

SCALE
-

LOCAL GOVERNMENT AUTHORITY
-

POSTED SPEED
70-110km/h

ROAD AUTHORITY
MAIN ROADS WA

WORKSITE SPEED
60km/h

CHECKED BY
TYLER HARTLEY

SIGNATURE
Tyler Hartley

ACCREDITATION
RTM-0066

DESIGNED BY
MICHAEL REED

SIGNATURE
Michael Reed

ACCREDITATION
AWTM-23-11536-02

GENERIC TRAFFIC GUIDANCE SCHEME RAIL APPROACH SETUPS 'X' AND 'RAIL' REINSTATEMENT WORKSITE BETWEEN 1.2M AND 3.0M

DRAWING NO
0922-01531-RA-002

REVISION
6