


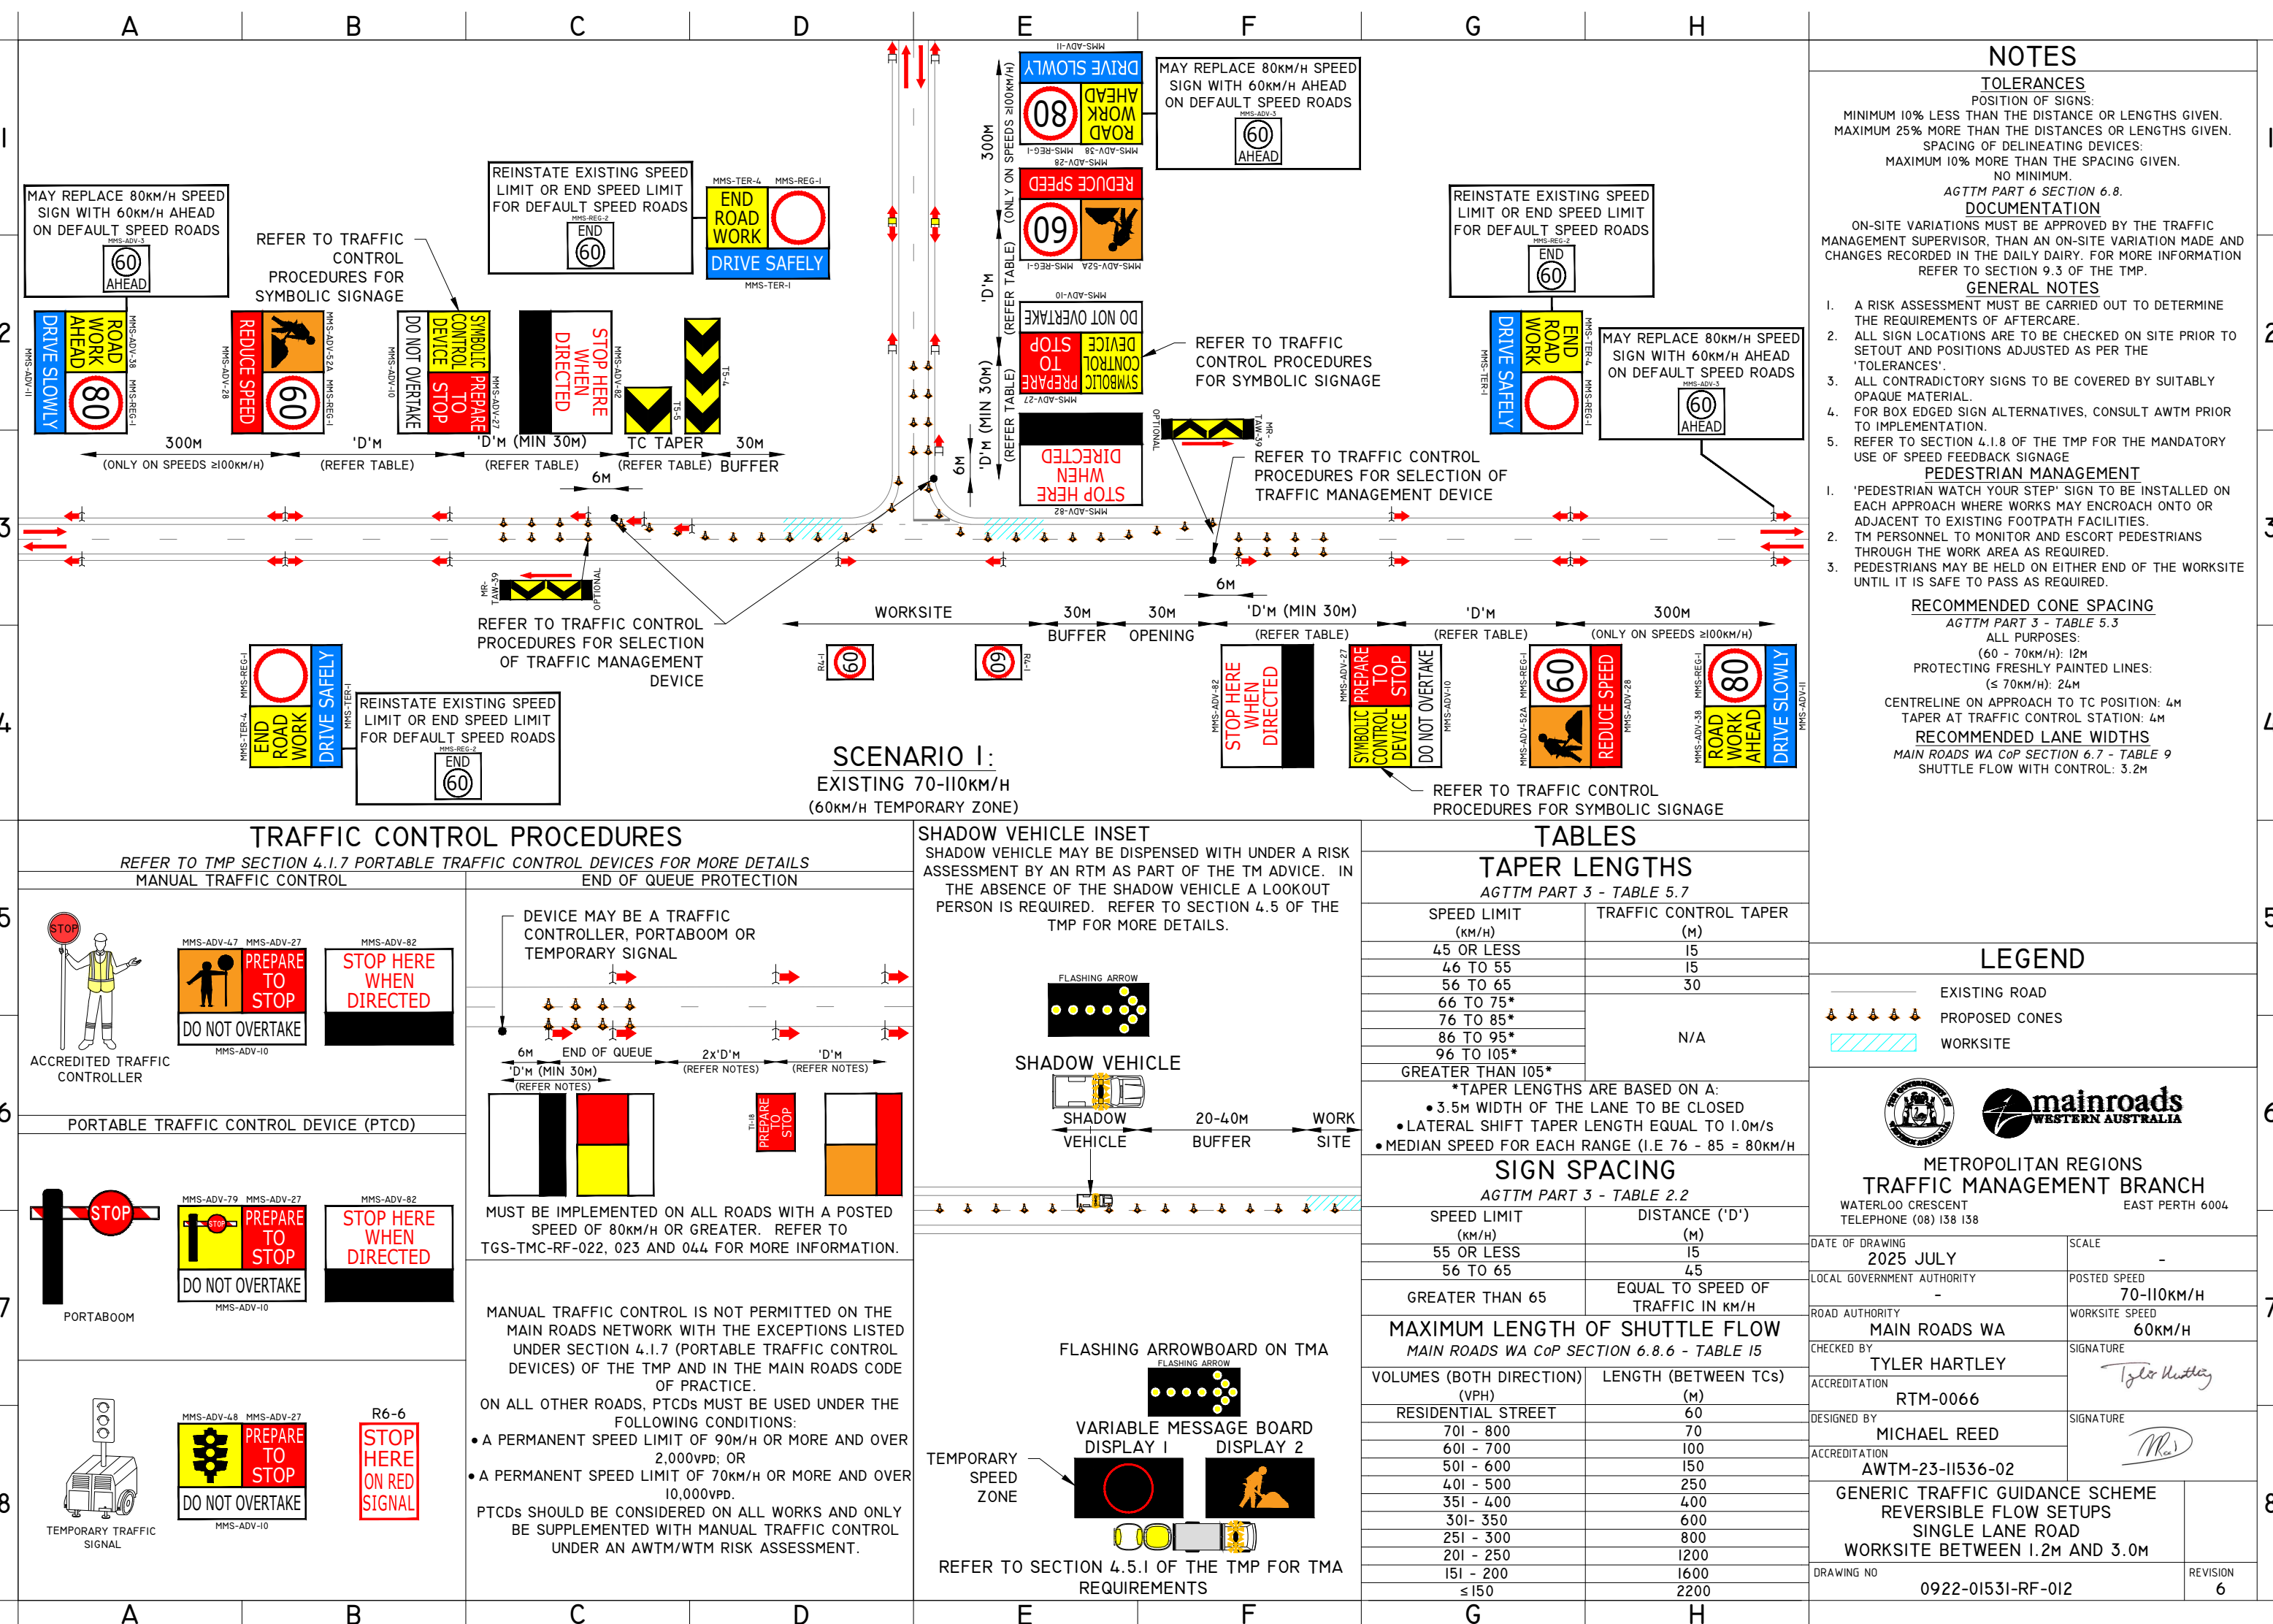

NOTES

- TOLERANCES**
- POSITION OF SIGNS:
MINIMUM 10% LESS THAN THE DISTANCE OR LENGTHS GIVEN.
MAXIMUM 25% MORE THAN THE DISTANCES OR LENGTHS GIVEN.
- SPACING OF DELINEATING DEVICES:
MAXIMUM 10% MORE THAN THE SPACING GIVEN.
NO MINIMUM.
- AGTTM PART 6 SECTION 6.8.
- DOCUMENTATION**
- ON-SITE VARIATIONS MUST BE APPROVED BY THE TRAFFIC MANAGEMENT SUPERVISOR, THAN AN ON-SITE VARIATION MADE AND CHANGES RECORDED IN THE DAILY DAIRY. FOR MORE INFORMATION REFER TO SECTION 9.3 OF THE TMP.
- GENERAL NOTES**
- A RISK ASSESSMENT MUST BE CARRIED OUT TO DETERMINE THE REQUIREMENTS OF AFTERCARE.
 - ALL SIGN LOCATIONS ARE TO BE CHECKED ON SITE PRIOR TO SETOUT AND POSITIONS ADJUSTED AS PER THE 'TOLERANCES'.
 - ALL CONTRADICTIONARY SIGNS TO BE COVERED BY SUITABLY OPAQUE MATERIAL.
 - FOR BOX EDGED SIGN ALTERNATIVES, CONSULT AWTM PRIOR TO IMPLEMENTATION.
 - REFER TO SECTION 4.1.8 OF THE TMP FOR THE MANDATORY USE OF SPEED FEEDBACK SIGNAGE
- PEDESTRIAN MANAGEMENT**
- 'PEDESTRIAN WATCH YOUR STEP' SIGN TO BE INSTALLED ON EACH APPROACH WHERE WORKS MAY ENCROACH ONTO OR ADJACENT TO EXISTING FOOTPATH FACILITIES.
 - TM PERSONNEL TO MONITOR AND ESCORT PEDESTRIANS THROUGH THE WORK AREA AS REQUIRED.
 - PEDESTRIANS MAY BE HELD ON EITHER END OF THE WORKSITE UNTIL IT IS SAFE TO PASS AS REQUIRED.
- RECOMMENDED CONE SPACING**
- AGTTM PART 3 - TABLE 5.3
- ALL PURPOSES:
(60 - 70km/h): 12m
PROTECTING FRESHLY PAINTED LINES:
(≤ 70km/h): 24m
- CENTRELINE ON APPROACH TO TC POSITION: 4m
TAPER AT TRAFFIC CONTROL STATION: 4m
- RECOMMENDED LANE WIDTHS**
- MAIN ROADS WA COP SECTION 6.7 - TABLE 9
SHUTTLE FLOW WITH CONTROL: 3.2m

LEGEND

- EXISTING ROAD
- PROPOSED CONES
- WORKSITE



METROPOLITAN REGIONS
TRAFFIC MANAGEMENT BRANCH
WATERLOO CRESCENT
TELEPHONE (08) 138 138
EAST PERTH 6004

DATE OF DRAWING	2025 JULY	SCALE	-
LOCAL GOVERNMENT AUTHORITY	-	POSTED SPEED	70-110km/h
ROAD AUTHORITY	MAIN ROADS WA	WORKSITE SPEED	60km/h
CHECKED BY	TYLER HARTLEY	SIGNATURE	<i>Tyler Hartley</i>
ACCREDITATION	RTM-0066	SIGNATURE	<i>Michael Reed</i>
DESIGNED BY	MICHAEL REED	SIGNATURE	<i>Michael Reed</i>
ACCREDITATION	AWTM-23-11536-02		
GENERIC TRAFFIC GUIDANCE SCHEME REVERSIBLE FLOW SETUPS SINGLE LANE ROAD WORKSITE BETWEEN 1.2m AND 3.0m			
DRAWING NO	0922-01531-RF-012	REVISION	6