


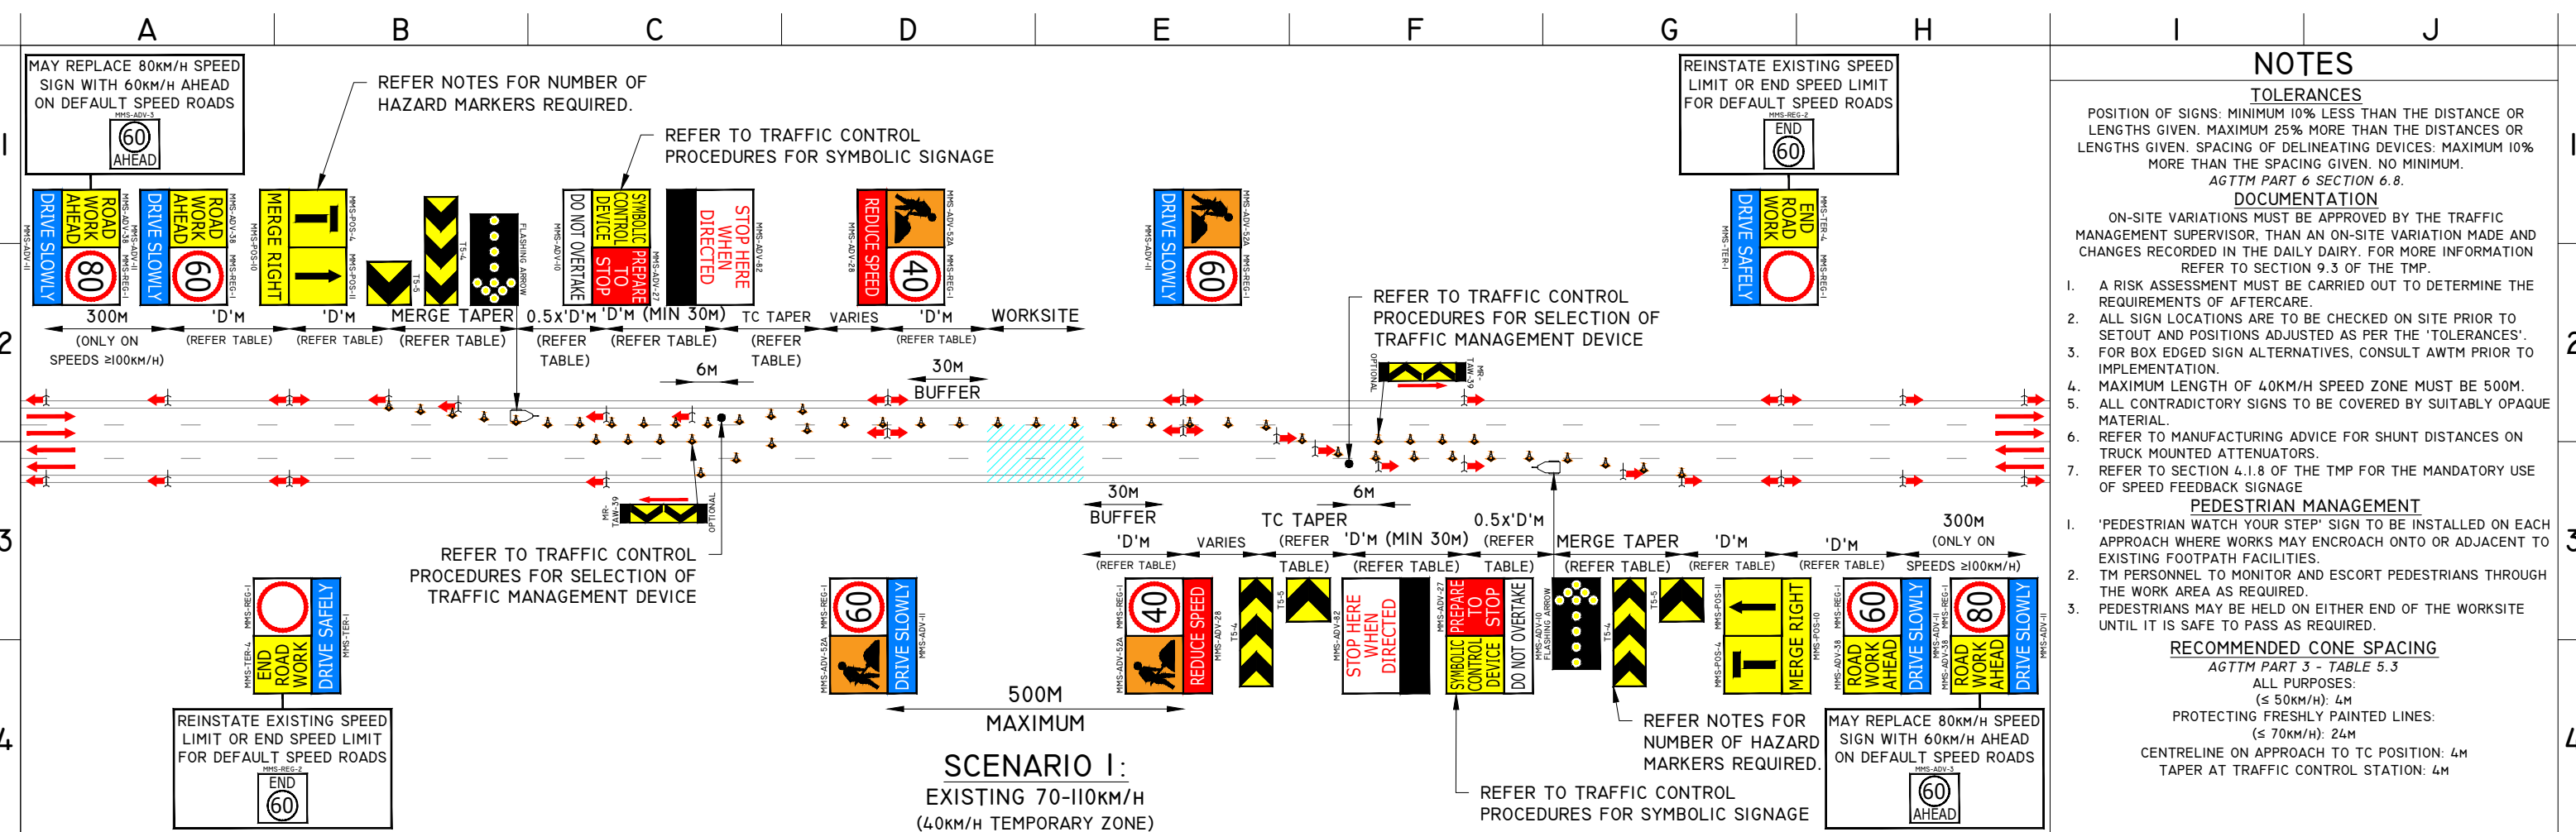

TRAFFIC CONTROL PROCEDURES

REFER TO TMP SECTION 4.1.7 PORTABLE TRAFFIC CONTROL DEVICES FOR MORE DETAILS

MANUAL TRAFFIC CONTROL

ACCREDITED TRAFFIC CONTROLLER

PORTABLE TRAFFIC CONTROL DEVICE (PTCD)

PORTABOOM

TEMPORARY TRAFFIC SIGNAL

SHADOW VEHICLE INSET

SHADOW VEHICLE MAY BE DISPENSED WITH UNDER A RISK ASSESSMENT BY AN RTM AS PART OF THE TM ADVICE. IN THE ABSENCE OF THE SHADOW VEHICLE A LOOKOUT PERSON IS REQUIRED. REFER TO SECTION 4.5 OF THE TMP FOR MORE DETAILS.

FLASHING ARROW

SHADOW VEHICLE

SHADOW VEHICLE 20-40M BUFFER WORK SITE

FLASHING ARROWBOARD ON TMA

VARIABLE MESSAGE BOARD DISPLAY 1 DISPLAY 2

TEMPORARY SPEED ZONE

REFER TO SECTION 4.5.1 OF THE TMP FOR TMA REQUIREMENTS

TABLES

SIGN SPACING		TAPER LENGTHS		
AGTMM PART 3 - TABLE 2.2		AGTMM PART 3 - TABLE 5.7		
SPEED LIMIT (KM/H)	DISTANCE ('D') (M)	SPEED LIMIT (KM/H)	TRAFFIC CONTROL TAPER (M)	MERGE TAPER (M)
55 OR LESS	15	45 OR LESS	15	15
56 TO 65	45	46 TO 55	15	30
GREATER THAN 65	EQUAL TO SPEED OF TRAFFIC IN KM/H	56 TO 65	30	60
MAXIMUM LENGTH OF SHUTTLE FLOW MAIN ROADS WA CoP SECTION 6.8.6 - TABLE 15		66 TO 75*	N/A	115
		76 TO 85*		130
		86 TO 95*		145
		96 TO 105*		160
		GREATER THAN 105*		180
VOLUMES (BOTH DIRECTION) (VPH)	LENGTH (BETWEEN TCS) (M)	*TAPER LENGTHS ARE BASED ON A: 3.5M WIDTH OF THE LANE TO BE CLOSED - LATERAL SHIFT TAPER LENGTH EQUAL TO 1.0M/s - MERGE TAPER LENGTH EQUAL TO 0.6M/s		
RESIDENTIAL STREET	60	TEMPORARY HAZARD MARKERS AGTMM PART 3 - 5.4.2 PAGE 65		
701 - 800	70			
601 - 700	100			
501 - 600	150			
401 - 500	250			
351 - 400	400			
301 - 350	600			
251 - 300	800	A CONTINUOUS LINE OF T5-4 HAZARD MARKERS MUST BE MADE USING THE FOLLOWING RECOMMENDED NUMBERS.		
201 - 250	1200			
151 - 200	1600			
≤ 150	2200			
RECOMMENDED LANE WIDTHS MRWA CoP SECTION 6.7 - TABLE 7				
RECOMMENDED LANE WIDTHS: ≤ 60KM/H: 3.2M 61 - 80KM/H: 3.5M		NUMBER OF SHIFT MARKERS		
MINIMUM LANE WIDTHS: ≤ 60KM/H: 3.0M 61 - 80KM/H: 3.2M				
SHUTTLE FLOW WITH CONTROL: 3.2M				