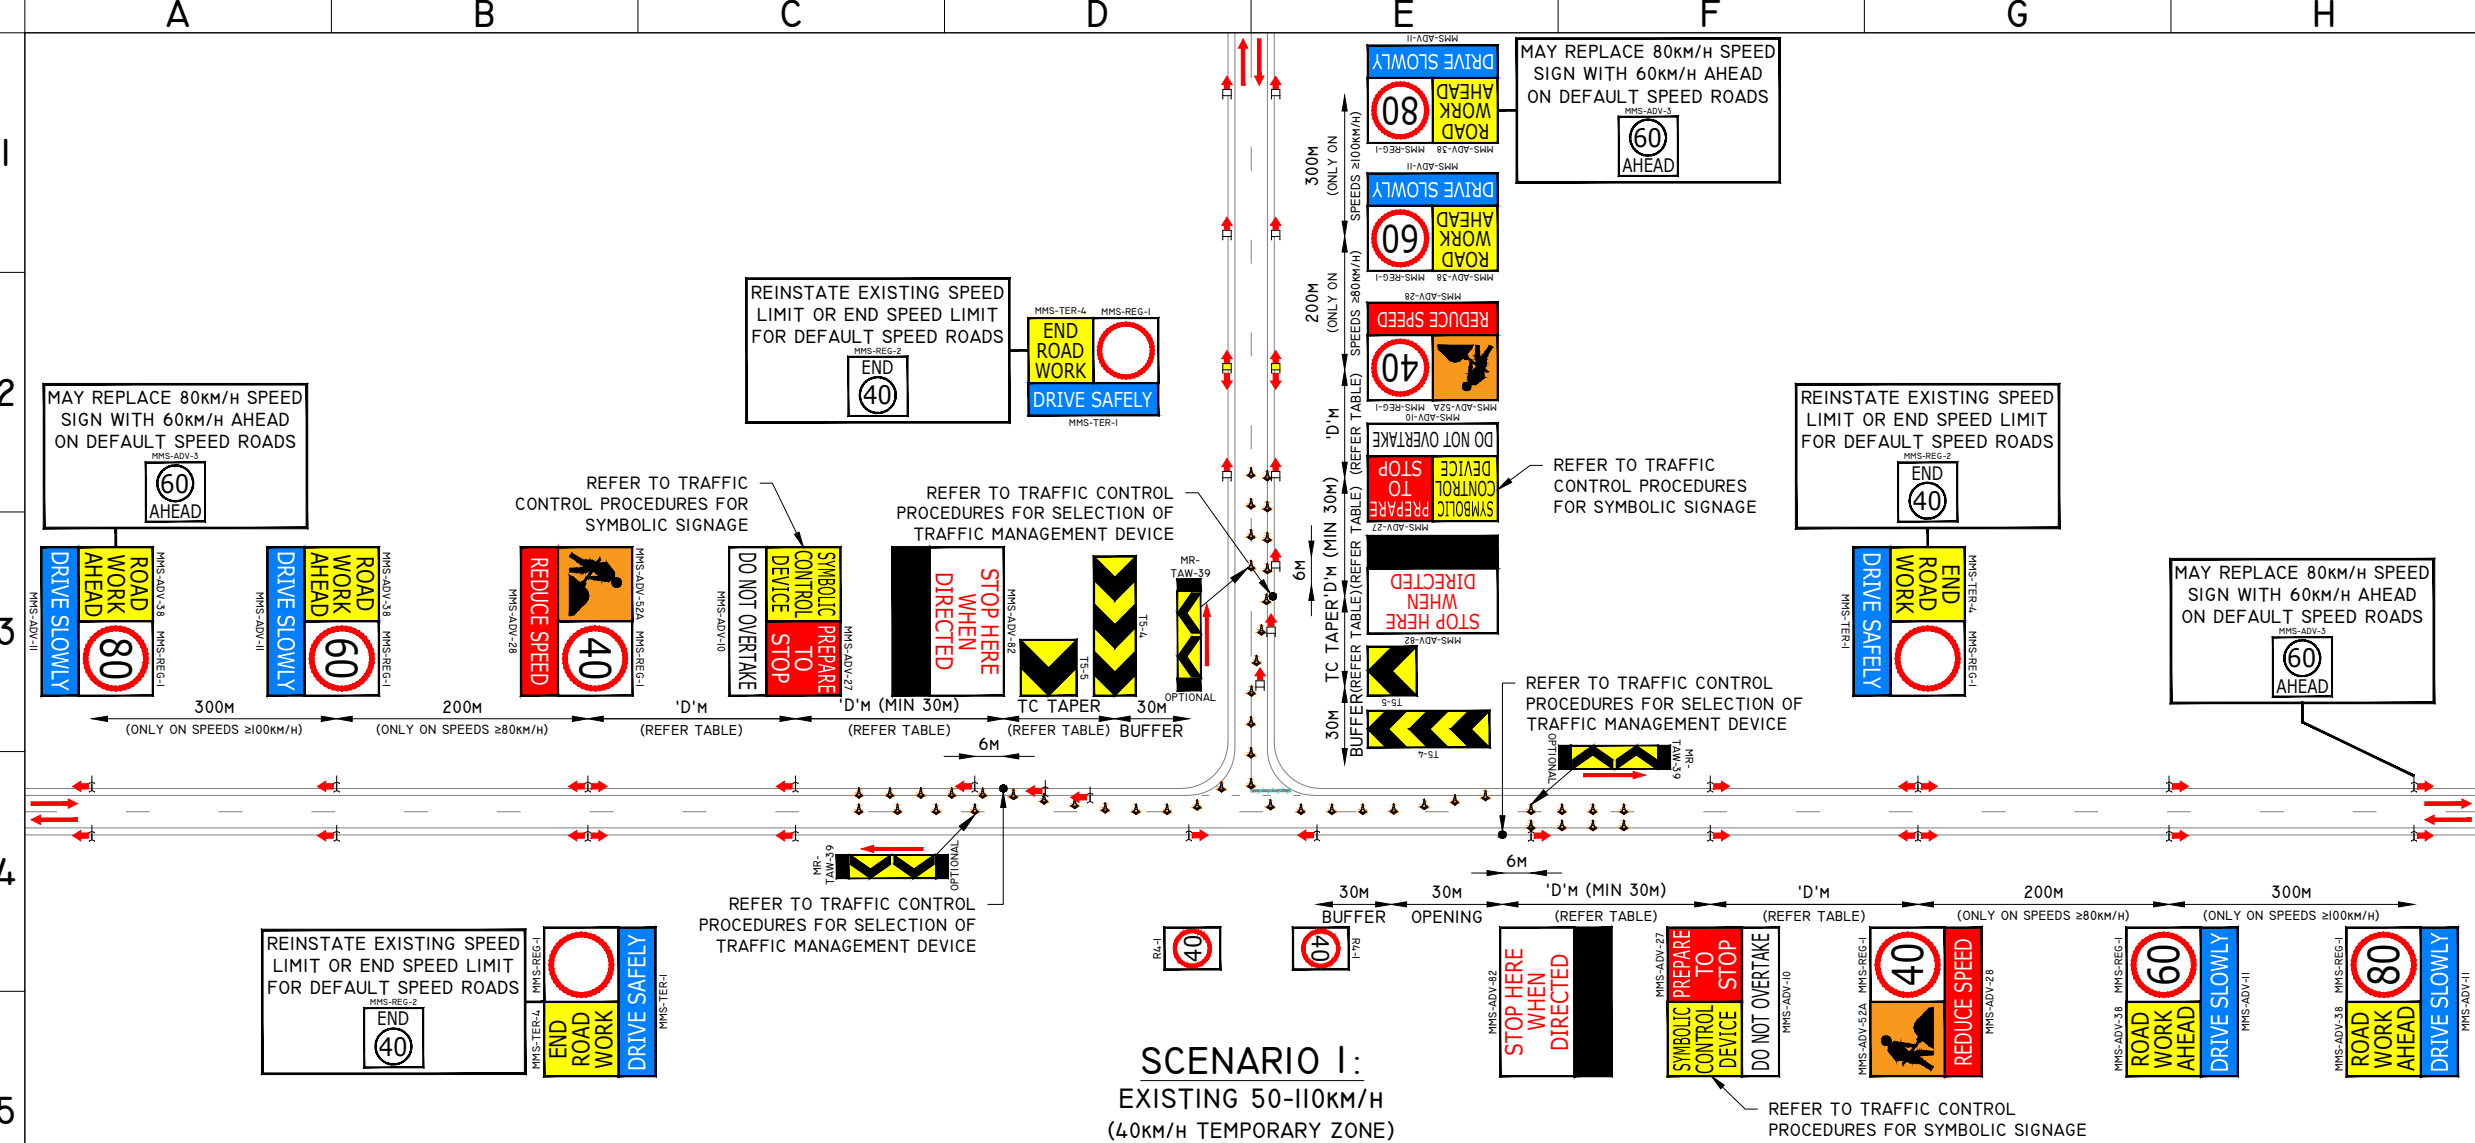




- NOTES
- TOLERANCES
- POSITION OF SIGNS: MINIMUM 10% LESS THAN THE DISTANCE OR LENGTHS GIVEN. MAXIMUM 25% MORE THAN THE DISTANCES OR LENGTHS GIVEN. SPACING OF DELINEATING DEVICES: MAXIMUM 10% MORE THAN THE SPACING GIVEN. NO MINIMUM.
- AGTTM PART 6 SECTION 6.8.
- DOCUMENTATION
- ON-SITE VARIATIONS MUST BE APPROVED BY THE TRAFFIC MANAGEMENT SUPERVISOR, THAN AN ON-SITE VARIATION MADE AND CHANGES RECORDED IN THE DAILY DAIRY. FOR MORE INFORMATION REFER TO SECTION 9.3 OF THE TMP.
1.

A RISK ASSESSMENT MUST BE CARRIED OUT TO DETERMINE THE REQUIREMENTS OF AFTERCARE.
2.

ALL SIGN LOCATIONS ARE TO BE CHECKED ON SITE PRIOR TO SETOUT AND POSITIONS ADJUSTED AS PER THE 'TOLERANCES'.
3.

FOR BOX EDGED SIGN ALTERNATIVES, CONSULT AWTM PRIOR TO IMPLEMENTATION.
4.

ALL CONTRADICTIONARY SIGNS TO BE COVERED BY SUITABLY OPAQUE MATERIAL.
5.

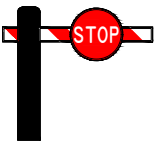
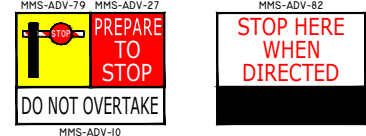
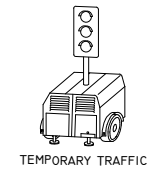
MAXIMUM LENGTH OF 40km/H TEMPORARY SPEED ZONE MUST BE 500M.
6.

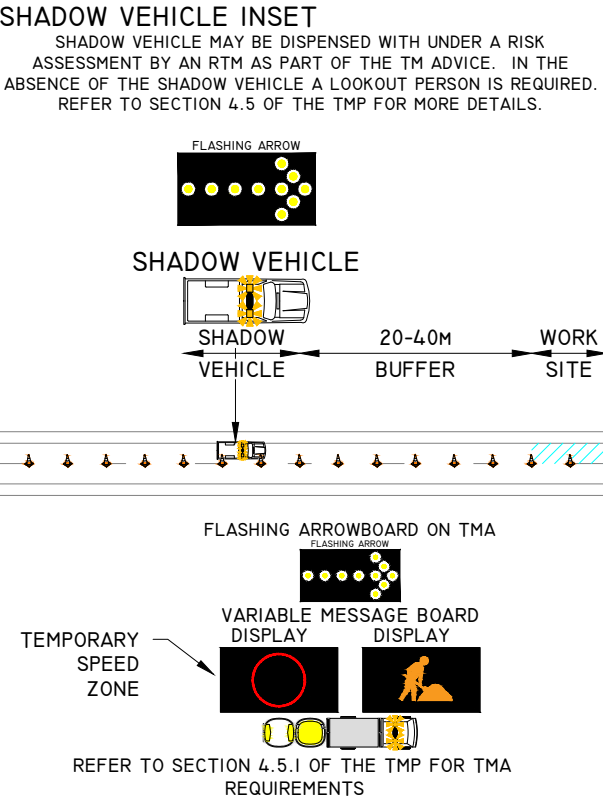
REFER TO SECTION 4.1.8 OF THE TMP FOR THE MANDATORY USE OF SPEED FEEDBACK SIGNAGE
- PEDESTRIAN MANAGEMENT
1.

'PEDESTRIAN WATCH YOUR STEP' SIGN TO BE INSTALLED ON EACH APPROACH WHERE WORKS MAY ENCROACH ONTO OR ADJACENT TO EXISTING FOOTPATH FACILITIES.
2.

TM PERSONNEL TO MONITOR AND ESCORT PEDESTRIANS THROUGH THE WORK AREA AS REQUIRED.
3.

PEDESTRIANS MAY BE HELD ON EITHER END OF THE WORKSITE UNTIL IT IS SAFE TO PASS AS REQUIRED.
- RECOMMENDED CONE SPACING
- AGTTM PART 3 - TABLE 5.3
- ALL PURPOSES:
- (≤ 50km/H): 4M
- PROTECTING FRESHLY PAINTED LINES:
- (≤ 70km/H): 24M
- CENTRELINE ON APPROACH TO TC POSITION: 4M
- TAPER AT TRAFFIC CONTROL STATION: 4M
- RECOMMENDED LANE WIDTHS
- MAIN ROADS WA CoP SECTION 6.7 - TABLE 9
- SHUTTLE FLOW WITH CONTROL: 3.2M

TRAFFIC CONTROL PROCEDURES		
REFER TO TMP SECTION 4.1.7 PORTABLE TRAFFIC CONTROL DEVICES FOR MORE DETAILS		
MANUAL TRAFFIC CONTROL		
 ACCREDITED TRAFFIC CONTROLLER		
PORTABLE TRAFFIC CONTROL DEVICE (PTCD)		
 PORTABOOM		
 TEMPORARY TRAFFIC SIGNAL		



TABLES	
MAXIMUM LENGTH OF SHUTTLE FLOW MAIN ROADS WA CoP SECTION 6.8.6 - TABLE 15	
VOLUMES (BOTH DIRECTION) (VPH)	LENGTH (BETWEEN TCS) (M)
RESIDENTIAL STREET	60
701 - 800	70
601 - 700	100
501 - 600	150
401 - 500	250
351 - 400	400
301 - 350	600
251 - 300	800
201 - 250	1200
151 - 200	1600
≤ 150	2200

TAPER LENGTHS AGTTM PART 3 - TABLE 5.7	
SPEED LIMIT (KM/H)	TRAFFIC CONTROL TAPER (M)
45 OR LESS	15
46 TO 55	15
56 TO 65	30
66 TO 75*	N/A
76 TO 85*	
86 TO 95*	
96 TO 105*	
GREATER THAN 105*	
*TAPER LENGTHS ARE BASED ON A: • 3.5M WIDTH OF THE LANE TO BE CLOSED • LATERAL SHIFT TAPER LENGTH EQUAL TO 1.0M/S • MEDIAN SPEED FOR EACH RANGE (I.E 76 - 85 = 80KM/H)	

SIGN SPACING AGTTM PART 3 - TABLE 2.2	
SPEED LIMIT (KM/H)	DISTANCE ('D') (M)
55 OR LESS	15
56 TO 65	45
GREATER THAN 65	EQUAL TO SPEED OF TRAFFIC IN KM/H