


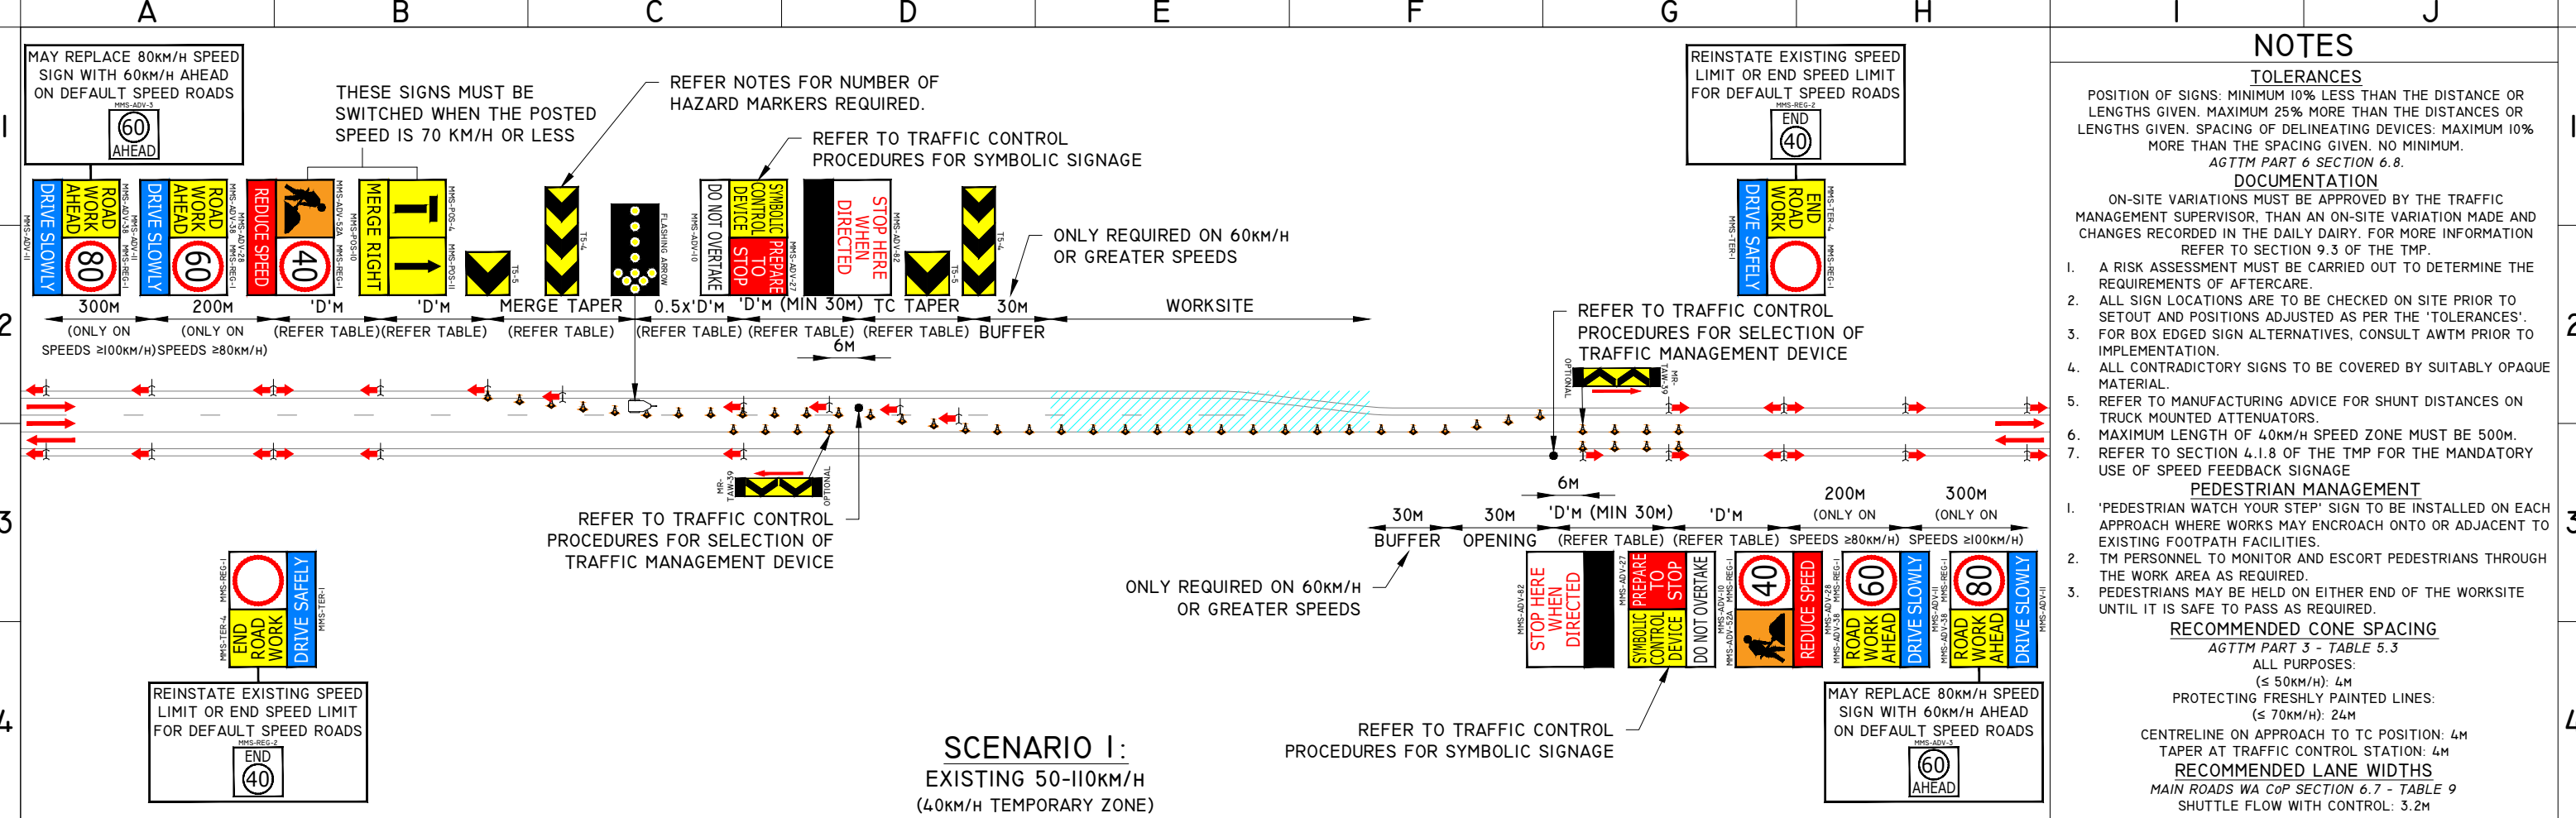

- NOTES
- TOLERANCES
- POSITION OF SIGNS: MINIMUM 10% LESS THAN THE DISTANCE OR LENGTHS GIVEN. MAXIMUM 25% MORE THAN THE DISTANCES OR LENGTHS GIVEN. SPACING OF DELINEATING DEVICES: MAXIMUM 10% MORE THAN THE SPACING GIVEN. NO MINIMUM.
- AGTTM PART 6 SECTION 6.8.
- DOCUMENTATION
- ON-SITE VARIATIONS MUST BE APPROVED BY THE TRAFFIC MANAGEMENT SUPERVISOR, THAN AN ON-SITE VARIATION MADE AND CHANGES RECORDED IN THE DAILY DAIRY. FOR MORE INFORMATION REFER TO SECTION 9.3 OF THE TMP.
1.

A RISK ASSESSMENT MUST BE CARRIED OUT TO DETERMINE THE REQUIREMENTS OF AFTERCARE.
2.

ALL SIGN LOCATIONS ARE TO BE CHECKED ON SITE PRIOR TO SETOUT AND POSITIONS ADJUSTED AS PER THE 'TOLERANCES'.
3.

FOR BOX EDGED SIGN ALTERNATIVES, CONSULT AWTM PRIOR TO IMPLEMENTATION.
4.

ALL CONTRADICTIONARY SIGNS TO BE COVERED BY SUITABLY OPAQUE MATERIAL.
5.

REFER TO MANUFACTURING ADVICE FOR SHUNT DISTANCES ON TRUCK MOUNTED ATTENUATORS.
6.

MAXIMUM LENGTH OF 40km/h SPEED ZONE MUST BE 500M.
7.

REFER TO SECTION 4.1.8 OF THE TMP FOR THE MANDATORY USE OF SPEED FEEDBACK SIGNAGE
- PEDESTRIAN MANAGEMENT
1.

'PEDESTRIAN WATCH YOUR STEP' SIGN TO BE INSTALLED ON EACH APPROACH WHERE WORKS MAY ENCROACH ONTO OR ADJACENT TO EXISTING FOOTPATH FACILITIES.
2.

TM PERSONNEL TO MONITOR AND ESCORT PEDESTRIANS THROUGH THE WORK AREA AS REQUIRED.
3.

PEDESTRIANS MAY BE HELD ON EITHER END OF THE WORKSITE UNTIL IT IS SAFE TO PASS AS REQUIRED.
- RECOMMENDED CONE SPACING
- AGTTM PART 3 - TABLE 5.3
- ALL PURPOSES:
- ≤ 50km/h): 4M
- PROTECTING FRESHLY PAINTED LINES:
- ≤ 70km/h): 24M
- CENTRELINE ON APPROACH TO TC POSITION: 4M
- TAPER AT TRAFFIC CONTROL STATION: 4M
- RECOMMENDED LANE WIDTHS
- MAIN ROADS WA CoP SECTION 6.7 - TABLE 9
- SHUTTLE FLOW WITH CONTROL: 3.2M

TRAFFIC CONTROL PROCEDURES

REFER TO TMP SECTION 4.1.7 PORTABLE TRAFFIC CONTROL DEVICES FOR MORE DETAILS

MANUAL TRAFFIC CONTROL

5

ACCREDITED TRAFFIC CONTROLLER

6

PORTABLE TRAFFIC CONTROL DEVICE (PTCD)

7

PORTABOOM

8

TEMPORARY TRAFFIC SIGNAL

END OF QUEUE PROTECTION

DEVICE MAY BE A TRAFFIC CONTROLLER, PORTABOOM OR TEMPORARY SIGNAL

MUST BE IMPLEMENTED ON ALL ROADS WITH A POSTED SPEED OF 80km/h OR GREATER. REFER TO TGS-TMC-RF-022, 023 AND 044 FOR MORE INFORMATION.

MANUAL TRAFFIC CONTROL IS NOT PERMITTED ON THE MAIN ROADS NETWORK WITH THE EXCEPTIONS LISTED UNDER SECTION 4.1.7 (PORTABLE TRAFFIC CONTROL DEVICES) OF THE TMP AND IN THE MAIN ROADS CODE OF PRACTICE.

ON ALL OTHER ROADS, PTCDS MUST BE USED UNDER THE FOLLOWING CONDITIONS:

• A PERMANENT SPEED LIMIT OF 90m/h OR MORE AND OVER 2,000VPD; OR

• A PERMANENT SPEED LIMIT OF 70km/h OR MORE AND OVER 10,000VPD.

PTCDs SHOULD BE CONSIDERED ON ALL WORKS AND ONLY BE SUPPLEMENTED WITH MANUAL TRAFFIC CONTROL UNDER AN AWTM/WTM RISK ASSESSMENT.

SHADOW VEHICLE INSET

SHADOW VEHICLE MAY BE DISPENSED WITH UNDER A RISK ASSESSMENT BY AN RTM AS PART OF THE TM ADVICE. IN THE ABSENCE OF THE SHADOW VEHICLE A LOOKOUT PERSON IS REQUIRED. REFER TO SECTION 4.5 OF THE TMP FOR MORE DETAILS.

FLASHING ARROWBOARD ON TMA

VARIABLE MESSAGE BOARD

DISPLAY 1

DISPLAY 2

TEMPORARY SPEED ZONE

REFER TO SECTION 4.5.1 OF THE TMP FOR TMA REQUIREMENTS

TABLES

SIGN SPACING

AGTTM PART 3 - TABLE 2.2

SPEED LIMIT (KM/H)	DISTANCE ('D')
55 OR LESS	15
56 TO 65	45
GREATER THAN 65	EQUAL TO SPEED OF TRAFFIC IN KM/H

MAXIMUM LENGTH OF SHUTTLE FLOW

MAIN ROADS WA CoP SECTION 6.8.6 - TABLE 15

VOLUMES (BOTH DIRECTION) (VPH)	LENGTH (BETWEEN TCS) (M)
RESIDENTIAL STREET	60
701 - 800	70
601 - 700	100
501 - 600	150
401 - 500	250
351 - 400	400
301- 350	600
251 - 300	800
201 - 250	1200
151 - 200	1600
≤ 150	2200

TAPER LENGTHS

AGTTM PART 3 - TABLE 5.7

SPEED LIMIT (KM/H)	TRAFFIC CONTROL TAPER (M)	MERGE TAPER (M)
45 OR LESS	15	15
46 TO 55	15	30
56 TO 65	30	60
66 TO 75*	N/A	115
76 TO 85*		130
86 TO 95*		145
96 TO 105*		160
GREATER THAN 105*		180

*TAPER LENGTHS ARE BASED ON A:

• 3.5M WIDTH OF THE LANE TO BE CLOSED

• LATERAL SHIFT TAPER LENGTH EQUAL TO 1.0M/s

• MERGE TAPER LENGTH EQUAL TO 0.6M/s

• MEDIAN SPEED FOR EACH RANGE (I.E 76 - 85 = 80km/h)

TEMPORARY HAZARD MARKERS

AGTTM PART 3 - 5.4.2 PAGE 65

A CONTINUOUS LINE OF T5-4 HAZARD MARKERS MUST BE MADE USING THE FOLLOWING RECOMMENDED NUMBERS.

NUMBER OF SHIFT MARKERS	LENGTH OF TAPER
2	≤60M
4	≤115M
6	≤130M
8	≤145M
EVERY 20M	>145M
	WITHIN A CLOSED LANE