

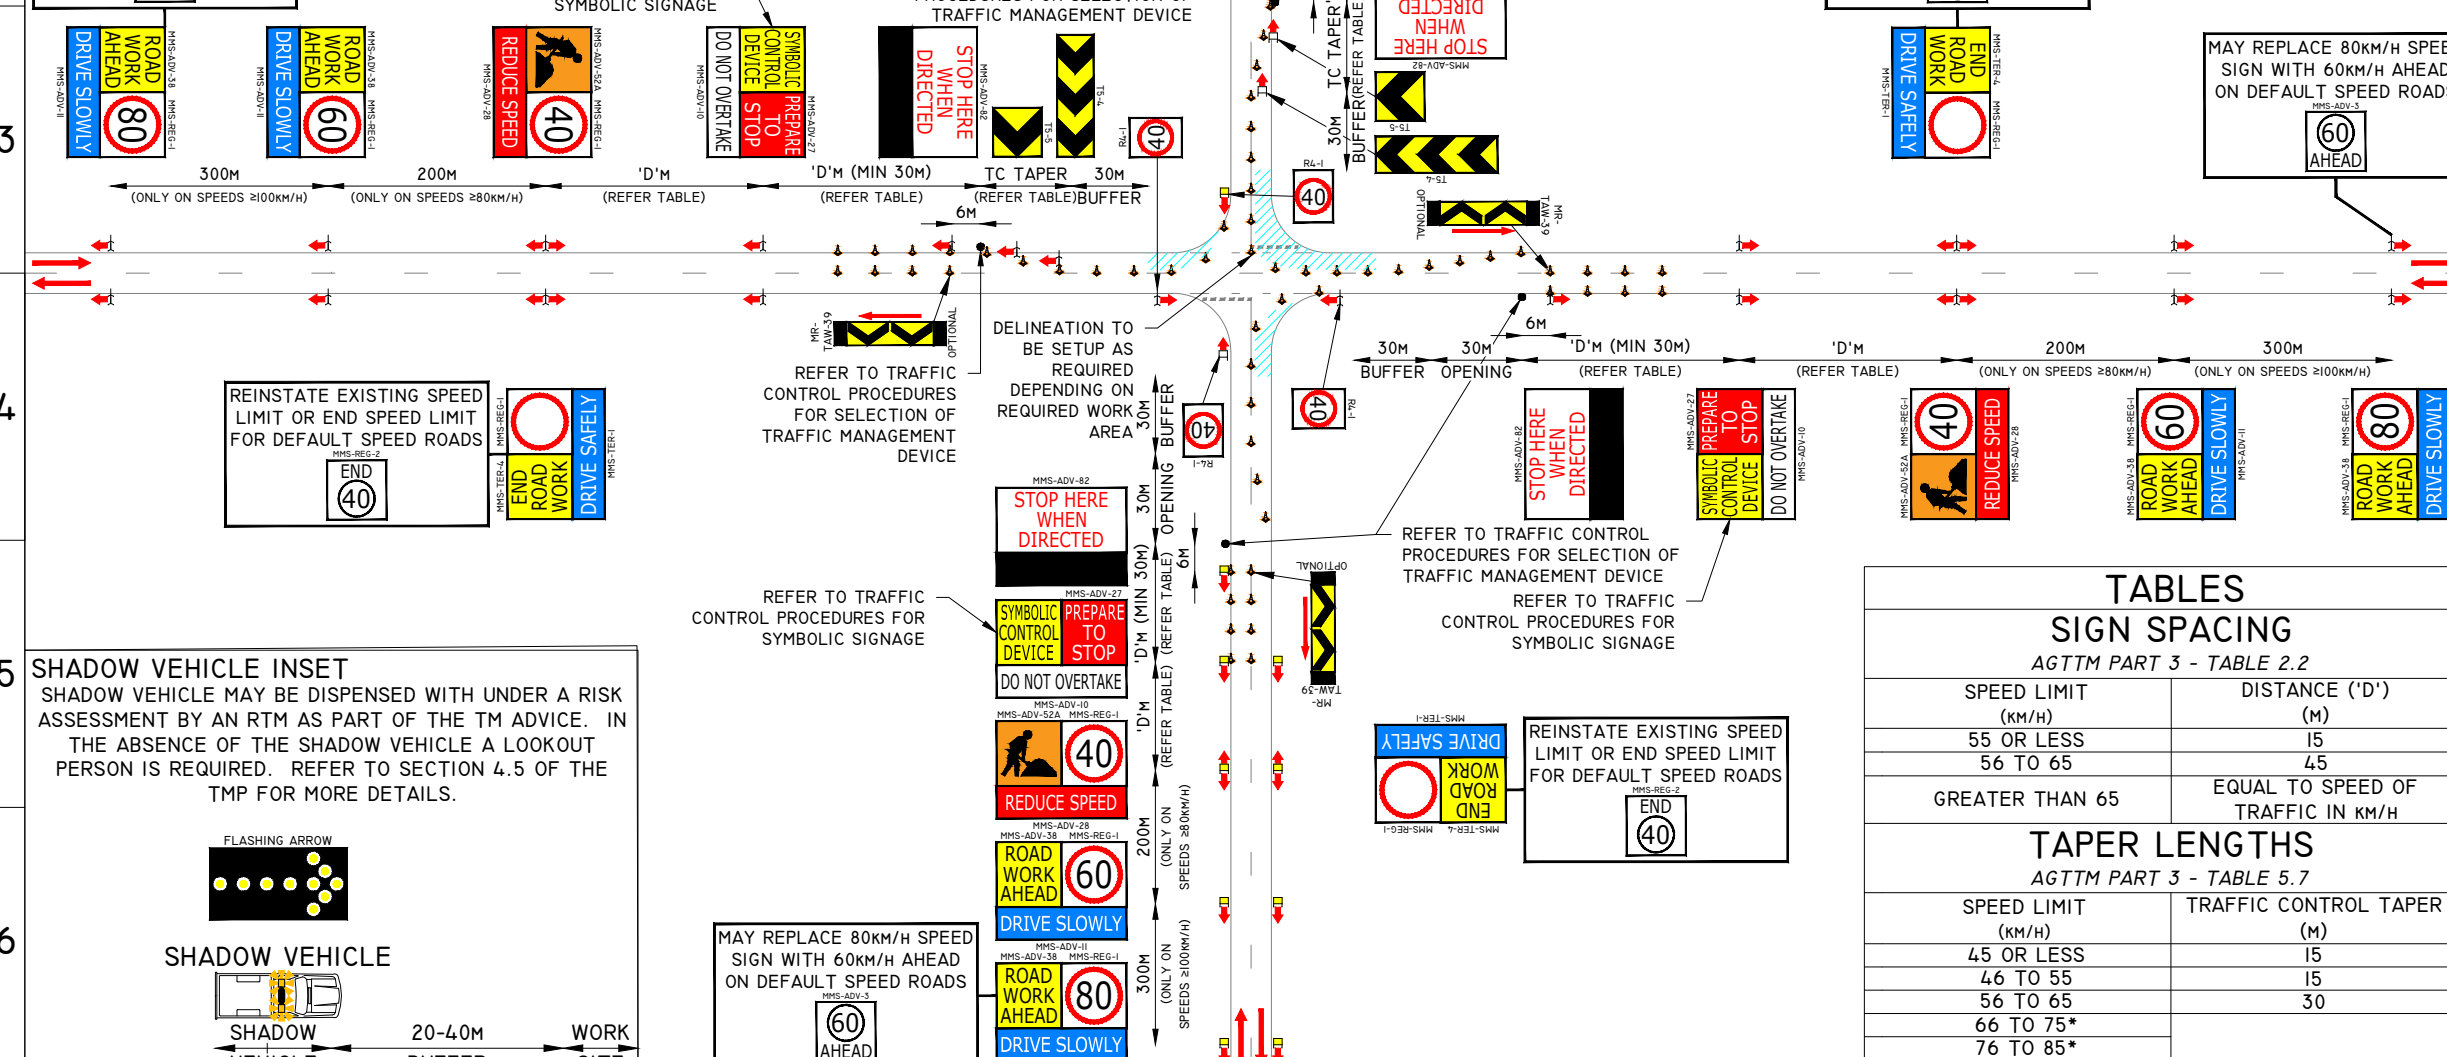


SCENARIO I:
EXISTING 50-110KM/H
(40KM/H TEMPORARY ZONE)


MAY REPLACE 80KM/H SPEED
SIGN WITH 60KM/H AHEAD
ON DEFAULT SPEED ROADS

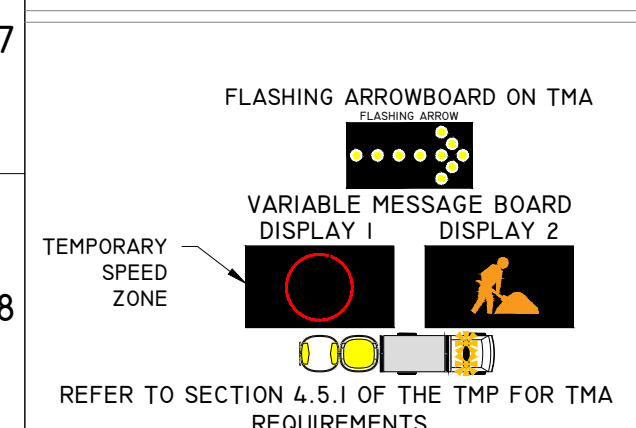

SHADOW VEHICLE INSET
SHADOW VEHICLE MAY BE DISPENSED WITH UNDER A RISK
ASSESSMENT BY AN RTM AS PART OF THE TM ADVICE. IN
THE ABSENCE OF THE SHADOW VEHICLE A LOOKOUT
PERSON IS REQUIRED. REFER TO SECTION 4.5 OF THE
TMP FOR MORE DETAILS.

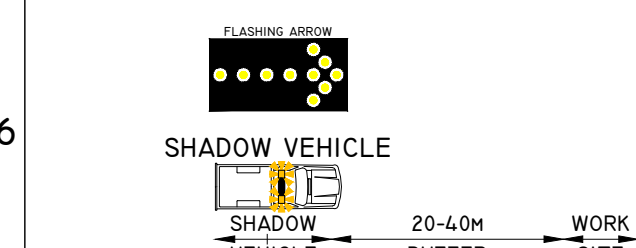

TRAFFIC CONTROL PROCEDURES
REFER TO TMP SECTION 4.1.7 PORTABLE TRAFFIC CONTROL DEVICES FOR MORE DETAILS

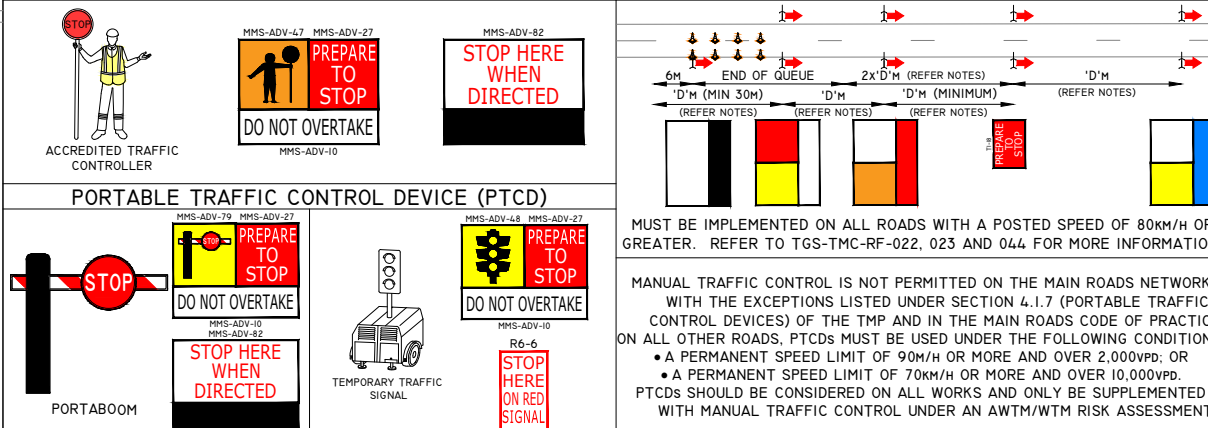

TABLES
SIGN SPACING
AGTTM PART 3 - TABLE 2.2

SPEED LIMIT (KM/H)	DISTANCE ('D') (M)
55 OR LESS	15
56 TO 65	45
GREATER THAN 65	EQUAL TO SPEED OF TRAFFIC IN KM/H

TAPER LENGTHS
AGTTM PART 3 - TABLE 5.7

SPEED LIMIT (KM/H)	TRAFFIC CONTROL TAPER (M)
45 OR LESS	15
46 TO 55	15
56 TO 65	30
66 TO 75*	
76 TO 85*	
86 TO 95*	
96 TO 105*	
GREATER THAN 105*	N/A

*TAPER LENGTHS ARE BASED ON A:
• 3.5M WIDTH OF THE LANE TO BE CLOSED
• LATERAL SHIFT TAPER LENGTH EQUAL TO 1.0M/S
• MEDIAN SPEED FOR EACH RANGE (I.E 76 - 85 = 80KM/H)

MAXIMUM LENGTH OF SHUTTLE FLOW
MAIN ROADS WA CoP SECTION 6.8.6 - TABLE 15

VOLUMES (BOTH DIRECTION) (VPH)	LENGTH (BETWEEN TCS) (M)
RESIDENTIAL STREET	60
701 - 800	70
601 - 700	100
501 - 600	150
401 - 500	250
351 - 400	400
301 - 350	600
251 - 300	800
201 - 250	1200
151 - 200	1600
≤ 150	2200

NOTES

TOLERANCES

POSITION OF SIGNS:

MINIMUM 10% LESS THAN THE DISTANCE OR LENGTHS GIVEN.

MAXIMUM 25% MORE THAN THE DISTANCES OR LENGTHS GIVEN.

SPACING OF DELINEATING DEVICES:

MAXIMUM 10% MORE THAN THE SPACING GIVEN.

NO MINIMUM.

AGTTM PART 6 SECTION 6.8.

DOCUMENTATION

ON-SITE VARIATIONS MUST BE APPROVED BY THE TRAFFIC
MANAGEMENT SUPERVISOR. THAN AN ON-SITE VARIATION MADE AND
CHANGES RECORDED IN THE DAILY DAIRY. FOR MORE INFORMATION
REFER TO SECTION 9.3 OF THE TMP.

GENERAL NOTES

1. A RISK ASSESSMENT MUST BE CARRIED OUT TO DETERMINE
THE REQUIREMENTS OF AFTERCARE.

2. ALL SIGN LOCATIONS ARE TO BE CHECKED ON SITE PRIOR TO
SETOUT AND POSITIONS ADJUSTED AS PER THE
'TOLERANCES'.

3. ALL CONTRADICTIONARY SIGNS TO BE COVERED BY SUITABLY
OPAQUE MATERIAL.

4. FOR BOX EDGED SIGN ALTERNATIVES, CONSULT AWTM PRIOR
TO IMPLEMENTATION.

5. MAXIMUM LENGTH OF 40KM/H TEMPORARY SPEED ZONE MUST
BE 500M.

6. SHADOW VEHICLE MAY BE DISPENSED WITH UNDER RISK
ASSESSMENT UNDERTAKEN BY AN RTM AS PART OF THE TM
ADVICE. IN THE ABSENCE OF SHADOW VEHICLE A LOOKOUT
PERSON IS REQUIRED. REFER TO SECTION 4.5 OF THE TMP
FOR MORE DETAILS.

7. REFER TO SECTION 4.1.8 OF THE TMP FOR THE MANDATORY
USE OF SPEED FEEDBACK SIGNAGE

PEDESTRIAN MANAGEMENT

1. 'PEDESTRIAN WATCH YOUR STEP' SIGN TO BE INSTALLED ON
EACH APPROACH WHERE WORKS MAY ENCROACH ONTO OR
ADJACENT TO EXISTING FOOTPATH FACILITIES.

2. TM PERSONNEL TO MONITOR AND ESCORT PEDESTRIANS
THROUGH THE WORK AREA AS REQUIRED.

3. PEDESTRIANS MAY BE HELD ON EITHER END OF THE WORKSITE
UNTIL IT IS SAFE TO PASS AS REQUIRED.

RECOMMENDED CONE SPACING

AGTTM PART 3 - TABLE 5.3

ALL PURPOSES:

(≤ 50KM/H): 4M

PROTECTING FRESHLY PAINTED LINES:

(≤ 70KM/H): 24M

CENTRELINE ON APPROACH TO TC POSITION: 4M

TAPER AT TRAFFIC CONTROL STATION: 4M

RECOMMENDED LANE WIDTHS

MAIN ROADS WA CoP SECTION 6.7 - TABLE 9

SHUTTLE FLOW WITH CONTROL: 3.2M

LEGEND

EXISTING ROAD

PROPOSED CONES

WORKSITE

METROPOLITAN REGIONS
TRAFFIC MANAGEMENT BRANCH

WATERLOO CRESCENT
TELEPHONE (08) 138 138

EAST PERTH 6004

DATE OF DRAWING
2025 JULY

SCALE
-

LOCAL GOVERNMENT AUTHORITY
-

POSTED SPEED
50-110KM/H

ROAD AUTHORITY
MAIN ROADS WA

WORKSITE SPEED
40KM/H

CHECKED BY
TYLER HARTLEY

SIGNATURE

ACCREDITATION
RTM-0066

SIGNATURE

DESIGNED BY
MICHAEL REED

ACCREDITATION
AWTM-23-11536-02

GENERIC TRAFFIC GUIDANCE SCHEME
REVERSIBLE FLOW SETUPS
4-WAY INTERSECTION
WORKSITE WITHIN 1.2M

DRAWING NO
0922-01531-RF-035

REVISION
6