


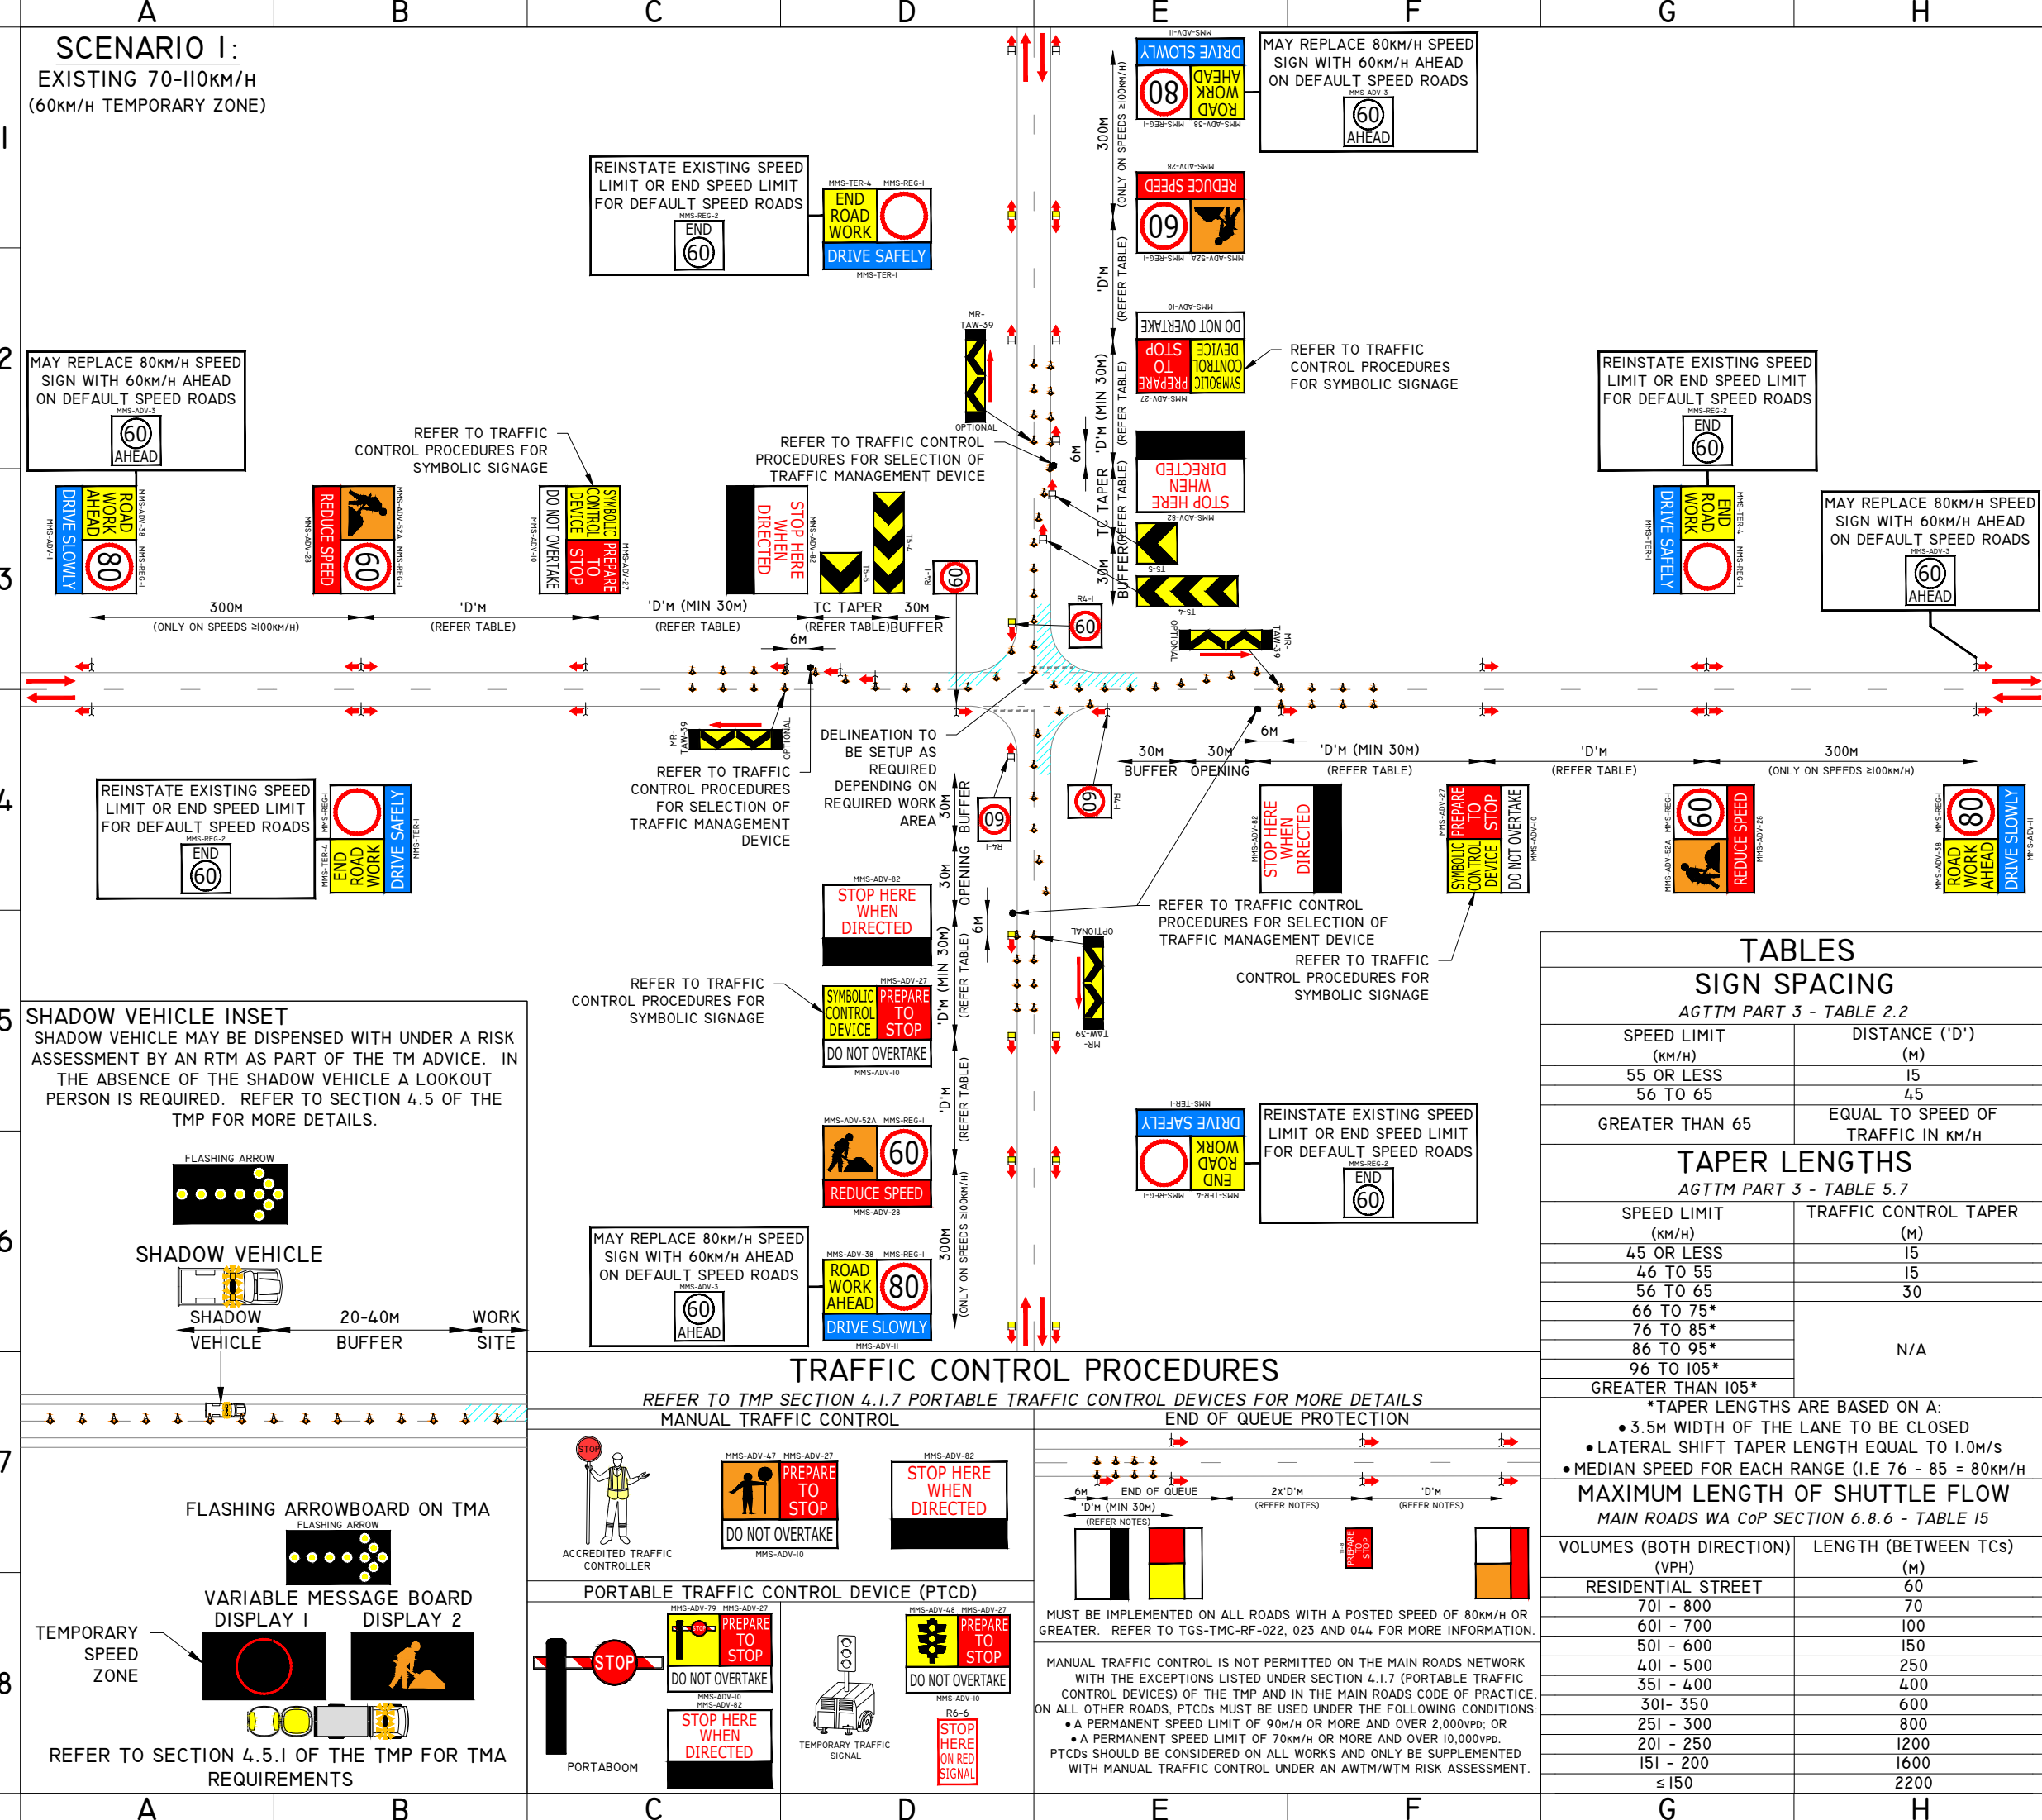

NOTES

TOLERANCES
POSITION OF SIGNS:
MINIMUM 10% LESS THAN THE DISTANCE OR LENGTHS GIVEN.
MAXIMUM 25% MORE THAN THE DISTANCES OR LENGTHS GIVEN.
SPACING OF DELINEATING DEVICES:
MAXIMUM 10% MORE THAN THE SPACING GIVEN.
NO MINIMUM.
AGTTM PART 6 SECTION 6.8.

DOCUMENTATION
ON-SITE VARIATIONS MUST BE APPROVED BY THE TRAFFIC MANAGEMENT SUPERVISOR. THAN AN ON-SITE VARIATION MADE AND CHANGES RECORDED IN THE DAILY DAIRY. FOR MORE INFORMATION REFER TO SECTION 9.3 OF THE TMP.

GENERAL NOTES

- A RISK ASSESSMENT MUST BE CARRIED OUT TO DETERMINE THE REQUIREMENTS OF AFTERCARE.
- ALL SIGN LOCATIONS ARE TO BE CHECKED ON SITE PRIOR TO SETOUT AND POSITIONS ADJUSTED AS PER THE 'TOLERANCES'.
- ALL CONTRADICTIONARY SIGNS TO BE COVERED BY SUITABLY OPAQUE MATERIAL.
- FOR BOX EDGED SIGN ALTERNATIVES, CONSULT AWTM PRIOR TO IMPLEMENTATION.
- SHADOW VEHICLE MAY BE DISPENSED WITH UNDER RISK ASSESSMENT UNDERTAKEN BY AN RTM AS PART OF THE TM ADVICE. IN THE ABSENCE OF SHADOW VEHICLE A LOOKOUT PERSON IS REQUIRED. REFER TO SECTION 4.5 OF THE TMP FOR MORE DETAILS.
- REFER TO SECTION 4.1.8 OF THE TMP FOR THE MANDATORY USE OF SPEED FEEDBACK SIGNAGE

PEDESTRIAN MANAGEMENT

- 'PEDESTRIAN WATCH YOUR STEP' SIGN TO BE INSTALLED ON EACH APPROACH WHERE WORKS MAY ENCROACH ONTO OR ADJACENT TO EXISTING FOOTPATH FACILITIES.
- TM PERSONNEL TO MONITOR AND ESCORT PEDESTRIANS THROUGH THE WORK AREA AS REQUIRED.
- PEDESTRIANS MAY BE HELD ON EITHER END OF THE WORKSITE UNTIL IT IS SAFE TO PASS AS REQUIRED.

RECOMMENDED CONE SPACING
AGTTM PART 3 - TABLE 5.3
ALL PURPOSES:
(60 - 70km/h): 12M
PROTECTING FRESHLY PAINTED LINES:
(≤ 70km/h): 24M
CENTRELINE ON APPROACH TO TC POSITION: 4M
TAPER AT TRAFFIC CONTROL STATION: 4M

RECOMMENDED LANE WIDTHS
MAIN ROADS WA CoP SECTION 6.7 - TABLE 9
SHUTTLE FLOW WITH CONTROL: 3.2M

LEGEND

- EXISTING ROAD
- PROPOSED CONES
- WORKSITE

mainroads
WESTERN AUSTRALIA

METROPOLITAN REGIONS
TRAFFIC MANAGEMENT BRANCH
WATERLOO CRESCENT
TELEPHONE (08) 138 138
EAST PERTH 6004

DATE OF DRAWING: 2025 JULY
LOCAL GOVERNMENT AUTHORITY: -
ROAD AUTHORITY: MAIN ROADS WA
CHECKED BY: TYLER HARTLEY
ACCREDITATION: RTM-0066
DESIGNED BY: MICHAEL REED
ACCREDITATION: AWTM-23-11536-02

SCALE: -
POSTED SPEED: 70-110KM/H
WORKSITE SPEED: 60KM/H
SIGNATURE: Tyler Hartley
SIGNATURE: Michael Reed

GENERIC TRAFFIC GUIDANCE SCHEME
REVERSIBLE FLOW SETUPS
4-WAY INTERSECTION
WORKSITE BETWEEN 1.2M AND 3.0M

DRAWING NO: 0922-01531-RF-037
REVISION: 6