


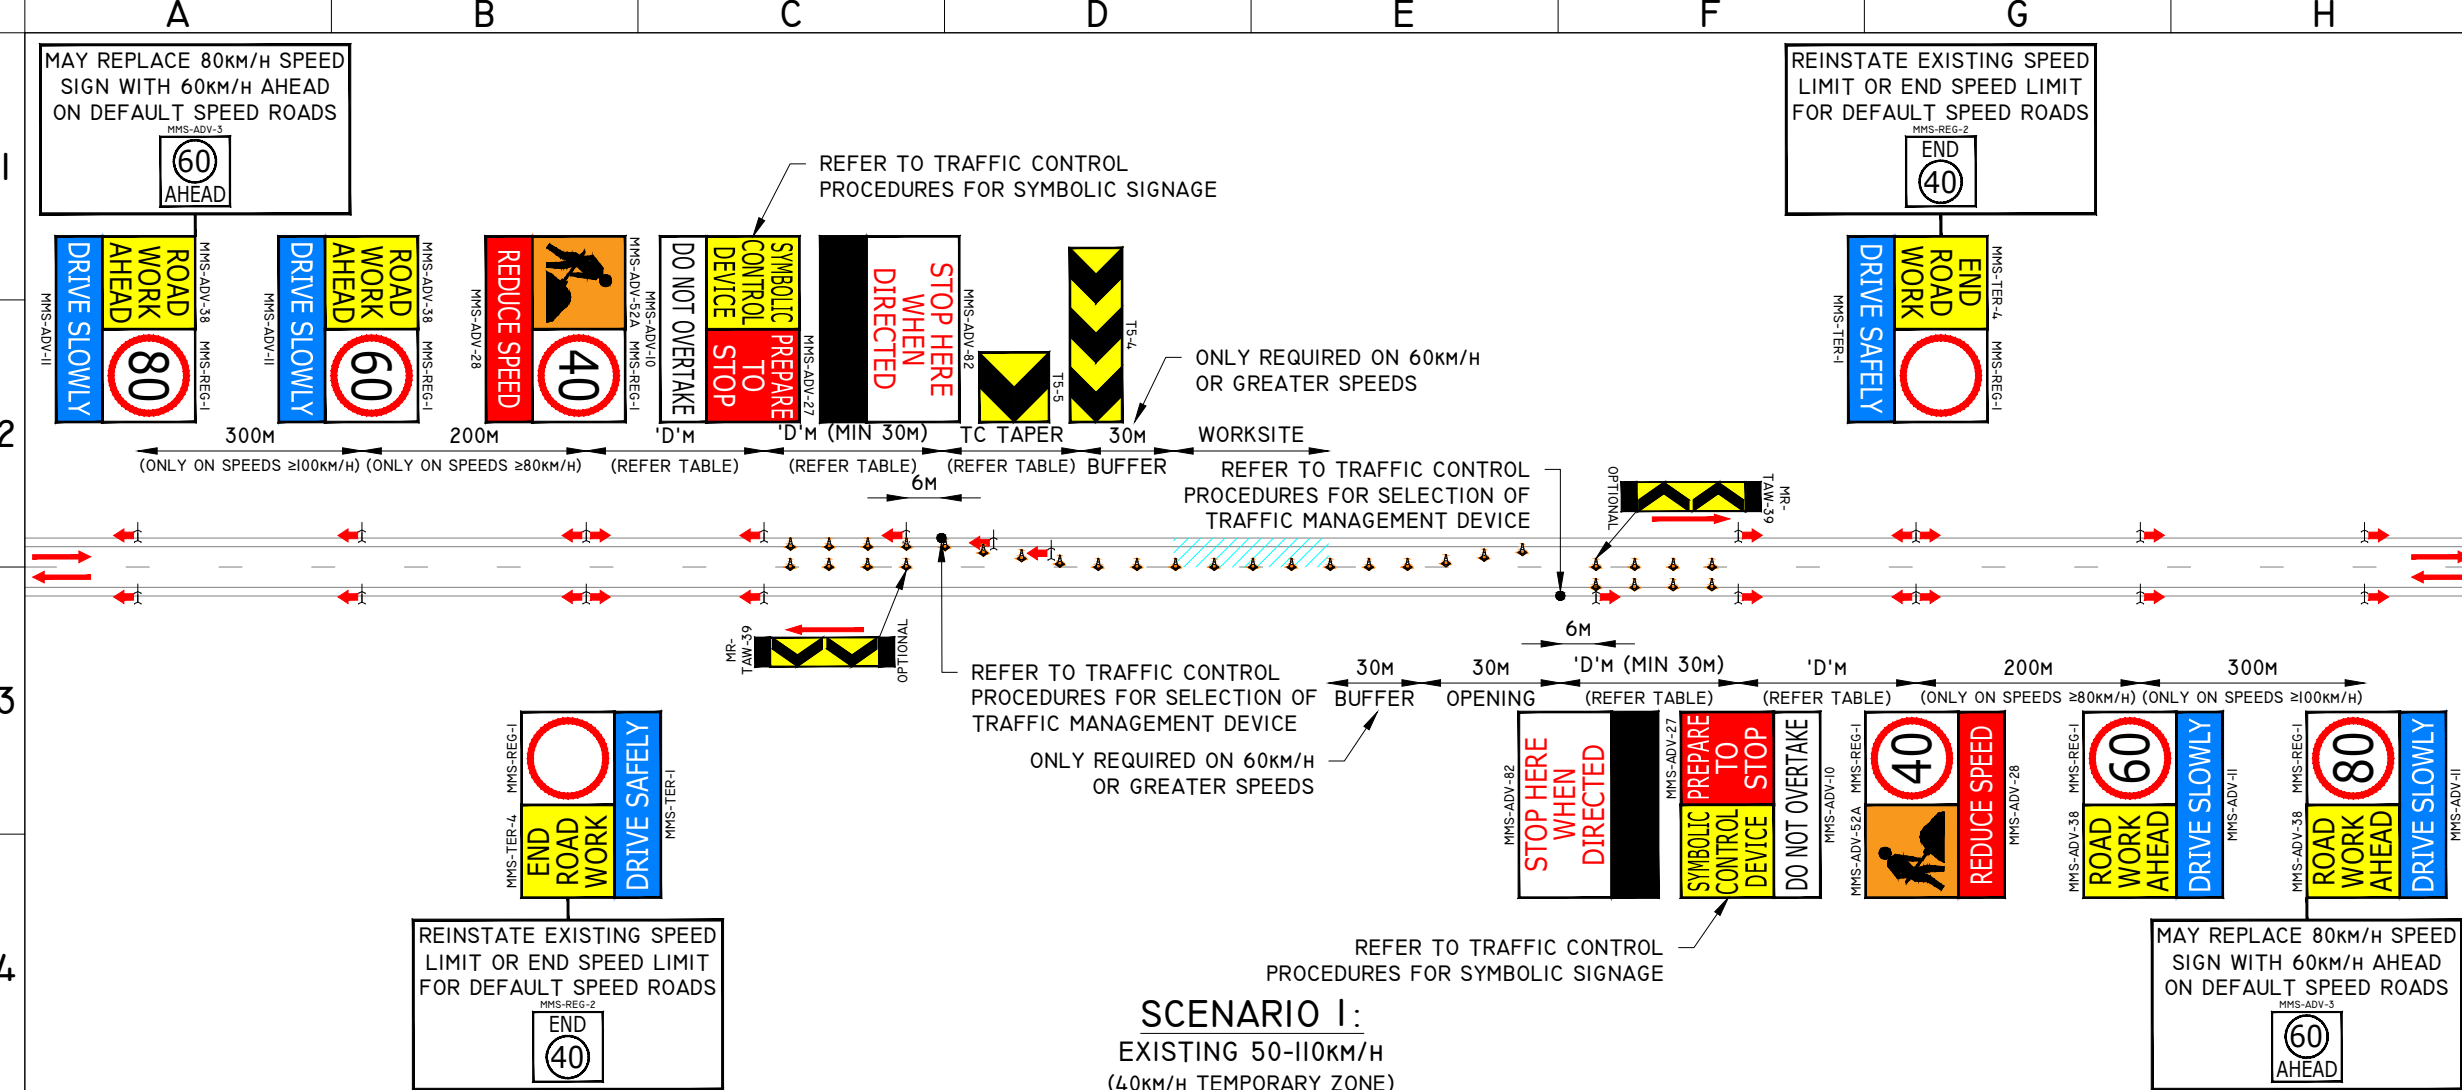

NOTES

TOLERANCES
POSITION OF SIGNS:
MINIMUM 10% LESS THAN THE DISTANCE OR LENGTHS GIVEN.
MAXIMUM 25% MORE THAN THE DISTANCES OR LENGTHS GIVEN.
SPACING OF DELINEATING DEVICES:
MAXIMUM 10% MORE THAN THE SPACING GIVEN.
NO MINIMUM.
AGTTM PART 6 SECTION 6.8.

DOCUMENTATION
ON-SITE VARIATIONS MUST BE APPROVED BY THE TRAFFIC MANAGEMENT SUPERVISOR, THAN AN ON-SITE VARIATION MADE AND CHANGES RECORDED IN THE DAILY DAIRY. FOR MORE INFORMATION REFER TO SECTION 9.3 OF THE TMP.

GENERAL NOTES

- A RISK ASSESSMENT MUST BE CARRIED OUT TO DETERMINE THE REQUIREMENTS OF AFTERCARE.
- ALL SIGN LOCATIONS ARE TO BE CHECKED ON SITE PRIOR TO SETOUT AND POSITIONS ADJUSTED AS PER THE 'TOLERANCES'.
- ALL CONTRADICTORY SIGNS TO BE COVERED BY SUITABLY OPAQUE MATERIAL.
- FOR BOX EDGED SIGN ALTERNATIVES, CONSULT AWTM PRIOR TO IMPLEMENTATION.
- MAXIMUM LENGTH OF 40KM/H SPEED ZONE MUST BE 500M.
- REFER TO SECTION 4.1.8 OF THE TMP FOR THE MANDATORY USE OF SPEED FEEDBACK SIGNAGE.

PEDESTRIAN MANAGEMENT

- 'PEDESTRIAN WATCH YOUR STEP' SIGN TO BE INSTALLED ON EACH APPROACH WHERE WORKS MAY ENCROACH ONTO OR ADJACENT TO EXISTING FOOTPATH FACILITIES.
- TM PERSONNEL TO MONITOR AND ESCORT PEDESTRIANS THROUGH THE WORK AREA AS REQUIRED.
- PEDESTRIANS MAY BE HELD ON EITHER END OF THE WORKSITE UNTIL IT IS SAFE TO PASS AS REQUIRED.

RECOMMENDED CONE SPACING
AGTTM PART 3 - TABLE 5.3
ALL PURPOSES:
(≤ 50KM/H): 4M
PROTECTING FRESHLY PAINTED LINES:
(≤ 70KM/H): 24M
CENTRELINE ON APPROACH TO TC POSITION: 4M
TAPER AT TRAFFIC CONTROL STATION: 4M

RECOMMENDED LANE WIDTHS
MAIN ROADS WA CoP SECTION 6.7 - TABLE 9
SHUTTLE FLOW WITH CONTROL: 3.2M

TRAFFIC CONTROL PROCEDURES
REFER TO TMP SECTION 4.1.7 PORTABLE TRAFFIC CONTROL DEVICES FOR MORE DETAILS

MANUAL TRAFFIC CONTROL

5. ACCREDITED TRAFFIC CONTROLLER (MMS-ADV-47, MMS-ADV-27, MMS-ADV-82, MMS-ADV-10)

6. PORTABLE TRAFFIC CONTROL DEVICE (PTCD) (MMS-ADV-79, MMS-ADV-27, MMS-ADV-82, MMS-ADV-10)

7. PORTABOOM (MMS-ADV-48, MMS-ADV-27, R6-6)

8. TEMPORARY TRAFFIC SIGNAL (MMS-ADV-48, MMS-ADV-27, MMS-ADV-10)

SHADOW VEHICLE INSET
SHADOW VEHICLE MAY BE DISPENSED WITH UNDER A RISK ASSESSMENT BY AN RTM AS PART OF THE TM ADVISE. IN THE ABSENCE OF THE SHADOW VEHICLE A LOOKOUT PERSON IS REQUIRED. REFER TO SECTION 4.5 OF THE TMP FOR MORE DETAILS.

SHADOW VEHICLE
FLASHING ARROW
SHADOW VEHICLE
20-40M BUFFER
WORK SITE

FLASHING ARROWBOARD ON TMA
FLASHING ARROW
VARIABLE MESSAGE BOARD DISPLAY 1
VARIABLE MESSAGE BOARD DISPLAY 2
TEMPORARY SPEED ZONE
REFER TO SECTION 4.5.1 OF THE TMP FOR TMA REQUIREMENTS

TABLES

TAPER LENGTHS
AGTTM PART 3 - TABLE 5.7

SPEED LIMIT (KM/H)	TRAFFIC CONTROL TAPER (M)
45 OR LESS	15
46 TO 55	15
56 TO 65	30
66 TO 75*	
76 TO 85*	
86 TO 95*	
96 TO 105*	
GREATER THAN 105*	N/A

*TAPER LENGTHS ARE BASED ON A:
• 3.5M WIDTH OF THE LANE TO BE CLOSED
• LATERAL SHIFT TAPER LENGTH EQUAL TO 1.0M/S
• MEDIAN SPEED FOR EACH RANGE (I.E 76 - 85 = 80KM/H)

SIGN SPACING
AGTTM PART 3 - TABLE 2.2

SPEED LIMIT (KM/H)	DISTANCE ('D')
55 OR LESS	15
56 TO 65	45
GREATER THAN 65	EQUAL TO SPEED OF TRAFFIC IN KM/H

MAXIMUM LENGTH OF SHUTTLE FLOW
MAIN ROADS WA CoP SECTION 6.8.6 - TABLE 15

VOLUMES (BOTH DIRECTION) (VPH)	LENGTH (BETWEEN TCS) (M)
RESIDENTIAL STREET	60
701 - 800	70
601 - 700	100
501 - 600	150
401 - 500	250
351 - 400	400
301 - 350	600
251 - 300	800
201 - 250	1200
151 - 200	1600
≤ 150	2200

LEGEND

- EXISTING ROAD
- PROPOSED CONES
- WORKSITE

mainroads WESTERN AUSTRALIA

METROPOLITAN REGIONS TRAFFIC MANAGEMENT BRANCH
WATERLOO CRESCENT
TELEPHONE (08) 138 138
EAST PERTH 6004

DATE OF DRAWING 2025 JULY
SCALE -

LOCAL GOVERNMENT AUTHORITY -
POSTED SPEED 50-110KM/H

ROAD AUTHORITY MAIN ROADS WA
WORKSITE SPEED 40KM/H

CHECKED BY TYLER HARTLEY
SIGNATURE Tyler Hartley

ACCREDITATION RTM-0066
SIGNATURE Michael Reed

DESIGNED BY MICHAEL REED
ACCREDITATION AWTM-23-11536-02
SIGNATURE Michael Reed

GENERIC TRAFFIC GUIDANCE SCHEME REVERSIBLE FLOW SETUPS SINGLE LANE ROAD WITHOUT EoQ WORKSITE WITHIN 1.2M

DRAWING NO 0922-01531-RF-046
REVISION 6