


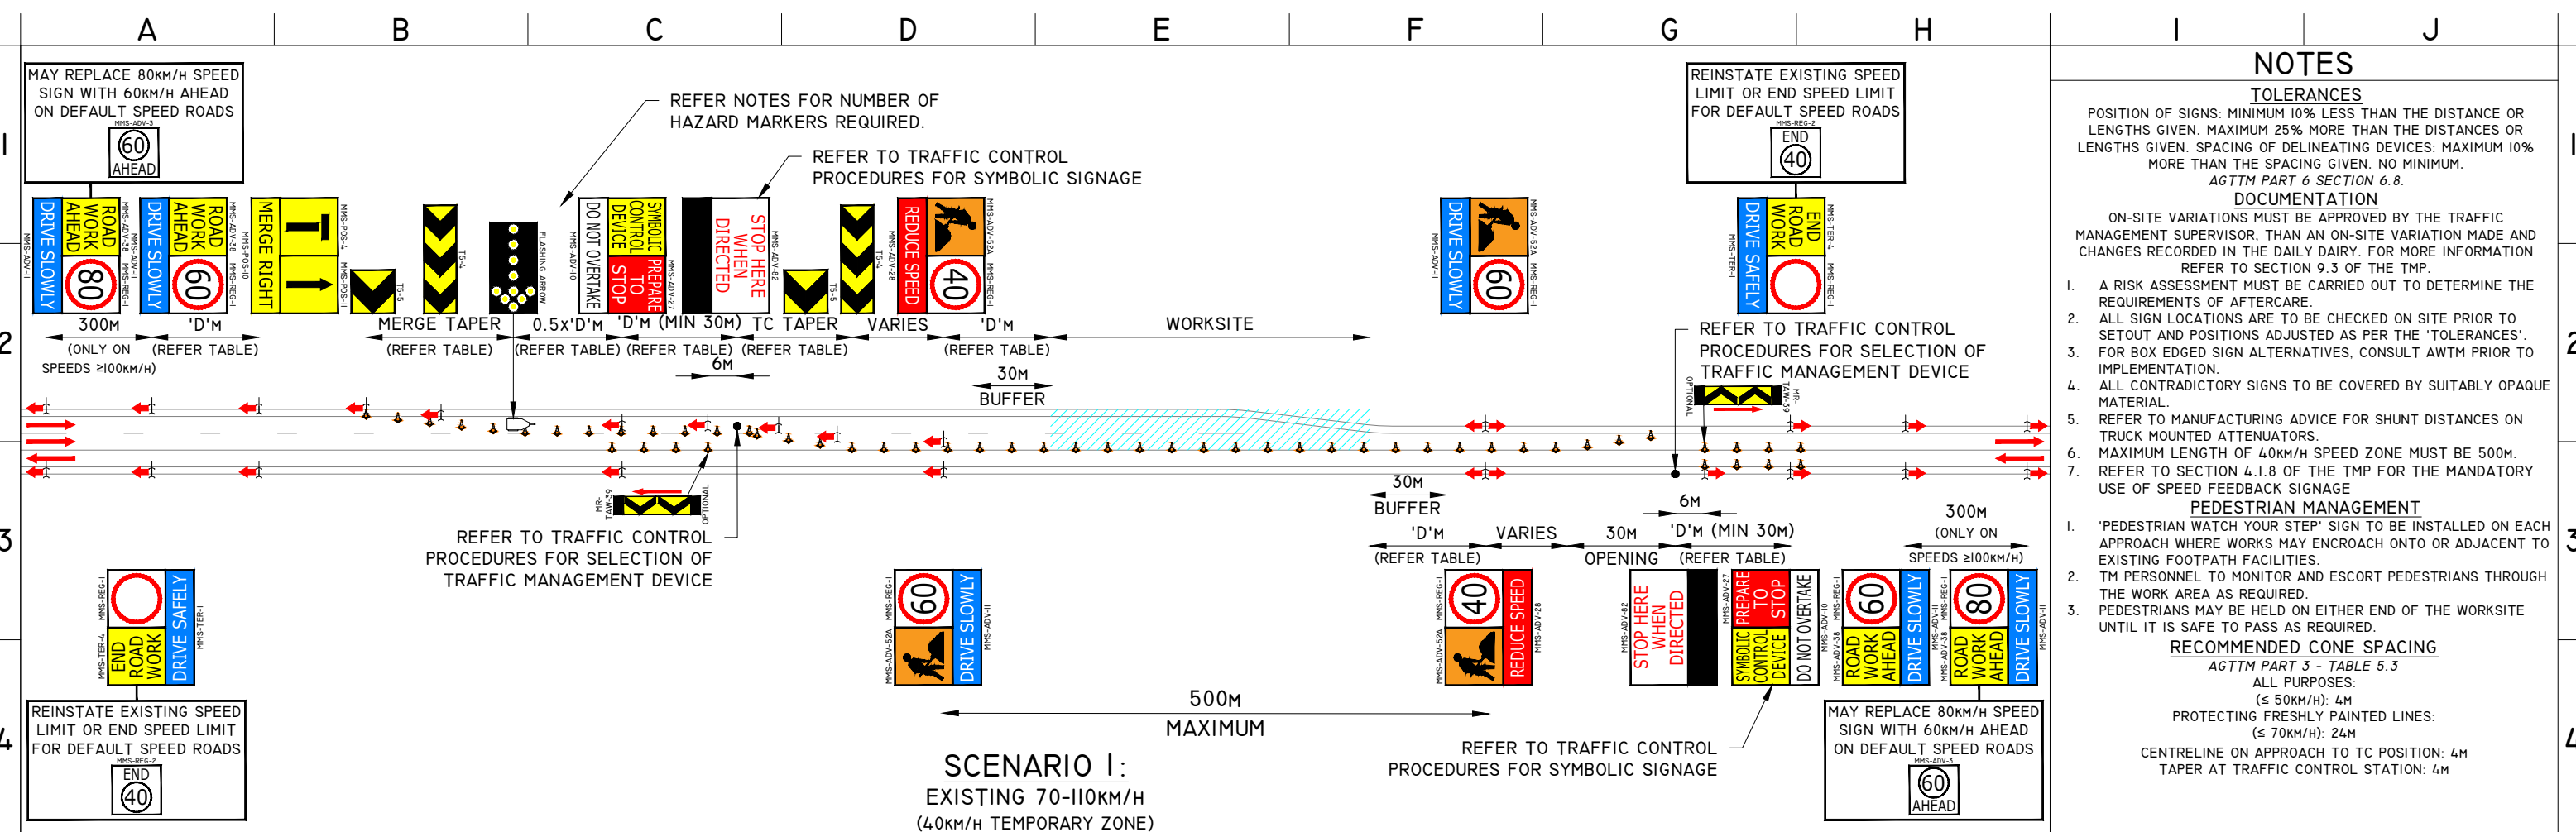

TRAFFIC CONTROL PROCEDURES

REFER TO TMP SECTION 4.1.7 PORTABLE TRAFFIC CONTROL DEVICES FOR MORE DETAILS

MANUAL TRAFFIC CONTROL

ACCREDITED TRAFFIC CONTROLLER

PORTABLE TRAFFIC CONTROL DEVICE (PTCD)

PORTABOOM

TEMPORARY TRAFFIC SIGNAL

SHADOW VEHICLE INSET

SHADOW VEHICLE MAY BE DISPENSED WITH UNDER A RISK ASSESSMENT BY AN RTM AS PART OF THE TM ADVICE. IN THE ABSENCE OF THE SHADOW VEHICLE A LOOKOUT PERSON IS REQUIRED. REFER TO SECTION 4.5 OF THE TMP FOR MORE DETAILS.

SHADOW VEHICLE

FLASHING ARROWBOARD ON TMA

TEMPORARY SPEED ZONE

REFER TO SECTION 4.5.1 OF THE TMP FOR TMA REQUIREMENTS

TABLES

SIGN SPACING		TAPER LENGTHS		
AGTTM PART 3 - TABLE 2.2		AGTTM PART 3 - TABLE 5.7		
SPEED LIMIT (km/h)	DISTANCE ('D') (m)	SPEED LIMIT (km/h)	TRAFFIC CONTROL TAPER (m)	MERGE TAPER (m)
55 OR LESS	15	45 OR LESS	15	15
56 TO 65	45	46 TO 55	15	30
GREATER THAN 65	EQUAL TO SPEED OF TRAFFIC IN km/h	56 TO 65	30	60
MAXIMUM LENGTH OF SHUTTLE FLOW MAIN ROADS WA CoP SECTION 6.8.6 - TABLE 15		66 TO 75*	N/A	115
		76 TO 85*		130
		86 TO 95*		145
		96 TO 105*		160
		GREATER THAN 105*		180
VOLUMES (BOTH DIRECTION) (VPH)		*TAPER LENGTHS ARE BASED ON A: 3.5m WIDTH OF THE LANE TO BE CLOSED - LATERAL SHIFT TAPER LENGTH EQUAL TO 1.0m/s - MERGE TAPER LENGTH EQUAL TO 0.6m/s		
RESIDENTIAL STREET		MEDIAN SPEED FOR EACH RANGE (I.E 76 - 85 = 80km/h)		
701 - 800	70	TEMPORARY HAZARD MARKERS		
601 - 700	100	AGTTM PART 3 - 5.4.2 PAGE 65		
501 - 600	150	A CONTINUOUS LINE OF T5-4 HAZARD MARKERS MUST BE MADE USING THE FOLLOWING RECOMMENDED NUMBERS.		
401 - 500	250	NUMBER OF SHIFT MARKERS		
351 - 400	400	LENGTH OF TAPER		
301 - 350	600	2		
251 - 300	800	4		
201 - 250	1200	6		
151 - 200	1600	8		
≤ 150	2200	EVERY 20M		
RECOMMENDED LANE WIDTHS		WITHIN A CLOSED LANE		
MRWA CoP SECTION 6.7 - TABLE 7		T5-4		
RECOMMENDED LANE WIDTHS:				
≤ 60km/h: 3.2m				
61 - 80km/h: 3.5m				
MINIMUM LANE WIDTHS:				
≤ 60km/h: 3.0m				
61 - 80km/h: 3.2m				
SHUTTLE FLOW WITH CONTROL: 3.2m				