



SCENARIO 1:

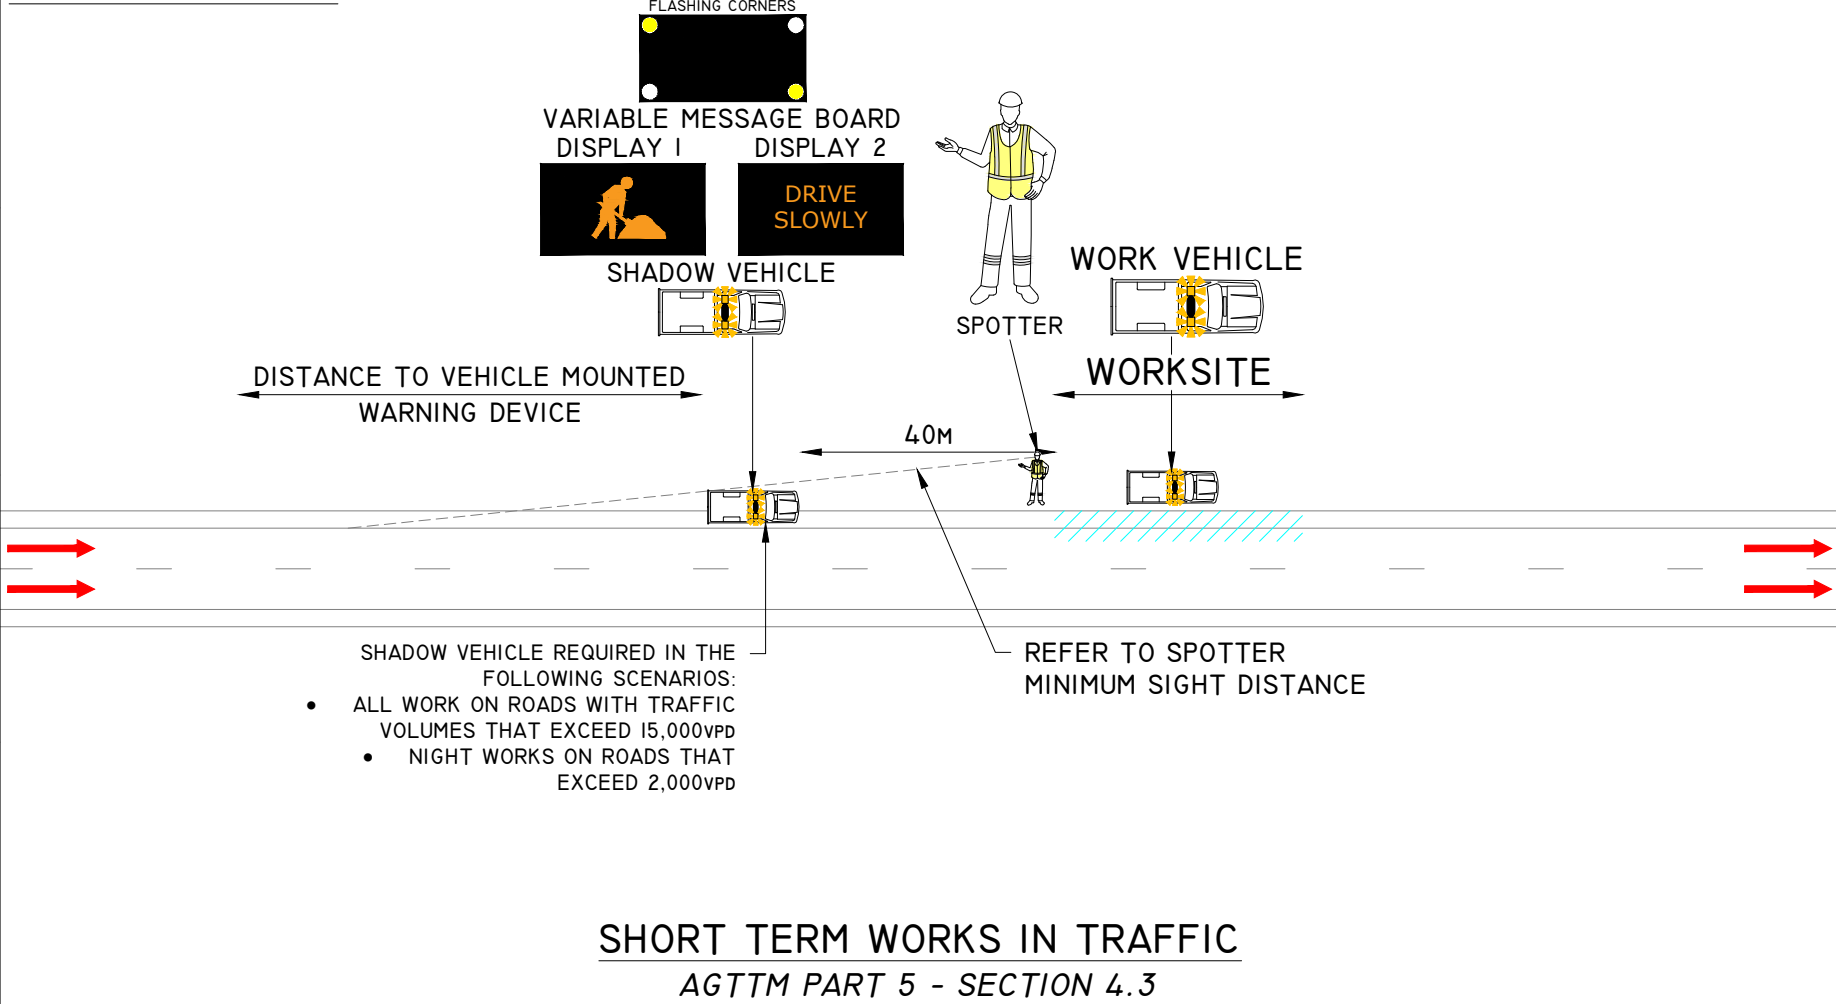

SCENARIO 2:

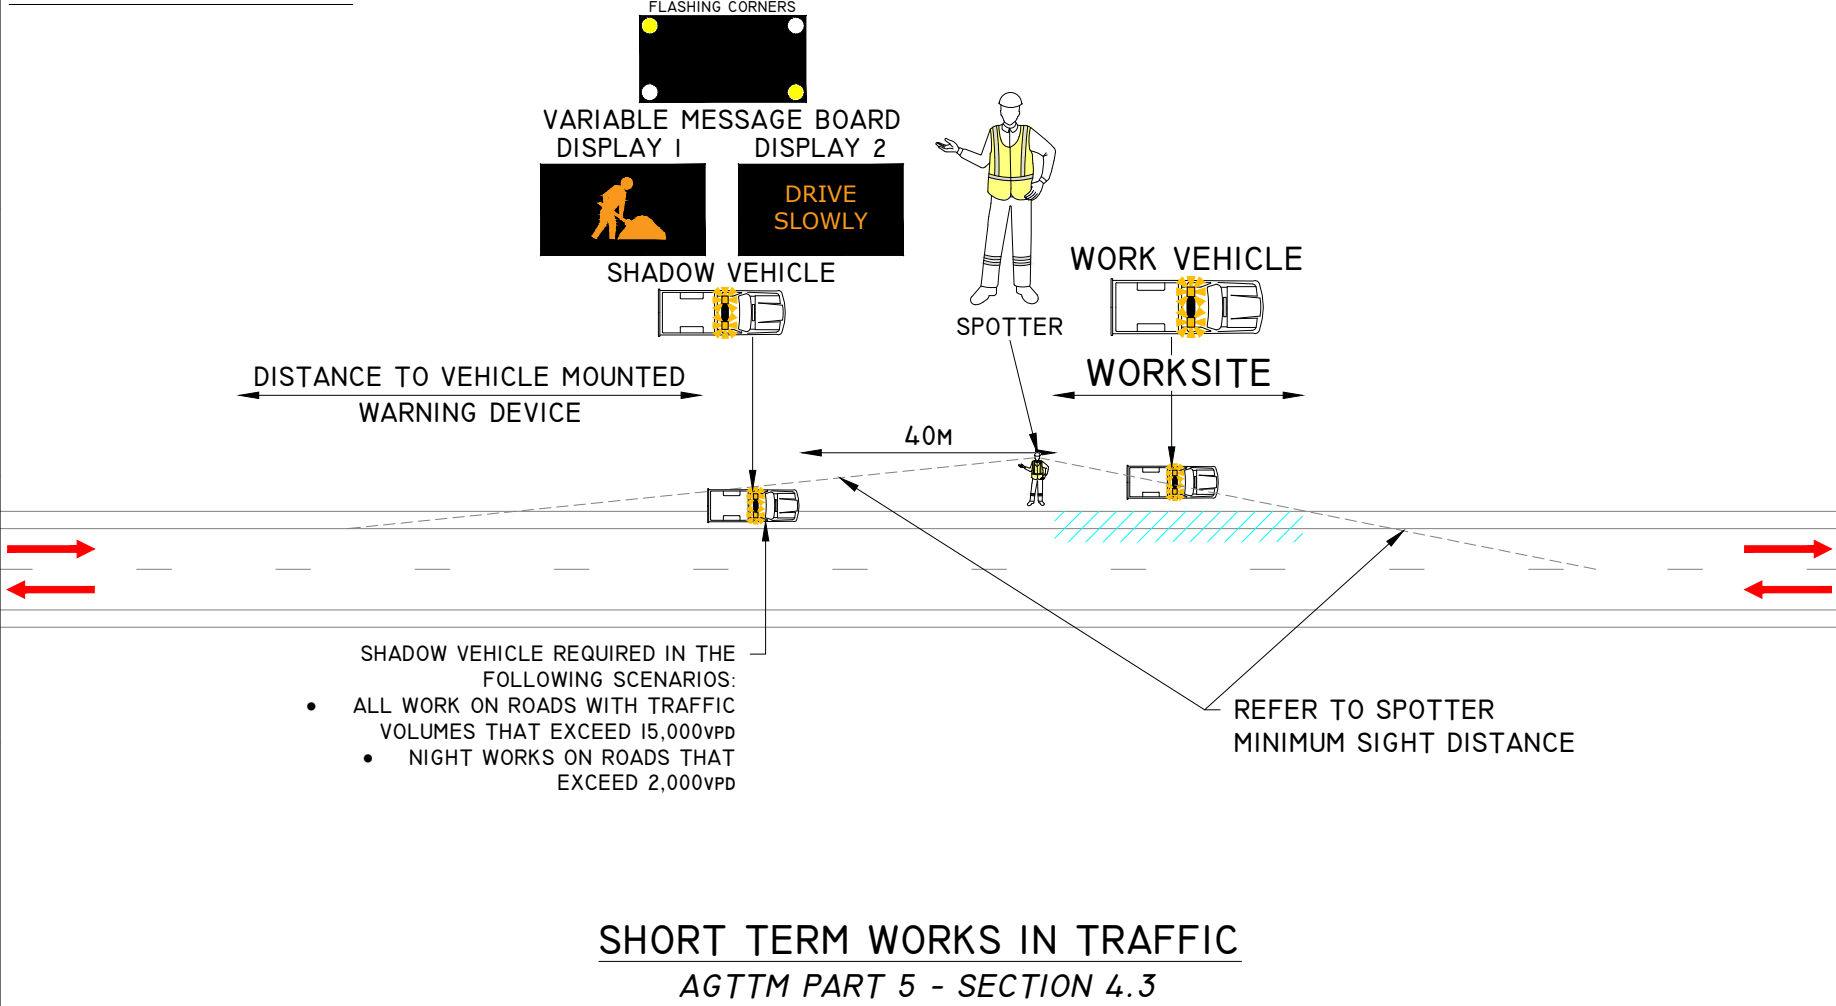

SCENARIO 1:
MULTI-LANE ROAD

- WORKS ARE PARTIALLY IN ONE LANE OF THE MULTI-LANE ROAD AND ALL LANES REMAIN OPEN TO TRAFFIC.
- WHERE THE LANE WIDTH IS GREATER THAN 4.5m AND THE WORK AREA IS IN THE LANE BUT IS MORE THAN 1.2m FROM THE REMAINING TRAFFIC FLOW.

SCENARIO 2:
TWO-WAY CARRIAGEWAY

- WHERE THE LANE WIDTH IS GREATER THAN 4.5m AND THE WORK AREA IS IN THE LANE BUT IS MORE THAN 1.2m FROM THE REMAINING TRAFFIC FLOW.
- WHERE THE WORKS ARE ON A ROAD WITH PARKED VEHICLES ADJACENT TO THE KERB AND THE WORKER IS EFFECTIVELY MORE THAN 1.2m FROM THE NEAREST LINE OF MOVING VEHICLES.

NOTES

- VEHICLE MUST BE EQUIPPED WITH A VEHICLE MOUNTED WARNING DEVICE.
- THE VEHICLE MOUNTED WARNING DEVICE SHALL BE MOUNTED AS HIGH AS PRACTICABLE AND NOT BE OBSCURED, E.G BY OVERHANGING VEGETATION OR A RAISED TRUCK BODY.
- ON HIGH SPEED / VOLUME ROADS, SHADOW VEHICLE MUST BE REPLACED WITH A TMA. A TMA MAY BE USED IN ALL OTHER CIRCUMSTANCE SUBJECT TO A RISK ASSESSMENT.
- THE FOLLOWING MUST BE ADHERED FOR WORKS IN TRAFFIC:
WITHIN 1.2m OR PARTIALLY WITHIN A LANE:
 - WORKS TAKE 5 MINUTES OR LESS.
 - A SPOTTER IS AVAILABLE TO WARN WORKERS ON FOOT TO VACATE THE ROAD WAY BEFORE THE ARRIVAL OF APPROACHING TRAFFIC WHICH IS NOT ALTERING PATH TO PASS THE WORKSITE.
 - THERE IS A MINIMUM SIGHT DISTANCE FROM APPROACHING ROAD USERS TO THE VEHICLE MOUNTED WARNING DEVICE.
 - 150m IF THE SPEED IS 60km/h OR LESS.
 - 250m IF THE SPEED IS MORE THAN 60km/h
 - WORKS DO NOT REDUCE THE OVERALL LANE WIDTH TO A CENTRELINE TO LESS THAN 3.5m OR IF THE VOLUME IS LESS THAN 50vpd, LESS THAN 3.3m.
 - WORKS DO NOT REDUCE ANY TRAFFIC LANE WIDTH ADJACENT TO A BARRIER LINE TO LESS THAN THAT NEEDED TO ALLOW VEHICLES TO PROCEED WITHOUT CROSSING THE LINE.BETWEEN 1.2m AND 3m OF TRAFFIC:
 - WORKS TAKE 20 MINUTES OR LESS.
 - A SPOTTER IS AVAILABLE TO WARN WORKERS ON FOOT TO VACATE THE ROAD WAY BEFORE THE ARRIVAL OF APPROACHING TRAFFIC WHICH IS NOT ALTERING PATH TO PASS THE WORKSITE.
 - THERE IS A MINIMUM SIGHT DISTANCE FROM APPROACHING ROAD USERS TO THE VEHICLE MOUNTED WARNING DEVICE.
 - 150m IF THE SPEED IS 60km/h OR LESS.
 - 250m IF THE SPEED IS MORE THAN 60km/h
- IF TWO OR MORE LOCATIONS WITHIN A SPACE OF 2km OR LESS REQUIRE WORK TO BE UNDERTAKEN, THE METHODS OF A FREQUENTLY CHANGING WORK AREA MUST APPLY, REFER TGS-TMC-STLI-005, 006 OR 007.
- PRIOR TO COMMENCEMENT OF WORKS, A RISK ASSESSMENT MUST BE UNDERTAKEN TO ENSURE THE WORKS CAN BE COMPLETED SAFELY. REFER TO THE TMP FOR RISK CONSIDERATIONS PRIOR TO SETUP.
- THE WORKS VEHICLE LOCATION MUST CONSIDER THE IMPACT ON VULNERABLE ROAD USERS AND CYCLISTS. THE WORK VEHICLE MUST BE LOCATED WITHIN 40m OF THE PROPOSED WORKS.
- EQUIPMENT OR MATERIALS BROUGHT TO THE SITE MUST BE UNLOADED FROM THE NON-TRAFFIC SIDE OF A STATIONARY WORK VEHICLE, OR THE REAR OF A STATIONARY WORK VEHICLE WITH A SPOTTER OR SHADOW VEHICLE IN PLACE.
- THE SPOTTER MUST BE WITHIN REASONABLE DISTANCE TO THE WORK LOCATION AT ALL TIMES (WITHIN 40m), TO VIEW AND PROVIDE ADVICE TO THE WORKERS.

DOCUMENTATION

DAILY RECORDS OF THE SITE LAYOUT INCLUDING DEVICES, SIGHT DISTANCE, RISK ASSESSMENTS, SIGNS OR TGS, MUST BE KEPT IN A DIARY OR IN WORK SHEETS (DAILY DAIRY). ANY SIGNIFICANT DEPARTURES FROM, OR ADDITIONS TO, THE SIGNS AND DEVICES INCLUDED IN THIS DIAGRAM SHOULD BE NOTED AND APPROVED.

TABLES

MINIMUM SIGHT DISTANCE TO VEHICLE MOUNTED WARNING DEVICE - NO SPOTTER

AGTTM PART 5 - TABLE 4.2

SPEED LIMIT (km/h)	DISTANCE (m)
≤45	225
46-55	275
56-65	335
66-75	390
76-85	445
86-95	500
96-110	555
>110	SPOTTER REQUIRED

WORK TASK ≤ 10 SECONDS. WORKER TO FACE ONCOMING TRAFFIC.

SPOTTER MINIMUM SIGHT DISTANCE

AGTTM PART 5 - TABLE 4.6

SPEED LIMIT (km/h)	DISTANCE (m)
≤45	80
46-55	100
56-65	120
66-75	140
76-85	160
86-95	180
96-105	200
>106	220

DISTANCES ARE FOR WORKER ON FOOT TO VACATE ROADWAY AT A MAX TRAVEL DISTANCE OF 3.5m

LEGEND

- EXISTING ROAD
- WORK ZONE



METROPOLITAN REGIONS
TRAFFIC MANAGEMENT BRANCH

WATERLOO CRESCENT
TELEPHONE (08) 138 138

EAST PERTH 6004

DATE OF DRAWING 2025 JULY	SCALE -
LOCAL GOVERNMENT AUTHORITY -	POSTED SPEED -
ROAD AUTHORITY MRWA	WORKSITE SPEED -
CHECKED BY TYLER HARTLEY	SIGNATURE <i>Tyler Hartley</i>
ACCREDITATION RTM-0066	
DESIGNED BY MICHAEL REED	SIGNATURE <i>Michael Reed</i>
ACCREDITATION AWTM-23-11536-02	

GENERIC TRAFFIC GUIDANCE SCHEME
SHORT TERM LOW IMPACT
SHORT TERM WORKS IN TRAFFIC
IN LIVE TRAFFIC LANE

DRAWING NO 0922-01531-STLI-004	REVISION 6
-----------------------------------	---------------