



SCENARIO 1:

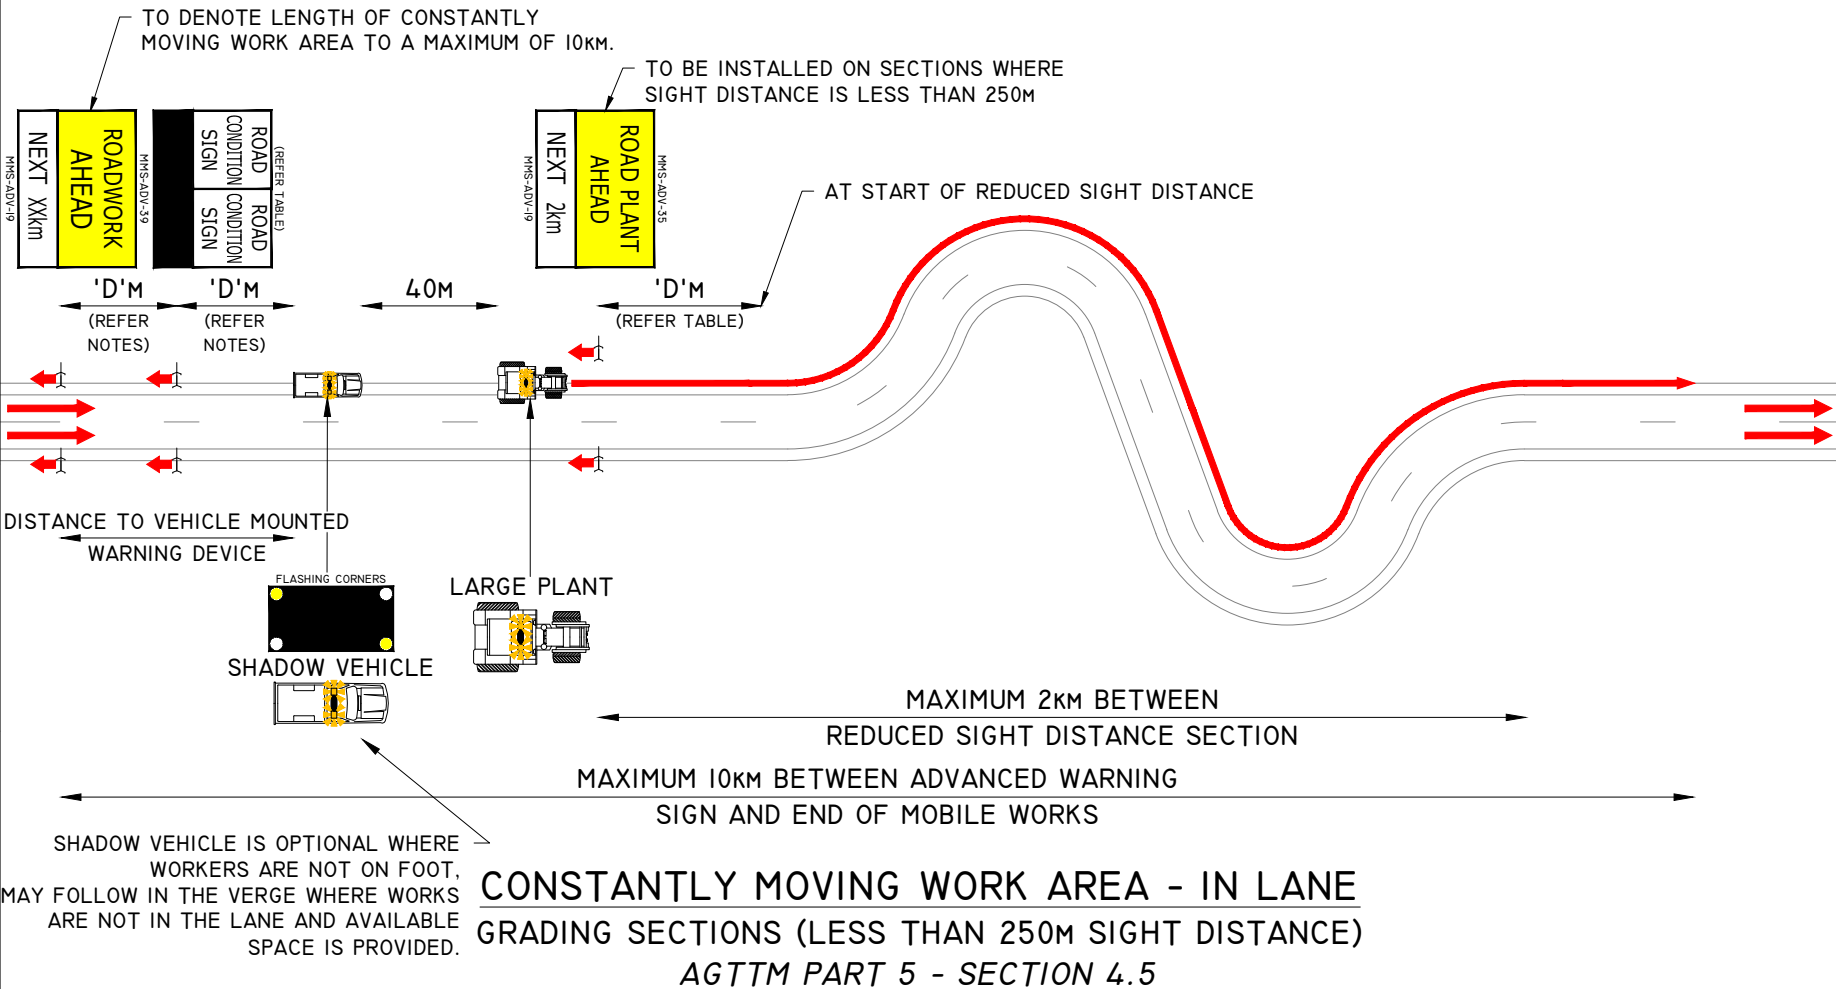

SCENARIO 2:

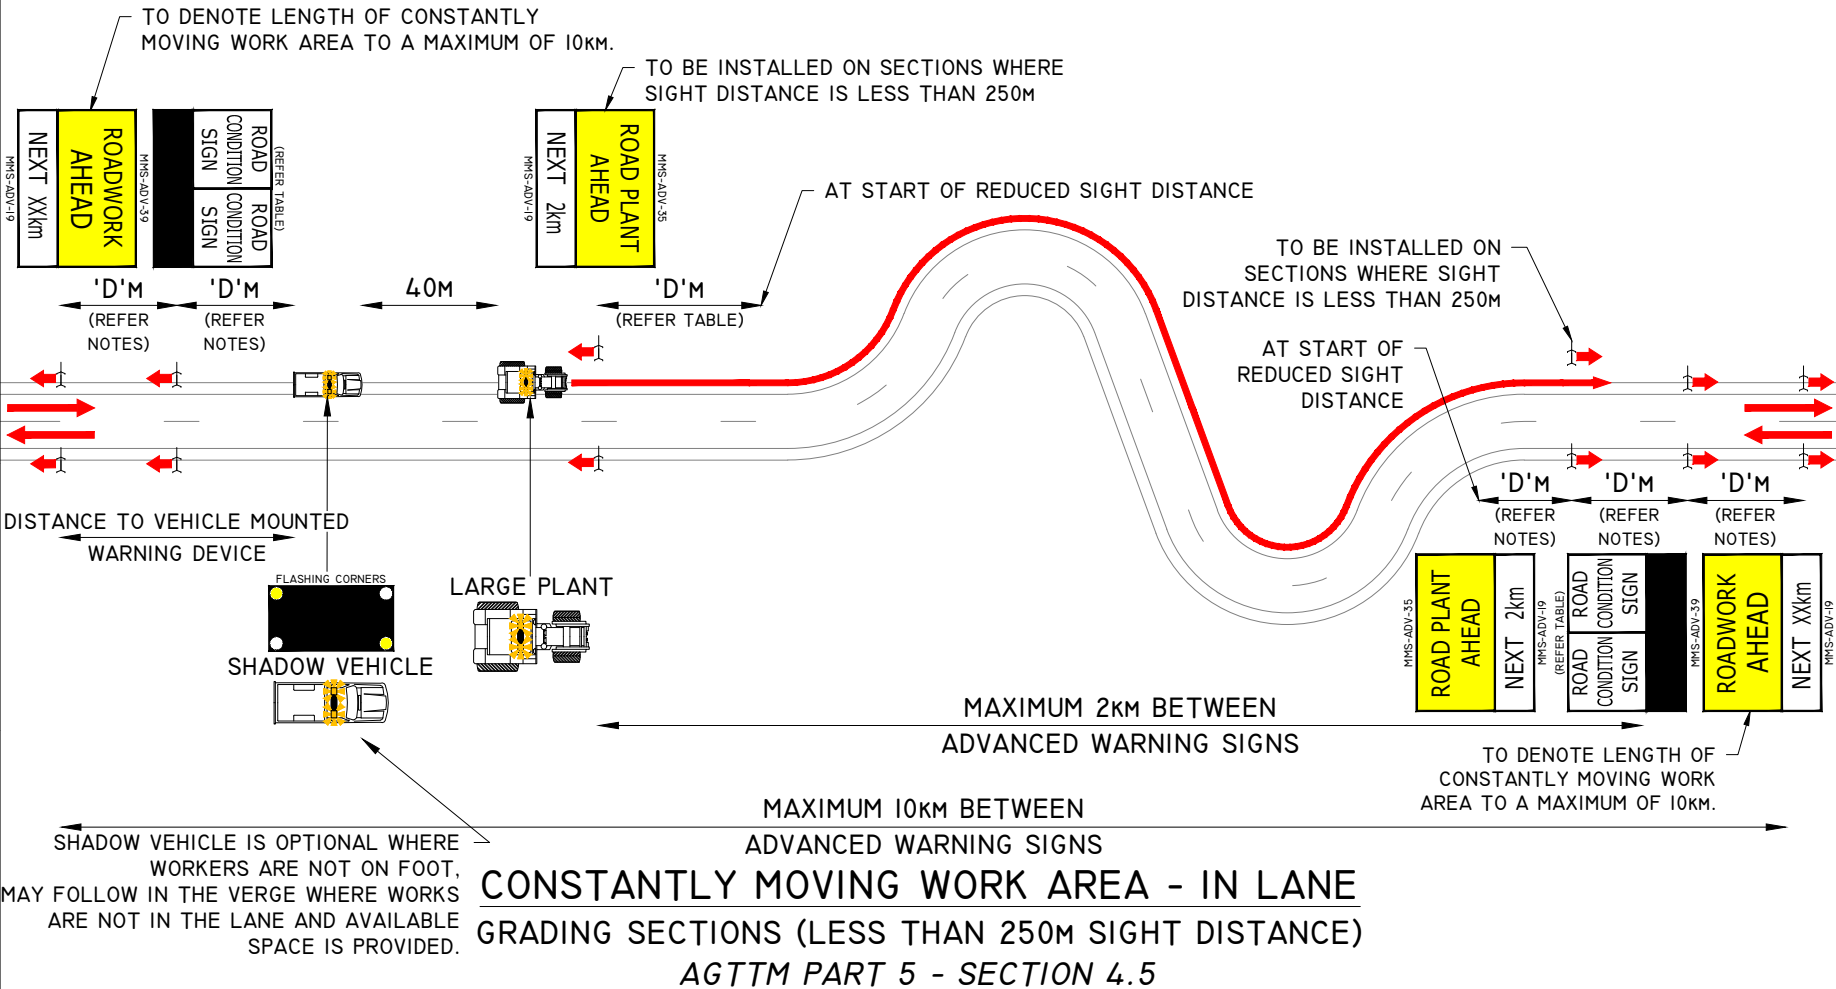

SCENARIO 1: MULTI-LANE ROAD SCENARIO 2: TWO-WAY CARRIAGEWAY NOTES

- ON HIGH SPEED / VOLUME ROADS, SHADOW VEHICLE MUST BE REPLACED WITH A TMA. A TMA MAY BE USED IN ALL OTHER CIRCUMSTANCE SUBJECT TO A RISK ASSESSMENT.
- VEHICLES MUST BE EQUIPPED WITH A VEHICLE MOUNTED WARNING DEVICE.
- THE VEHICLE MOUNTED WARNING DEVICE SHALL BE MOUNTED AS HIGH AS PRACTICABLE AND NOT BE OBSCURED, E.G BY OVERHANGING VEGETATION OR A RAISED TRUCK BODY.
- AS THE WORKS PROGRESS ALONG THE ROAD, THE SHADOW VEHICLE MOVES WITH THE WORK VEHICLE.
- THE FOLLOWING MUST BE ADHERED FOR CONSTANTLY MOVING WORK AREA:
 - THE GRADE AND OTHER WORK VEHICLES ARE WITHIN THE TRAFFIC LANE OR PARTIALLY WITHIN A TRAFFIC LANE.
 - THE WORK AREA MUST BE CONTINUALLY MOVING.
 - TRAFFIC VOLUMES ARE 3,000vpd OR LESS FOR ANY SPEED ENVIRONMENT.
 - WORKS MAY BE UNDERTAKEN IN BOUNDS OF UP TO 10km.
 - THE PROCEDURES IN NOTE 10 BELOW MUST BE FOLLOWED.
- FOR INSPECTION SCENARIOS REFER TO TGS-TMC-STLI-009. FOR SECTIONS OF ROAD WHERE THE SIGHT DISTANCE CAN BE MAINTAINED, REFER TO TGS-TMC-STLI-010.
- PRIOR TO COMMENCEMENT OF WORKS, A RISK ASSESSMENT MUST BE UNDERTAKEN TO ENSURE THE WORKS CAN BE COMPLETED SAFELY. REFER TO THE TMP FOR RISK CONSIDERATIONS PRIOR TO SETUP.
- THE WORKS AND SHADOW VEHICLE LOCATION MUST CONSIDER THE IMPACT ON VULNERABLE ROAD USERS AND CYCLISTS.
- ADVANCED WARNING SIGNS MAY BE OMITTED FOR A SECTION WHEN:
 - THE SIGHT DISTANCE FOR THE ENTIRE SECTION EXCEEDS 150m WHEN THE SPEED IS 60km/h OR LESS AND A VEHICLE MOUNTED WARNING DEVICE IS DISPLAYED.
 - THE SIGHT DISTANCE FOR THE ENTIRE SECTION EXCEED 250m WHEN THE SPEED IS MORE THAN 60km/h AND A VEHICLE MOUNTED WARNING DEVICE IS DISPLAYED.
- WHERE THE SIGHT DISTANCE FALLS TO LESS THAN 250m:
 - THE WORK MUST BE UNDERTAKEN IN BOUNDS OF NOT MORE THAN 10km SECTIONS. THE ROADWORK AHEAD SIGN IS TO BE DISPLAYED AT EITHER END OF THE WORKSITE.
 - ROAD PLANT AHEAD SIGNS TO BE INSTALLED WHERE THE SIGHT DISTANCE IS REDUCED. WHERE THERE ARE MULTIPLE SECTIONS OF REDUCED VISIBILITY GREATER THAN 2km FROM THE ORIGINAL SIGN, ADDITIONAL ROAD PLANT AHEAD SIGNS MUST BE IMPLEMENTED.
 - IF THERE IS DIFFICULTY TURNING A GRADER AROUND AT THE END OF A 2km SECTION, THE SECTION MAY BE EXTENDED TO THE NEXT AVAILABLE TURNING POINT BUT NOT MORE THAN 6km IN TOTAL LENGTH. WITHIN THE EXTENDED DISTANCE ADVANCED WARNING SIGNS MUST BE REPEATED EVERY 2km.
- A SPOTTER MUST BE USED FOR THE INSTALLATION OF SIGNAGE. REFER TO THE SPOTTER MINIMUM SIGHT DISTANCE TABLES.

DOCUMENTATION

DAILY RECORDS OF THE SITE LAYOUT INCLUDING DEVICES, SIGHT DISTANCE, RISK ASSESSMENTS, SIGNS OR TGS, MUST BE KEPT IN A DIARY OR IN WORK SHEETS (DAILY DAIRY). ANY SIGNIFICANT DEPARTURES FROM, OR ADDITIONS TO, THE SIGNS AND DEVICES INCLUDED IN THIS DIAGRAM SHOULD BE NOTED AND APPROVED.

ROAD CONDITION SIGNS PLACEMENT ON EITHER SIDE OF FRAME

(A) MMS-RC-8 SOFT EDGES			
RIGHT SIDE OF FRAME ONLY		LEFT SIDE OF FRAME ONLY	
(B) MMS-RC-1	(C) MMS-RC-6	(D) MMS-RC-2	(E) MMS-RC-5

TABLES

SIGN SPACING

AGTTM PART 3 - TABLE 2.2

SPEED LIMIT (KM/H)	DISTANCE ('D') (M)
55 OR LESS	15
56 TO 65	45
GREATER THAN 65	EQUAL TO SPEED OF TRAFFIC IN KM/H

MINIMUM SIGHT DISTANCE TO VEHICLE MOUNTED WARNING DEVICE - NO SPOTTER

AGTTM PART 5 - TABLE 4.2

SPEED LIMIT (KM/H)	DISTANCE (M)
≤45	225
46-55	275
56-65	335
66-75	390
76-85	445
86-95	500
96-110	555
>110	SPOTTER REQUIRED

WORK TASK ≤ 10 SECONDS. WORKER TO FACE ONCOMING TRAFFIC.

LEGEND

EXISTING ROAD



METROPOLITAN REGIONS
TRAFFIC MANAGEMENT BRANCH
WATERLOO CRESCENT
TELEPHONE (08) 138 138
EAST PERTH 6004

DATE OF DRAWING 2025 JULY	SCALE -
LOCAL GOVERNMENT AUTHORITY -	POSTED SPEED -
ROAD AUTHORITY MRWA	WORKSITE SPEED -
CHECKED BY TYLER HARTLEY	SIGNATURE
ACCREDITATION RTM-0066	SIGNATURE
DESIGNED BY MICHAEL REED	
ACCREDITATION AWTM-23-11536-02	
GENERIC TRAFFIC GUIDANCE SCHEME SHORT TERM LOW IMPACT CONSTANTLY MOVING WORK AREA IN LIVE TRAFFIC LANE	
DRAWING NO 0922-01531-STLI-011	REVISION 6