



SCENARIO 1:

- NOT TO BE USED ON
FREEWAYS OR HIGH SPEED
/ VOLUME HIGHWAYS

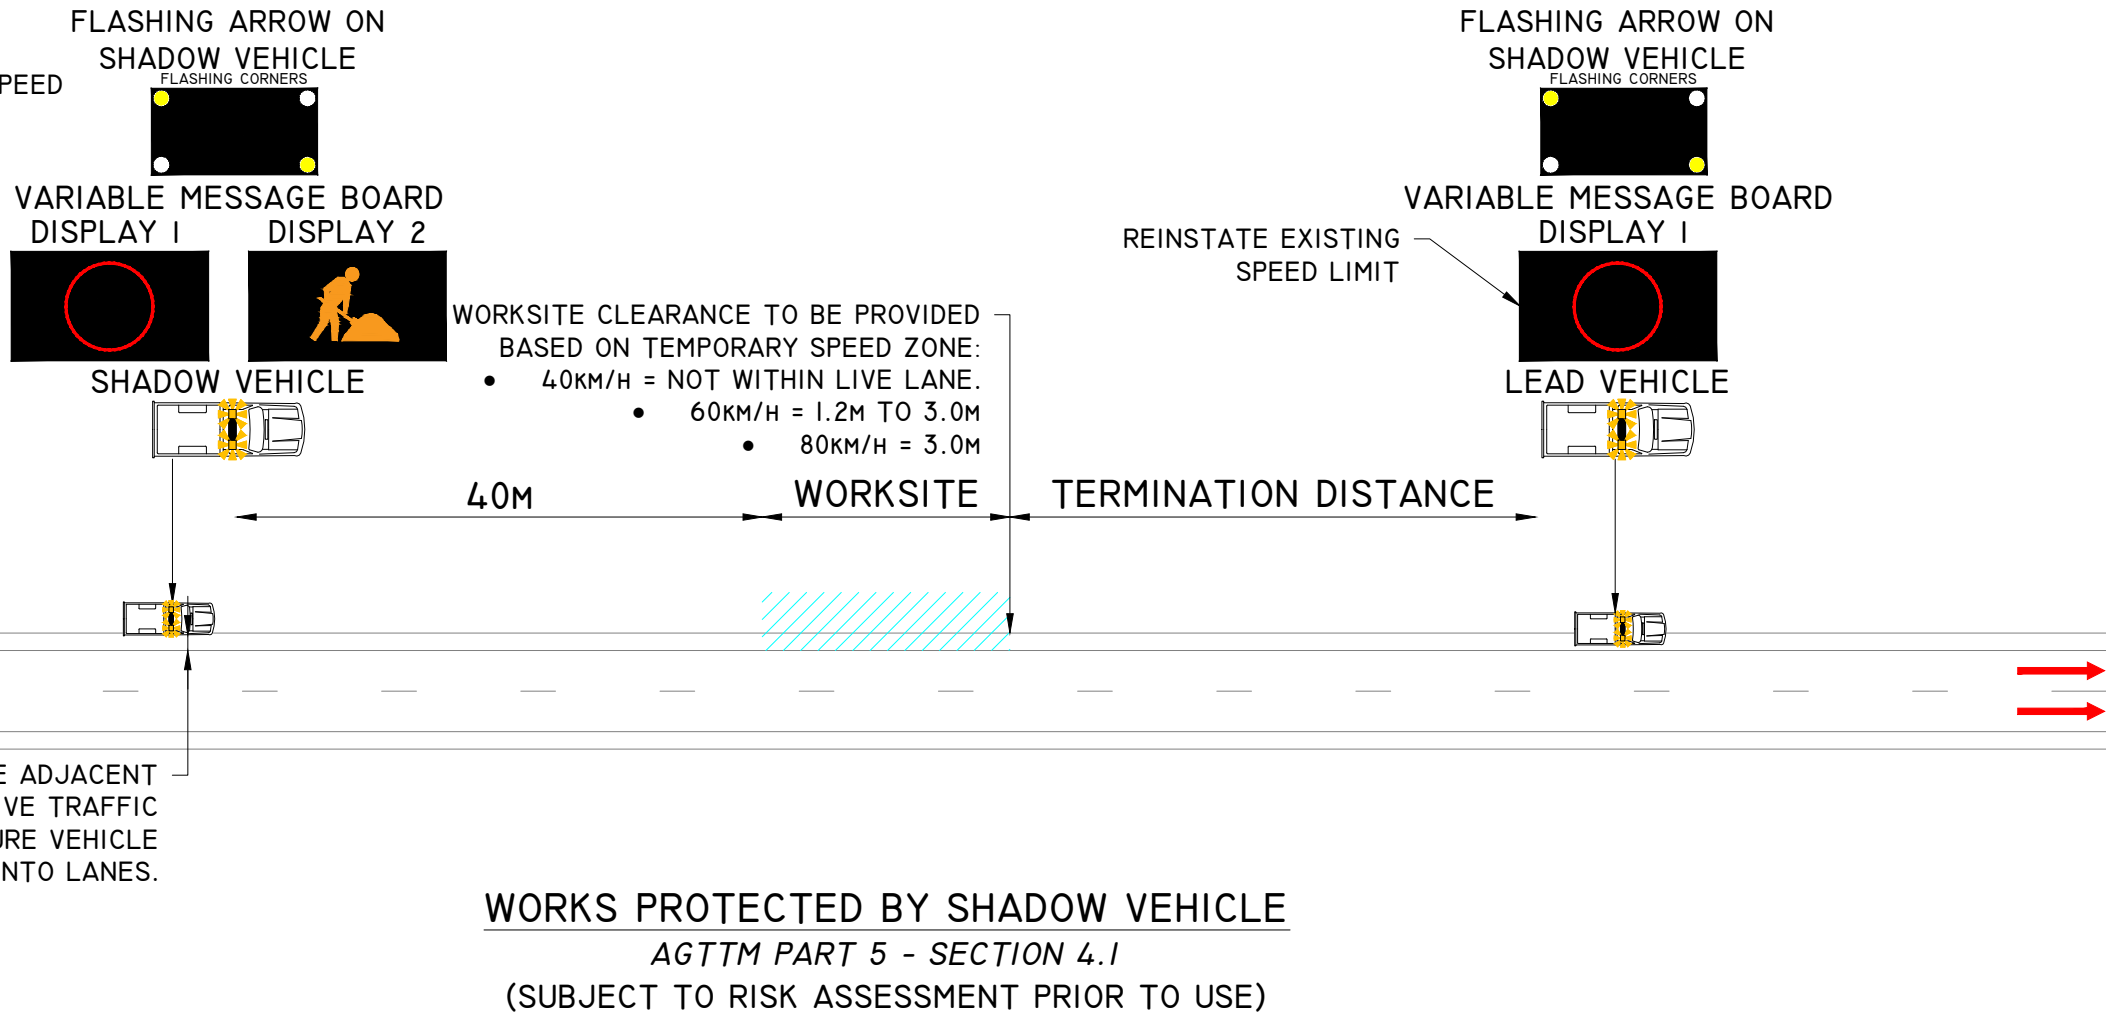

SCENARIO 2:

- NOT TO BE USED ON
FREEWAYS OR HIGH
SPEED / VOLUME
HIGHWAYS

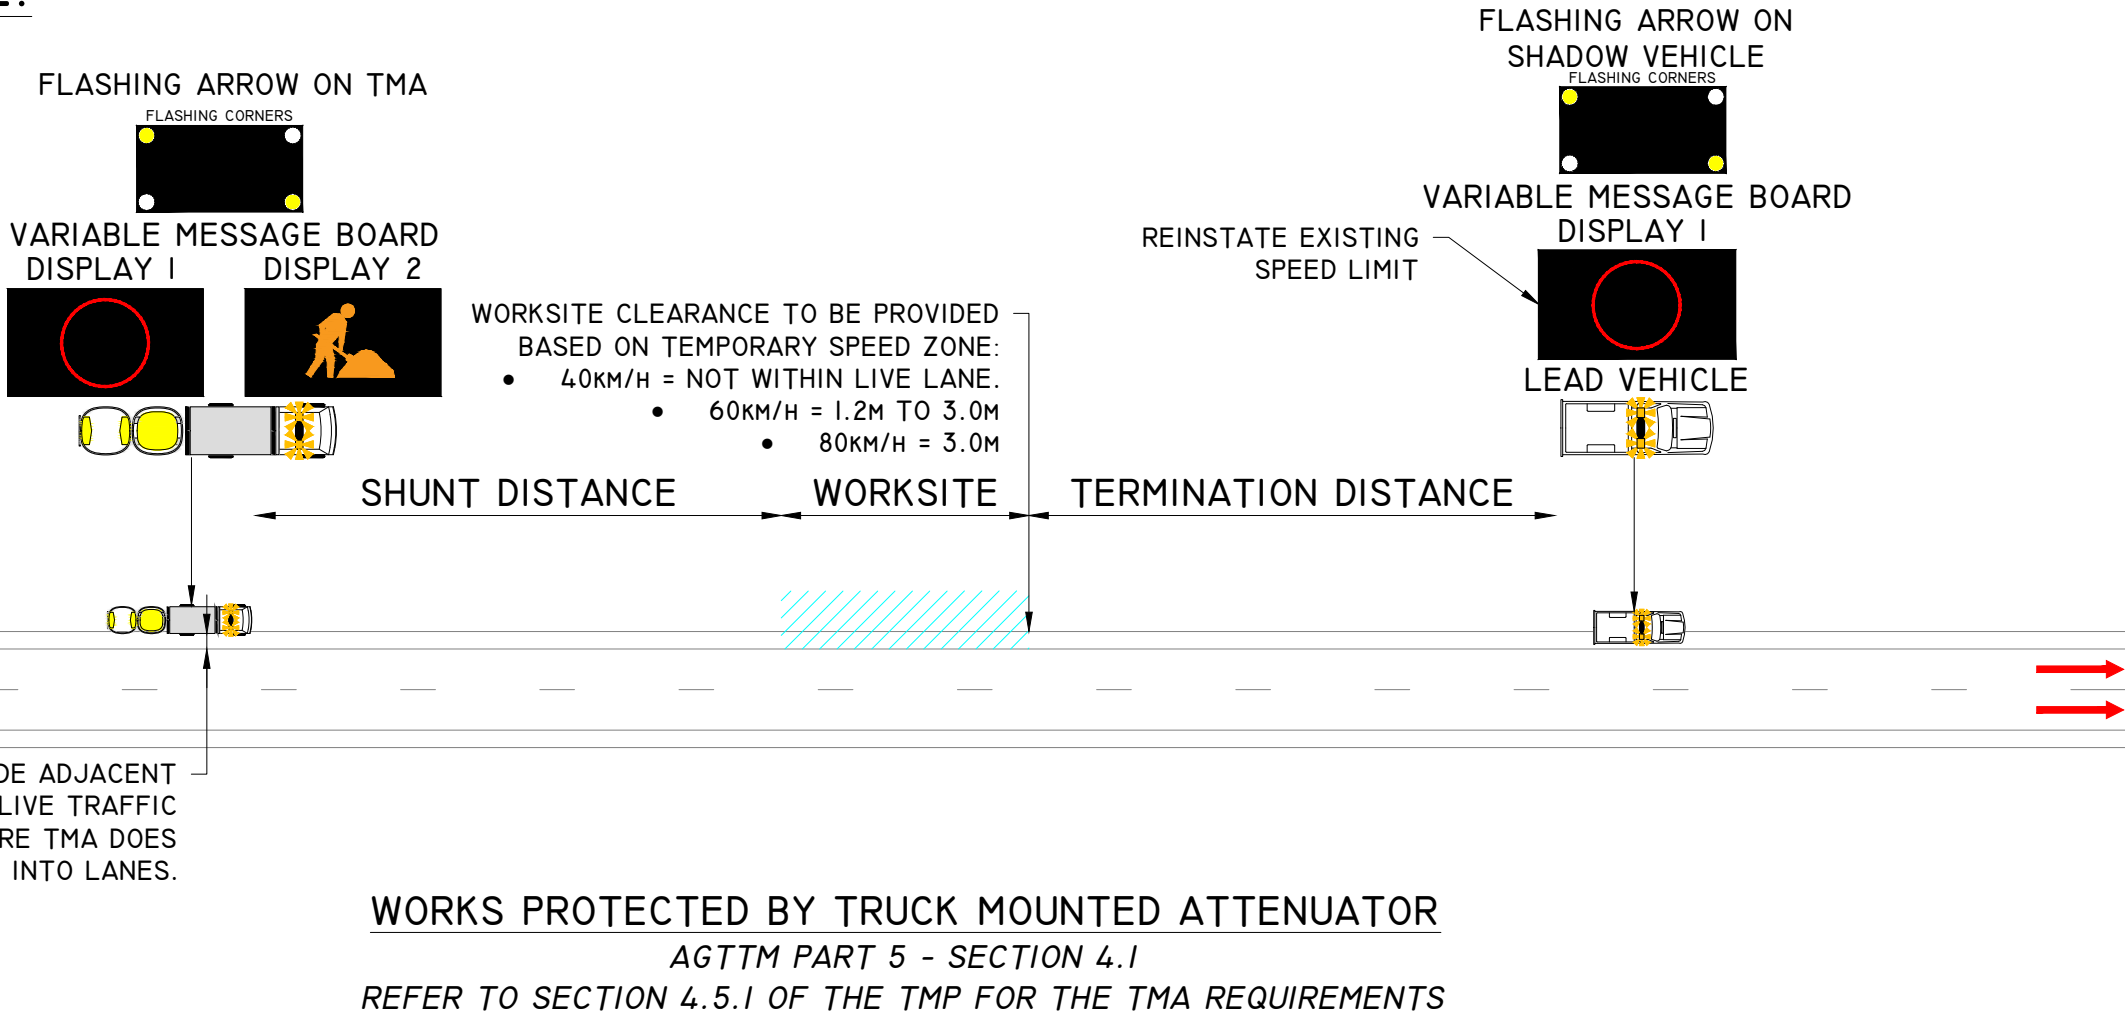

SCENARIO 1:
WORKS PROTECTED BY SHADOW VEHICLE
SCENARIO 2:
WORKS PROTECTED BY TMA
NOTES

- REFER TO THE REQUIREMENTS FOR EACH SCENARIO SET IN TGS-TMC-STLI-028.
- THIS DRAWING MUST BE USED IN CONJUNCTION WITH TGS-TMC-STLI-028.
- AN ON-SITE RISK ASSESSMENT MUST BE PROVIDED FOR THE USE OF TEMPORARY SPEED ZONES ON SHORT TERM LOW IMPACT WORKS AND THE SPEED ZONE SHOULD ONLY BE IMPLEMENTED WHERE REQUIRED.
- THE TEMPORARY SPEED ZONE MUST BE TERMINATED BY THE USE OF A VEHICLE MOUNTED SPEED RESTRICTION SIGN.
- THE SELECTION OF THE TEMPORARY SPEED ZONE MUST BE BASED ON THE PROPOSED RISK ASSESSMENT AND THE CLEARANCE OF WORKERS TO LIVE TRAFFIC LANES.

DOCUMENTATION

DAILY RECORDS OF THE SITE LAYOUT INCLUDING DEVICES, SIGHT DISTANCE, RISK ASSESSMENTS, SIGNS, TGS AND SPEED ZONES, MUST BE KEPT IN A DIARY OR IN WORK SHEETS (DAILY DAIRY). ANY SIGNIFICANT DEPARTURES FROM, OR ADDITIONS TO, THE SIGNS AND DEVICES INCLUDED IN THIS DIAGRAM SHOULD BE NOTED AND APPROVED.

LEGEND

- EXISTING ROAD
- WORK ZONE



METROPOLITAN REGIONS
TRAFFIC MANAGEMENT BRANCH
WATERLOO CRESCENT
TELEPHONE (08) 138 138
EAST PERTH 6004

DATE OF DRAWING 2025 JULY	SCALE -
LOCAL GOVERNMENT AUTHORITY -	POSTED SPEED -
ROAD AUTHORITY MRWA	WORKSITE SPEED -
CHECKED BY TYLER HARTLEY	SIGNATURE <i>Tyler Hartley</i>
ACCREDITATION RTM-0066	
DESIGNED BY MICHAEL REED	SIGNATURE <i>Michael Reed</i>
ACCREDITATION AWTM-23-11536-02	
GENERIC TRAFFIC GUIDANCE SCHEME SHORT TERM LOW IMPACT SPECIALIST VEHICLE TEMPORARY SPEED ZONE	
DRAWING NO 0922-01531-STLI-029	REVISION 6