


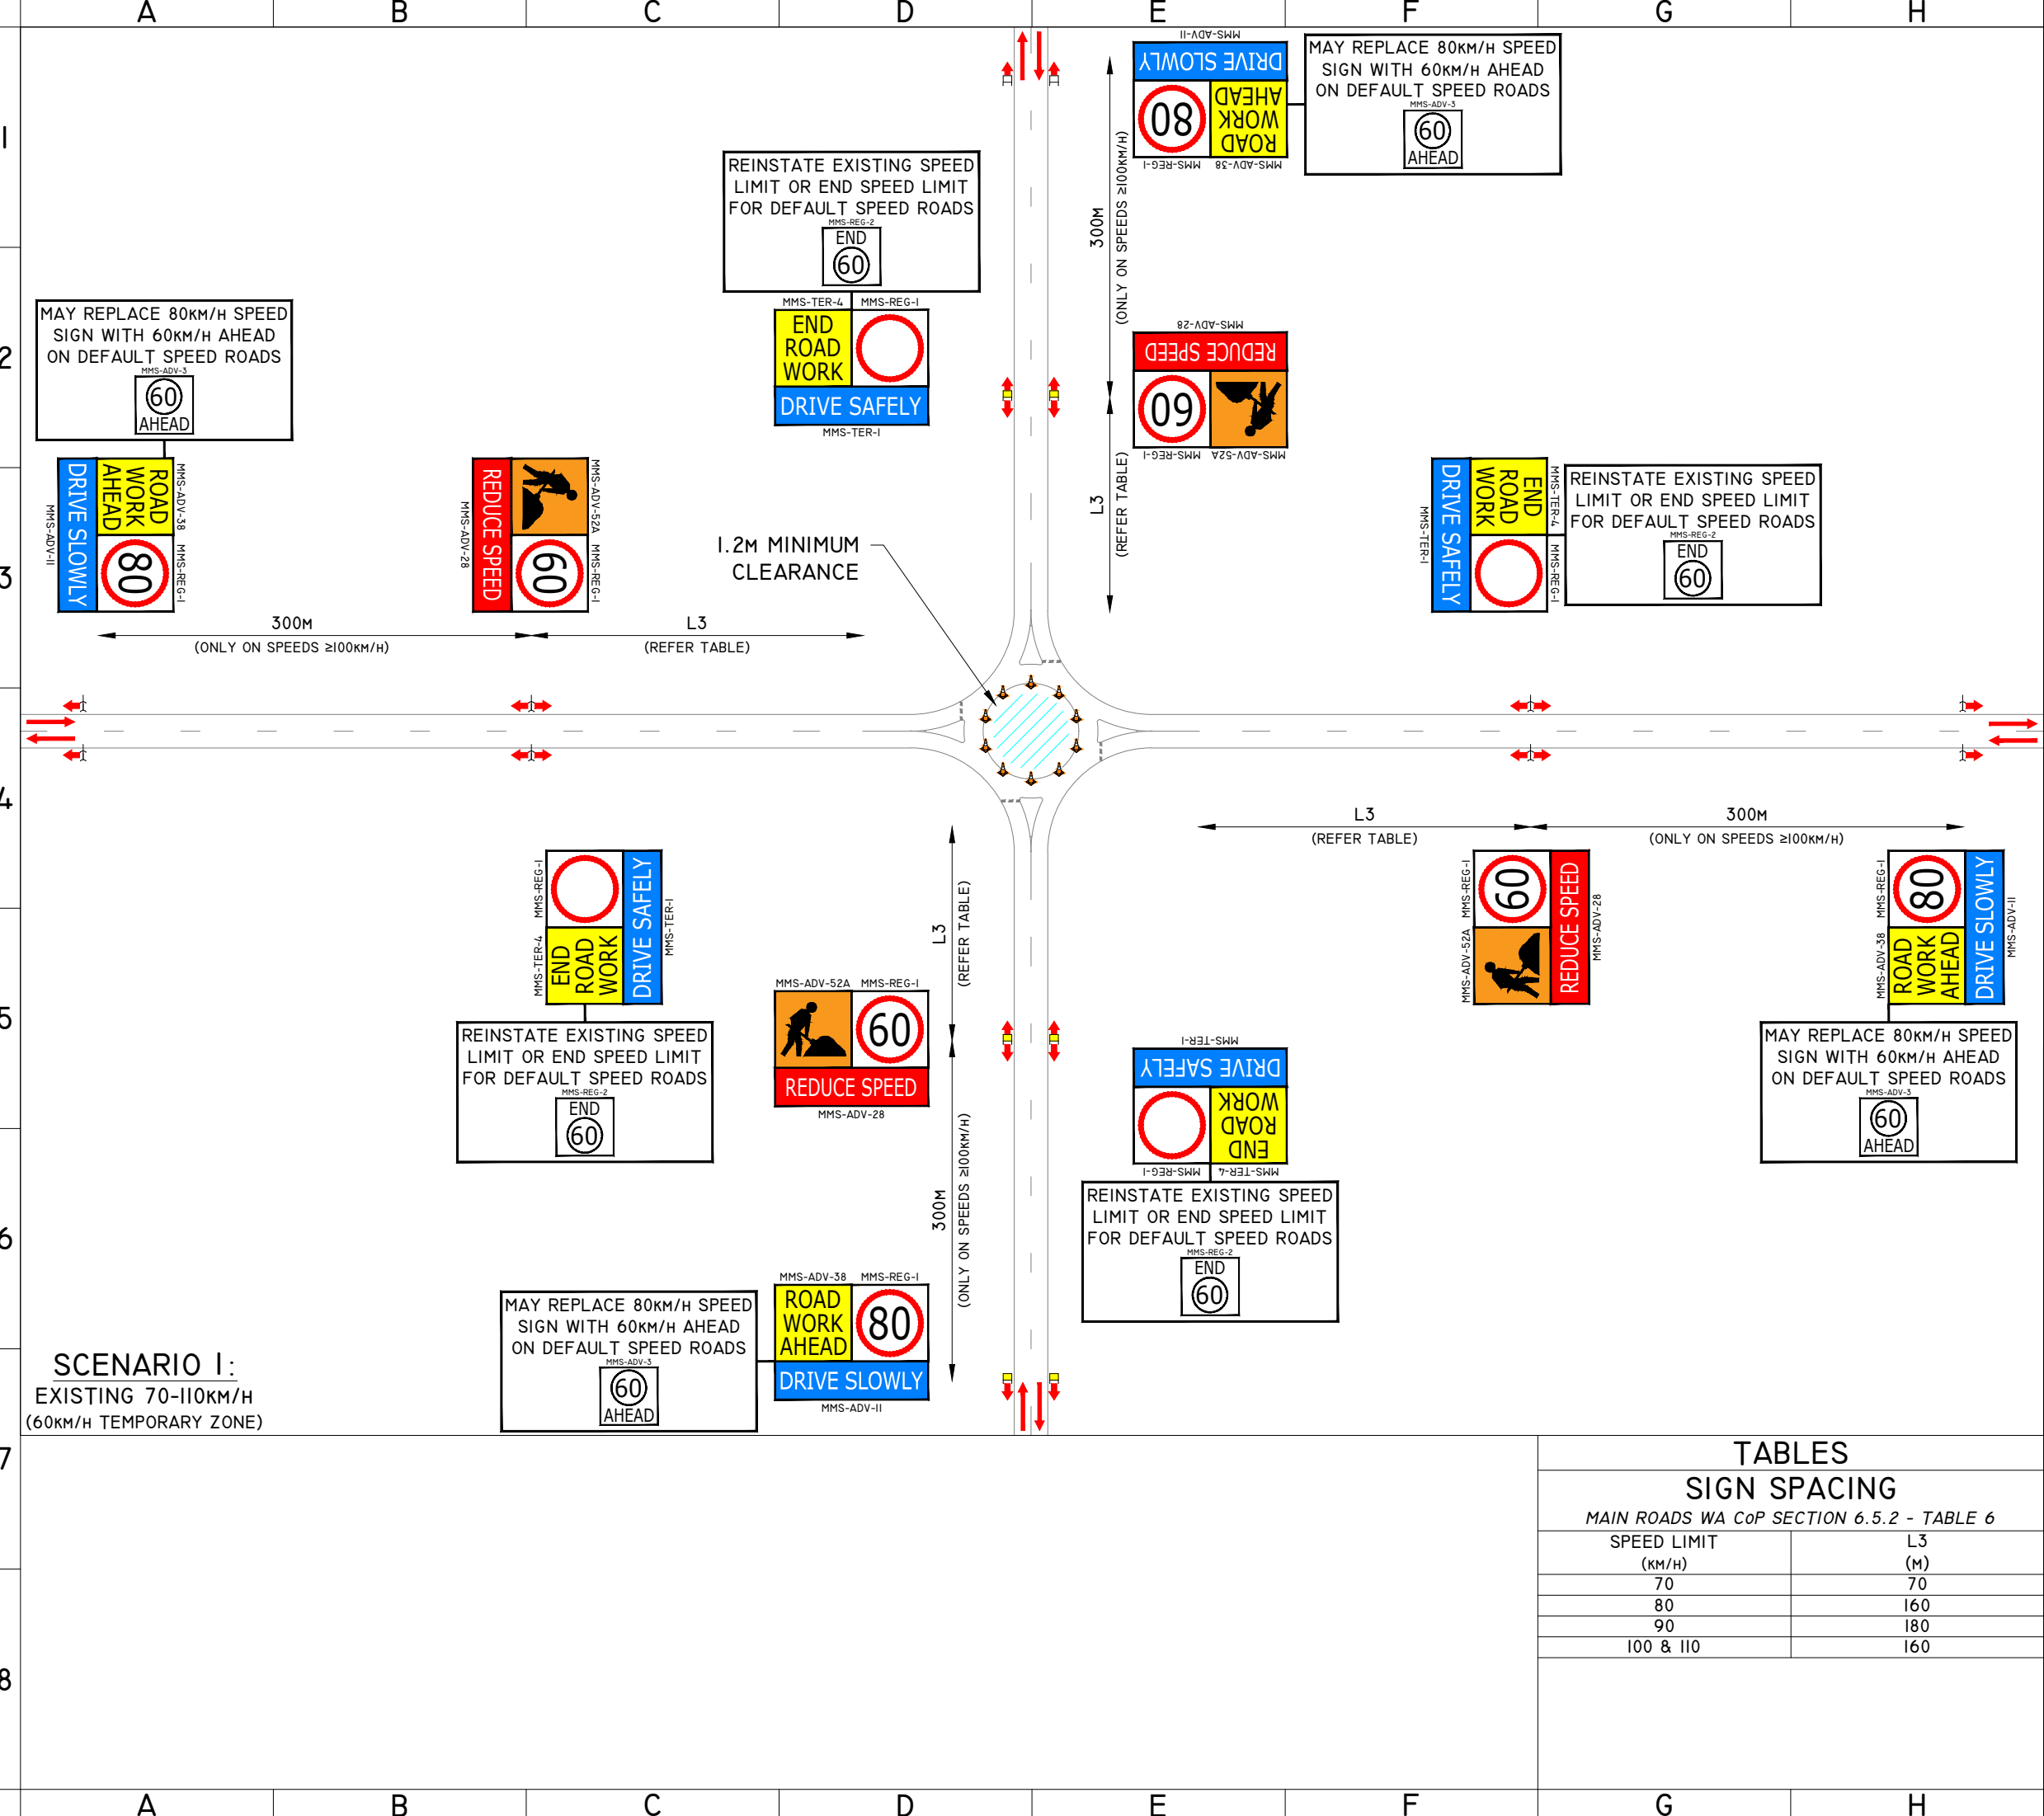

NOTES

TOLERANCES

POSITION OF SIGNS:
MINIMUM 10% LESS THAN THE DISTANCE OR LENGTHS GIVEN.
MAXIMUM 25% MORE THAN THE DISTANCES OR LENGTHS GIVEN.

SPACING OF DELINEATING DEVICES:
MAXIMUM 10% MORE THAN THE SPACING GIVEN.
NO MINIMUM.

AGTTM PART 6 SECTION 6.8.

DOCUMENTATION

IF REQUIRED, AN APPROVAL BY THE TRAFFIC MANAGEMENT SUPERVISOR MUST BE SOUGHT, THAN AN ON-SITE VARIATION MADE AND CHANGES RECORDED IN THE DAILY DAIRY. FOR MORE INFORMATION REFER TO SECTION 9.3 OF THE TMP.

- A RISK ASSESSMENT MUST BE CARRIED OUT TO DETERMINE THE REQUIREMENTS OF AFTERCARE.
- ALL SIGN LOCATIONS ARE TO BE CHECKED ON SITE PRIOR TO SETOUT AND POSITIONS ADJUSTED AS PER THE 'TOLERANCES'.
- FOR BOX EDGED SIGN ALTERNATIVES, CONSULT AWTM PRIOR TO IMPLEMENTATION.
- ALL CONTRADICTORY SIGNS WITHIN THE TM SETUP TO BE COVERED BY SUITABLY OPAQUE MATERIAL.

PEDESTRIAN MANAGEMENT

- 'PEDESTRIAN WATCH YOUR STEP' SIGN TO BE INSTALLED ON EACH APPROACH WHERE WORKS MAY ENCROACH ONTO OR ADJACENT TO EXISTING FOOTPATH FACILITIES.
- TM PERSONNEL TO MONITOR AND ESCORT PEDESTRIANS THROUGH THE WORK AREA AS REQUIRED.
- PEDESTRIANS MAY BE HELD ON EITHER END OF THE WORKSITE UNTIL IT IS SAFE TO PASS AS REQUIRED.

RECOMMENDED CONE SPACING

AGTTM PART 3 - TABLE 5.3

ALL PURPOSES:
(≤ 50KM/H): 4M

PROTECTING FRESHLY PAINTED LINES:
(≤ 70KM/H): 24M

LEGEND

EXISTING ROAD

PROPOSED CONES

WORKSITE



METROPOLITAN REGIONS
TRAFFIC MANAGEMENT BRANCH
WATERLOO CRESCENT
TELEPHONE (08) 138 138

EAST PERTH 6004

DATE OF DRAWING
2025 JULY

LOCAL GOVERNMENT AUTHORITY
-

ROAD AUTHORITY
MAIN ROADS WA

CHECKED BY
TYLER HARTLEY

ACCREDITATION
RTM-0066


DRAWN BY
MICHAEL REED

ACCREDITATION
AWTM-23-11536-02

SCALE
-

POSTED SPEED
70-110KM/H

WORKSITE SPEED
60KM/H

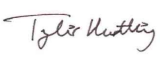SIGNATURE


SIGNATURE


TABLES

SIGN SPACING

MAIN ROADS WA CoP SECTION 6.5.2 - TABLE 6

SPEED LIMIT (KM/H)	L3 (M)
70	70
80	160
90	180
100 & 110	160

GENERIC TRAFFIC GUIDANCE SCHEME
WORKS OFF ROAD SETUPS
WITHIN ROUNDABOUT
WORKSITE BETWEEN 1.2M AND 3.0M

DRAWING NO
0922-01531-WR-016

REVISION
6