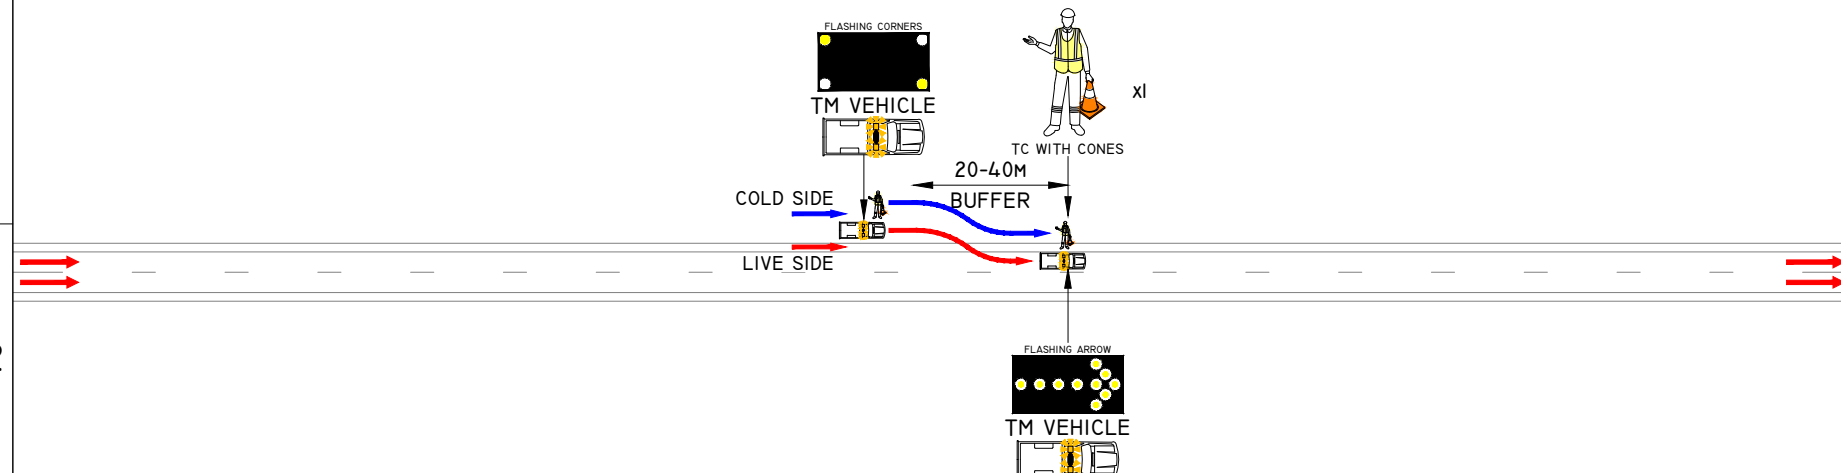
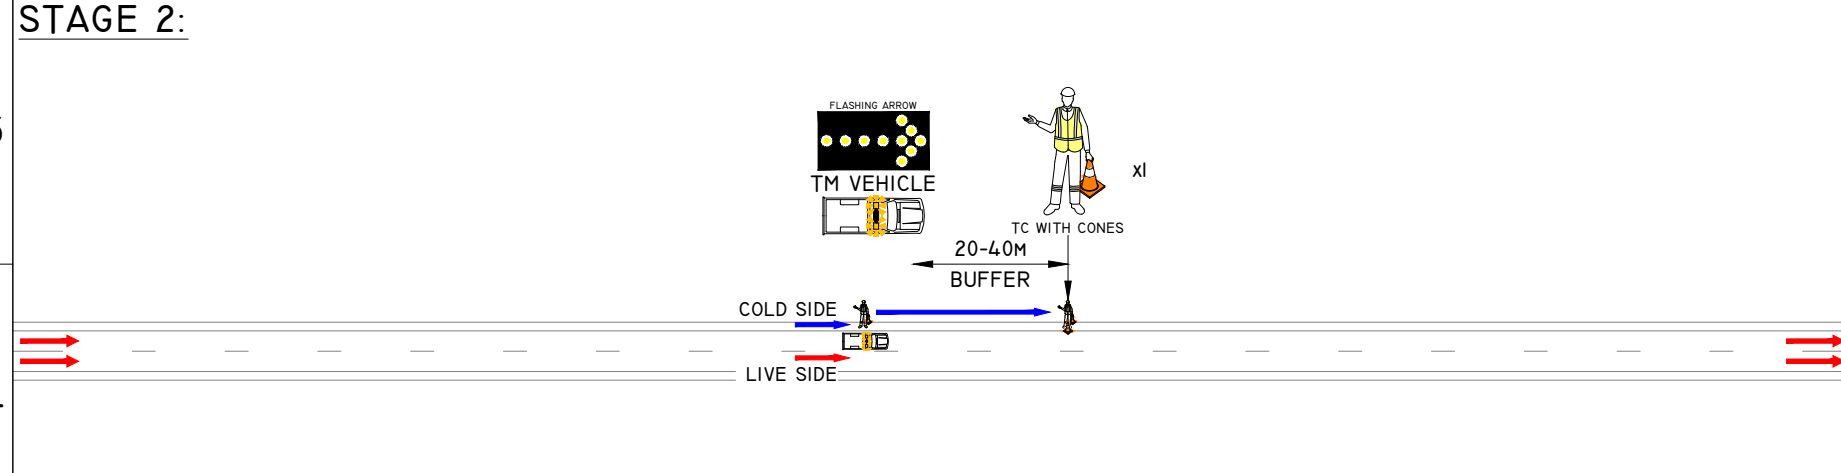
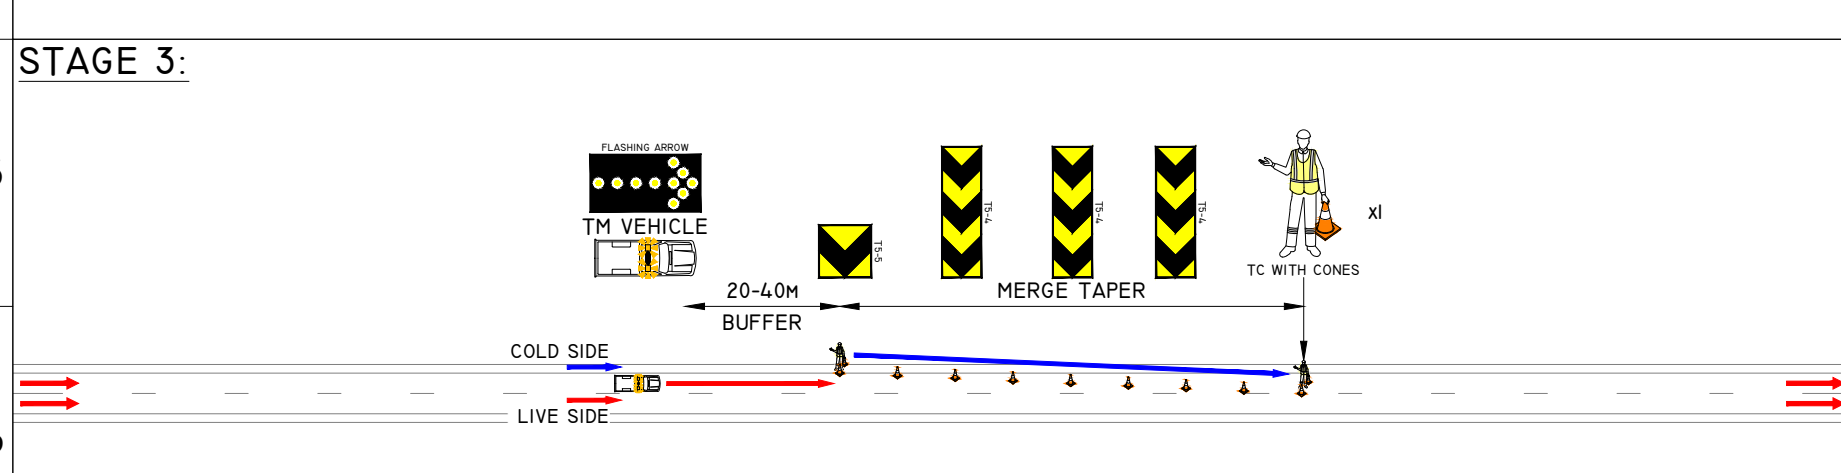
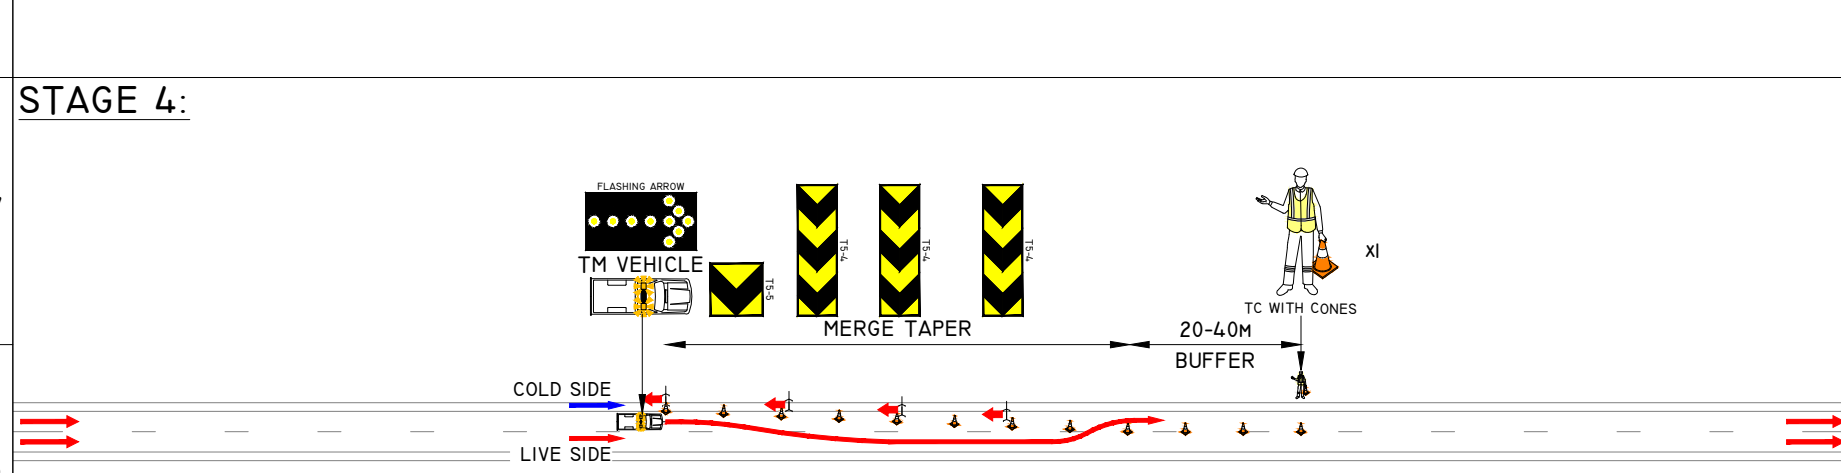


A		B		C		D		E		F		G		H																
STAGE 1:												IMPLEMENTATION PROCEDURES		NOTES																
1												STAGE 1: 1. VEHICLE SLOWS AND ENTERS EMERGENCY LANE/VERGE WITH BEACONS ACTIVATED AND BOARD SHOWING OPPOSING DIAGONAL BEACON FLASHES. 2. VEHICLE STOPS AND TRAFFIC CONTROLLER REMOVES CONES FROM COLD SIDE OF VEHICLE. 3. TC POSITIONS 20M IN ADVANCE OF WORK VEHICLE WITHIN EMERGENCY LANE WHILE WATCHING TRAFFIC. 4. WORK VEHICLE SWITCHES BOARD TO RIGHT ARROW AND ENTERS TRAFFIC LANE THROUGH A SUITABLE GAP IN TRAFFIC TO POSITION ITSELF ADJACENT TO TC.		DOCUMENTATION ON-SITE VARIATIONS MUST BE APPROVED BY THE TRAFFIC MANAGEMENT SUPERVISOR, THAN AN ON-SITE VARIATION MADE AND CHANGES RECORDED IN THE DAILY DAIRY. FOR MORE INFORMATION REFER TO SECTION 9.3 OF THE TMP. 1. TM VEHICLE SHALL BE ANY OF THE FOLLOWING: 1.1. TRAFFIC MANAGEMENT UTE 1.2. UTE WITH ARROW BOARD 1.3. CONE TRUCK 1.4. MR TRUCK 1.5. HR TRUCK 1.6. TRUCK MOUNTED ATTENUATOR 2. THIS DRAWING IS FOR IMPLEMENTATION ONLY AND MUST BE USED IN CONJUNCTION WITH AN APPROVED TRAFFIC MANAGEMENT LAYOUT TGS. 3. THIS DRAWING IS TO BE USED AS A GUIDELINE FOR THE TYPICAL MERGE TAPER INSTALLATION AND MAY CHANGE DEPENDING SITE REQUIREMENTS.																
2												STAGE 2: 1. VEHICLE STOPS IN LANE ADJACENT TO VERGE/EMERGENCY LANE. 2. TC WHILE MONITORING TRAFFIC BEGINS PLACEMENT OF CONE DELINEATION TAPER. 3. TC USES EMERGENCY LANE TO TRAVEL TO AND FROM WORK VEHICLE TO CONE PLACEMENT AREA WHILST MAINTAINING 2M FROM LIVE TRAFFIC. 4. CONE DEVICES TO BE DEPLOYED FROM COLD SIDE OF VEHICLE ONLY.																		
3												STAGE 3: 1. AS TAPER PROGRESSES, WORK VEHICLE TRACKS ALONG CLOSED LANE MAINTAINING AT LEAST 20M TO THE TC WORK LOCATION UNTIL REACHING START OF TAPER. 2. WORK VEHICLE TO STOP IN LANE AT START OF TAPER WHILST THE REST OF THE TAPER IS INSTALLED.																		
4												STAGE 4: 1. VEHICLE TO REMAIN AT START OF TAPER AS TC INSTALLS REMAINING CONES AND DEVICES FROM TAPER. 2. TC TO INSTALL 20M OF CONES IMMEDIATELY AFTER TAPER FOR THE CONTINUATION OF CONE INSTALL UNDER SHADOW VEHICLE PROTECTION. 3. ONCE TAPER IS COMPLETE, TC TO MOVE TO SHOULDER/VERGE AT A SAFE DISTANCE FROM LIVE TRAFFIC. 4. WORK VEHICLE TO MOVE TO END OF TAPER AND INSTALL REQUIRED FLASHING ARROW BOARD AND REMAINING DELINEATION DEVICES. TC OR DRIVER TO ACT AS SPOTTER WHILE ARROW BOARD IS DETACHED TO WARN OF ERRANT VEHICLES.																		
												FOR IMPLEMENTATION ONLY																		
												LEGEND EXISTING ROAD PROPOSED CONES TC MOVEMENTS TM VEHICLE MOVEMENTS																		
												 METROPOLITAN REGIONS TRAFFIC MANAGEMENT BRANCH WATERLOO CRESCENT TELEPHONE (08) 138 138 EAST PERTH 6004 <table><tr><td>DATE OF DRAWING 2025 JULY</td><td>SCALE -</td></tr><tr><td>LOCAL GOVERNMENT AUTHORITY -</td><td>POSTED SPEED -</td></tr><tr><td>ROAD AUTHORITY MAIN ROADS WA</td><td>WORKSITE SPEED -</td></tr><tr><td>CHECKED BY TYLER HARTLEY</td><td>SIGNATURE </td></tr><tr><td>ACCREDITATION RTM-0066</td><td rowspan="2">SIGNATURE </td></tr><tr><td>DESIGNED BY MICHAEL REED</td></tr><tr><td>ACCREDITATION AWTM-23-11536-02</td><td></td></tr></table> GENERIC TRAFFIC GUIDANCE SCHEME IMPLEMENTATION WORK SETUPS TAPER IMPLEMENTATION SETUP CONE DELINEATION <table><tr><td>DRAWING NO 0922-01531-IW-001</td><td>REVISION 6</td></tr></table>		DATE OF DRAWING 2025 JULY	SCALE -	LOCAL GOVERNMENT AUTHORITY -	POSTED SPEED -	ROAD AUTHORITY MAIN ROADS WA	WORKSITE SPEED -	CHECKED BY TYLER HARTLEY	SIGNATURE 	ACCREDITATION RTM-0066	SIGNATURE 	DESIGNED BY MICHAEL REED	ACCREDITATION AWTM-23-11536-02		DRAWING NO 0922-01531-IW-001	REVISION 6		
DATE OF DRAWING 2025 JULY	SCALE -																													
LOCAL GOVERNMENT AUTHORITY -	POSTED SPEED -																													
ROAD AUTHORITY MAIN ROADS WA	WORKSITE SPEED -																													
CHECKED BY TYLER HARTLEY	SIGNATURE 																													
ACCREDITATION RTM-0066	SIGNATURE 																													
DESIGNED BY MICHAEL REED																														
ACCREDITATION AWTM-23-11536-02																														
DRAWING NO 0922-01531-IW-001	REVISION 6																													
A		B		C		D		E		F		G		H																