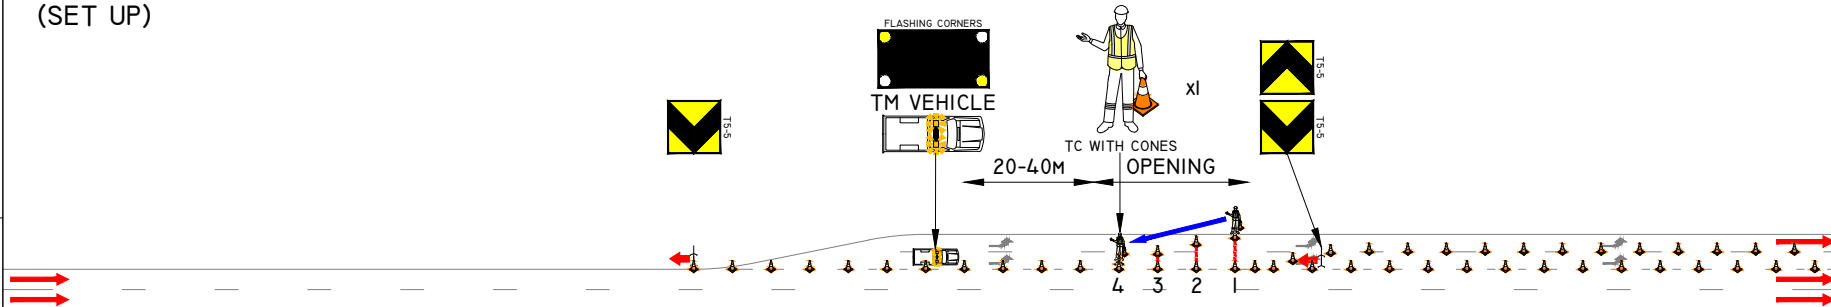
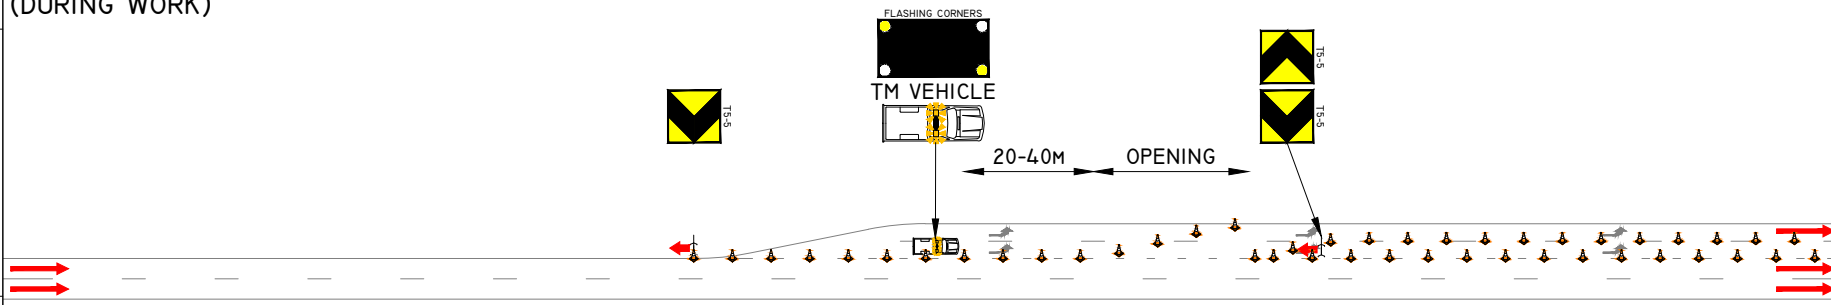
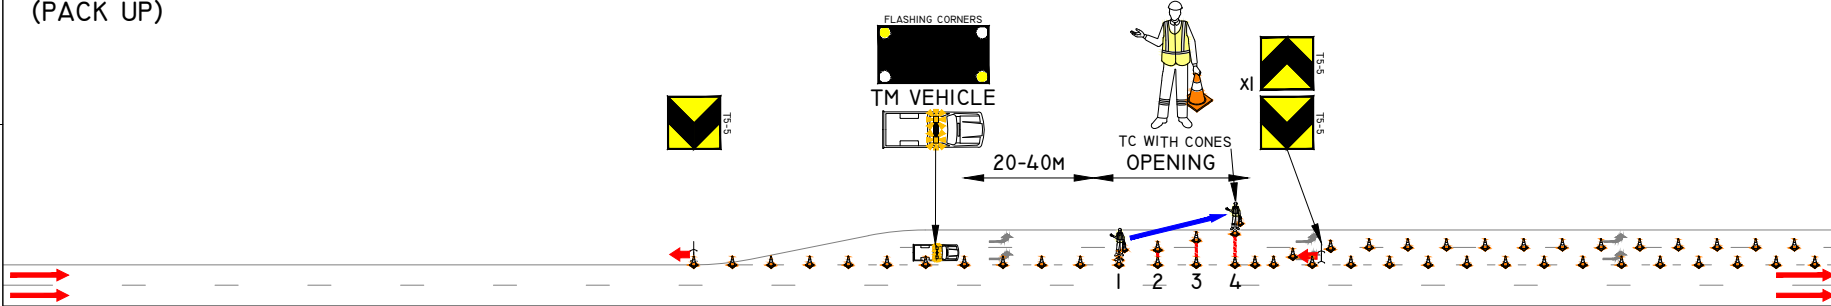


A		B		C		D		E		F		G		H															
STAGE 4: (SET UP)												IMPLEMENTATION PROCEDURES		NOTES															
												STAGE 4: 1. WORK CREW PREPARES EQUIPMENT IN ADVANCE OF WORK VEHICLE AREA. 2. DRIVER PLACES T5-5 SHIFT MARKERS AND MOVES TO VERGE. 3. TC SETS BACK CONE DELINEATION AS INDICATED FROM 1 - 4. TC TO OPERATE WITHIN CLOSED LANE SIDE AT ALL TIMES. 4. TRAFFIC CONTROLLER POSITIONS TO VERGE AND JOINS DRIVER. 5. TRAFFIC TO BE MONITORED IN ADVANCE AT ALL TIMES.		DOCUMENTATION ON-SITE VARIATIONS MUST BE APPROVED BY THE TRAFFIC MANAGEMENT SUPERVISOR, THAN AN ON-SITE VARIATION MADE AND CHANGES RECORDED IN THE DAILY DAIRY. FOR MORE INFORMATION REFER TO SECTION 9.3 OF THE TMP. 1. TM VEHICLE SHALL BE ANY OF THE FOLLOWING: 1.1. TRAFFIC MANAGEMENT UTE 1.2. UTE WITH ARROW BOARD 1.3. CONE TRUCK 1.4. MR TRUCK 1.5. HR TRUCK 1.6. TRUCK MOUNTED ATTENUATOR 2. THIS DRAWING IS FOR IMPLEMENTATION ONLY AND MUST BE USED IN CONJUNCTION WITH AN APPROVED TRAFFIC MANAGEMENT LAYOUT TGS. 3. THIS DRAWING IS TO BE USED AS A GUIDELINE FOR THE TYPICAL CHICANE INSTALLATION AND MAY CHANGE DEPENDING SITE REQUIREMENTS.															
STAGE 5: (DURING WORK)												STAGE 5: 1. WORKER RETURNS TO CLOSED LANE AND COMMENCES WORKS. 2. TRAFFIC CONTROLLER REMAINS IN ADVANCE WATCHING FOR TRAFFIC. 3. ONCE WORKS ARE COMPLETE TRAFFIC CONTROLLER POSITIONS READY FOR STAGE 6.		FOR IMPLEMENTATION ONLY LEGEND - EXISTING ROAD - PROPOSED CONES - TC MOVEMENTS															
																													
STAGE 6: (PACK UP)												STAGE 6: 1. TRAFFIC CONTROLLER RETURNS CONE DELINEATION TO CLOSE OFF ACCESS TO LEFT TURN LANES. TRAFFIC CONTROLLER WORKS FROM END OF WORKSITE TOWARDS TRUCK REINSTATING STRAIGHT DELINEATION. 2. DRIVER REMOVES T5-5 SHIFT MARKERS. 3. TRAFFIC CONTROLLER COLLECTS CONES RE-OPNEING THE TURN LANE.		  METROPOLITAN REGIONS TRAFFIC MANAGEMENT BRANCH WATERLOO CRESCENT TELEPHONE (08) 138 138 EAST PERTH 6004 <table><tr><td>DATE OF DRAWING 2025 JULY</td><td>SCALE -</td></tr><tr><td>LOCAL GOVERNMENT AUTHORITY -</td><td>POSTED SPEED -</td></tr><tr><td>ROAD AUTHORITY MAIN ROADS WA</td><td>WORKSITE SPEED -</td></tr><tr><td>CHECKED BY TYLER HARTLEY</td><td>SIGNATURE </td></tr><tr><td>ACCREDITATION RTM-0066</td><td rowspan="3">SIGNATURE </td></tr><tr><td>DESIGNED BY MICHAEL REED</td></tr><tr><td>ACCREDITATION AWTM-23-11536-02</td></tr></table> GENERIC TRAFFIC GUIDANCE SCHEME IMPLEMENTATION WORK SETUPS CHICANE SETUP CONE DELINEATION (2/2) <table><tr><td>DRAWING NO 0922-01531-IW-004</td><td>REVISION 6</td></tr></table>		DATE OF DRAWING 2025 JULY	SCALE -	LOCAL GOVERNMENT AUTHORITY -	POSTED SPEED -	ROAD AUTHORITY MAIN ROADS WA	WORKSITE SPEED -	CHECKED BY TYLER HARTLEY	SIGNATURE 	ACCREDITATION RTM-0066	SIGNATURE 	DESIGNED BY MICHAEL REED	ACCREDITATION AWTM-23-11536-02	DRAWING NO 0922-01531-IW-004	REVISION 6
DATE OF DRAWING 2025 JULY	SCALE -																												
LOCAL GOVERNMENT AUTHORITY -	POSTED SPEED -																												
ROAD AUTHORITY MAIN ROADS WA	WORKSITE SPEED -																												
CHECKED BY TYLER HARTLEY	SIGNATURE 																												
ACCREDITATION RTM-0066	SIGNATURE 																												
DESIGNED BY MICHAEL REED																													
ACCREDITATION AWTM-23-11536-02																													
DRAWING NO 0922-01531-IW-004	REVISION 6																												
																													
A		B		C		D		E		F		G		H															