


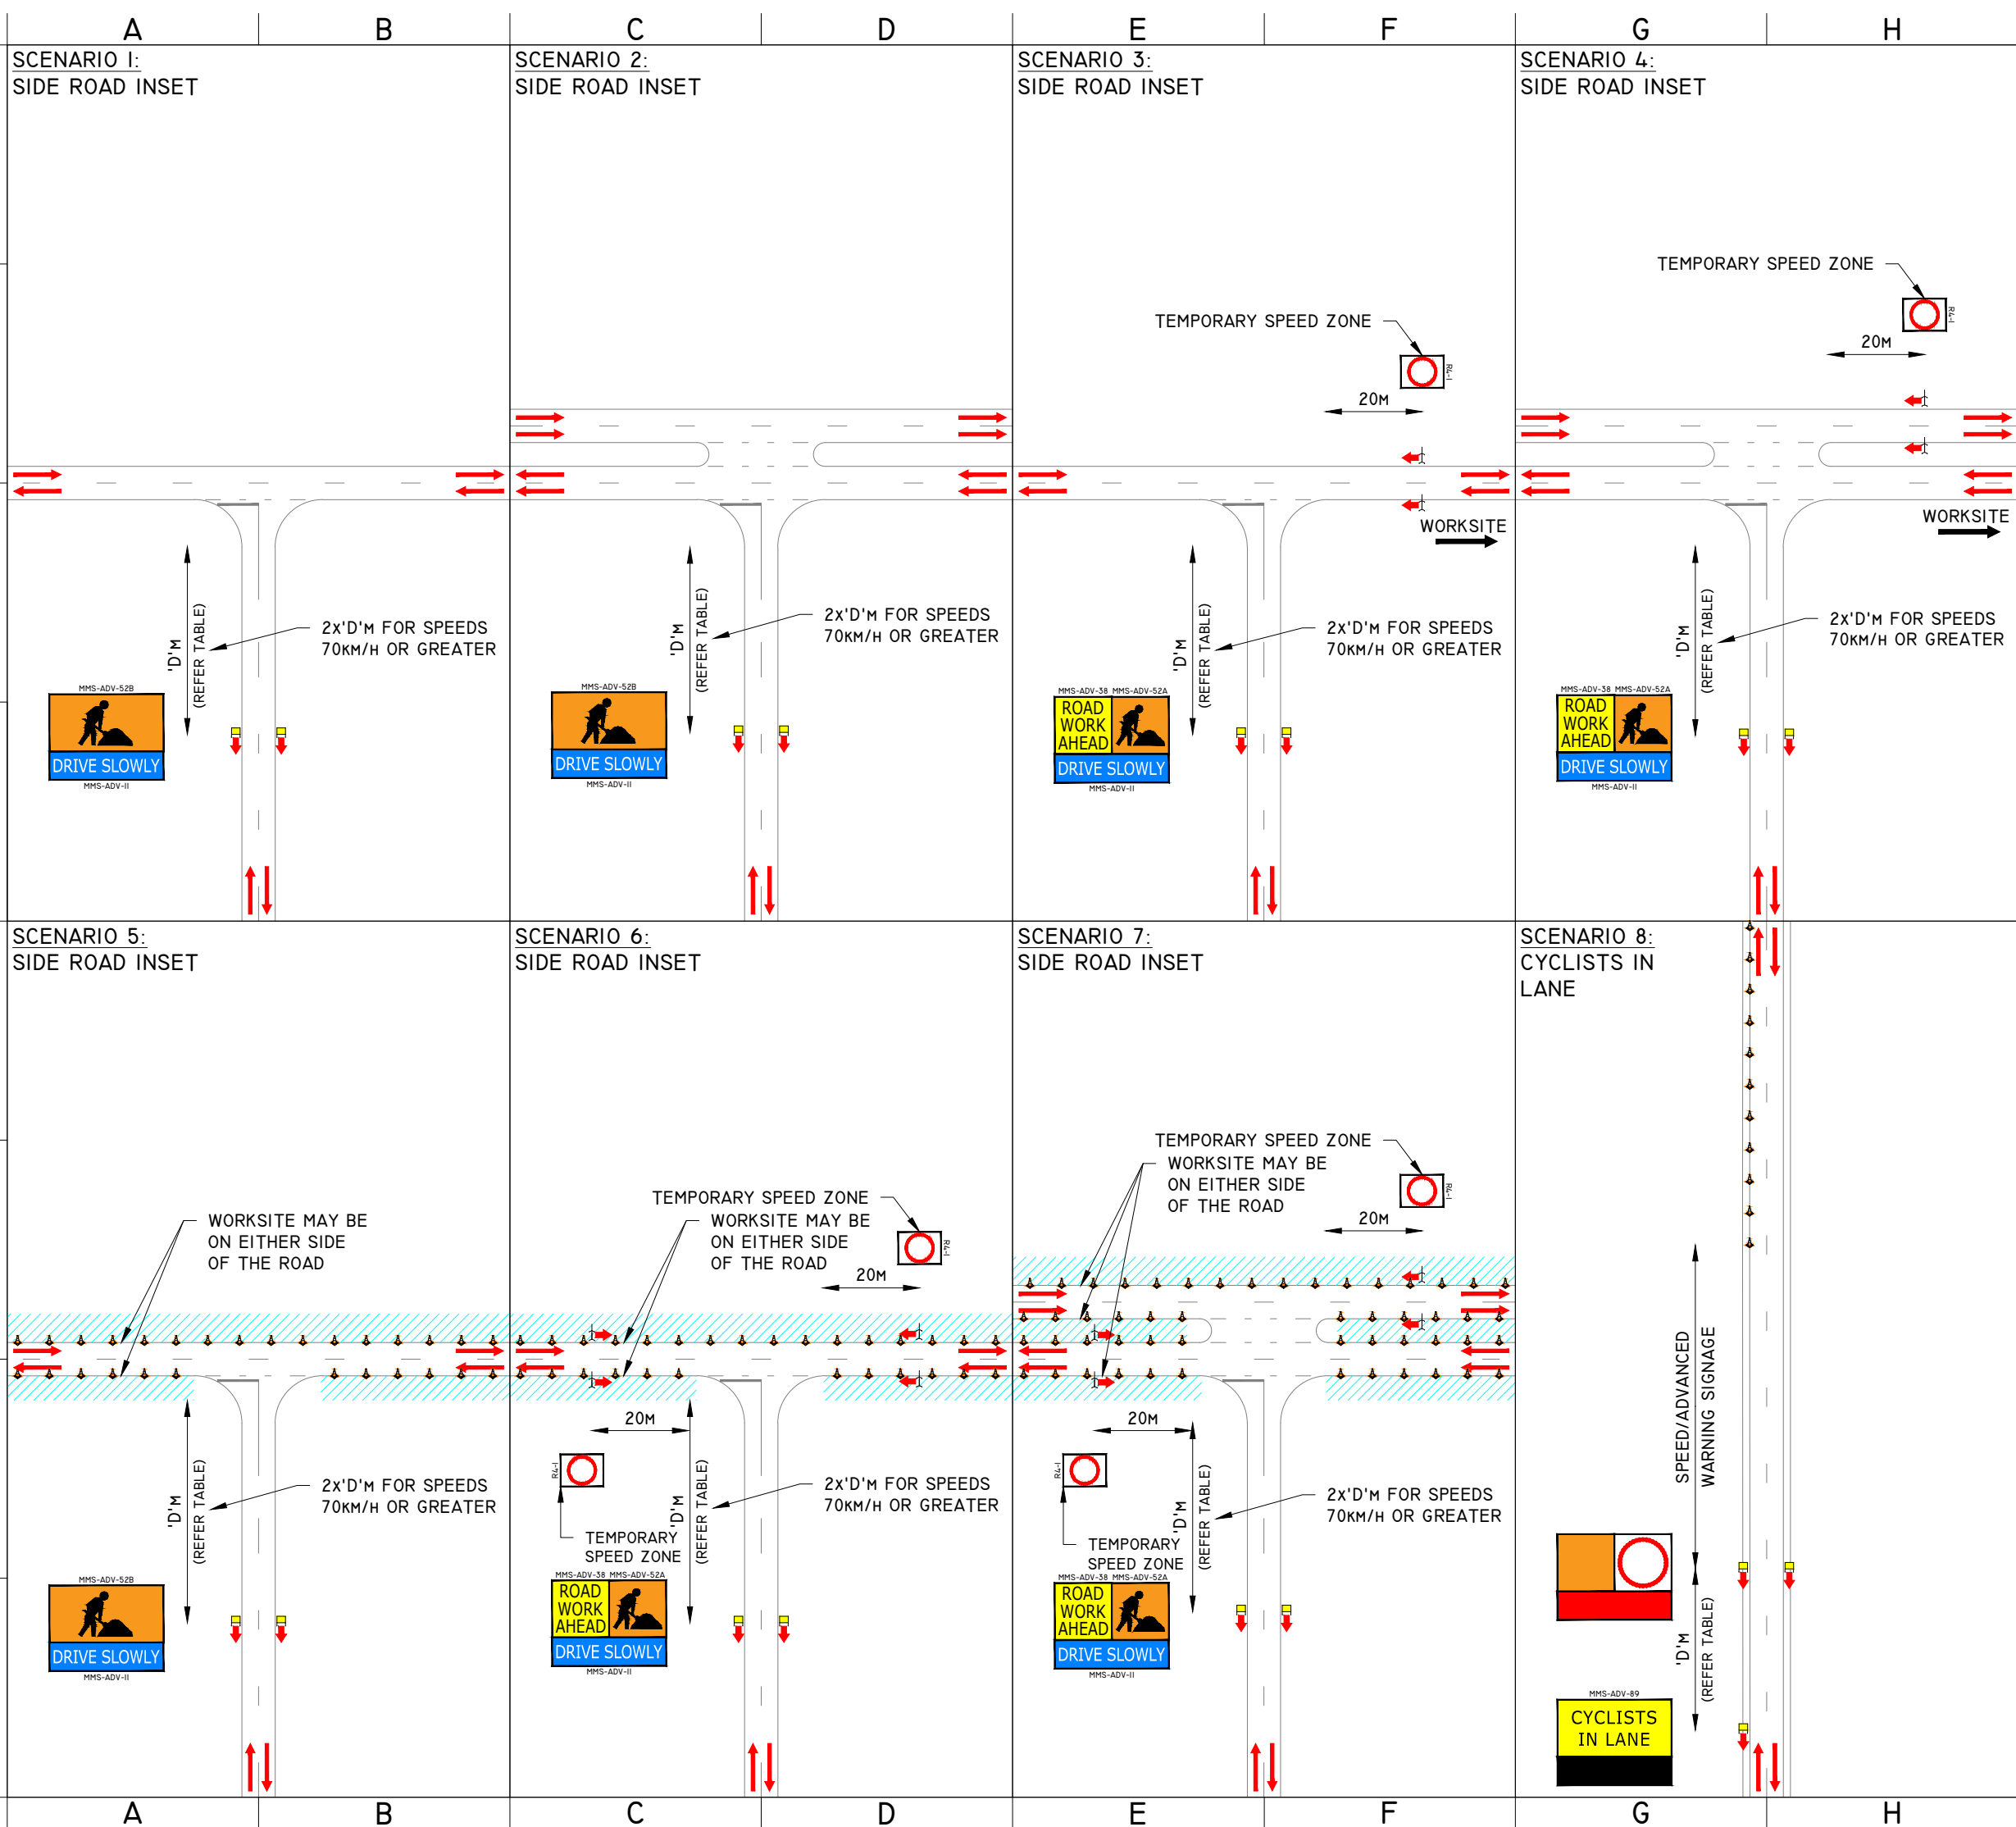

NOTES		
TOLERANCES POSITION OF SIGNS: MINIMUM 10% LESS THAN THE DISTANCE OR LENGTHS GIVEN. MAXIMUM 25% MORE THAN THE DISTANCES OR LENGTHS GIVEN. SPACING OF DELINEATING DEVICES: MAXIMUM 10% MORE THAN THE SPACING GIVEN. NO MINIMUM. AGTMM PART 6 SECTION 6.8.		1
DOCUMENTATION IF REQUIRED, AN APPROVAL BY THE TRAFFIC MANAGEMENT SUPERVISOR MUST BE SOUGHT, THAN AN ON-SITE VARIATION MADE AND CHANGES RECORDED IN THE DAILY DAIRY. FOR MORE INFORMATION REFER TO SECTION 9.3 OF THE TMP.		2
GENERAL NOTES 1. ALL SIGN LOCATIONS ARE TO BE CHECKED ON SITE PRIOR TO SETOUT AND POSITIONS ADJUSTED AS PER THE 'TOLERANCES'. 2. FOR BOX EDGED SIGN ALTERNATIVES, CONSULT AWTMM PRIOR TO IMPLEMENTATION.		
TABLES		
SIGN SPACING AGTMM PART 3 - TABLE 2.2		
SPEED LIMIT (KM/H)	DISTANCE ('D') (M)	
55 OR LESS	15	3
56 TO 65	45	
GREATER THAN 65	EQUAL TO SPEED OF TRAFFIC IN KM/H	
		4
		5
LEGEND		
— EXISTING ROAD		
🚧 🚧 🚧 🚧 PROPOSED CONES		
▨ WORKSITE		
 		6
METROPOLITAN REGIONS TRAFFIC MANAGEMENT BRANCH WATERLOO CRESCENT EAST PERTH 6004 TELEPHONE (08) 138 138		
DATE OF DRAWING 2025 JULY	SCALE -	
LOCAL GOVERNMENT AUTHORITY -	POSTED SPEED -	7
ROAD AUTHORITY MAIN ROADS WA	WORKSITE SPEED -	
CHECKED BY TYLER HARTLEY	SIGNATURE 	
ACCREDITATION RTM-0066		
DRAWN BY MICHAEL REED	SIGNATURE 	
ACCREDITATION AWTM-23-I1536-02		
GENERIC TRAFFIC GUIDANCE SCHEME WORKS OFF ROAD SETUPS MULTIPLE ROAD CONFIGURATIONS SIDE ROAD INSETS		8
DRAWING NO 0922-01531-WR-I01		REVISION 6