SCENARIO 1:

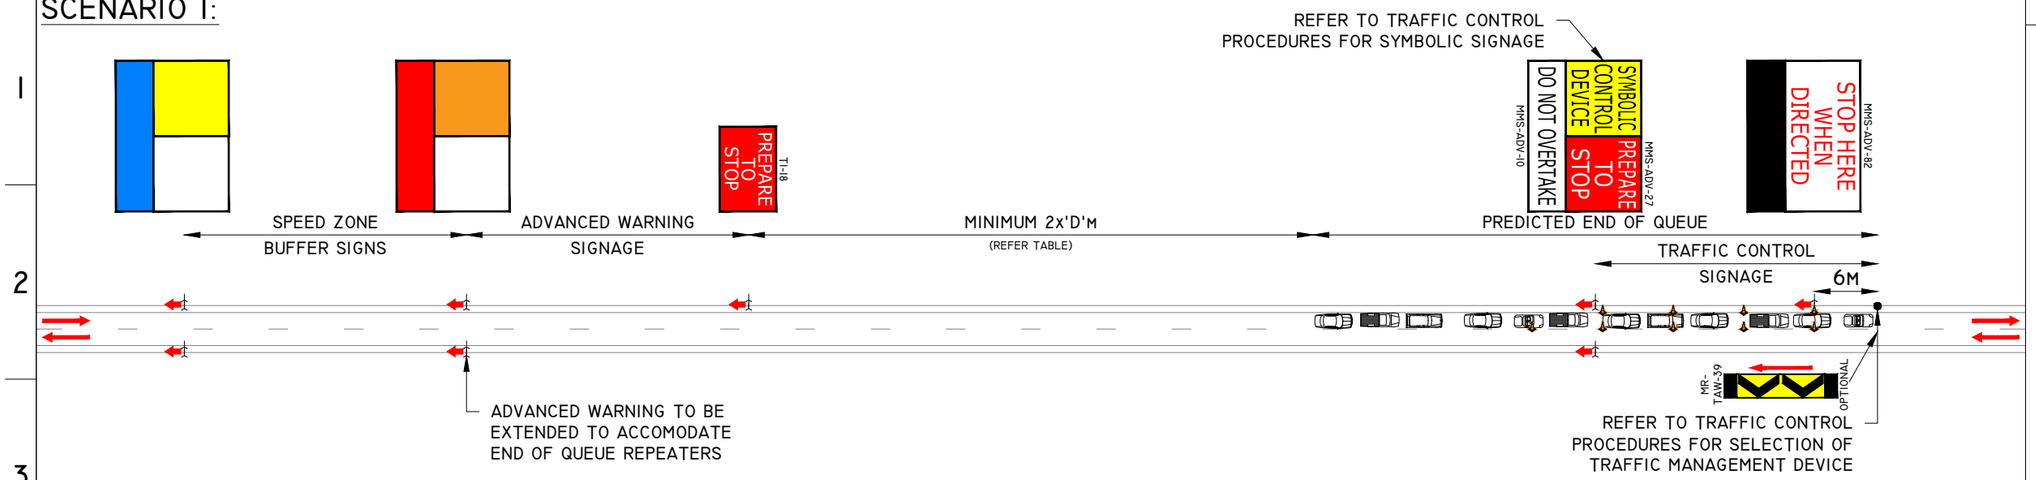

EXISTING 80-110KM/H
(QUEUE LENGTHS LESS THAN 4x'D'M)

SCENARIO 2:

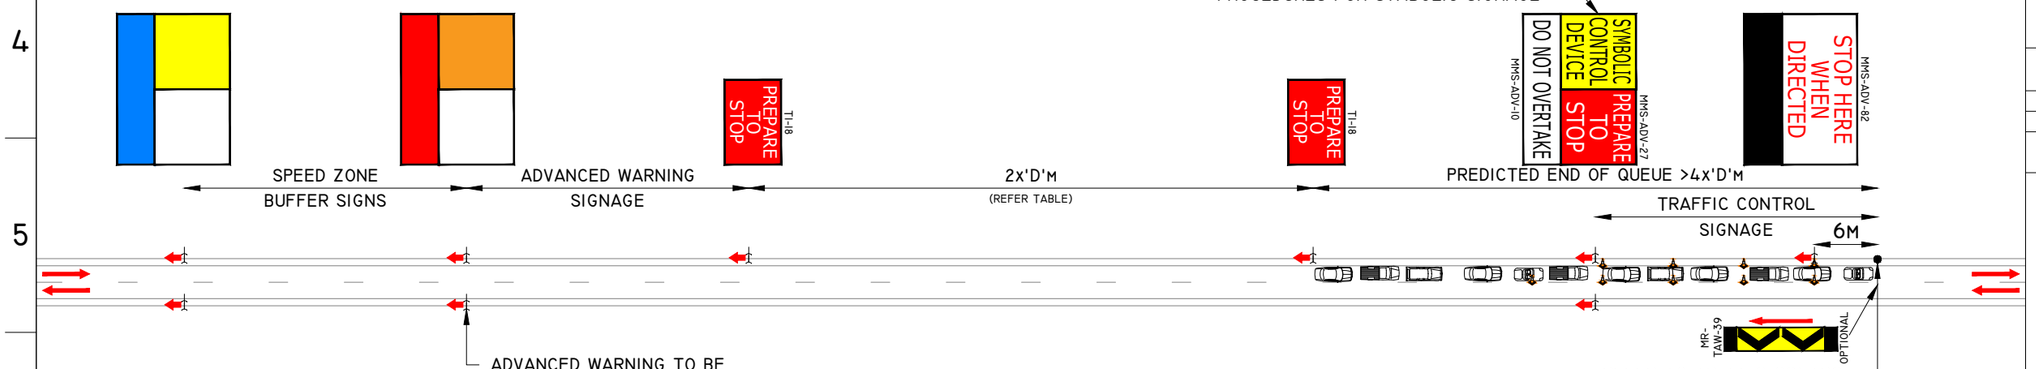

EXISTING 40-110KM/H
(QUEUE LENGTHS MORE THAN 4x'D'M)

TRAFFIC CONTROL PROCEDURES

REFER TO TMP SECTION 4.1.7 PORTABLE TRAFFIC CONTROL DEVICES FOR MORE DETAILS

MANUAL TRAFFIC CONTROL

MANUAL TRAFFIC CONTROL IS NOT PERMITTED ON THE MAIN ROADS NETWORK WITH THE EXCEPTIONS LISTED UNDER SECTION 4.1.7 (PORTABLE TRAFFIC CONTROL DEVICES) OF THE TMP AND IN THE MAIN ROADS CODE OF PRACTICE.
ON ALL OTHER ROADS, PTCDs MUST BE USED UNDER THE FOLLOWING CONDITIONS:

- A PERMANENT SPEED LIMIT OF 90M/H OR MORE AND OVER 2,000VPD; OR
- A PERMANENT SPEED LIMIT OF 80KM/H OR MORE AND OVER 10,000VPD.

PTCDs SHOULD BE CONSIDERED ON ALL WORKS AND ONLY BE SUPPLEMENTED WITH MANUAL TRAFFIC CONTROL UNDER AN AWTM/WTM RISK ASSESSMENT.

PORTABLE TRAFFIC CONTROL DEVICE (PTCD)

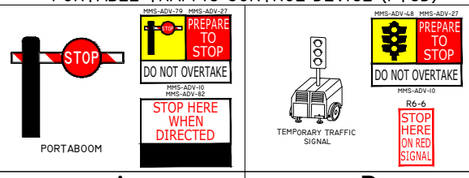

NOTES

TOLERANCES

POSITION OF SIGNS: MINIMUM 10% LESS THAN THE DISTANCE OR LENGTHS GIVEN. MAXIMUM 25% MORE THAN THE DISTANCES OR LENGTHS GIVEN. SPACING OF DELINEATING DEVICES: MAXIMUM 10% MORE THAN THE SPACING GIVEN. NO MINIMUM.
AGTTM PART 6 SECTION 6.8.

DOCUMENTATION

ON-SITE VARIATIONS MUST BE APPROVED BY THE TRAFFIC MANAGEMENT SUPERVISOR, THAN AN ON-SITE VARIATION MADE AND CHANGES RECORDED IN THE DAILY DAIRY. FOR MORE INFORMATION REFER TO SECTION 9.3 OF THE TMP.

1. SIGHT DISTANCE TO PREPARE TO STOP SIGNS TO BE MINIMUM 2x'D'M.
2. THESE SCENARIOS DO NOT DEPICT THE REQUIRED SPEED REDUCTIONS AND ADVANCED WARNING SIGNAGE WHICH MUST BE INCLUDED. ADVANCED WARNING SIGNS MUST BE AT LEAST 'D'M IN ADVANCE OF THE PREPARE TO STOP SIGN.
3. IT IS RECOMMENDED, WHERE POSSIBLE, THE PREPARE TO STOP (TI-18B) SIGN IS USED IN ADVANCE OF THE END OF QUEUE.
4. PREDICTED QUEUE LENGTHS MUST BE CALCULATED FOR ALL APPROACHES. THE END OF QUEUE CALCULATIONS MUST BE ISSUED WITH THE TM ADVICE FOR REFERENCE.
5. A SECOND TRAFFIC CONTROLLER MAY BE USED TO SLOW VEHICLES DOWN PRIOR TO THE PRIMARY TRAFFIC CONTROLLER.
6. QUEUE LENGTHS ARE TO BE MONITORED FOR THE DURATION OF THE WORKS TO DETERMINE IF ADDITIONAL WARNING SIGNS NEED TO BE RELOCATED.

TABLES

SIGN SPACING

AGTTM PART 3 - TABLE 2.2

SPEED LIMIT (KM/H)	DISTANCE ('D') (M)
55 OR LESS	15
56 TO 65	45
GREATER THAN 65	EQUAL TO SPEED OF TRAFFIC IN KM/H

LEGEND

EXISTING ROAD

PROPOSED CONES

METROPOLITAN REGIONS
TRAFFIC MANAGEMENT BRANCH
WATERLOO CRESCENT EAST PERTH 6004
TELEPHONE (08) 138 138

DATE OF DRAWING: 2025 JULY	DESIGNED BY: MICHAEL REED	ACCREDITATION: AWTM-23-11536-02	SIGNATURE
POSTED SPEED: VARIES	CHECKED BY: TYLER HARTLEY	ACCREDITATION: RTM-0066	SIGNATURE
WORKSITE SPEED: VARIES	SCALE: -	ROAD AUTHORITY: MAIN ROADS WA	LOCAL GOVERNMENT AUTHORITY: -

SCENARIO 1:

- TO BE USED WHERE QUEUE LENGTHS DO NOT EXCEED 4x'D'M AND SPEEDS ARE LESS THAN 70KM/H

SCENARIO 2:

- TO BE USED WHERE QUEUE LENGTHS EXCEED 4x'D'M

GENERIC TRAFFIC GUIDANCE SCHEME
REVERSIBLE FLOW SETUPS
HIGH SPEED ROADS
END OF QUEUE PROTECTION

DRAWING NO: 0922-01531-RF-022

REVISION: 6