


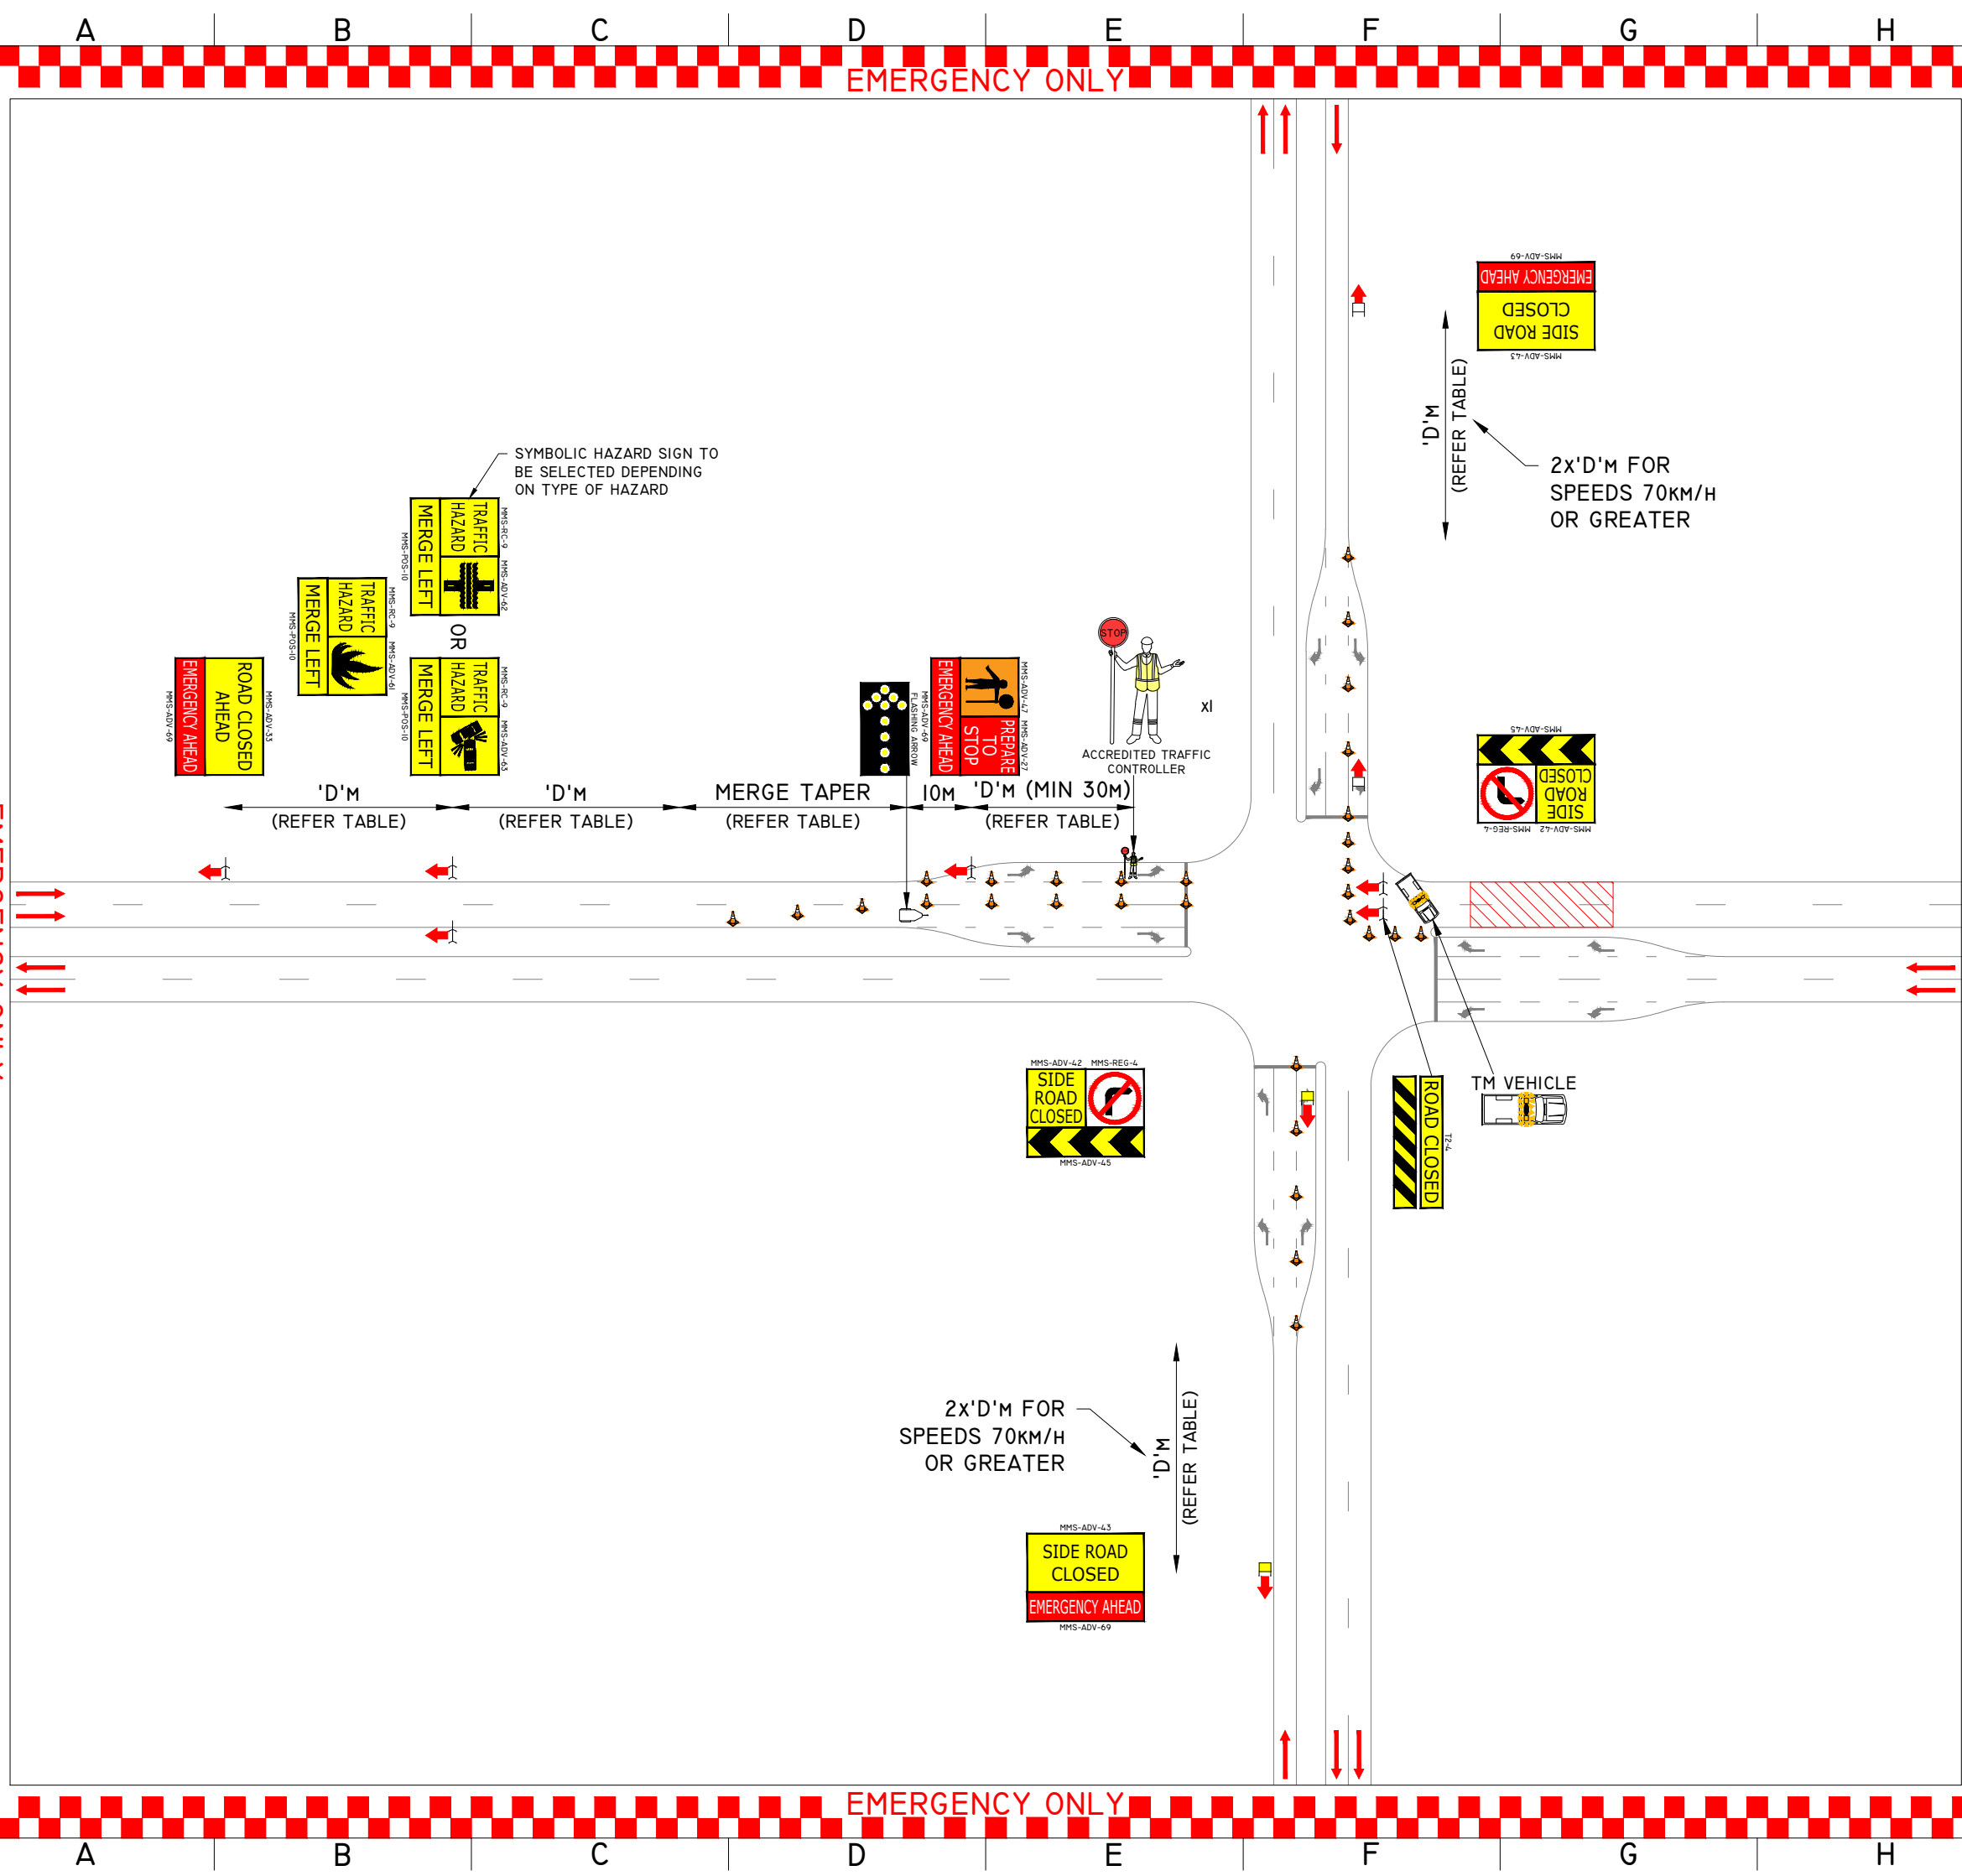

NOTES

TOLERANCES:
POSITION OF SIGNS:
MINIMUM 10% LESS THAN THE DISTANCE OR LENGTHS GIVEN.
MAXIMUM 25% MORE THAN THE DISTANCES OR LENGTHS GIVEN.
SPACING OF DELINEATING DEVICES:
MAXIMUM 10% MORE THAN THE SPACING GIVEN.
NO MINIMUM.

AGTTM PART 6 SECTION 6.8.

DOCUMENTATION

ON-SITE VARIATIONS MUST BE APPROVED BY THE TRAFFIC MANAGEMENT SUPERVISOR, THAN AN ON-SITE VARIATION MADE AND CHANGES RECORDED IN THE DAILY DAIRY. FOR MORE INFORMATION REFER TO SECTION 9.3 OF THE TMP.

1. PLAN TO BE USED FOR EMERGENCY WORKS ONLY.
2. ONE TM VEHICLE WILL BE REQUIRED FOR EVERY CLOSURE POINT AROUND EMERGENCY.
3. THIS PLAN MAY BE USED IN CONJUNCTION WITH OTHER EMERGENCY PLANS TO FORM A SAFE BARRIER AROUND THE HAZARD.
4. 'STOP HERE WHEN DIRECTED' SIGNAGE TO BE INSTALLED IF AVAILABLE ON SITE.

TABLES

SIGN SPACING

AGTTM PART 3 - TABLE 2.2

SPEED LIMIT (KM/H)	DISTANCE ('D') (M)
55 OR LESS	15
56 TO 65	45
GREATER THAN 65	EQUAL TO SPEED OF TRAFFIC IN KM/H

TAPER LENGTHS

AGTTM PART 3 - TABLE 5.7

SPEED LIMIT (KM/H)	MERGE TAPER (M)
45 OR LESS	15
46 TO 55	30
56 TO 65	60
66 TO 75*	115
76 TO 85*	130
86 TO 95*	145
96 TO 105*	160
GREATER THAN 105*	180

*TAPER LENGTHS ARE BASED ON A:

- 3.5M WIDTH OF THE LANE TO BE CLOSED
- MERGE TAPER LENGTH EQUAL TO 0.6M/S
- MEDIAN SPEED FOR EACH RANGE (I.E 76 - 85 = 80KM/H)

LEGEND

- EXISTING ROAD
- PROPOSED CONES
- HAZARD



**METROPOLITAN REGIONS
TRAFFIC MANAGEMENT BRANCH**

WATERLOO CRESCENT
TELEPHONE (08) 138 138

EAST PERTH 6004

DATE OF DRAWING 2025 JULY	SCALE -
STRAIGHT LINE KILOMETERS (SLK) -	POSTED SPEED -
ROAD AUTHORITY MRWA	WORKSITE SPEED -
CHECKED BY TYLER HARTLEY	SIGNATURE <i>Tyler Hartley</i>
ACCREDITATION RTM-0066	
DESIGNED BY MICHAEL REED	SIGNATURE <i>Michael Reed</i>
ACCREDITATION AWTM-23-11536-02	

**GENERIC TRAFFIC GUIDANCE SCHEME
EMERGENCY WORK SCENARIOS
MAJOR 4-WAY INTERSECTION
ROAD CLOSURE POINT**

DRAWING NO 0922-01531-EW-004	REVISION 6
---------------------------------	---------------