


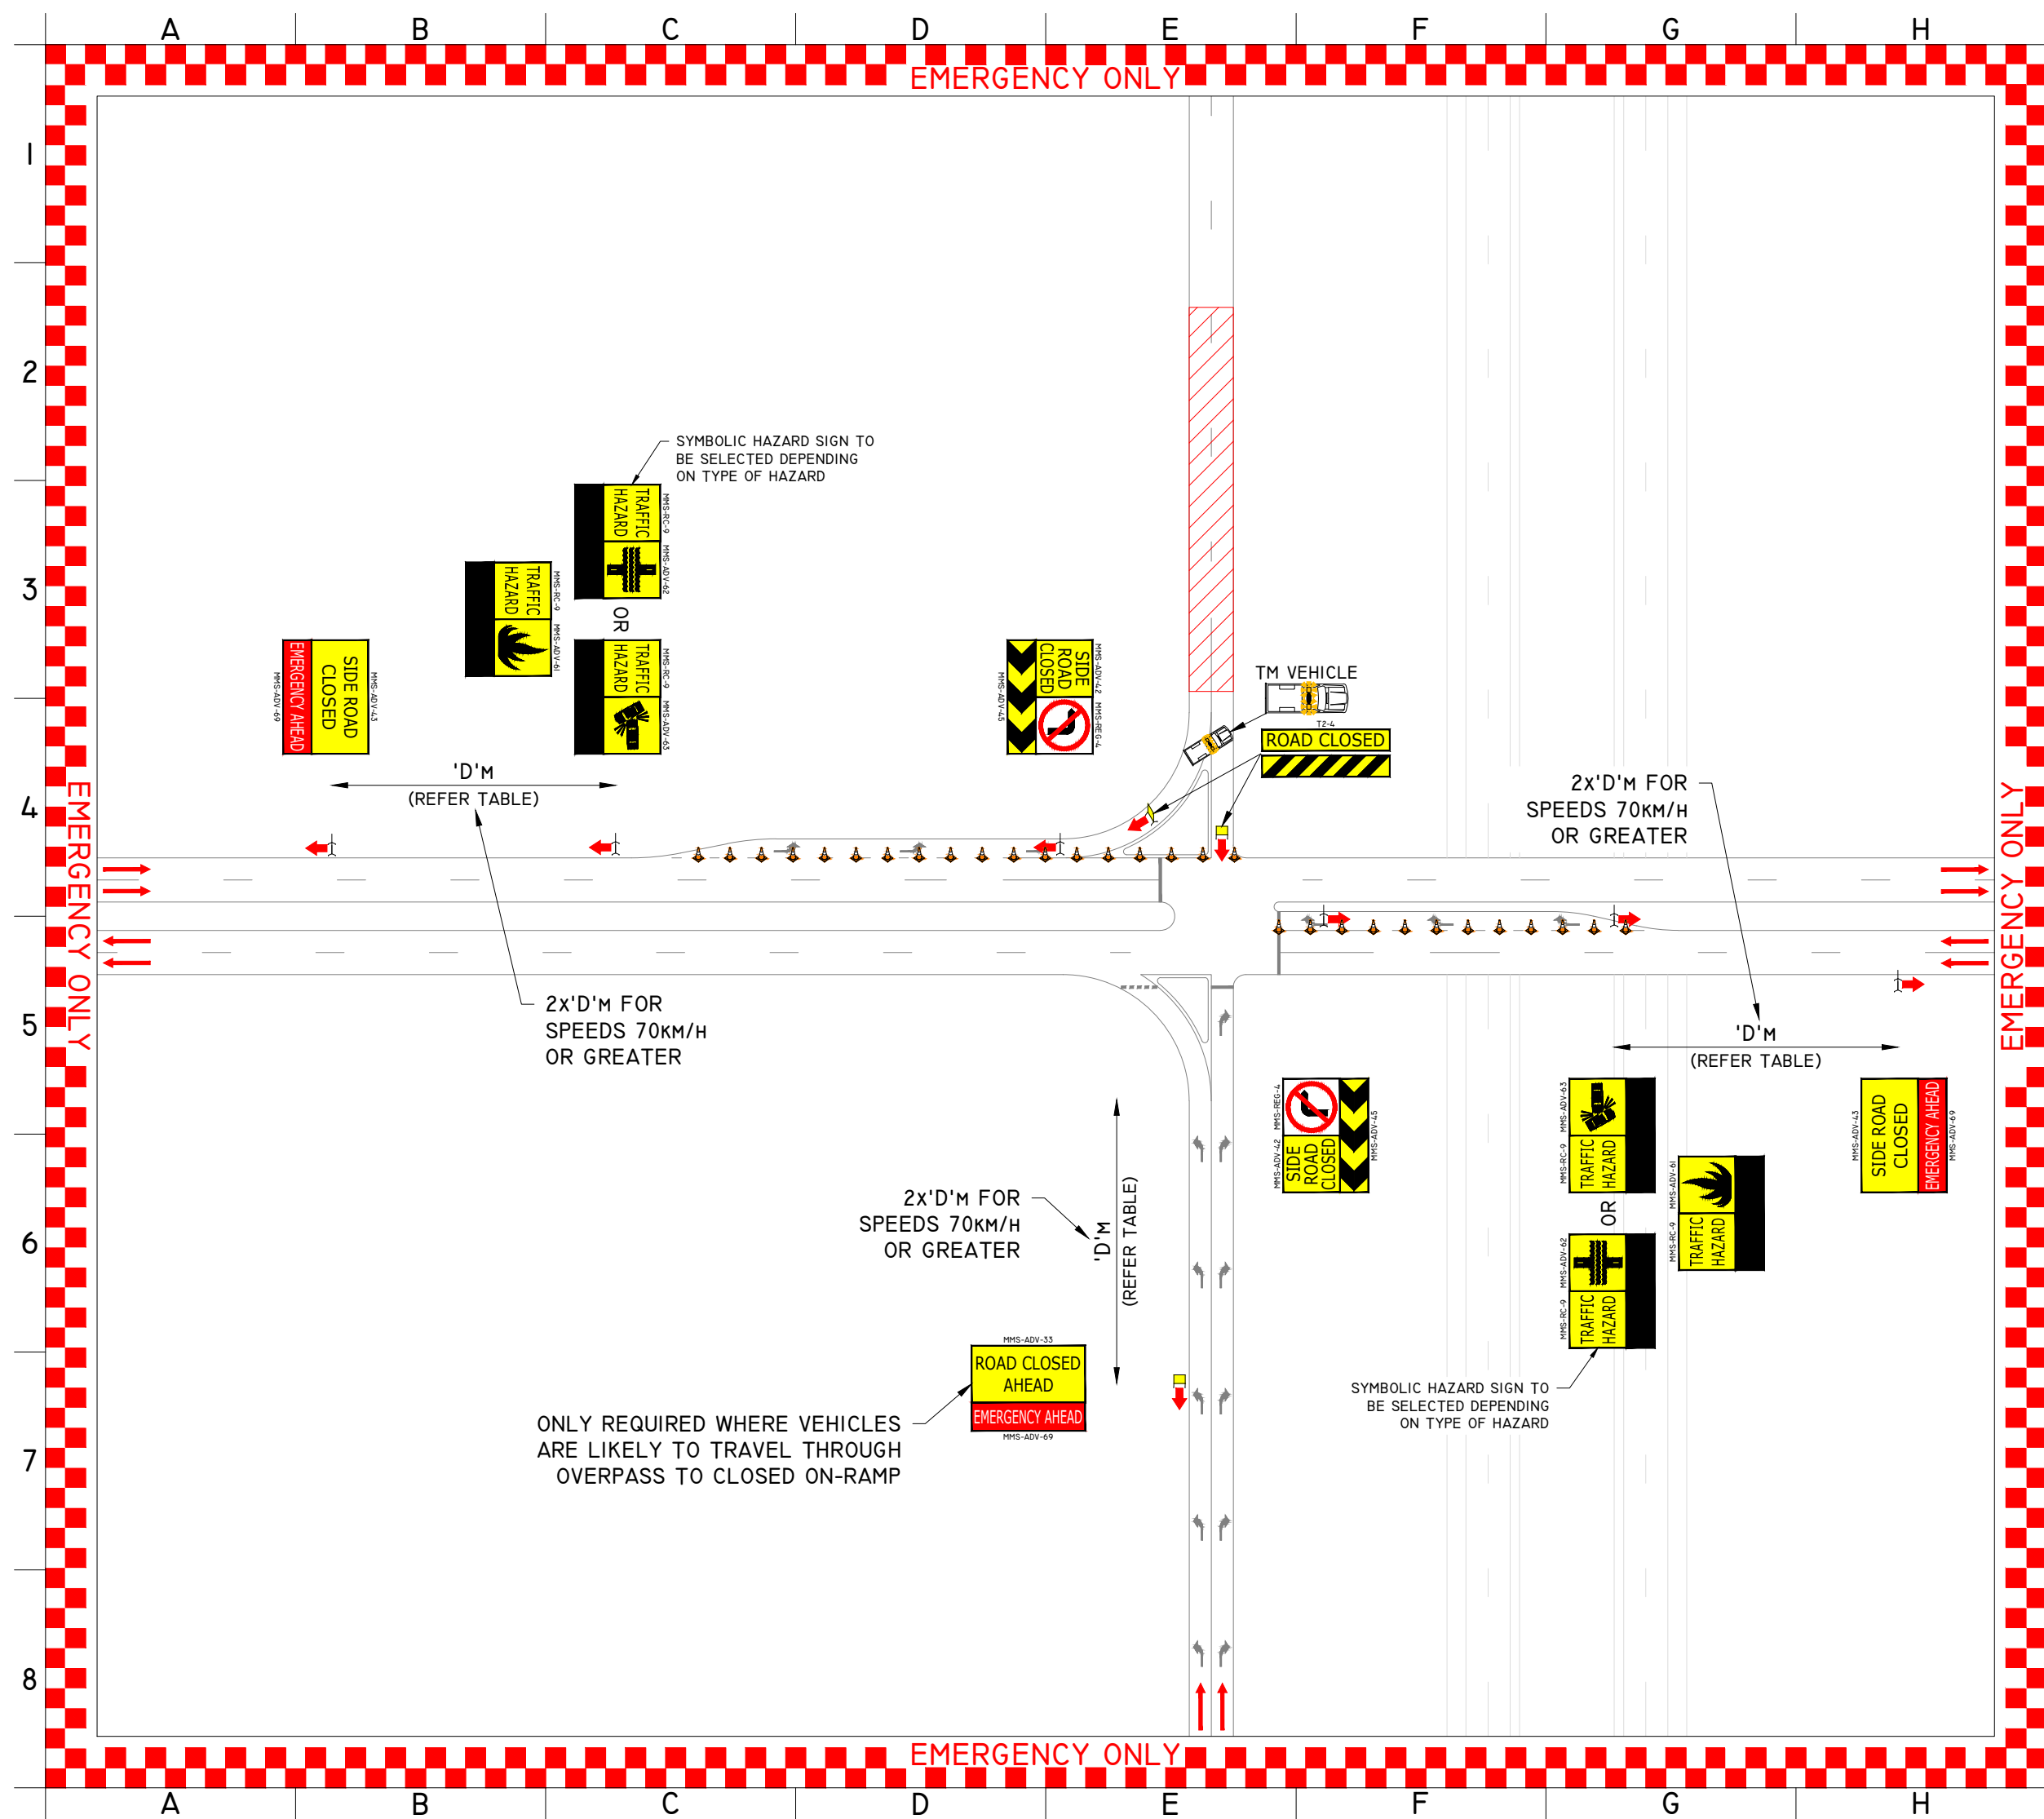

## NOTES

### TOLERANCES:

#### POSITION OF SIGNS:

MINIMUM 10% LESS THAN THE DISTANCE OR LENGTHS GIVEN.  
MAXIMUM 25% MORE THAN THE DISTANCES OR LENGTHS GIVEN.  
SPACING OF DELINEATING DEVICES:  
MAXIMUM 10% MORE THAN THE SPACING GIVEN.  
NO MINIMUM.

#### AGTTM PART 6 SECTION 6.8.

### DOCUMENTATION

ON-SITE VARIATIONS MUST BE APPROVED BY THE TRAFFIC MANAGEMENT SUPERVISOR, THAN AN ON-SITE VARIATION MADE AND CHANGES RECORDED IN THE DAILY DAIRY. FOR MORE INFORMATION REFER TO SECTION 9.3 OF THE TMP.

1. PLAN TO BE USED FOR EMERGENCY WORKS ONLY.
2. ONE TM VEHICLE WILL BE REQUIRED FOR EVERY CLOSURE POINT AROUND EMERGENCY.
3. THIS PLAN MAY BE USED IN CONJUNCTION WITH OTHER EMERGENCY PLANS TO FORM A SAFE BARRIER AROUND THE HAZARD.

## TABLES

### SIGN SPACING

AGTTM PART 3 - TABLE 2.2

| SPEED LIMIT (km/h) | DISTANCE ('D') (m)                |
|--------------------|-----------------------------------|
| 55 OR LESS         | 15                                |
| 56 TO 65           | 45                                |
| GREATER THAN 65    | EQUAL TO SPEED OF TRAFFIC IN km/h |

## LEGEND

- EXISTING ROAD
- PROPOSED CONES
- HAZARD



### METROPOLITAN REGIONS TRAFFIC MANAGEMENT BRANCH

WATERLOO CRESCENT  
TELEPHONE (08) 138 138

|                                     |                                   |
|-------------------------------------|-----------------------------------|
| DATE OF DRAWING<br>2025 JULY        | SCALE<br>-                        |
| STRAIGHT LINE KILOMETERS (SLK)<br>- | POSTED SPEED<br>-                 |
| ROAD AUTHORITY<br>MRWA              | WORKSITE SPEED<br>-               |
| CHECKED BY<br>TYLER HARTLEY         | SIGNATURE<br><i>Tyler Hartley</i> |
| ACCREDITATION<br>RTM-0066           |                                   |
| DESIGNED BY<br>MICHAEL REED         | SIGNATURE<br><i>Michael Reed</i>  |
| ACCREDITATION<br>AWTM-23-11536-02   |                                   |

GENERIC TRAFFIC GUIDANCE SCHEME  
EMERGENCY WORK SCENARIOS  
OVERPASS ON-RAMP  
CLOSURE POINT

|                                 |               |
|---------------------------------|---------------|
| DRAWING NO<br>0922-01531-EW-009 | REVISION<br>6 |
|---------------------------------|---------------|