



SCENARIO 1:

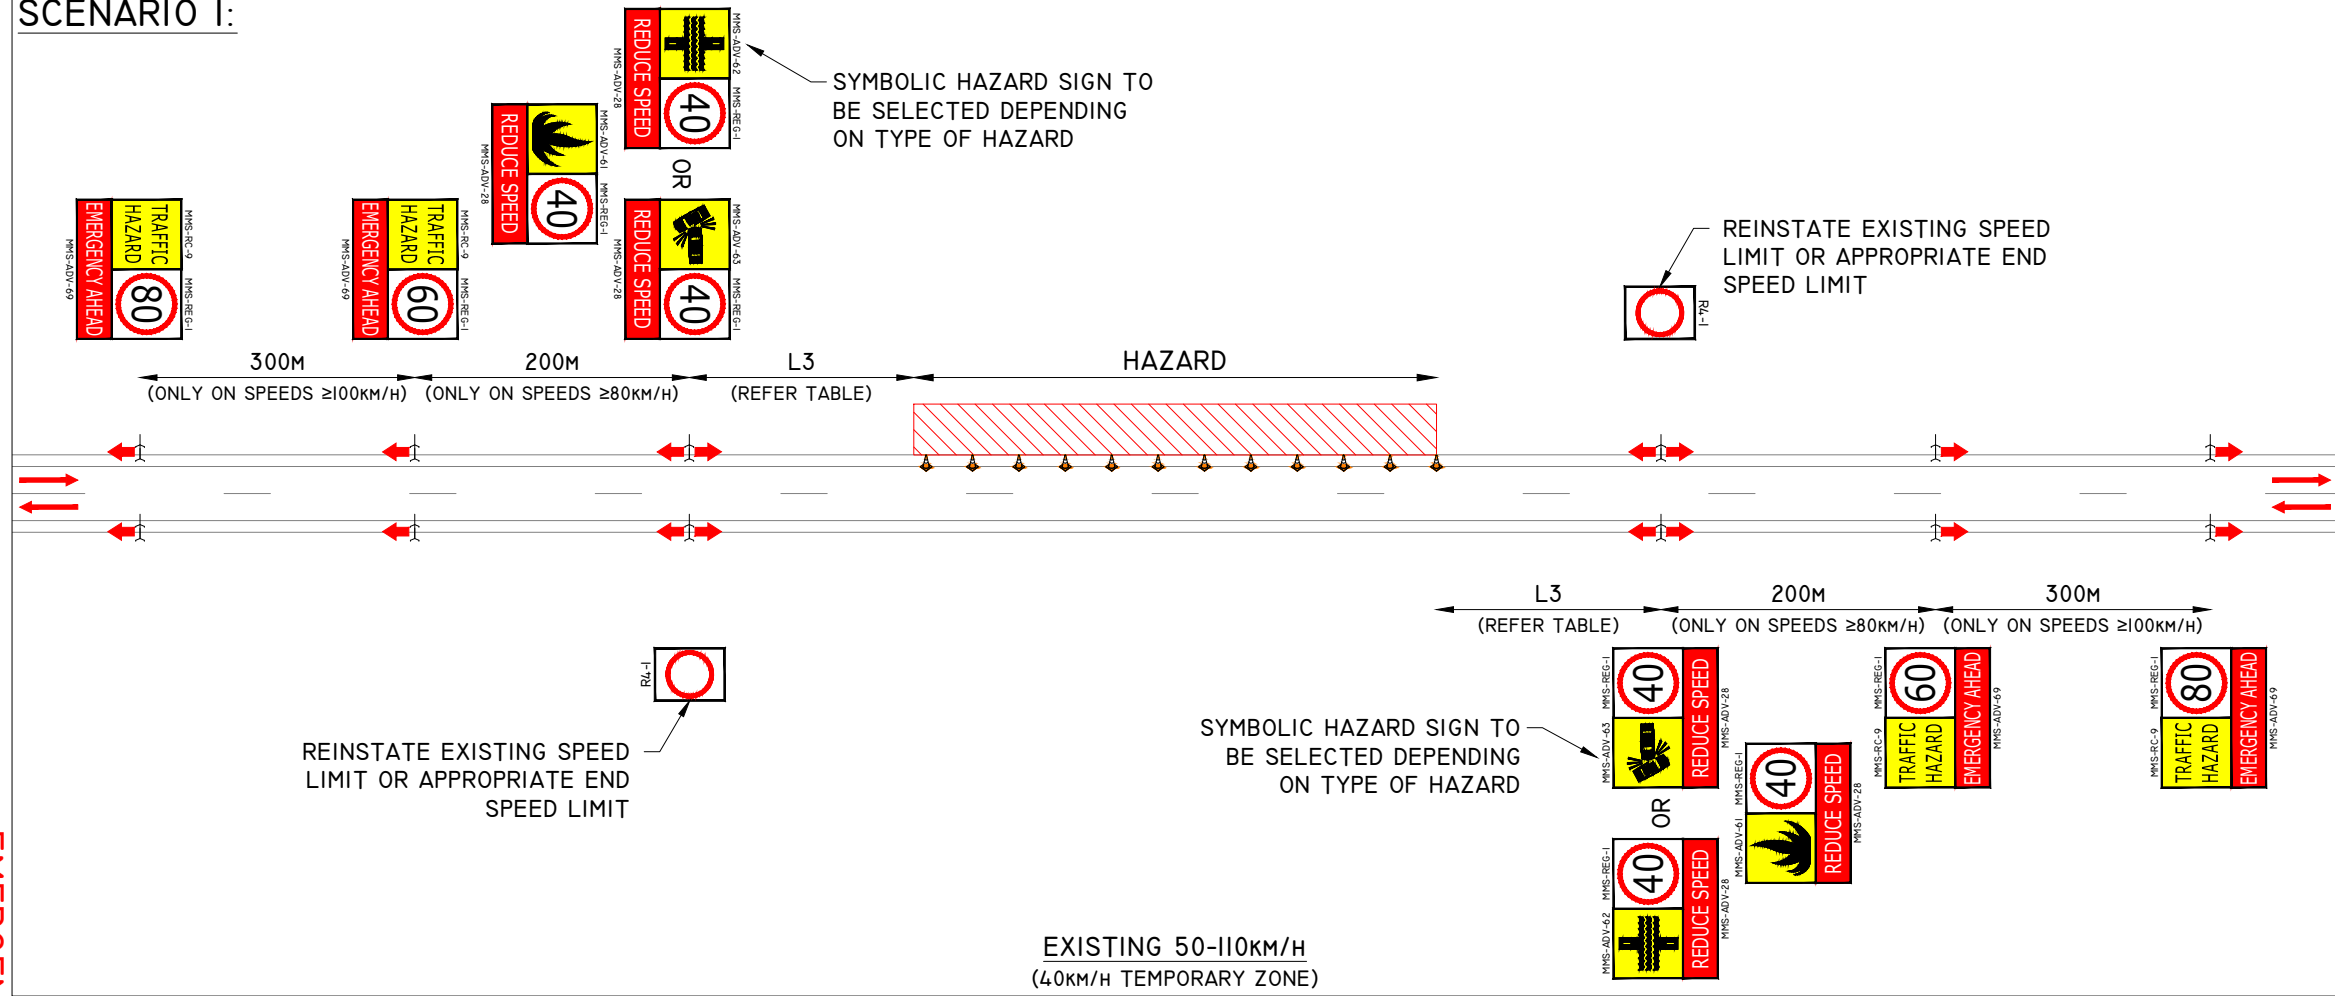

SCENARIO 2:

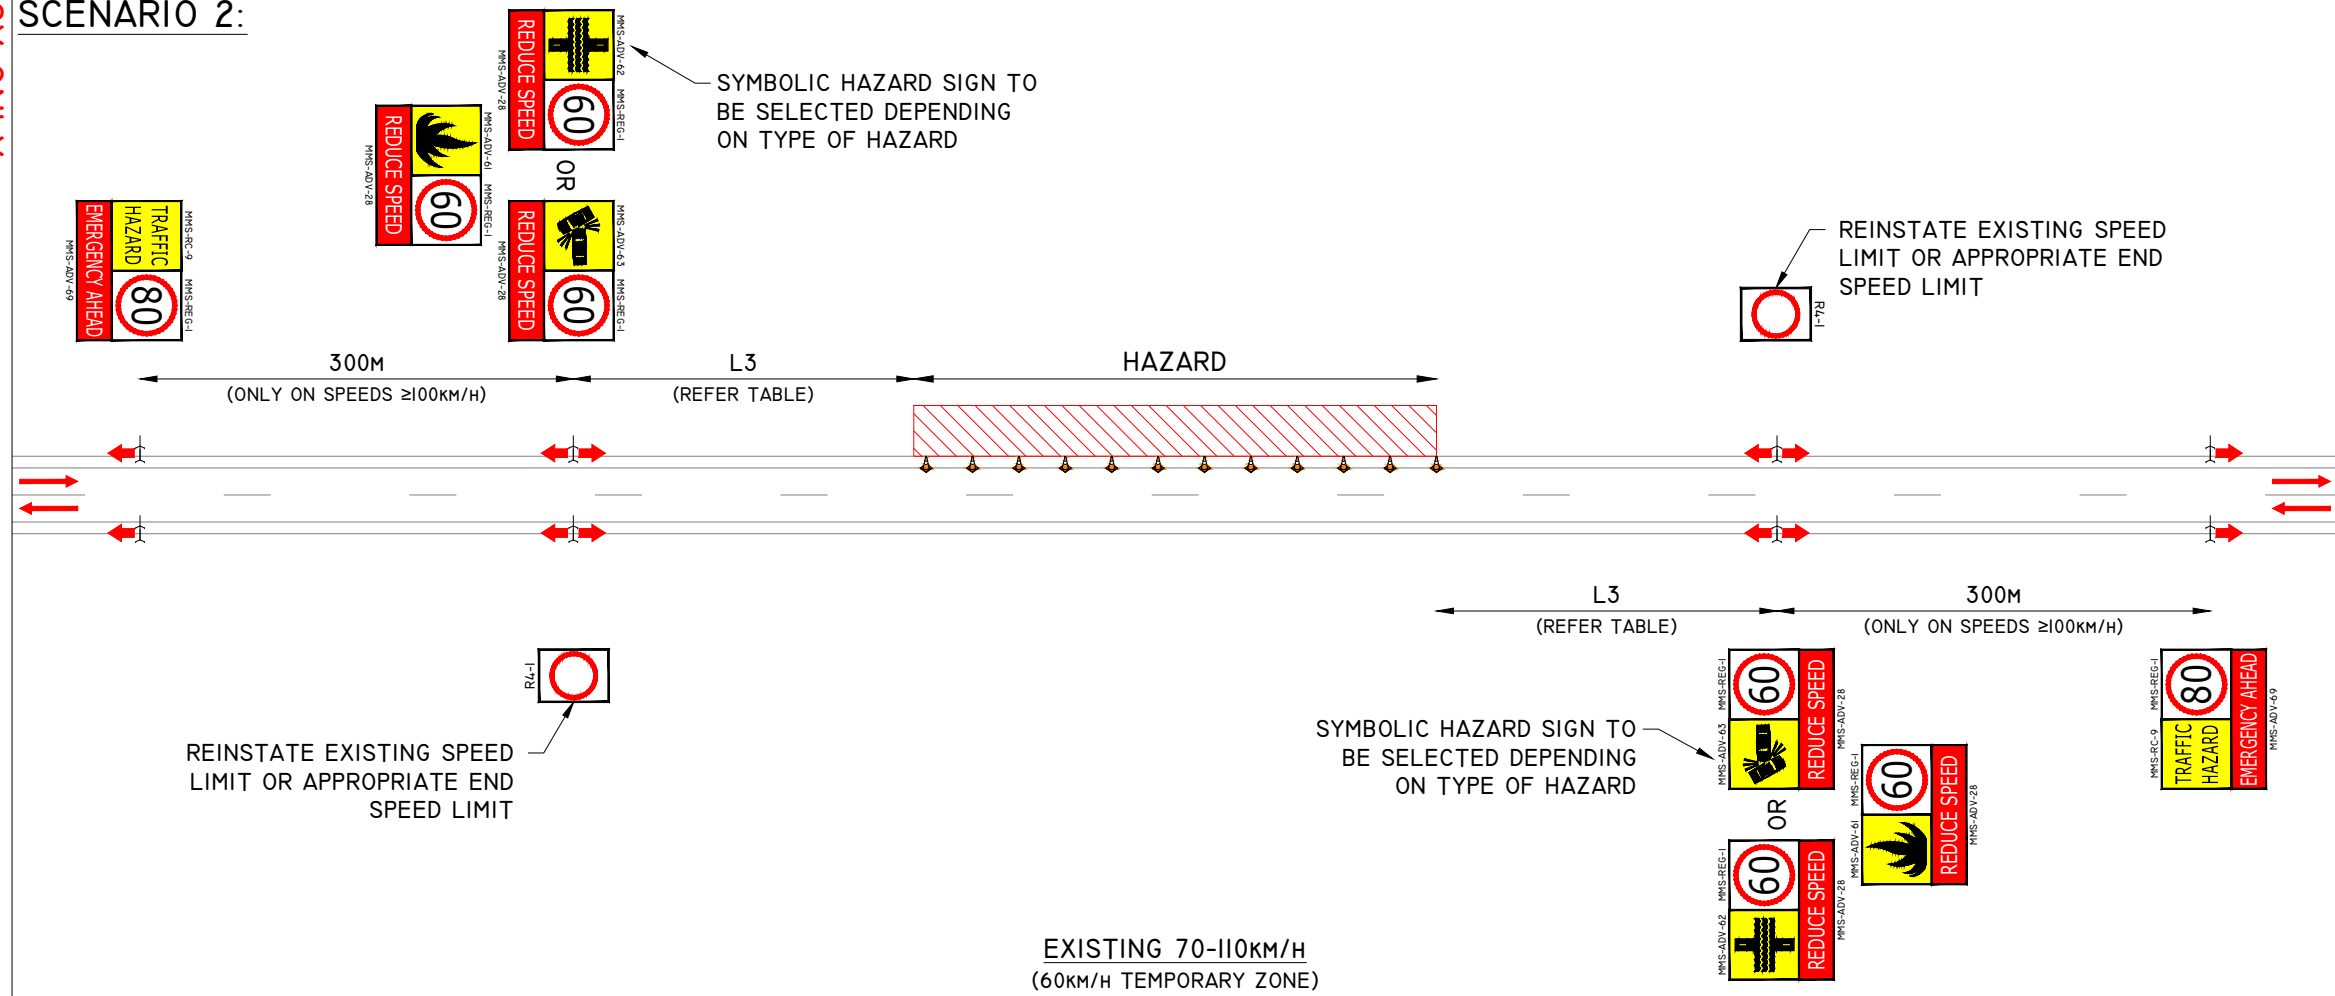

NOTES

- TOLERANCES:
POSITION OF SIGNS:
MINIMUM 10% LESS THAN THE DISTANCE OR LENGTHS GIVEN.
MAXIMUM 25% MORE THAN THE DISTANCES OR LENGTHS GIVEN.
SPACING OF DELINEATING DEVICES:
MAXIMUM 10% MORE THAN THE SPACING GIVEN.
NO MINIMUM.
AGTTM PART 6 SECTION 6.8.
DOCUMENTATION
ON-SITE VARIATIONS MUST BE APPROVED BY THE TRAFFIC MANAGEMENT SUPERVISOR, THAN AN ON-SITE VARIATION MADE AND CHANGES RECORDED IN THE DAILY DAIRY. FOR MORE INFORMATION REFER TO SECTION 9.3 OF THE TMP.
1. PLAN TO BE USED FOR EMERGENCY WORKS ONLY.
 2. TCs MAY BE USED ON SITE WHERE EMERGENCY ENCROACHES INTO LIVE LANES.
 3. ADDITIONAL CONES MAY BE DELIVERED TO SITE DEPENDING ON LENGTH OF EMERGENCY SETUP.
 4. 'STOP HERE WHEN DIRECTED' SIGNAGE TO BE INSTALLED IF AVAILABLE ON SITE.

TABLES

SIGN SPACING

AGTTM PART 3 - TABLE 2.2

SPEED LIMIT (KM/H)	DISTANCE ('D') (M)
55 OR LESS	15
56 TO 65	45
GREATER THAN 65	EQUAL TO SPEED OF TRAFFIC IN KM/H

MAIN ROADS WA CoP SECTION 6.5.2 - TABLE 6

SPEED LIMIT (KM/H)	L3 (TEMPORARY 40KM/H) (M)
60 OR LESS	45
70	70
80 OR GREATER	90

SPEED LIMIT (KM/H)	L3 (TEMPORARY 60KM/H) (M)
70	70
80	160
90	180
100 & 110	160

LEGEND

- EXISTING ROAD
PROPOSED CONES
HAZARD



METROPOLITAN REGIONS
TRAFFIC MANAGEMENT BRANCH
WATERLOO CRESCENT
TELEPHONE (08) 138 138
EAST PERTH 6004

DATE OF DRAWING 2025 JULY	SCALE -
STRAIGHT LINE KILOMETERS (SLK) -	POSTED SPEED -
ROAD AUTHORITY MRWA	WORKSITE SPEED -
CHECKED BY TYLER HARTLEY	SIGNATURE Tyler Hartley
ACCREDITATION RTM-0066	
DESIGNED BY MICHAEL REED	SIGNATURE Michael Reed
ACCREDITATION AWTM-23-11536-02	

GENERIC TRAFFIC GUIDANCE SCHEME
EMERGENCY WORK SCENARIOS
VERGE WORKS
TWO WAY ROAD

DRAWING NO 0922-01531-EW-016	REVISION 6
---------------------------------	---------------