



SCENARIO 1:

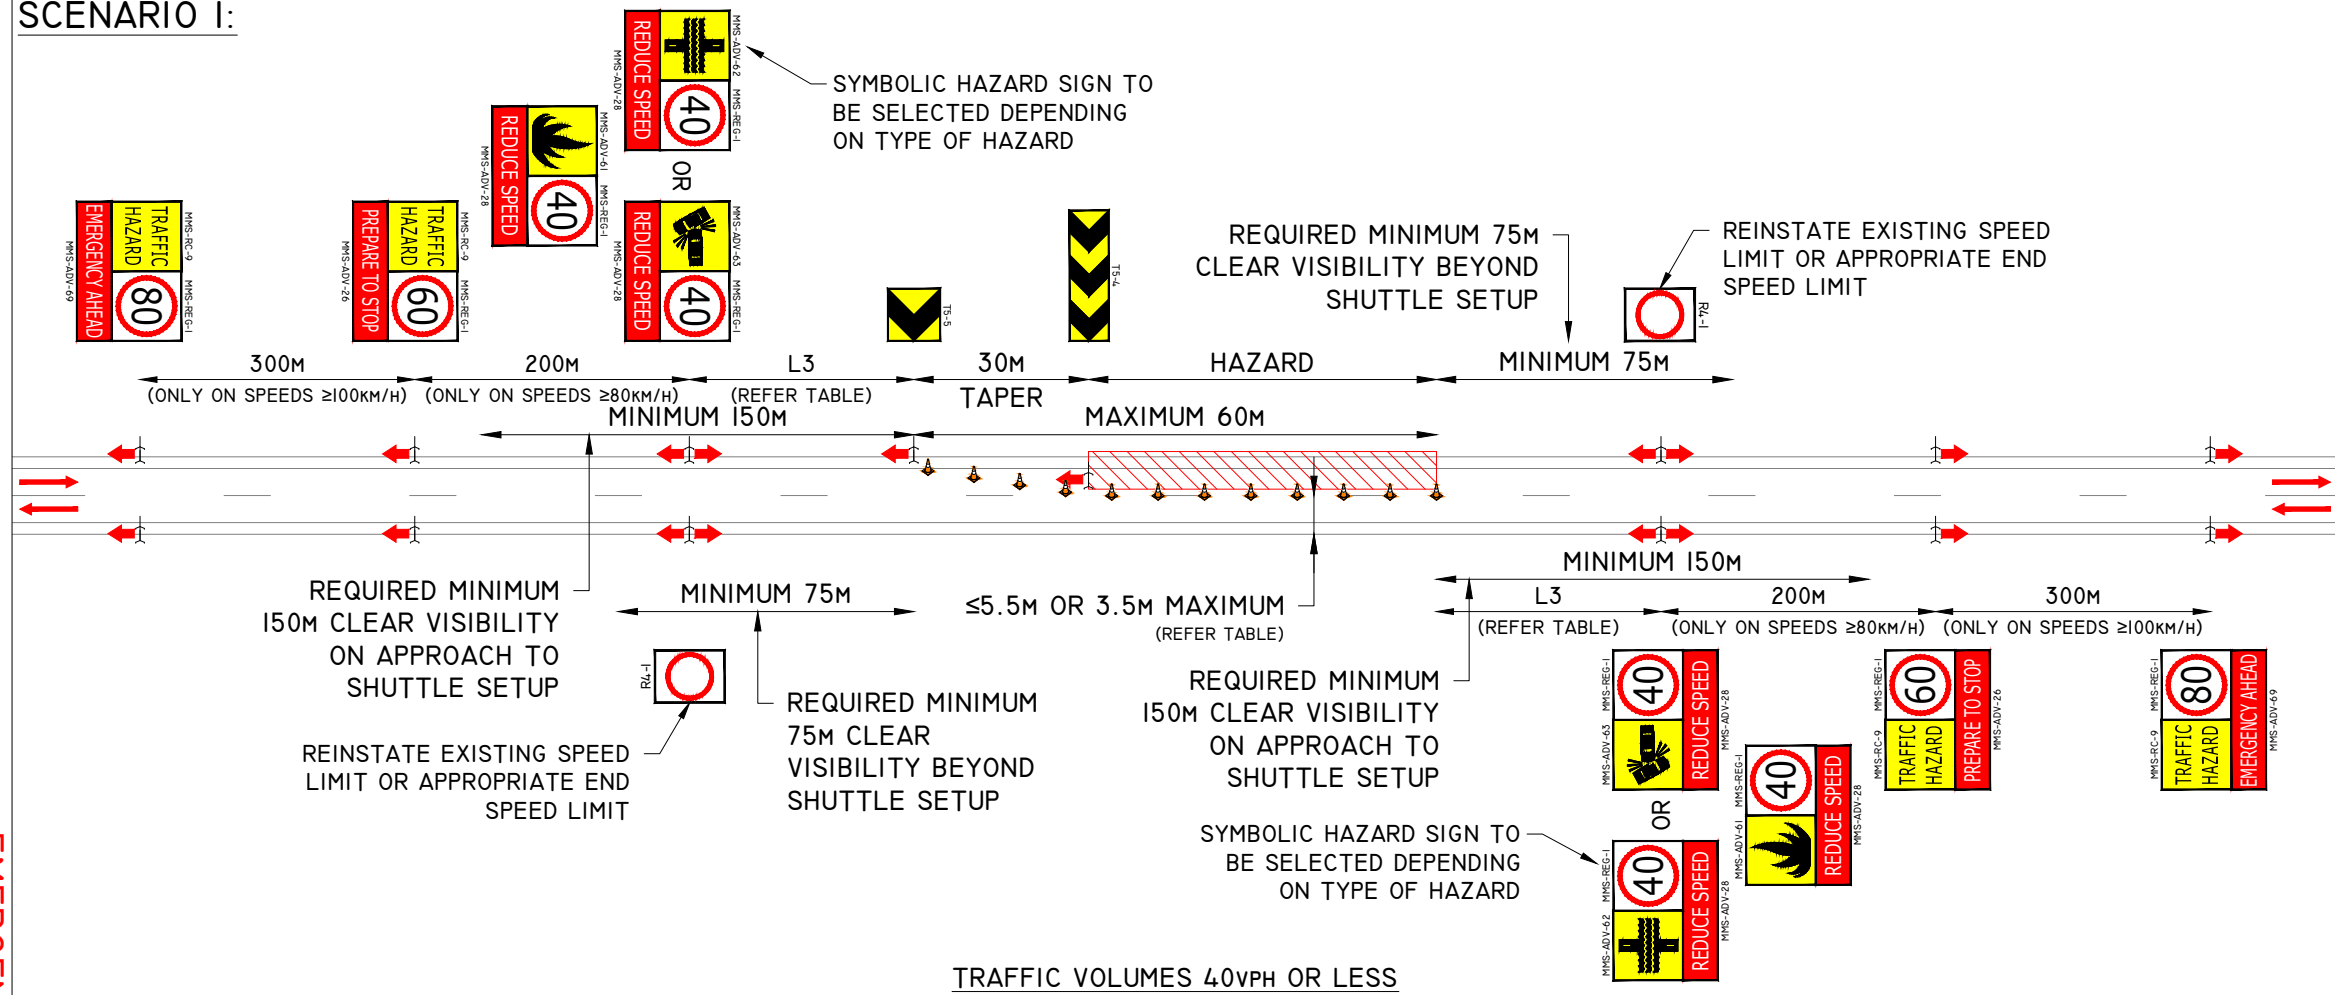

SCENARIO 2:

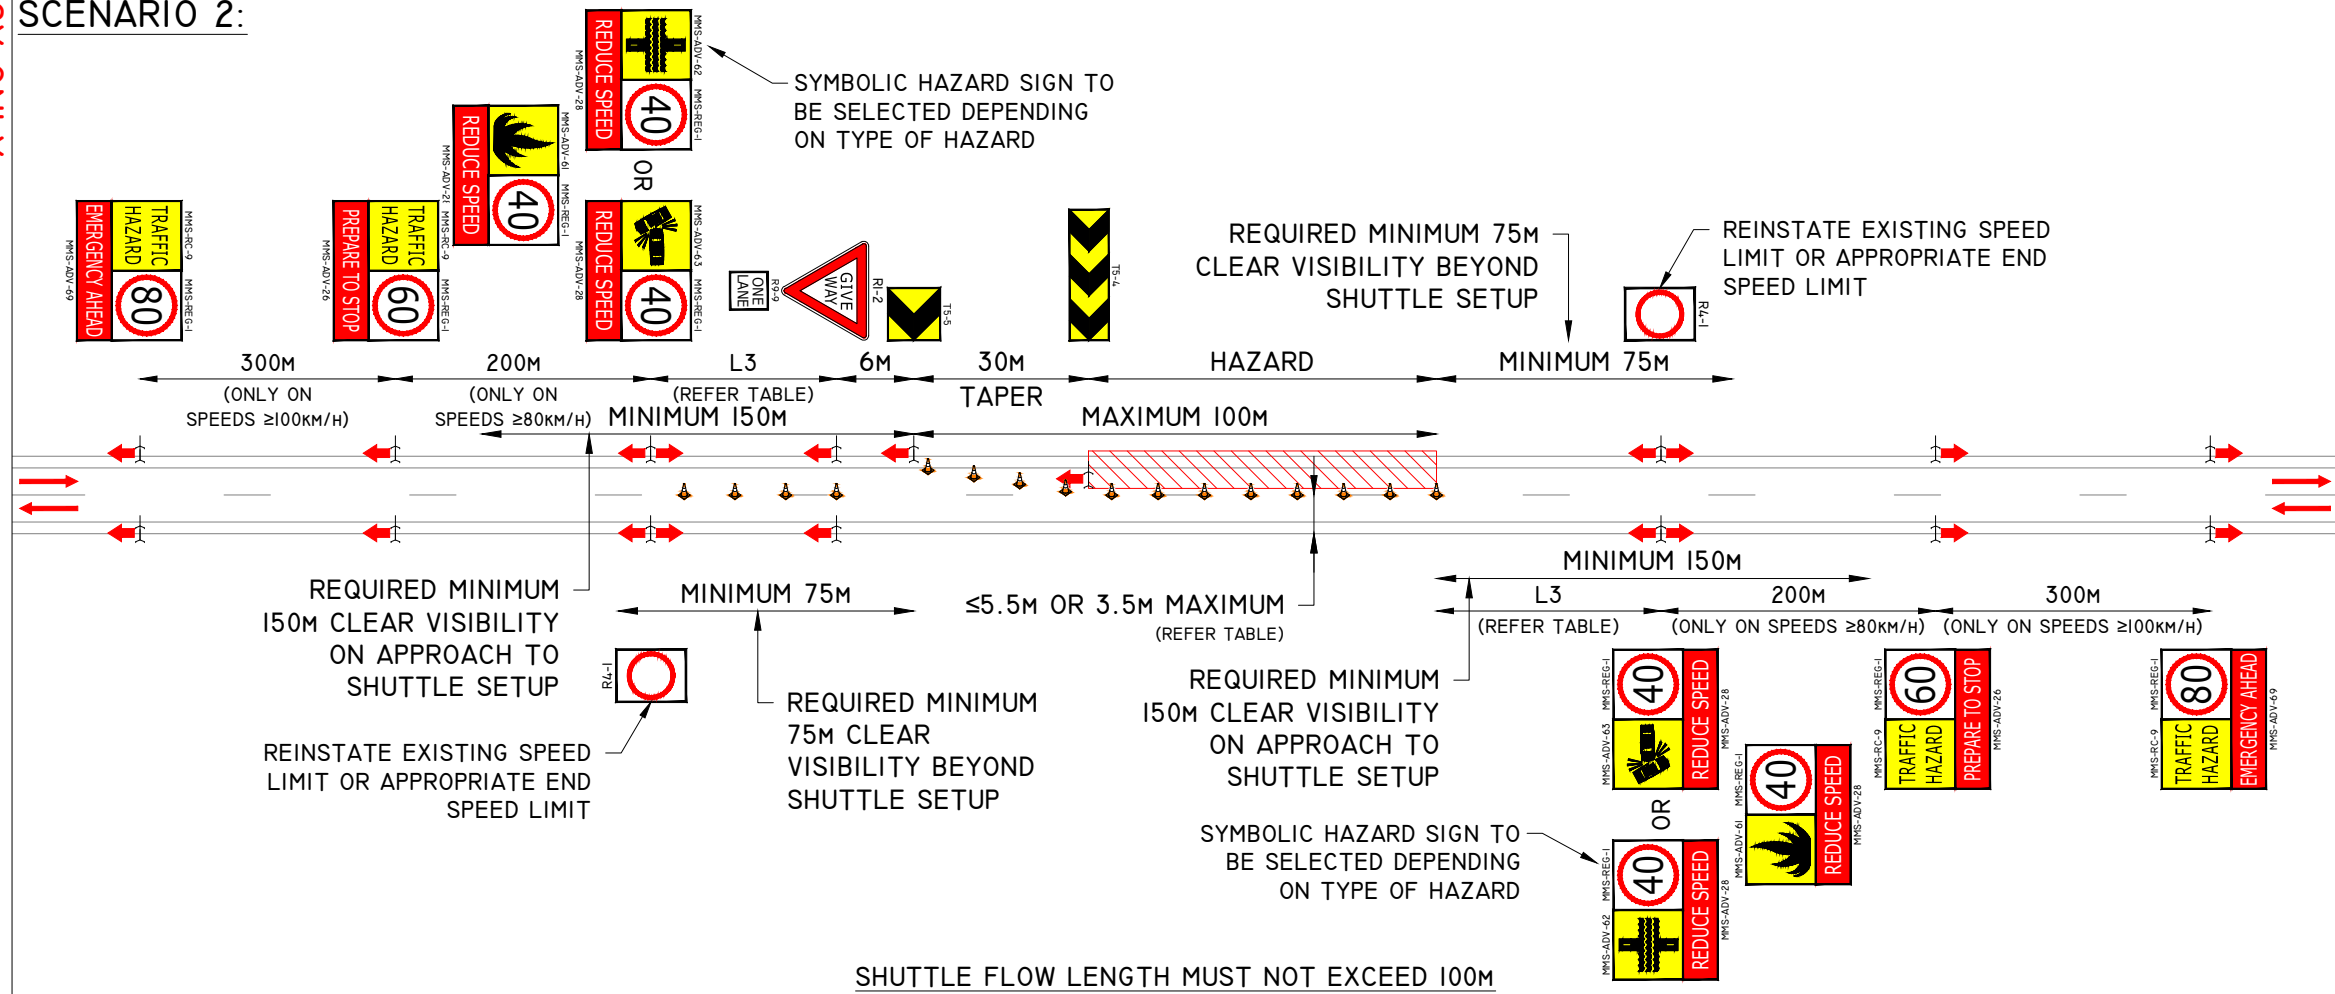

NOTES

- TOLERANCES:
POSITION OF SIGNS:
MINIMUM 10% LESS THAN THE DISTANCE OR LENGTHS GIVEN.
MAXIMUM 25% MORE THAN THE DISTANCES OR LENGTHS GIVEN.
SPACING OF DELINEATING DEVICES:
MAXIMUM 10% MORE THAN THE SPACING GIVEN.
NO MINIMUM.
AGTTM PART 6 SECTION 6.8.
- DOCUMENTATION
ON-SITE VARIATIONS MUST BE APPROVED BY THE TRAFFIC MANAGEMENT SUPERVISOR, THAN AN ON-SITE VARIATION MADE AND CHANGES RECORDED IN THE DAILY DAIRY. FOR MORE INFORMATION REFER TO SECTION 9.3 OF THE TMP.
1. PLAN TO BE USED FOR EMERGENCY WORKS ONLY.
 2. THIS PLAN IS ONLY TO BE USED AS A FIRST RESPONSE TO AN EMERGENCY AND AS SOON AS POSSIBLE REPLACED BY PTD STOP/SLOW SCENARIOS AS PER TGS-EW-005.
 3. WHERE A 5.5M+ LANE CAN BE PROVIDED, TWO WAY TRAFFIC MAY BE ALLOWED. IF THE WIDTH CANNOT BE MAINTAINED, THE WIDTH SHOULD BE REDUCED TO A MAXIMUM OF 3.5M TO ENSURE VEHICLES OPERATE IN A SINGLE FILE UNDER SHUTTLE WORKING CONDITIONS.
 4. WHERE TRAFFIC IS OPERATING UNDER A SHUTTLE SITUATION TRAFFIC REQUIRES CLEAR VISIBILITY PAST THE WORKSITE FOR 75M AND THE WORKSITE MUST NOT EXCEED 60M IN LENGTH. A MINIMUM 150M MUST BE PROVIDED FOR ROAD USERS ON THE APPROACH TO THE SHUTTLE FLOW.
 5. WHERE THE WORKSITE LENGTHS REQUIRES EXTENSION TO MAXIMUM 100M A GIVE WAY AND ONE WAY SIGN MUST BE PROVIDED AT ONE END OF THE SHUTTLE FLOW.

TABLES

SIGN SPACING

AGTTM PART 3 - TABLE 2.2

SPEED LIMIT (KM/H)	DISTANCE ('D') (M)
55 OR LESS	15
56 TO 65	45
GREATER THAN 65	EQUAL TO SPEED OF TRAFFIC IN KM/H
MAIN ROADS WA CoP SECTION 6.5.2 - TABLE 6	
SPEED LIMIT (KM/H)	L3 (M)
60 OR LESS	45
70	70
80 OR GREATER	90

LEGEND

- EXISTING ROAD
PROPOSED CONES
HAZARD



METROPOLITAN REGIONS
TRAFFIC MANAGEMENT BRANCH
WATERLOO CRESCENT
TELEPHONE (08) 138 138
EAST PERTH 6004

DATE OF DRAWING	2025 JULY	SCALE	-
STRAIGHT LINE KILOMETERS (SLK)	-	POSTED SPEED	-
ROAD AUTHORITY	MRWA	WORKSITE SPEED	-
CHECKED BY	TYLER HARTLEY	SIGNATURE	<i>Tyler Hartley</i>
ACCREDITATION	RTM-0066	SIGNATURE	<i>Michael Reed</i>
DESIGNED BY	MICHAEL REED	SIGNATURE	<i>Michael Reed</i>
ACCREDITATION	AWTM-23-11536-02	SIGNATURE	<i>Michael Reed</i>
GENERIC TRAFFIC GUIDANCE SCHEME EMERGENCY WORK SCENARIOS SHUTTLE FLOW TWO WAY ROAD		DRAWING NO	0922-01531-EW-017
		REVISION	6