
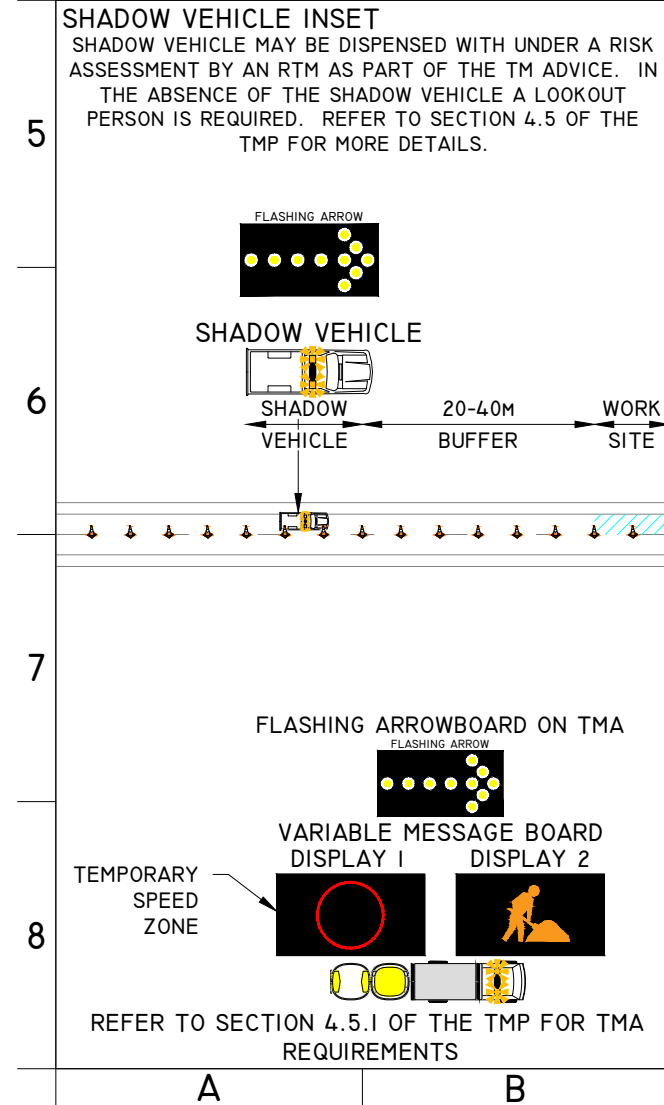


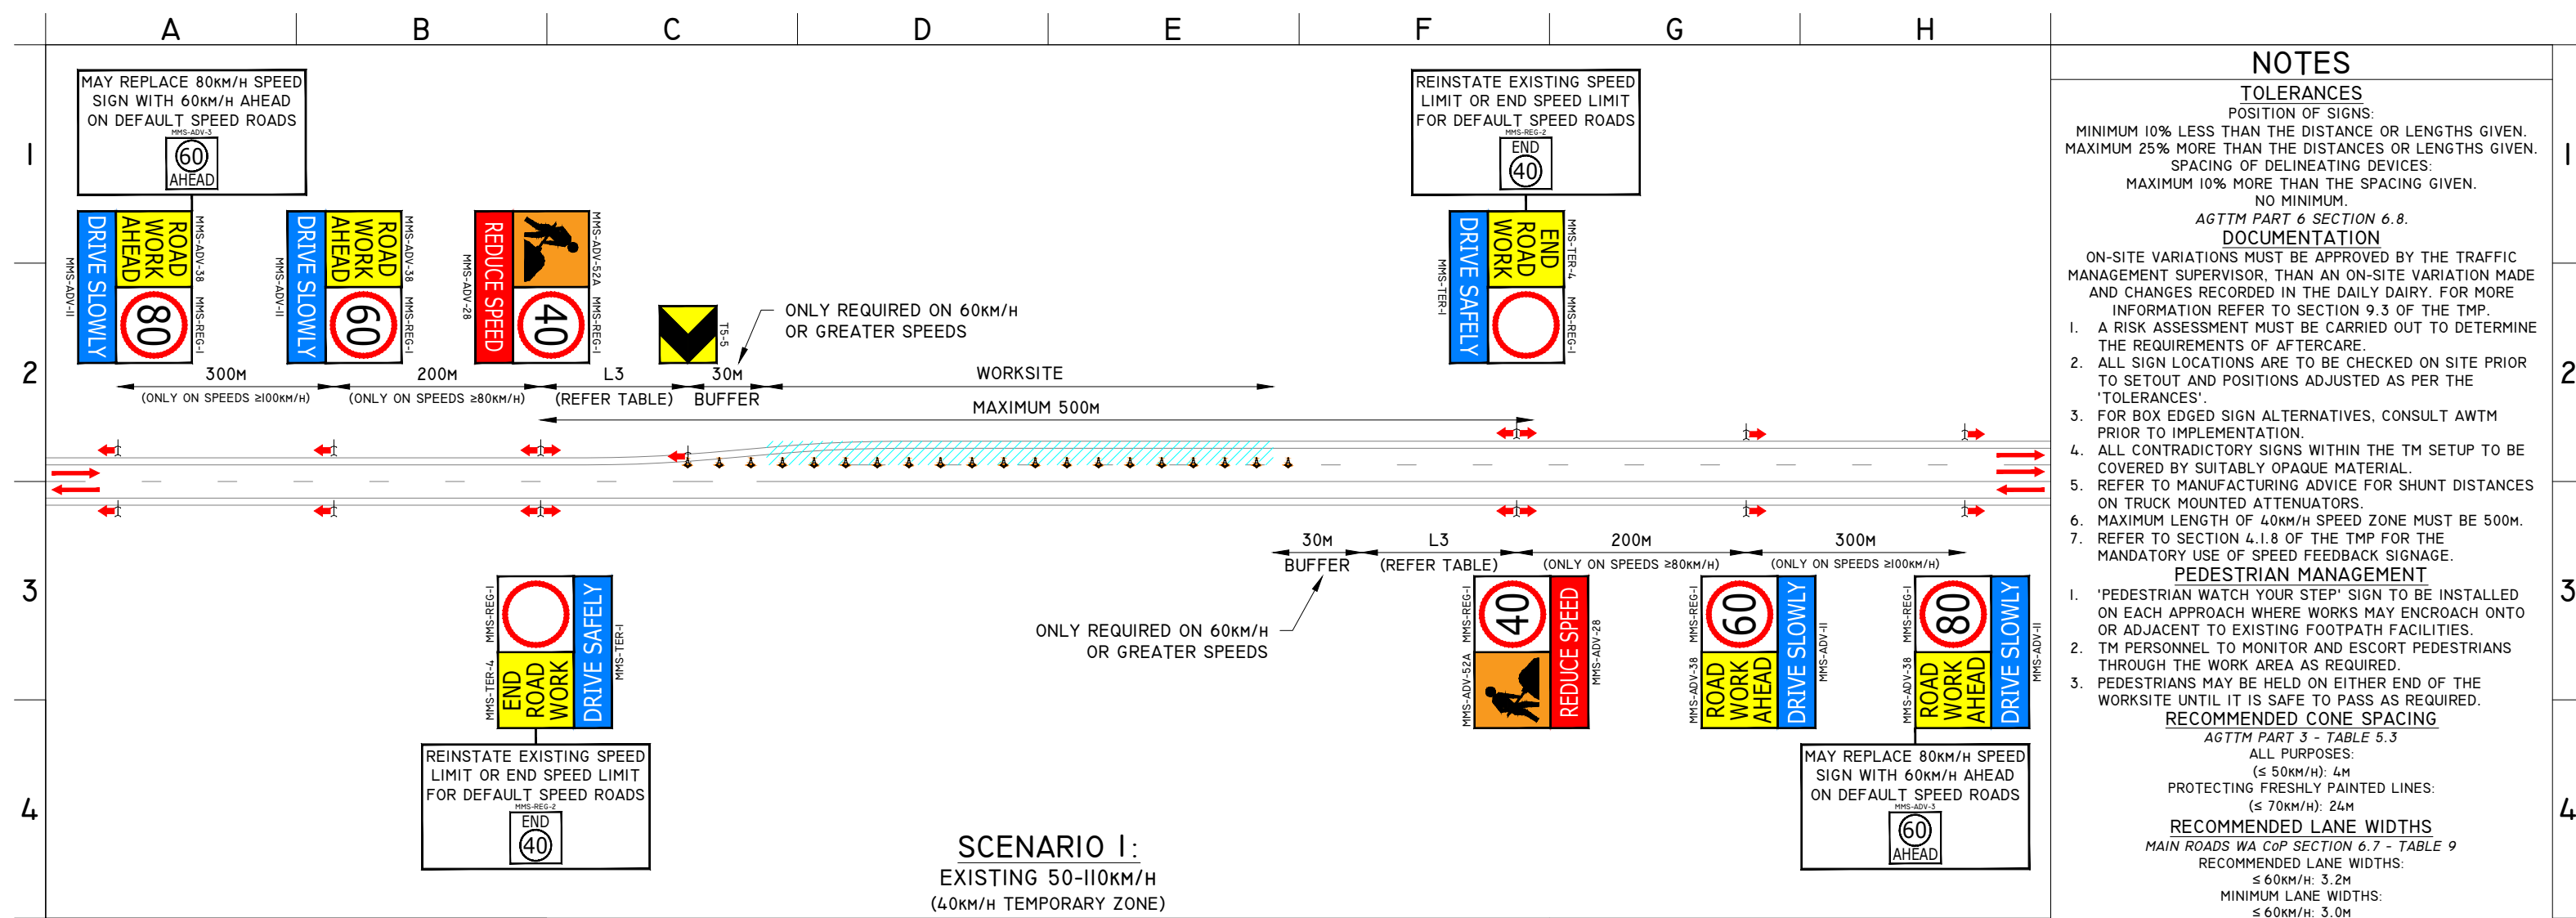

TABLES SIGN SPACING <i>MAIN ROADS WA CoP SECTION 6.5.2 - TABLE 6</i>	
SPEED LIMIT (KM/H)	L3 (M)
60 OR LESS	45
70	70
80 OR GREATER	90

		5
LEGEND		
 EXISTING ROAD  PROPOSED CONES  WORKSITE		
  METROPOLITAN REGIONS TRAFFIC MANAGEMENT BRANCH WATERLOO CRESCENT TELEPHONE (08) 138 138 EAST PERTH 6004		
DATE OF DRAWING 2025 JULY		SCALE -
LOCAL GOVERNMENT AUTHORITY -		POSTED SPEED 50-110km/h
ROAD AUTHORITY MAIN ROADS WA		WORKSITE SPEED 40km/h
CHECKED BY TYLER HARTLEY		SIGNATURE 
ACCREDITATION RTM-0066		
DESIGNED BY MICHAEL REED		SIGNATURE 
ACCREDITATION AWTM-23-11536-02		
GENERIC TRAFFIC GUIDANCE SCHEME LANE CLOSURE SETUPS OVERTAKING LANE CLOSURE WORKSITE WITHIN 1.2M		8
DRAWING NO 0922-01531-LC-018		REVISION 6