

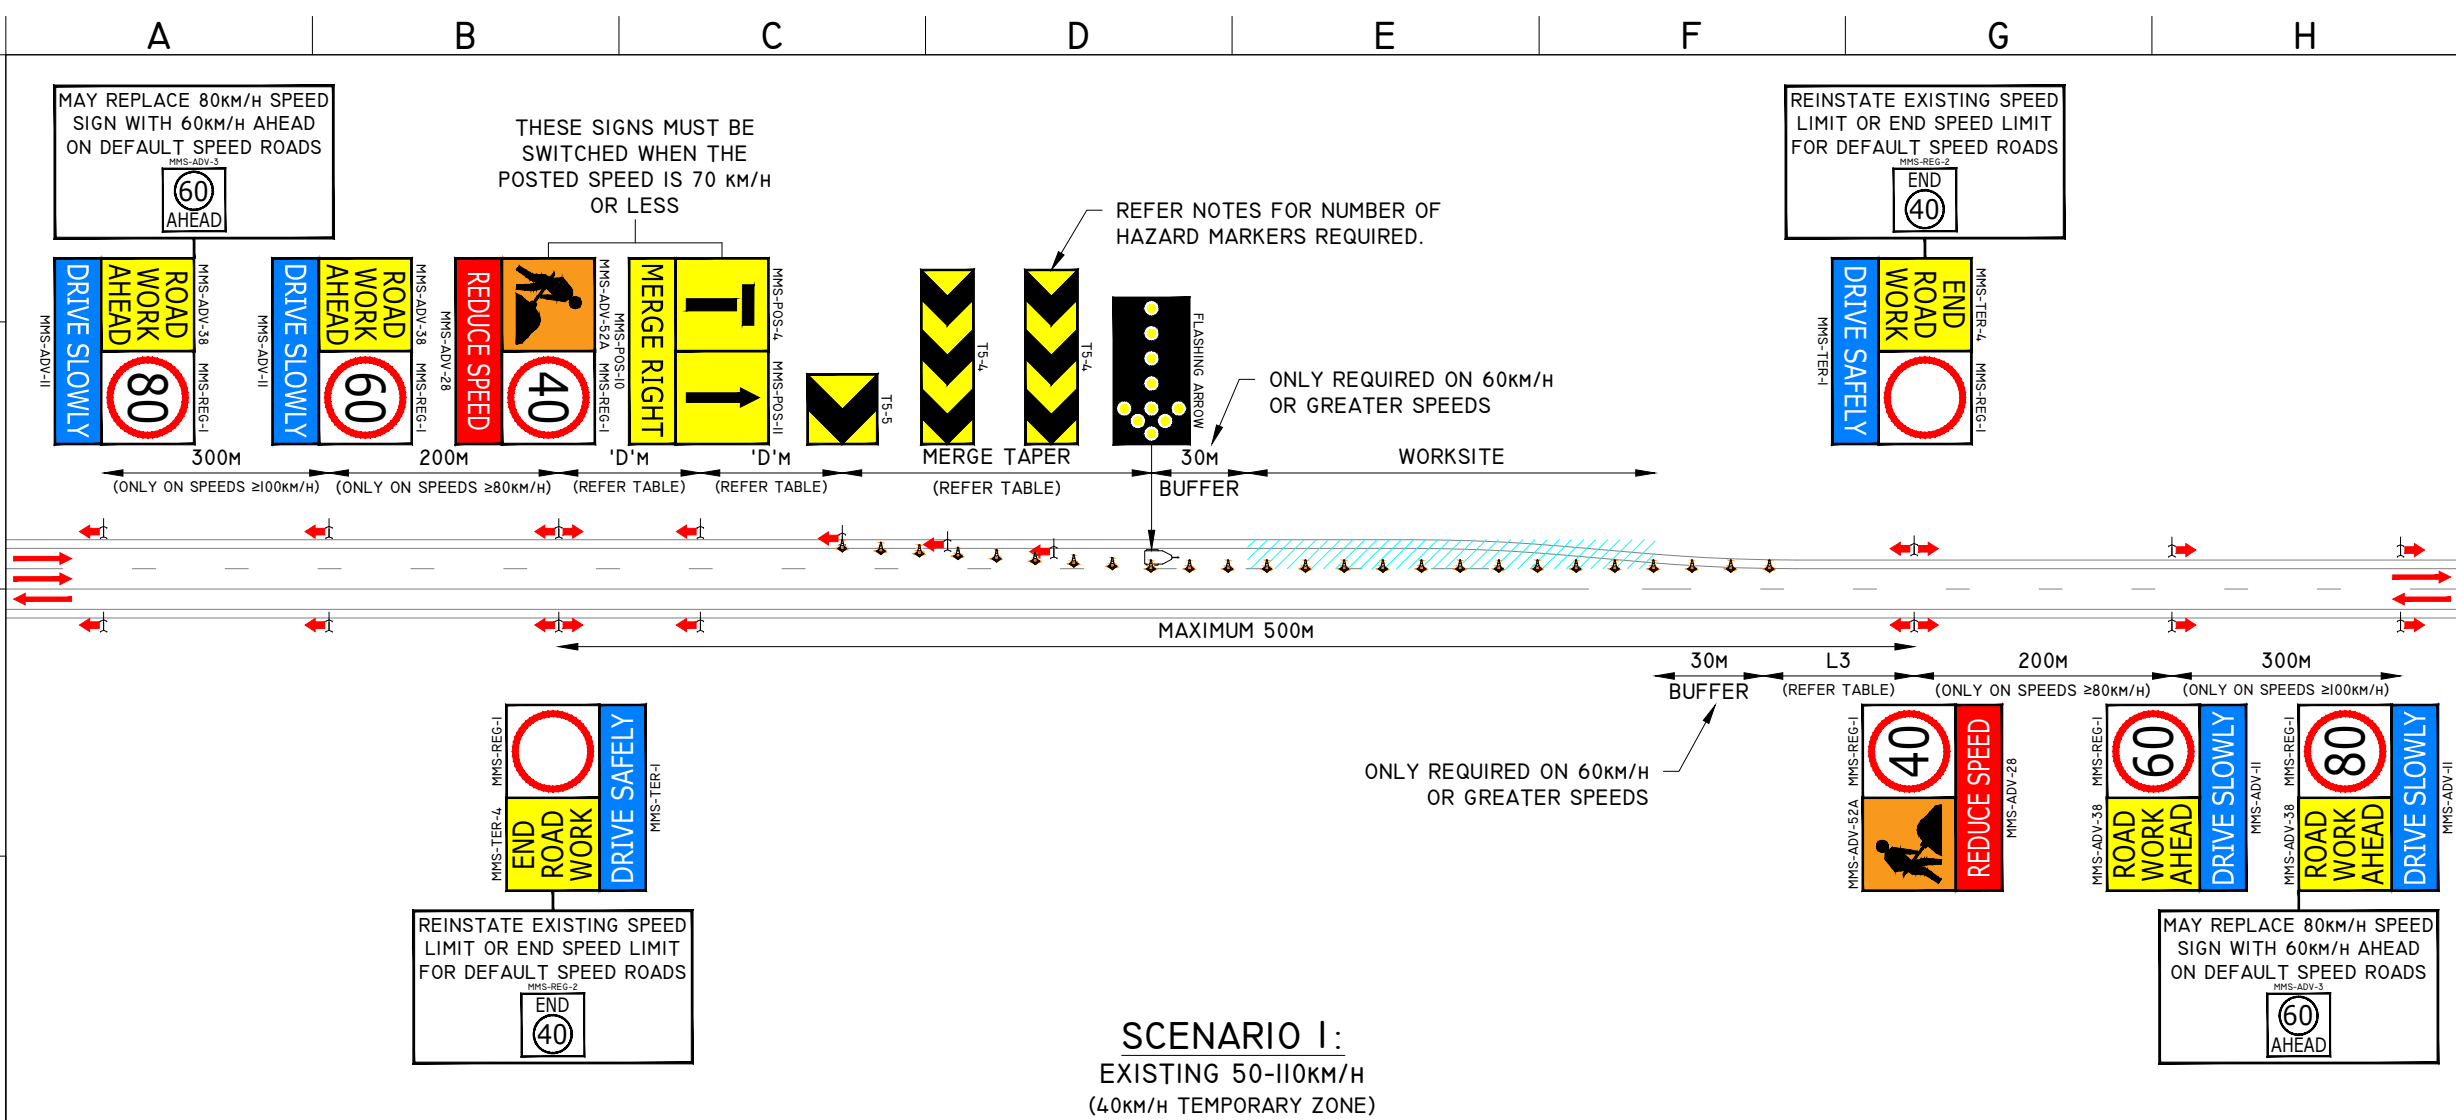


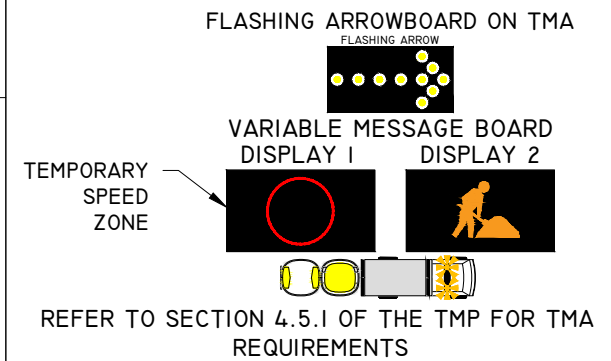

SHADOW VEHICLE INSET
SHADOW VEHICLE MAY BE DISPENSED WITH UNDER A RISK
ASSESSMENT BY AN RTM AS PART OF THE TM ADVICE. IN
THE ABSENCE OF THE SHADOW VEHICLE A LOOKOUT
PERSON IS REQUIRED. REFER TO SECTION 4.5 OF THE
TMP FOR MORE DETAILS.

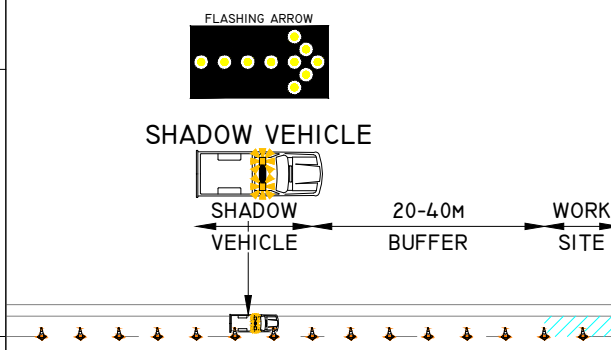

SIGN SPACING	
AGTMM PART 3 - TABLE 2.2	
SPEED LIMIT (KM/H)	DISTANCE ('D') (M)
55 OR LESS	15
56 TO 65	45
GREATER THAN 65	EQUAL TO SPEED OF TRAFFIC IN KM/H
MAIN ROADS WA CoP SECTION 6.5.2 - TABLE 6	
SPEED LIMIT (KM/H)	L3 (M)
60 OR LESS	45
70	70
80 OR GREATER	90

TABLES TAPER LENGTHS AGTMM PART 3 - TABLE 5.7		
SPEED LIMIT (KM/H)		MERGE TAPER (M)
45 OR LESS		15
46 TO 55		30
56 TO 65		60
66 TO 75*		115
76 TO 85*		130
86 TO 95*		145
96 TO 105*		160
GREATER THAN 105*		180
*TAPER LENGTHS ARE BASED ON A: • 3.5M WIDTH OF THE LANE TO BE CLOSED • MERGE TAPER LENGTH EQUAL TO 0.6M/s • MEDIAN SPEED FOR EACH RANGE (I.E 76 - 85 = 80KM/H)		
TEMPORARY HAZARD MARKERS AGTMM PART 3 - 5.4.2 PAGE 65		
A CONTINUOUS LINE OF T5-4 HAZARD MARKERS MUST BE MADE USING THE FOLLOWING RECOMMENDED NUMBERS.  T5-4	NUMBER OF SHIFT MARKERS	LENGTH OF TAPER
	2	≤60M
	4	≤115M
	6	≤130M
	8	≤145M
	EVERY 20M	>145M
		WITHIN A CLOSED LANE

[illegible]

NOTES

TOLERANCES

POSITION OF SIGNS:

MINIMUM 10% LESS THAN THE DISTANCE OR LENGTHS GIVEN.
MAXIMUM 10% MORE THAN THE DISTANCES OR LENGTHS GIVEN.

SPACING OF DELINEATING DEVICES:

MAXIMUM 10% MORE THAN THE SPACING GIVEN.
NO MINIMUM.

AGTMM PART 6 SECTION 6.8.

DOCUMENTATION

ON-SITE VARIATIONS MUST BE APPROVED BY THE TRAFFIC MANAGEMENT SUPERVISOR, THAN AN ON-SITE VARIATION MADE AND CHANGES RECORDED IN THE DAILY DAIRY. FOR MORE INFORMATION REFER TO SECTION 9.3 OF THE TMP.

1. A RISK ASSESSMENT MUST BE CARRIED OUT TO DETERMINE THE REQUIREMENTS OF AFTERCARE.
2. ALL SIGN LOCATIONS ARE TO BE CHECKED ON SITE PRIOR TO SETOUT AND POSITIONS ADJUSTED AS PER THE 'TOLERANCES'.
3. FOR BOX EDGED SIGN ALTERNATIVES, CONSULT AWTM PRIOR TO IMPLEMENTATION.
4. ALL CONTRADICTIONARY SIGNS WITHIN THE TM SETUP TO BE COVERED BY SUITABLY OPAQUE MATERIAL.
5. REFER TO MANUFACTURING ADVICE FOR SHUNT DISTANCES ON TRUCK MOUNTED ATTENUATORS.
6. MAXIMUM LENGTH OF 40km/h SPEED ZONE MUST BE 500M.
7. REFER TO SECTION 4.1.8 OF THE TMP FOR THE MANDATORY USE OF SPEED FEEDBACK SIGNAGE.

PEDESTRIAN MANAGEMENT

1. 'PEDESTRIAN WATCH YOUR STEP' SIGN TO BE INSTALLED ON EACH APPROACH WHERE WORKS MAY ENCROACH ONTO OR ADJACENT TO EXISTING FOOTPATH FACILITIES.
2. TM PERSONNEL TO MONITOR AND ESCORT PEDESTRIANS THROUGH THE WORK AREA AS REQUIRED.
3. PEDESTRIANS MAY BE HELD ON EITHER END OF THE WORKSITE UNTIL IT IS SAFE TO PASS AS REQUIRED.

RECOMMENDED CONE SPACING

AGTMM PART 3 - TABLE 5.3

ALL PURPOSES:

(≤ 50km/h): 4m

PROTECTING FRESHLY PAINTED LINES:

(≤ 70km/h): 24m

RECOMMENDED LANE WIDTHS

MAIN ROADS WA CoP SECTION 6.7 - TABLE 9

RECOMMENDED LANE WIDTHS:


≤ 60km/h: 3.2m

MINIMUM LANE WIDTHS:

≤ 60km/h: 3.0m

LEGEND

- EXISTING ROAD
- PROPOSED CONES
- WORKSITE

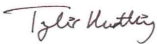 	
METROPOLITAN REGIONS TRAFFIC MANAGEMENT BRANCH	
WATERLOO CRESCENT TELEPHONE (08) 138 138	EAST PERTH 6004
DATE OF DRAWING 2025 JULY	SCALE -
LOCAL GOVERNMENT AUTHORITY -	POSTED SPEED 50-110KM/H
ROAD AUTHORITY MAIN ROADS WA	WORKSITE SPEED 40KM/H
CHECKED BY TYLER HARTLEY	SIGNATURE 
CREDITATION RTM-0066	SIGNATURE 
DESIGNED BY MICHAEL REED	
CREDITATION AWTM-23-11536-02	
GENERIC TRAFFIC GUIDANCE SCHEME LANE CLOSURE SETUPS OVERTAKING LANE CLOSURE WORKSITE WITHIN 1.2M	
DRAWING NO 0922-01531-LC-020	REVISION 6