

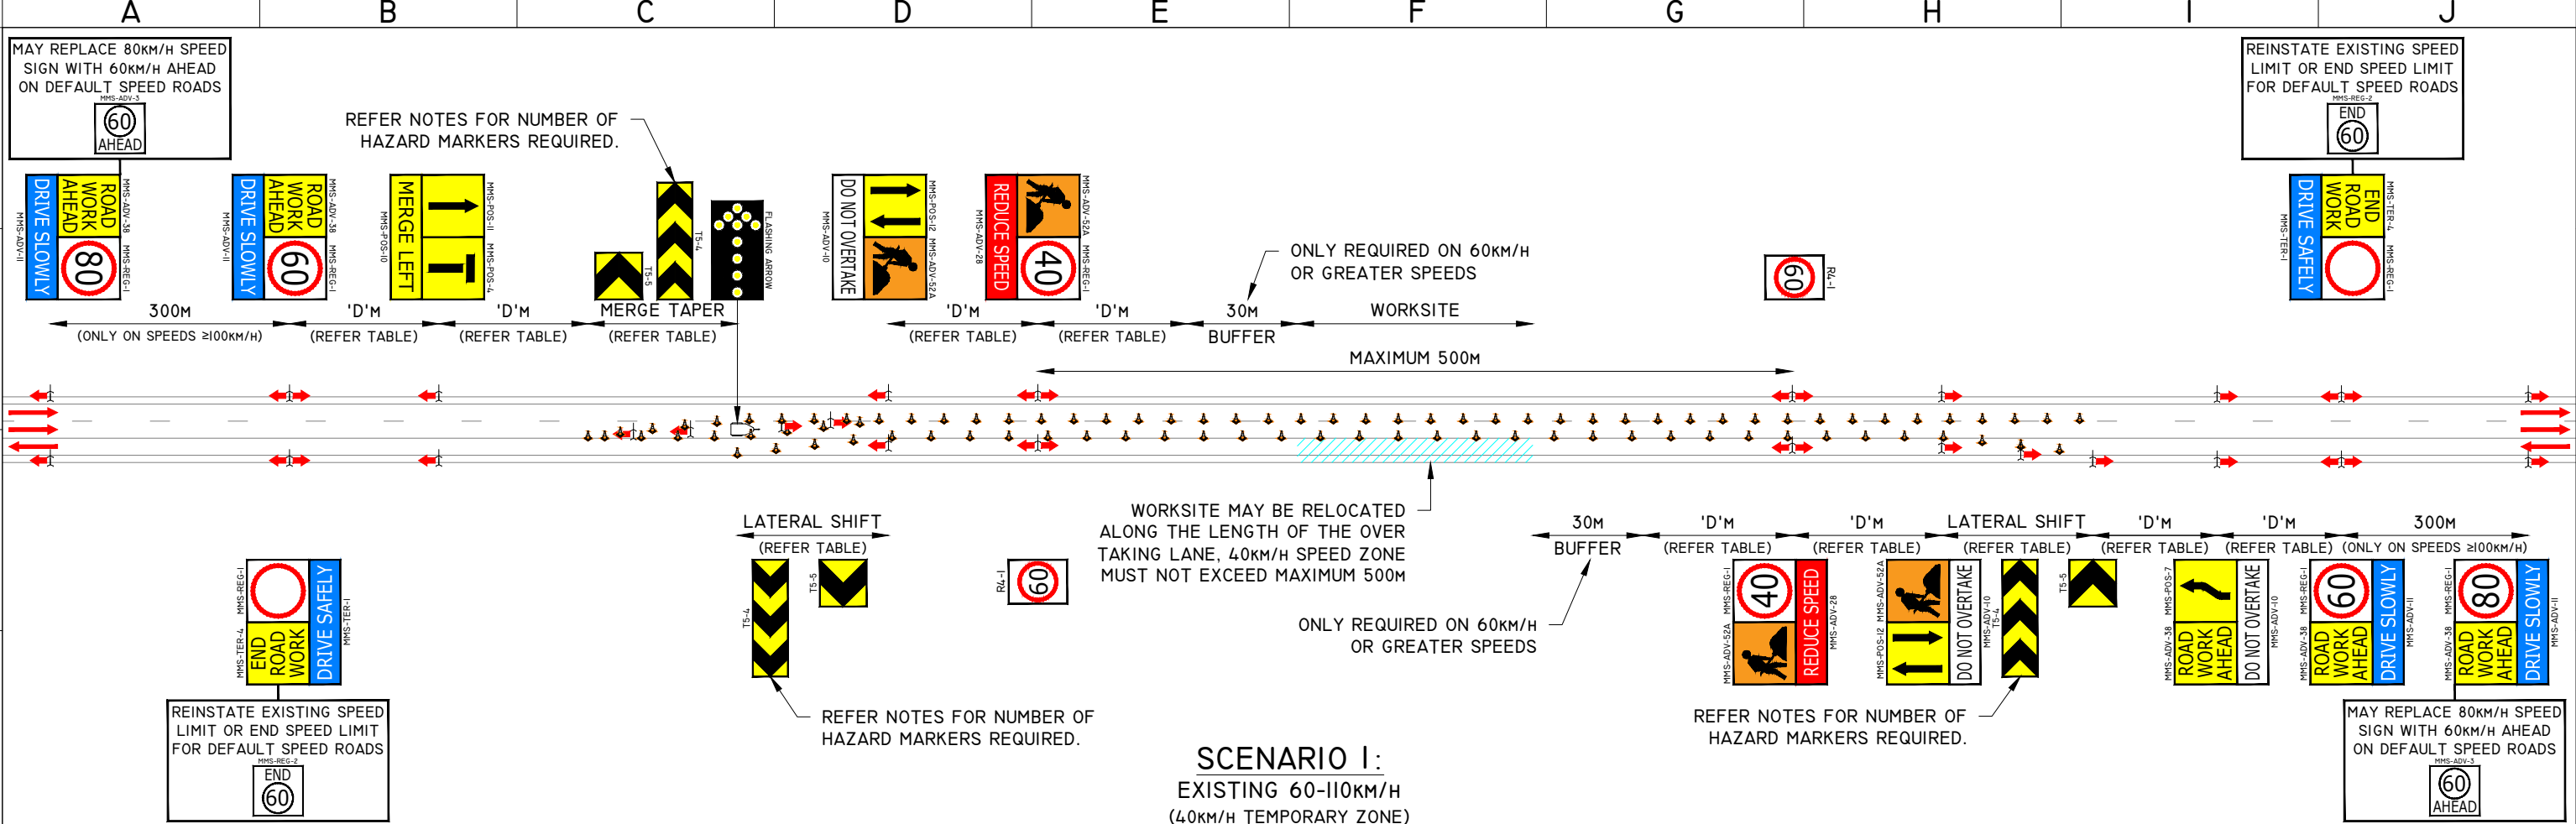


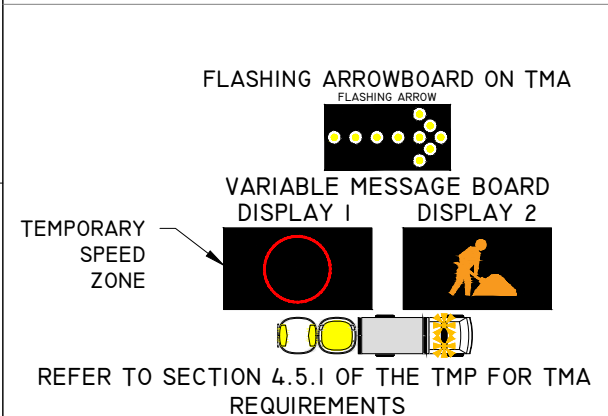

SHADOW VEHICLE INSET
SHADOW VEHICLE MAY BE DISPENSED WITH UNDER A RISK ASSESSMENT BY AN RTM AS PART OF THE TM ADVICE. IN THE ABSENCE OF THE SHADOW VEHICLE A LOOKOUT PERSON IS REQUIRED. REFER TO SECTION 4.5 OF THE TMP FOR MORE DETAILS.

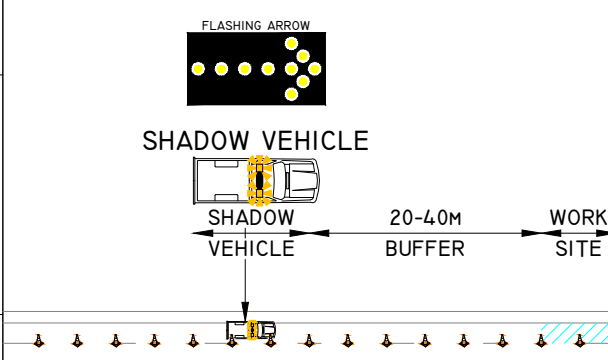

TABLES				
SIGN SPACING		TAPER LENGTHS		
AGTTM PART 3 - TABLE 2.2		AGTTM PART 3 - TABLE 5.7		
SPEED LIMIT (KM/H)	DISTANCE ('D') (M)	SPEED LIMIT (KM/H)	LATERAL SHIFT TAPER (M)	MERGE TAPER (M)
55 OR LESS	15	45 OR LESS	5	15
56 TO 65	45	46 TO 55	15	30
GREATER THAN 65	EQUAL TO SPEED OF TRAFFIC IN KM/H	56 TO 65	30	60
		66 TO 75*	70	115
		76 TO 85*	80	130
		86 TO 95*	90	145
		96 TO 105*	100	160
		GREATER THAN 105*	110	180
*TAPER LENGTHS ARE BASED ON A: 3.5m WIDTH OF THE LANE TO BE CLOSED - LATERAL SHIFT TAPER LENGTH EQUAL TO 1.0m/s - MERGE TAPER LENGTH EQUAL TO 0.6m/s				
MEDIAN SPEED FOR EACH RANGE (I.E 76 - 85 = 80KM/H)				
TEMPORARY HAZARD MARKERS				
AGTTM PART 3 - 5.4.2 PAGE 65				
A CONTINUOUS LINE OF T5-4 HAZARD MARKERS MUST BE MADE USING THE FOLLOWING RECOMMENDED NUMBERS.		NUMBER OF SHIFT MARKERS		LENGTH OF TAPER
		2		≤60M
		4		≤115M
		6		≤130M
		8		≤145M
		EVERY 20M		>145M WITHIN A CLOSED LANE

- NOTES**
- TOLERANCES**
POSITION OF SIGNS: MINIMUM 10% LESS THAN THE DISTANCE OR LENGTHS GIVEN. MAXIMUM 25% MORE THAN THE DISTANCES OR LENGTHS GIVEN. SPACING OF DELINEATING DEVICES: MAXIMUM 10% MORE THAN THE SPACING GIVEN. NO MINIMUM.
AGTTM PART 6 SECTION 6.8.
- DOCUMENTATION**
ON-SITE VARIATIONS MUST BE APPROVED BY THE TRAFFIC MANAGEMENT SUPERVISOR, THAN AN ON-SITE VARIATION MADE AND CHANGES RECORDED IN THE DAILY DAIRY. FOR MORE INFORMATION REFER TO SECTION 9.3 OF THE TMP.
- A RISK ASSESSMENT MUST BE CARRIED OUT TO DETERMINE THE REQUIREMENTS OF AFTERCARE.
 - ALL SIGN LOCATIONS ARE TO BE CHECKED ON SITE PRIOR TO SETOUT AND POSITIONS ADJUSTED AS PER THE 'TOLERANCES'.
 - FOR BOX EDGED SIGN ALTERNATIVES, CONSULT AWTM PRIOR TO IMPLEMENTATION.
 - ALL CONTRADICTORY SIGNS TO BE COVERED BY SUITABLY OPAQUE MATERIAL.
 - REFER TO MANUFACTURING ADVICE FOR SHUNT DISTANCES ON TRUCK MOUNTED ATTENUATORS.
 - MAXIMUM LENGTH OF 40KM/H SPEED ZONE MUST BE 500M.
 - REFER TO SECTION 4.1.8 OF THE TMP FOR THE MANDATORY USE OF SPEED FEEDBACK SIGNAGE
- PEDESTRIAN MANAGEMENT**
- 'PEDESTRIAN WATCH YOUR STEP' SIGN TO BE INSTALLED ON EACH APPROACH WHERE WORKS MAY ENCROACH ONTO OR ADJACENT TO EXISTING FOOTPATH FACILITIES.
 - TM PERSONNEL TO MONITOR AND ESCORT PEDESTRIANS THROUGH THE WORK AREA AS REQUIRED.
 - PEDESTRIANS MAY BE HELD ON EITHER END OF THE WORKSITE UNTIL IT IS SAFE TO PASS AS REQUIRED.
- RECOMMENDED CONE SPACING**
AGTTM PART 3 - TABLE 5.3
ALL PURPOSES:
(≤ 50KM/H): 4M
(60 - 70KM/H): 12M
PROTECTING FRESHLY PAINTED LINES:
(≤ 70KM/H): 24M
- RECOMMENDED LANE WIDTHS**
MAIN ROADS WA CoP SECTION 6.7 - TABLE 9
RECOMMENDED LANE WIDTHS:
≤ 60KM/H: 3.2M
MINIMUM LANE WIDTHS:
≤ 60KM/H: 3.0M