
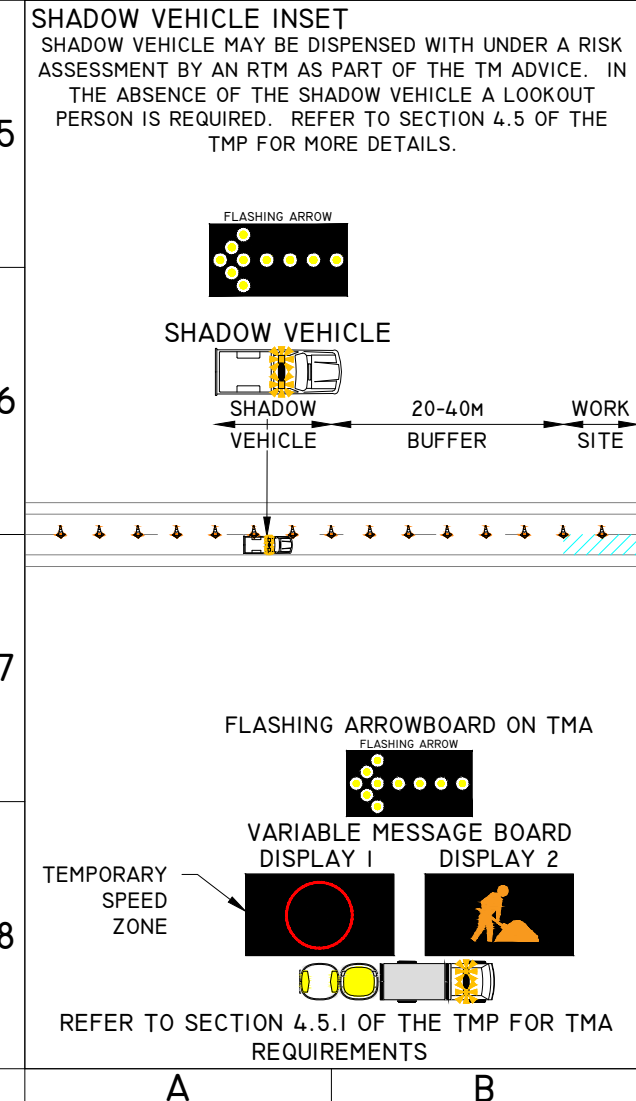


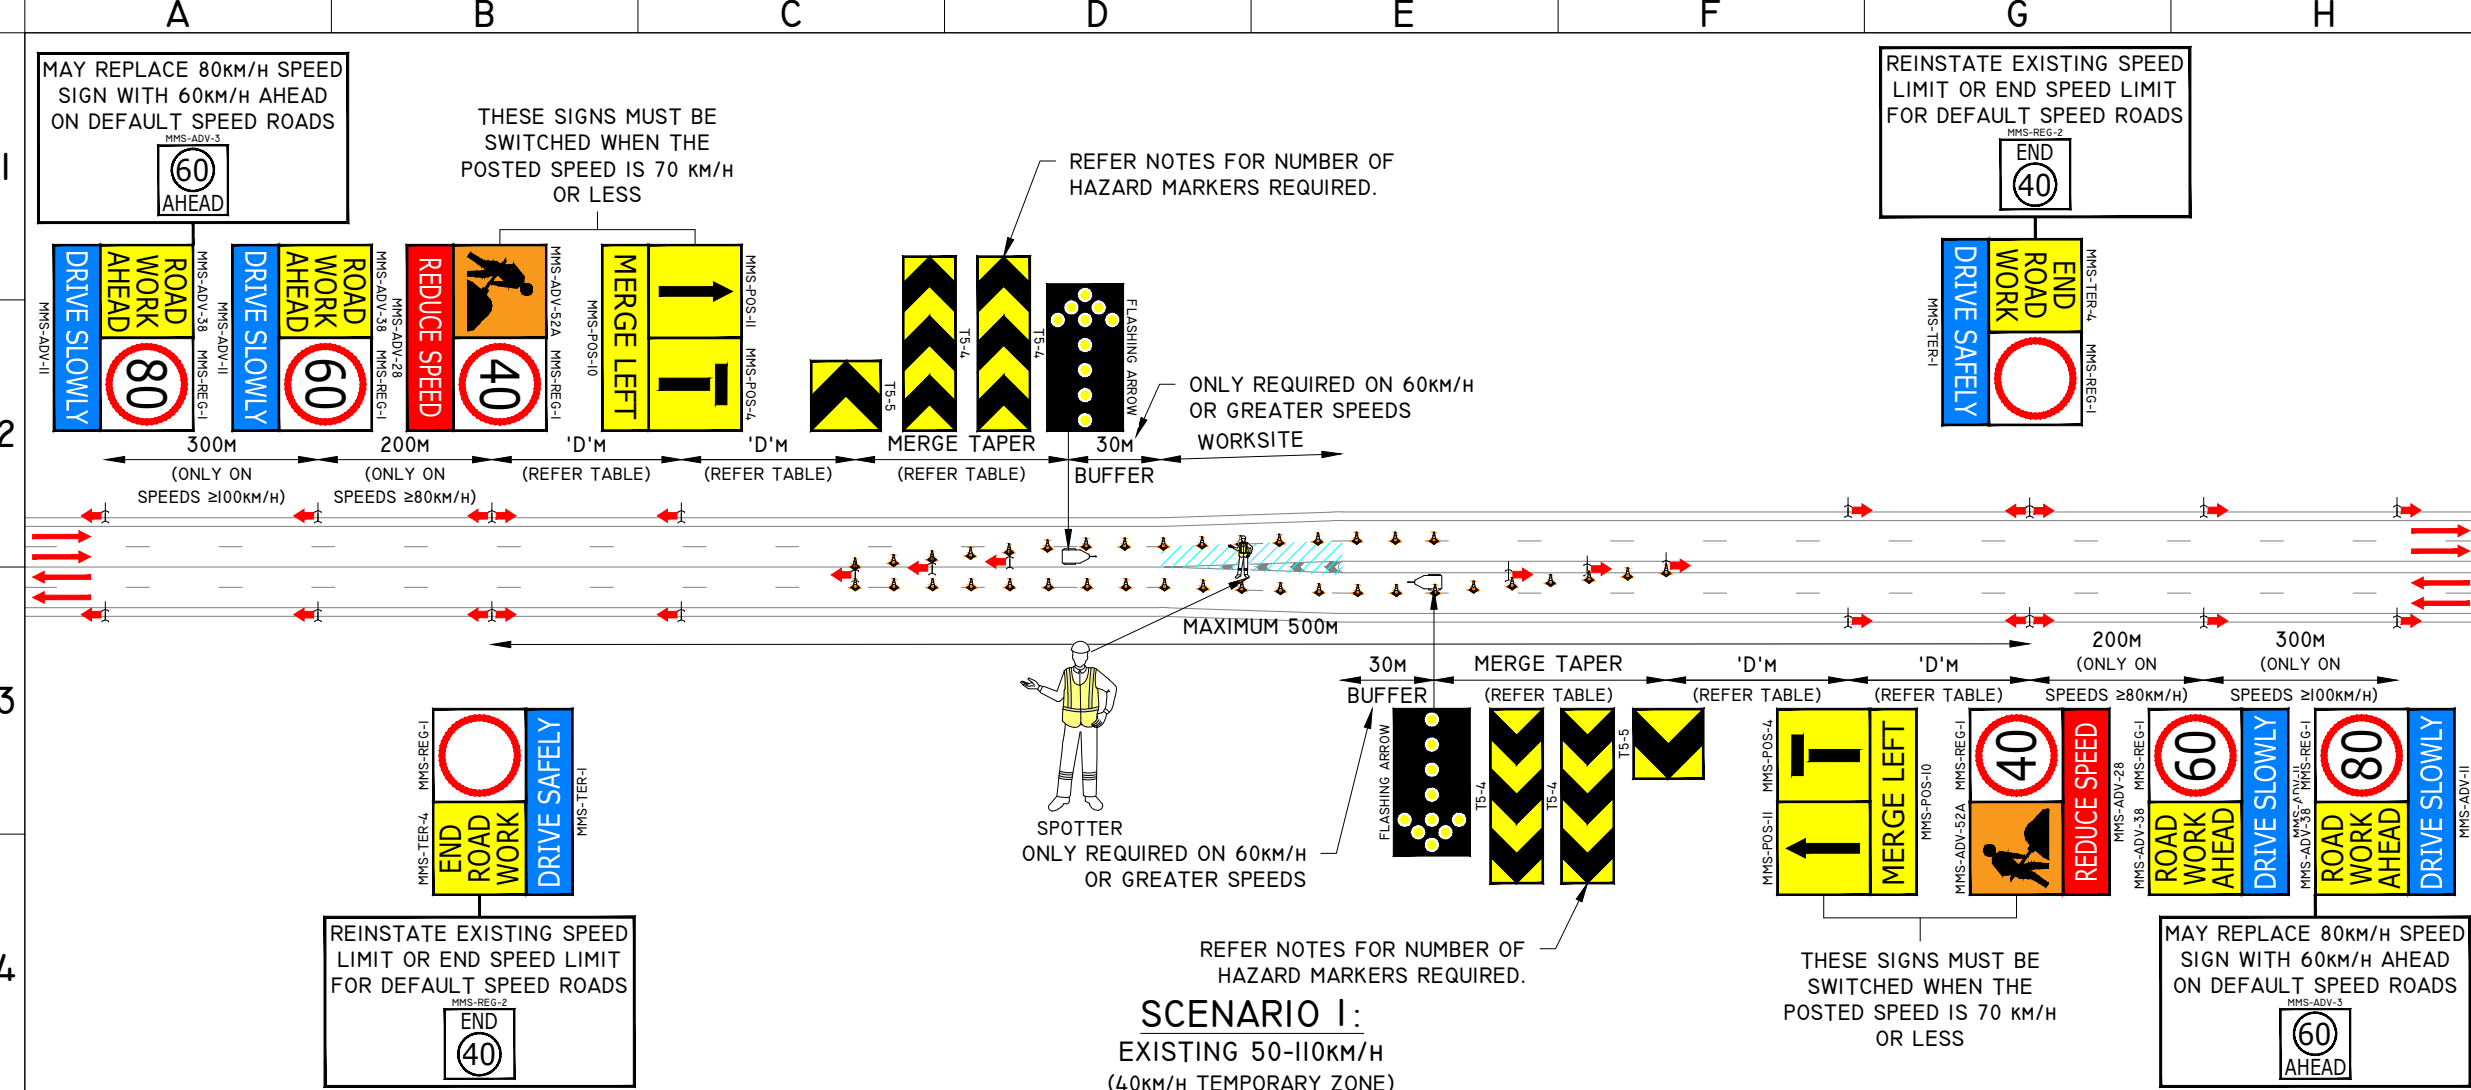

TABLES		
TAPER LENGTHS		
AGTTM PART 3 - TABLE 5.7		
SPEED LIMIT (KM/H)	MERGE TAPER (M)	
45 OR LESS	15	
46 TO 55	30	
56 TO 65	60	
66 TO 75*	115	
76 TO 85*	130	
86 TO 95*	145	
96 TO 105*	160	
GREATER THAN 105*	180	
*TAPER LENGTHS ARE BASED ON A:		
• 3.5M WIDTH OF THE LANE TO BE CLOSED		
• MERGE TAPER LENGTH EQUAL TO 0.6M/S		
• MEDIAN SPEED FOR EACH RANGE (I.E 76 - 85 = 80KM/H)		
TEMPORARY HAZARD MARKERS		
AGTTM PART 3 - 5.4.2 PAGE 65		
A CONTINUOUS LINE OF T5-4 HAZARD MARKERS MUST BE MADE USING THE FOLLOWING RECOMMENDED NUMBERS. 	NUMBER OF SHIFT MARKERS	LENGTH OF TAPER
	2	≤60M
	4	≤115M
	6	≤130M
	8	≤145M
	EVERY 20M	>145M
		WITHIN A CLOSED LANE
SIGN SPACING		
AGTTM PART 3 - TABLE 2.2		
SPEED LIMIT (KM/H)	DISTANCE ('D') (M)	
55 OR LESS	15	
56 TO 65	45	
GREATER THAN 65	EQUAL TO SPEED OF TRAFFIC IN KM/H	
G		H

NOTES

TOLERANCES

POSITION OF SIGNS:
MINIMUM 10% LESS THAN THE DISTANCE OR LENGTHS GIVEN.
MAXIMUM 25% MORE THAN THE DISTANCES OR LENGTHS GIVEN.

SPACING OF DELINEATING DEVICES:
MAXIMUM 10% MORE THAN THE SPACING GIVEN.
NO MINIMUM.

AGTTM PART 6 SECTION 6.8.

DOCUMENTATION

ON-SITE VARIATIONS MUST BE APPROVED BY THE TRAFFIC MANAGEMENT SUPERVISOR, THAN AN ON-SITE VARIATION MADE AND CHANGES RECORDED IN THE DAILY DAIRY. FOR MORE INFORMATION REFER TO SECTION 9.3 OF THE TMP.

- A RISK ASSESSMENT MUST BE CARRIED OUT TO DETERMINE THE REQUIREMENTS OF AFTERCARE.
- ALL SIGN LOCATIONS ARE TO BE CHECKED ON SITE PRIOR TO SETOUT AND POSITIONS ADJUSTED AS PER THE 'TOLERANCES'.
- ALL CONTRADICTIONARY SIGNS WITHIN THE TM SETUP TO BE COVERED BY SUITABLY OPAQUE MATERIAL.
- FOR BOX EDGED SIGN ALTERNATIVES, CONSULT AWTM PRIOR TO IMPLEMENTATION.
- MAXIMUM LENGTH OF 40KM/H SPEED ZONE MUST BE 500M.
- REFER TO SECTION 4.1.8 OF THE TMP FOR THE MANDATORY USE OF SPEED FEEDBACK SIGNAGE

PEDESTRIAN MANAGEMENT

- 'PEDESTRIAN WATCH YOUR STEP' SIGN TO BE INSTALLED ON EACH APPROACH WHERE WORKS MAY ENCROACH ONTO OR ADJACENT TO EXISTING FOOTPATH FACILITIES.
- TM PERSONNEL TO MONITOR AND ESCORT PEDESTRIANS THROUGH THE WORK AREA AS REQUIRED.
- PEDESTRIANS MAY BE HELD ON EITHER END OF THE WORKSITE UNTIL IT IS SAFE TO PASS AS REQUIRED.

RECOMMENDED CONE SPACING

AGTTM PART 3 - TABLE 5.3
ALL PURPOSES:
(≤ 50KM/H): 4M
PROTECTING FRESHLY PAINTED LINES:
(≤ 70KM/H): 24M

RECOMMENDED LANE WIDTHS

MAIN ROADS WA CoP SECTION 6.7 - TABLE 9
RECOMMENDED LANE WIDTHS:
≤ 60KM/H: 3.2M
MINIMUM LANE WIDTHS:
≤ 60KM/H: 3.0M

LEGEND

EXISTING ROAD
PROPOSED CONES
WORKSITE

METROPOLITAN REGIONS TRAFFIC MANAGEMENT BRANCH

WATERLOO CRESCENT
TELEPHONE (08) 138 138

DATE OF DRAWING
2025 JULY

LOCAL GOVERNMENT AUTHORITY
-

ROAD AUTHORITY
MAIN ROADS WA

CHECKED BY
TYLER HARTLEY

ACCREDITATION
RTM-0066

DESIGNED BY
MICHAEL REED

ACCREDITATION
AWTM-23-11536-02

SCALE
-

POSTED SPEED
50-110KM/H

WORKSITE SPEED
40KM/H

SIGNATURE
Tyler Hartley

SIGNATURE
Michael Reed

GENERIC TRAFFIC GUIDANCE SCHEME
LANE CLOSURE SETUPS
MEDIAN GORE MARKING - DUAL LANE
WORKSITE WITHIN 1.2M

DRAWING NO
0922-01531-LC-033

REVISION
6