

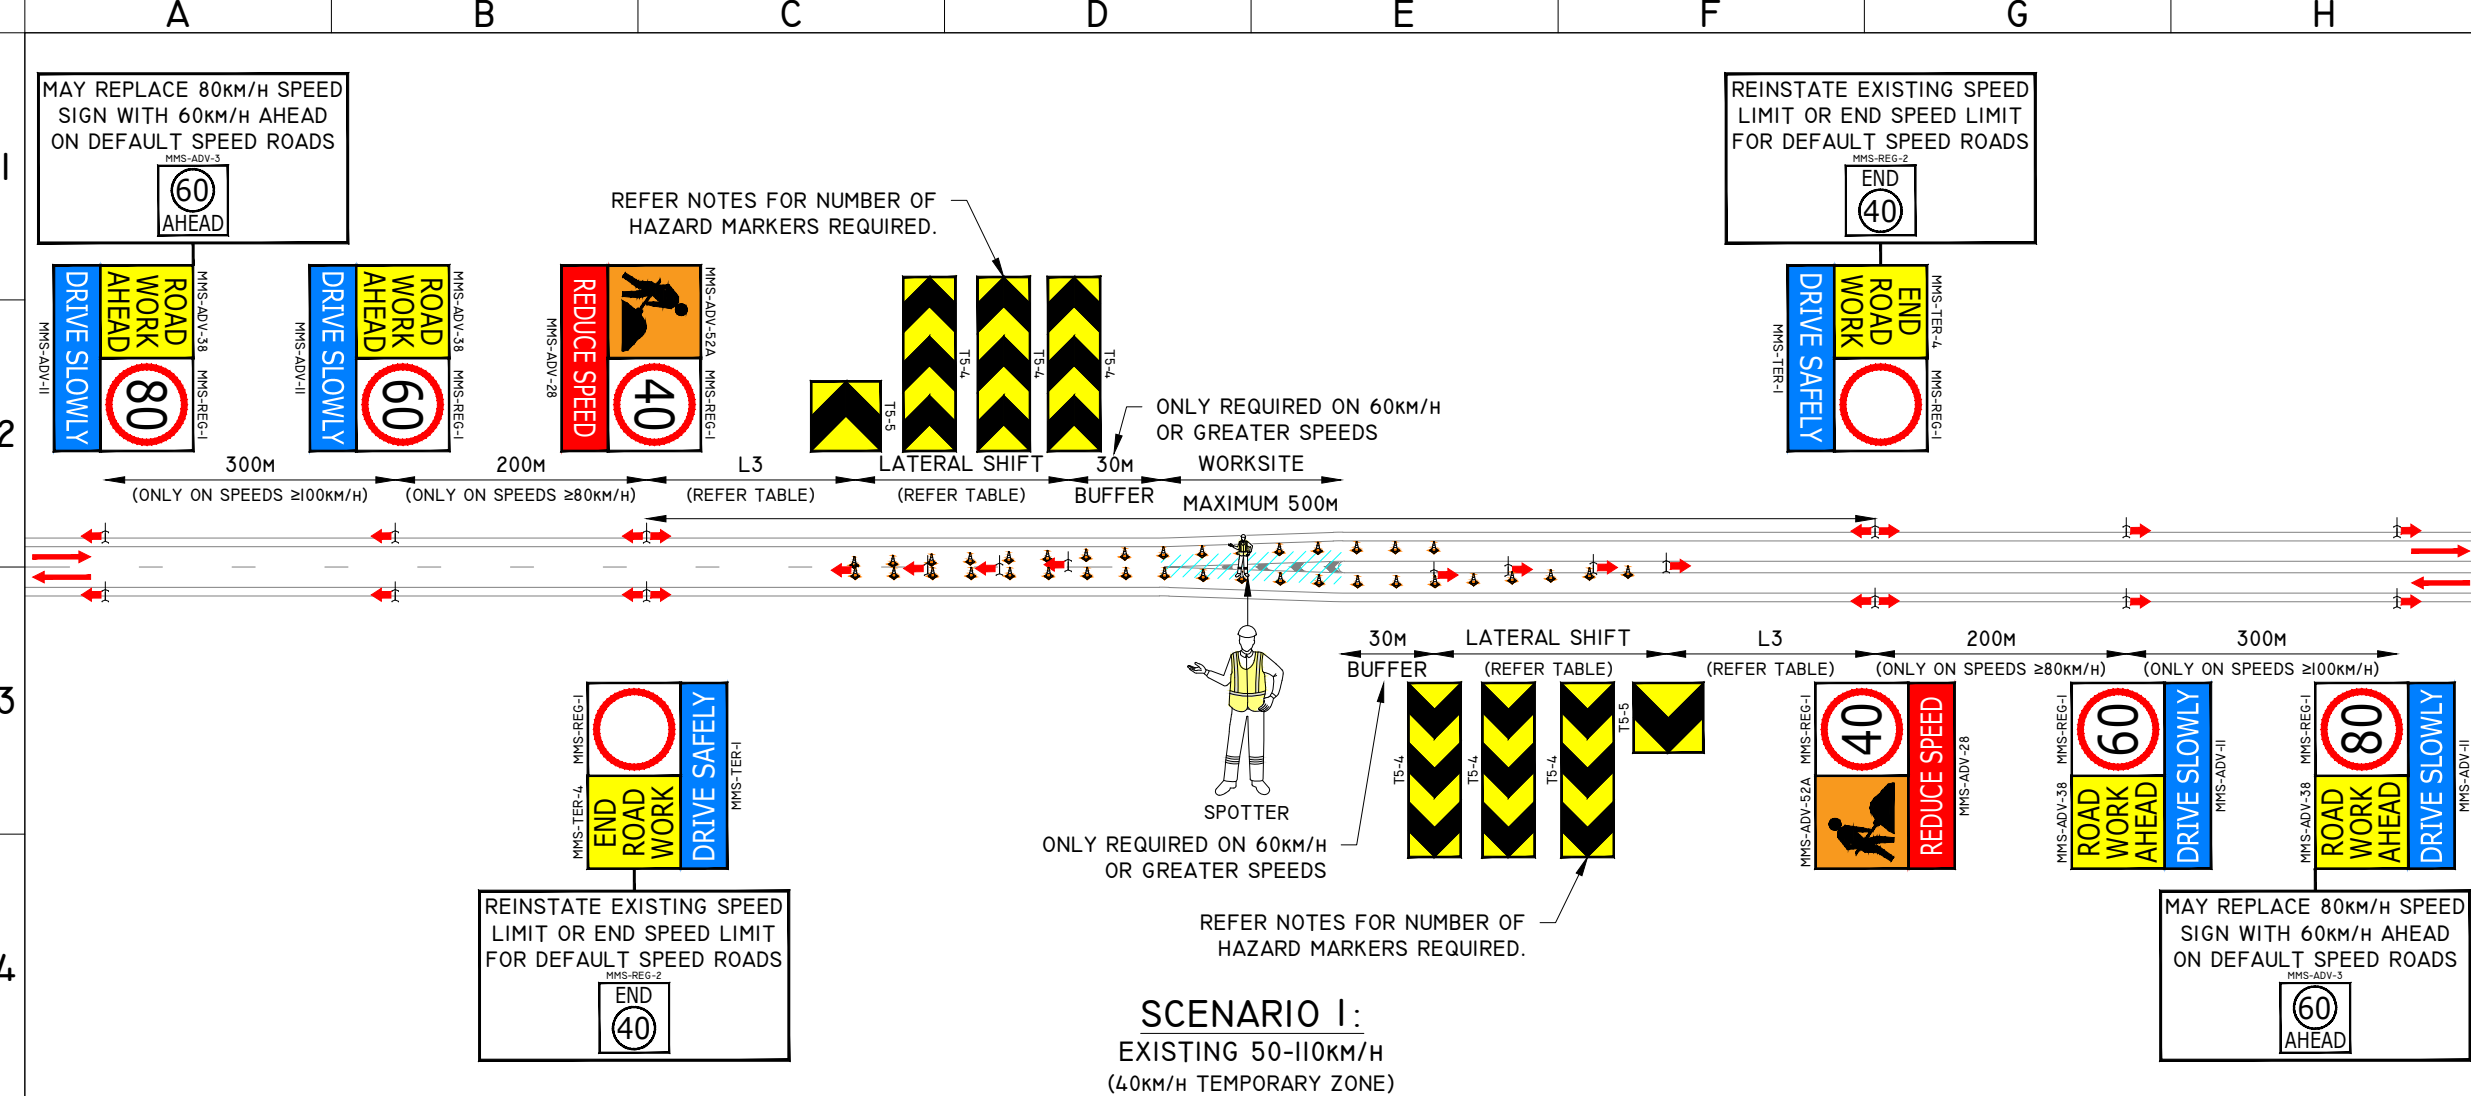


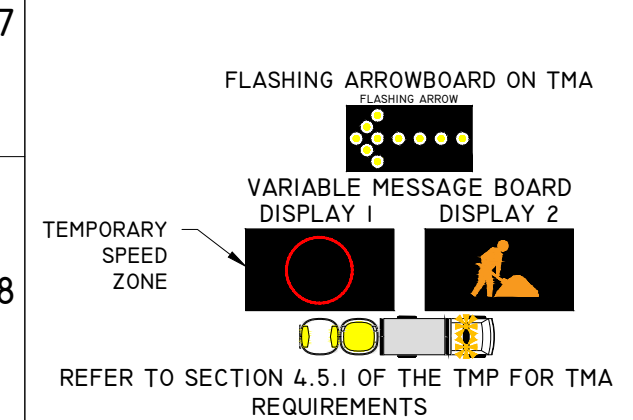

SHADOW VEHICLE INSET
SHADOW VEHICLE MAY BE DISPENSED WITH UNDER A RISK ASSESSMENT BY AN RTM AS PART OF THE TM ADVICE. IN THE ABSENCE OF THE SHADOW VEHICLE A LOOKOUT PERSON IS REQUIRED. REFER TO SECTION 4.5 OF THE TMP FOR MORE DETAILS.

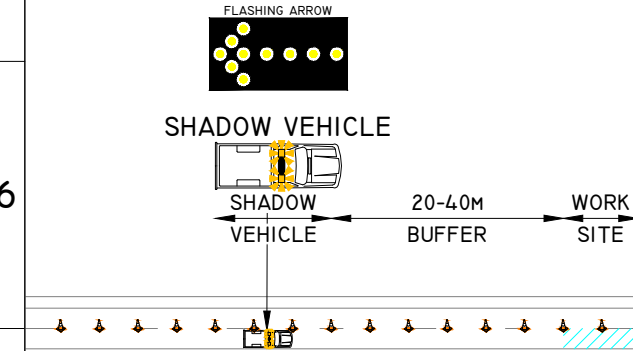

NOTES

TOLERANCES

POSITION OF SIGNS:
MINIMUM 10% LESS THAN THE DISTANCE OR LENGTHS GIVEN.
MAXIMUM 25% MORE THAN THE DISTANCES OR LENGTHS GIVEN.

SPACING OF DELINEATING DEVICES:
MAXIMUM 10% MORE THAN THE SPACING GIVEN.
NO MINIMUM.

AGTTM PART 6 SECTION 6.8.

DOCUMENTATION

ON-SITE VARIATIONS MUST BE APPROVED BY THE TRAFFIC MANAGEMENT SUPERVISOR, THAN AN ON-SITE VARIATION MADE AND CHANGES RECORDED IN THE DAILY DAIRY. FOR MORE INFORMATION REFER TO SECTION 9.3 OF THE TMP.

- A RISK ASSESSMENT MUST BE CARRIED OUT TO DETERMINE THE REQUIREMENTS OF AFTERCARE.
- ALL SIGN LOCATIONS ARE TO BE CHECKED ON SITE PRIOR TO SETOUT AND POSITIONS ADJUSTED AS PER THE 'TOLERANCES'.
- ALL CONTRADICTORY SIGNS WITHIN THE TM SETUP TO BE COVERED BY SUITABLY OPAQUE MATERIAL.
- FOR BOX EDGED SIGN ALTERNATIVES, CONSULT AWTM PRIOR TO IMPLEMENTATION.
- MAXIMUM LENGTH OF 40km/h SPEED ZONE MUST BE 500M.
- REFER TO SECTION 4.1.8 OF THE TMP FOR THE MANDATORY USE OF SPEED FEEDBACK SIGNAGE

PEDESTRIAN MANAGEMENT

- 'PEDESTRIAN WATCH YOUR STEP' SIGN TO BE INSTALLED ON EACH APPROACH WHERE WORKS MAY ENCR OACH ONTO OR ADJACENT TO EXISTING FOOTPATH FACILITIES.
- TM PERSONNEL TO MONITOR AND ESCORT PEDESTRIANS THROUGH THE WORK AREA AS REQUIRED.
- PEDESTRIANS MAY BE HELD ON EITHER END OF THE WORKSITE UNTIL IT IS SAFE TO PASS AS REQUIRED.

RECOMMENDED CONE SPACING

AGTTM PART 3 - TABLE 5.3

ALL PURPOSES:
(≤ 50km/h): 4M
PROTECTING FRESHLY PAINTED LINES:
(≤ 70km/h): 24M

RECOMMENDED LANE WIDTHS

MAIN ROADS WA CoP SECTION 6.7 - TABLE 7

RECOMMENDED LANE WIDTHS:
≤ 60km/h: 3.2M
MINIMUM LANE WIDTHS:
≤ 60km/h: 3.0M

TABLES		
TAPER LENGTHS		
AGTTM PART 3 - TABLE 5.7		
SPEED LIMIT (KM/H)	LATERAL SHIFT TAPER (M)	
45 OR LESS	5	
46 TO 55	15	
56 TO 65	30	
66 TO 75*	70	
76 TO 85*	80	
86 TO 95*	90	
96 TO 105*	100	
GREATER THAN 105*	110	
*TAPER LENGTHS ARE BASED ON A:		
• 3.5M WIDTH OF THE LANE TO BE CLOSED		
• LATERAL SHIFT TAPER LENGTH EQUAL TO 1.0M/S		
• MEDIAN SPEED FOR EACH RANGE (I.E 76 - 85 = 80KM/H		
TEMPORARY HAZARD MARKERS		
AGTTM PART 3 - 5.4.2 PAGE 65		
A CONTINUOUS LINE OF T5-4 HAZARD MARKERS MUST BE MADE USING THE FOLLOWING RECOMMENDED NUMBERS.	NUMBER OF SHIFT MARKERS	LENGTH OF TAPER
	2	≤60M
	4	≤115M
	6	≤130M
	8	≤145M
	EVERY 20M	>145M
		WITHIN A CLOSED LANE
		
TS-4		
SIGN SPACING		
MAIN ROADS WA CoP SECTION 6.5.2 - TABLE 6		
SPEED LIMIT (KM/H)	L3 (M)	
60 OR LESS	45	
70	70	
80 OR GREATER	90	

LEGEND

EXISTING ROAD

PROPOSED CONES

WORKSITE



METROPOLITAN REGIONS
TRAFFIC MANAGEMENT BRANCH

WATERLOO CRESCENT
TELEPHONE (08) 138 138

EAST PERTH 6004

DATE OF DRAWING	2025 JULY	SCALE	-	
LOCAL GOVERNMENT AUTHORITY	-	POSTED SPEED	50-110KM/H	
ROAD AUTHORITY	MAIN ROADS WA	WORKSITE SPEED	40KM/H	
CHECKED BY	TYLER HARTLEY	SIGNATURE		
ACCREDITATION	RTM-0066	SIGNATURE		
DESIGNED BY	MICHAEL REED	GENERIC TRAFFIC GUIDANCE SCHEME LATERAL SHIFT SETUPS MEDIAN GORE MARKING - SINGLE LANE WORKSITE WITHIN 1.2M		
ACCREDITATION	AWTM-23-11536-02			
DRAWING NO	0922-01531-LS-010		REVISION	6