


SCENARIO I:

THIS SCENARIO IS TO BE USED ON UNSEALED ROADS ONLY.
WHERE THE SIGHT DISTANCE TO THE ROAD GRADERS WARNING
DEVICE IS AT LEAST 250M AND VEHICLES MAY PASS THE
GRADER WITHOUT LEAVING THE ROAD WAY.

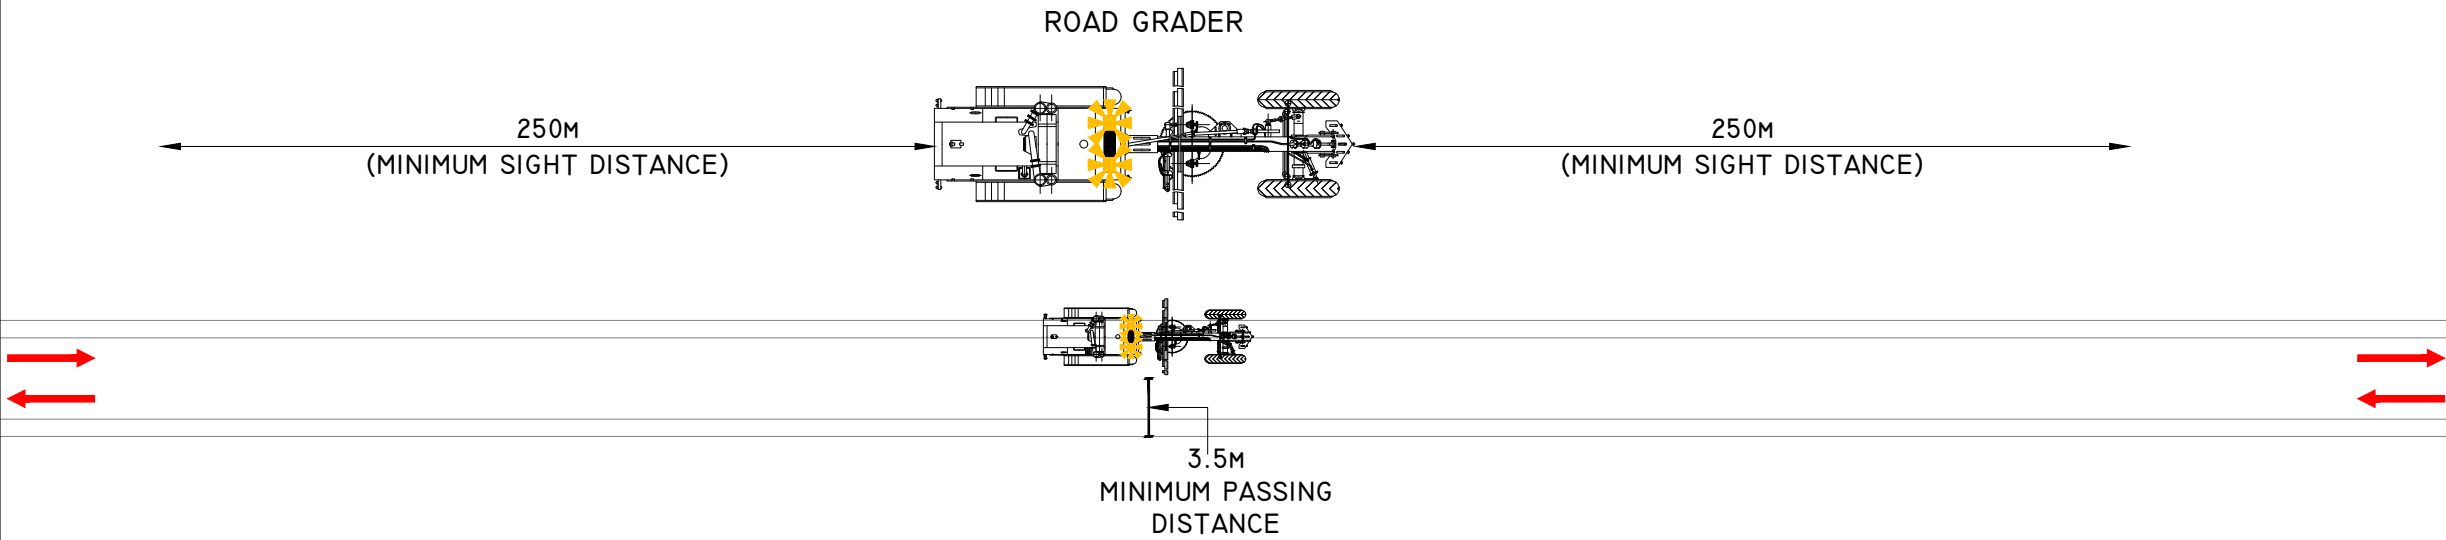

NOTES

- 1. THIS DRAWING MAY BE USED ON THE FOLLOWING SCENARIOS:
 - 1.1. WHERE THERE ARE NO WORKERS ON FOOT
 - 1.2. WHERE THE ROAD IS UNSEALED
 - 1.3. WHERE THE SIGHT DISTANCE TO THE GRADER IS AT LEAST 250M IN EACH DIRECTION
- 2. WHERE A VEHICLE IS REQUIRED TO STOP FOR AN EXTENDED PERIOD OF TIME, A SHORT TERM LOW IMPACT DRAWING MUST BE USED.
- 3. THIS DRAWING IS FOR GRADING WORKS ONLY
- 4. PRIOR TO THE START OF WORKS, A RISK ASSESSMENT IS REQUIRED TO DETERMINE IF THE WORKS CAN BE COMPLETED SAFELY. REFER TO THE TMP FOR RISK CONSIDERATIONS.
- 5. VEHICLE LOCATIONS MUST CONSIDER THE IMPACT ON VULNERABLE ROAD USERS AND CYCLISTS.

DOCUMENTATION

DAILY RECORDS OF THE SITE LAYOUT INCLUDING DEVICES, SIGHT DISTANCE, RISK ASSESSMENTS, SIGNS OR TGS, MUST BE KEPT IN A DIARY OR IN WORK SHEETS (DAILY DAIRY). ANY SIGNIFICANT DEPARTURES FROM, OR ADDITIONS TO, THE SIGNS AND DEVICES INCLUDED IN THIS DIAGRAM SHOULD BE NOTED AND APPROVED.

LEGEND

EXISTING ROAD



METROPOLITAN REGIONS
TRAFFIC MANAGEMENT BRANCH

WATERLOO CRESCENT
TELEPHONE (08) 138 138

EAST PERTH 6004

DATE OF DRAWING 2025 JULY	SCALE -
LOCAL GOVERNMENT AUTHORITY -	POSTED SPEED -
ROAD AUTHORITY MAIN ROADS WA	WORKSITE SPEED -
CHECKED BY TYLER HARTLEY	SIGNATURE 
ACCREDITATION RTM-0066	
DESIGNED BY MICHAEL REED	SIGNATURE 
ACCREDITATION AWTM-23-11536-02	
GENERIC TRAFFIC GUIDANCE SCHEME CLASS 2 - MOBILE SCENARIOS ROAD GRADER WORKS NO WORKERS ON FOOT	
DRAWING NO 0922-01531-MS2-026	REVISION 6