


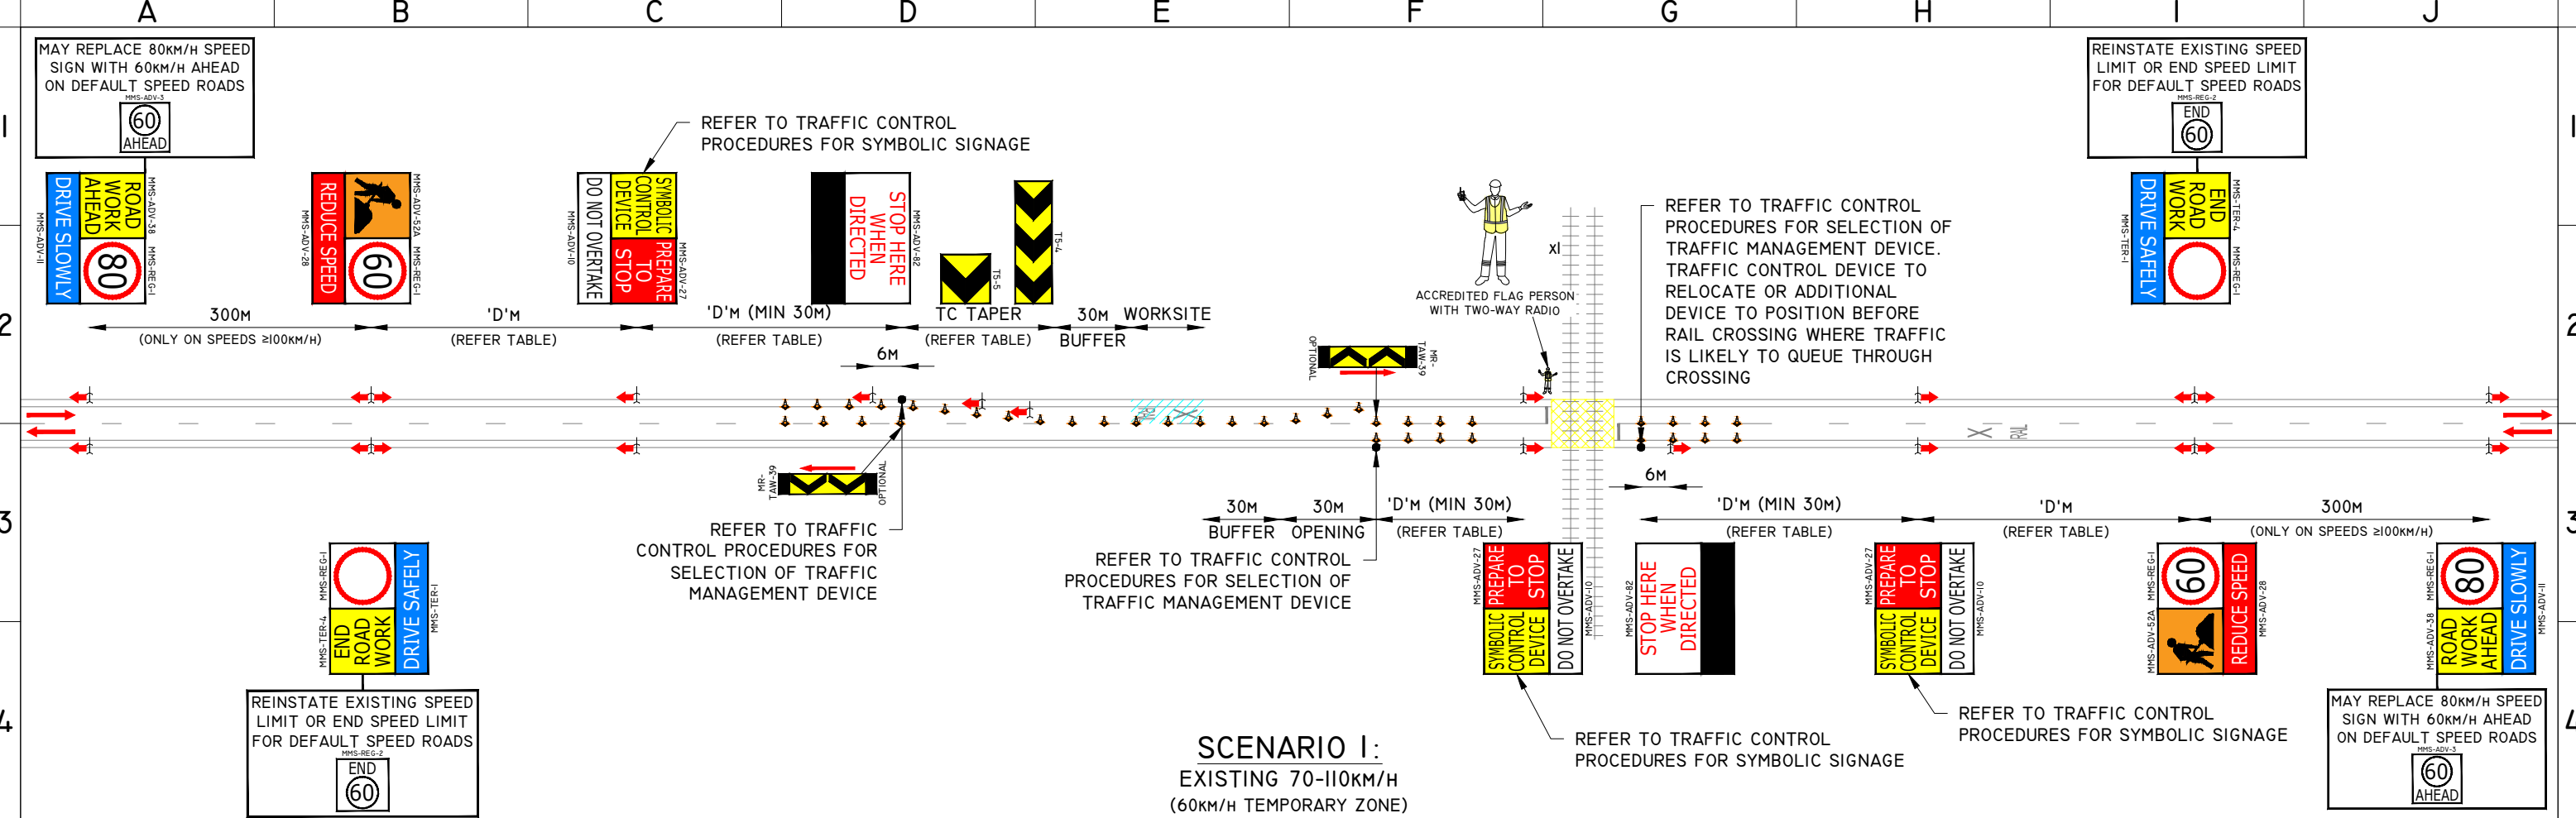

TRAFFIC CONTROL PROCEDURES

REFER TO TMP SECTION 4.1.7 PORTABLE TRAFFIC CONTROL DEVICES FOR MORE DETAILS

MANUAL TRAFFIC CONTROL

ACCREDITED TRAFFIC CONTROLLER

SLOW SIDE OF BAT TO BE COVERED AT RAIL CROSSING
PORTABLE TRAFFIC CONTROL DEVICE (PTCD)

PORTABOOM

TEMPORARY TRAFFIC SIGNAL

MMS-ADV-47 MMS-ADV-27

MMS-ADV-82

MMS-ADV-10

MMS-ADV-79 MMS-ADV-27

MMS-ADV-82

MMS-ADV-10

MMS-ADV-48 MMS-ADV-27

R6-6

MMS-ADV-10

END OF QUEUE PROTECTION

DEVICE MAY BE A TRAFFIC CONTROLLER, PORTABOOM OR TEMPORARY SIGNAL

6M END OF QUEUE 2x'D'M (REFER NOTES) 'D'M (REFER NOTES)

MUST BE IMPLEMENTED ON ALL ROADS WITH A POSTED SPEED OF 80km/h OR GREATER. REFER TO TGS-TMC-RF-022, 023 AND 044 FOR MORE INFORMATION.

MANUAL TRAFFIC CONTROL IS NOT PERMITTED ON THE MAIN ROADS NETWORK WITH THE EXCEPTIONS LISTED UNDER SECTION 4.1.7 (PORTABLE TRAFFIC CONTROL DEVICES) OF THE TMP AND IN THE MAIN ROADS CODE OF PRACTICE.

ON ALL OTHER ROADS, PTCDS MUST BE USED UNDER THE FOLLOWING CONDITIONS:

- A PERMANENT SPEED LIMIT OF 90m/h OR MORE AND OVER 2,000vpd: OR
- A PERMANENT SPEED LIMIT OF 70km/h OR MORE AND OVER 10,000vpd.

PTCDs SHOULD BE CONSIDERED ON ALL WORKS AND ONLY BE SUPPLEMENTED WITH MANUAL TRAFFIC CONTROL UNDER AN AWTM/WTM RISK ASSESSMENT.

SHADOW VEHICLE INSET

SHADOW VEHICLE MAY BE DISPENSED WITH UNDER A RISK ASSESSMENT BY AN RTM AS PART OF THE TM ADVISE. IN THE ABSENCE OF THE SHADOW VEHICLE A LOOKOUT PERSON IS REQUIRED. REFER TO SECTION 4.5 OF THE TMP FOR MORE DETAILS.

FLASHING ARROW
SHADOW VEHICLE
20-40M BUFFER
WORK SITE

TABLES

TAPER LENGTHS

AGTTM PART 3 - TABLE 5.7

SPEED LIMIT (km/h)	TRAFFIC CONTROL TAPER (m)
45 OR LESS	15
46 TO 55	15
56 TO 65	30
66 TO 75*	
76 TO 85*	
86 TO 95*	
96 TO 105*	
GREATER THAN 105*	N/A

*TAPER LENGTHS ARE BASED ON A:

- 3.5m WIDTH OF THE LANE TO BE CLOSED
- LATERAL SHIFT TAPER LENGTH EQUAL TO 1.0m/s
- MEDIAN SPEED FOR EACH RANGE (I.E 76 - 85 = 80km/h)

SIGN SPACING

AGTTM PART 3 - TABLE 2.2

SPEED LIMIT (km/h)	DISTANCE ('D')
55 OR LESS	15
56 TO 65	45
GREATER THAN 65	EQUAL TO SPEED OF TRAFFIC IN km/h

RECOMMENDED CONE SPACING

AGTTM PART 3 - TABLE 5.3

ALL PURPOSES:

- (60 - 70km/h): 12m

PROTECTING FRESHLY PAINTED LINES:

- (≤ 70km/h): 24m

CENTRELINE ON APPROACH TO TC POSITION: 4m

TAPER AT TRAFFIC CONTROL STATION: 4m

RECOMMENDED LANE WIDTHS

MAIN ROADS WA CoP SECTION 6.7 - TABLE 9

SHUTTLE FLOW WITH CONTROL: 3.2m

NOTES

TOLERANCES

POSITION OF SIGNS:

- MINIMUM 10% LESS THAN THE DISTANCE OR LENGTHS GIVEN.
- MAXIMUM 25% MORE THAN THE DISTANCES OR LENGTHS GIVEN.

SPACING OF DELINEATING DEVICES:

- MAXIMUM 10% MORE THAN THE SPACING GIVEN.
- NO MINIMUM.

AGTTM PART 6 SECTION 6.8. DOCUMENTATION

ON-SITE VARIATIONS MUST BE CARRIED OUT TO DETERMINE THE REQUIREMENTS OF AFTERCARE.

- ALL SIGN LOCATIONS ARE TO BE CHECKED ON SITE PRIOR TO SETOUT AND POSITIONS ADJUSTED AS PER THE 'TOLERANCES'.
- ALL CONTRADICTIONARY SIGNS WITHIN THE TM SETUP TO BE COVERED BY SUITABLY OPAQUE MATERIAL.
- FOR BOX EDGED SIGN ALTERNATIVES, CONSULT AWTM PRIOR TO IMPLEMENTATION.
- WORKERS TO REMAIN 10M CLEAR OF RAILWAY TRACKS AT ALL TIMES.
- ACCREDITED FLAG PERSON TO MONITOR AND WARN OF INCOMING TRAINS OVER TWO-WAY RADIO. TCS WILL HOLD ALL TRAFFIC TO ALLOW TRAIN TO PASS.
- TRAFFIC SHALL NEVER BE ALLOWED TO QUEUE/STACK ACROSS THE RAIL CORRIDOR.
- REFER TO SECTION 4.1.8 OF THE TMP FOR THE MANDATORY USE OF SPEED FEEDBACK SIGNAGE

PEDESTRIAN MANAGEMENT

- 'PEDESTRIAN WATCH YOUR STEP' SIGN TO BE INSTALLED ON EACH APPROACH WHERE WORKS MAY ENCRACH ONTO OR ADJACENT TO EXISTING FOOTPATH FACILITIES.
- TM PERSONNEL TO MONITOR AND ESCORT PEDESTRIANS THROUGH THE WORK AREA AS REQUIRED.
- PEDESTRIANS MAY BE HELD ON EITHER END OF THE WORKSITE UNTIL IT IS SAFE TO PASS AS REQUIRED.

METROPOLITAN REGIONS
TRAFFIC MANAGEMENT BRANCH
WATERLOO CRESCENT
TELEPHONE (08) 158 158

DATE OF DRAWING
2025 JULY

POSTED SPEED
70-110km/h

WORKSITE SPEED
60km/h

DESIGNED BY
MICHAEL REED

CHECKED BY
TYLER HARTLEY

SCALE
-

ACCREDITATION
AWTM-23-11536-02

ACCREDITATION
RTM-0066

ROAD AUTHORITY
MAIN ROADS WA

SIGNATURE

SIGNATURE

LOCAL GOVERNMENT AUTHORITY
-

LEGEND

EXISTING ROAD

EXISTING RAILWAY TRACKS

PROPOSED CONES

WORKSITE

GENERIC TRAFFIC GUIDANCE SCHEME
RAIL APPROACH SETUPS
'X' AND 'RAIL' REINSTATEMENT
WORKSITE BETWEEN 1.2M AND 3.0M

DRAWING NO
0922-01531-RA-004

REVISION
6