

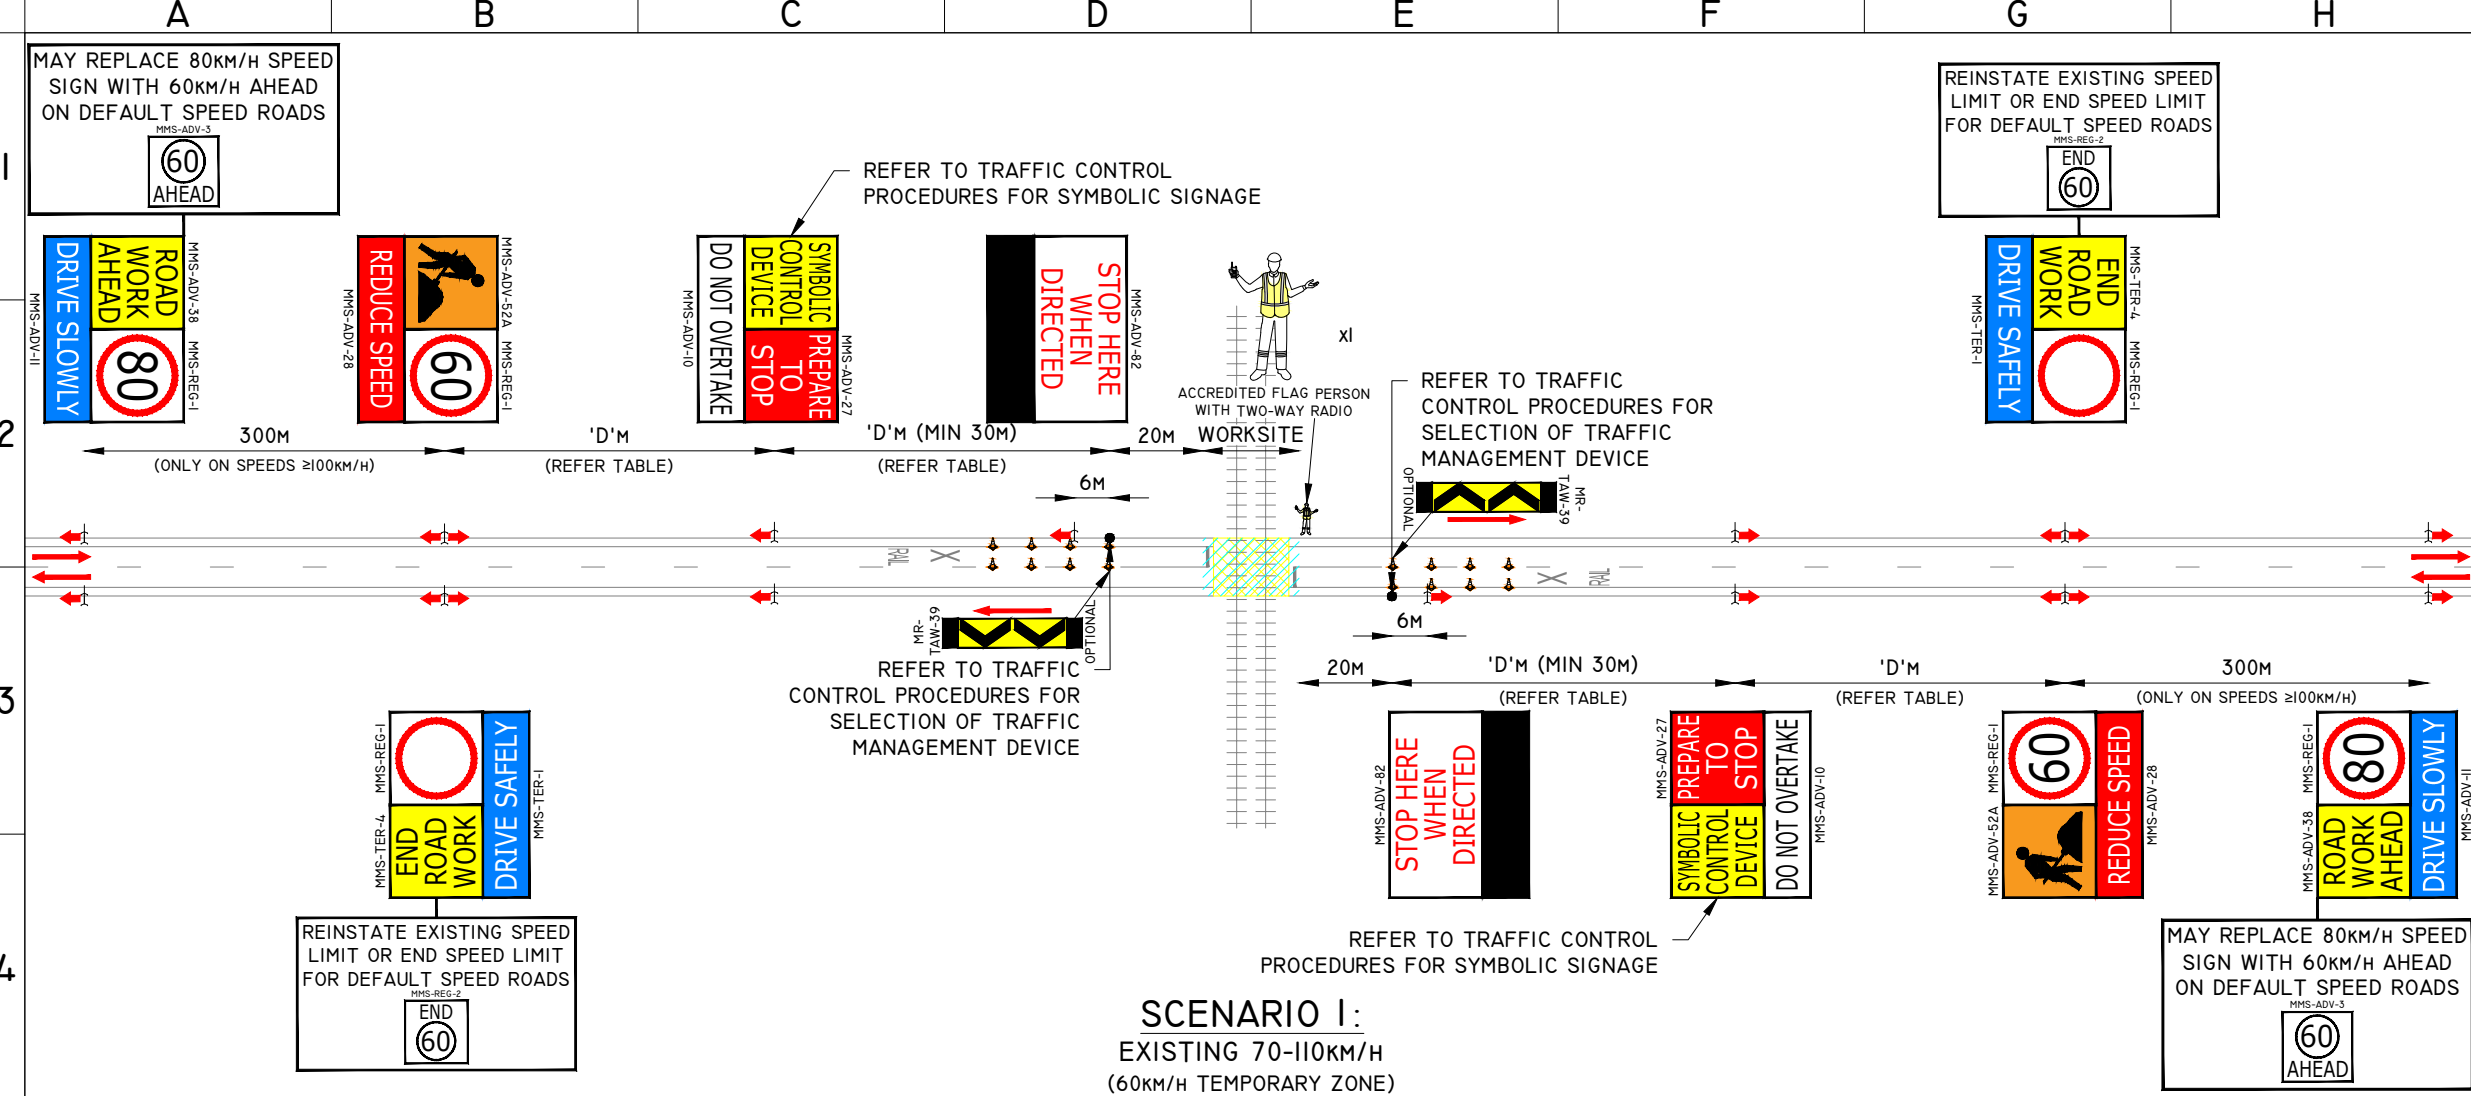
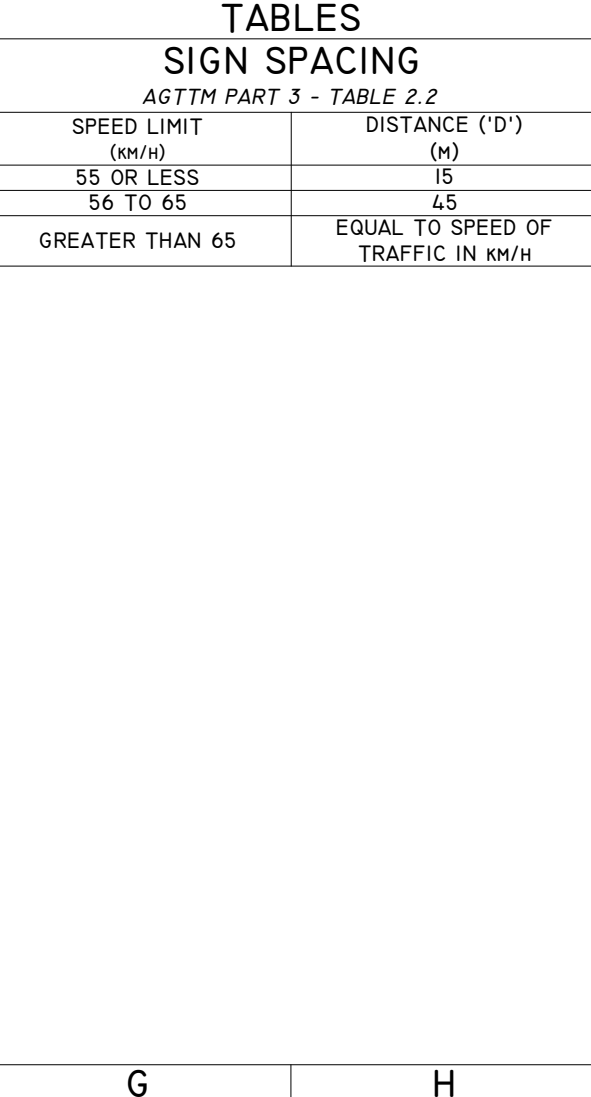


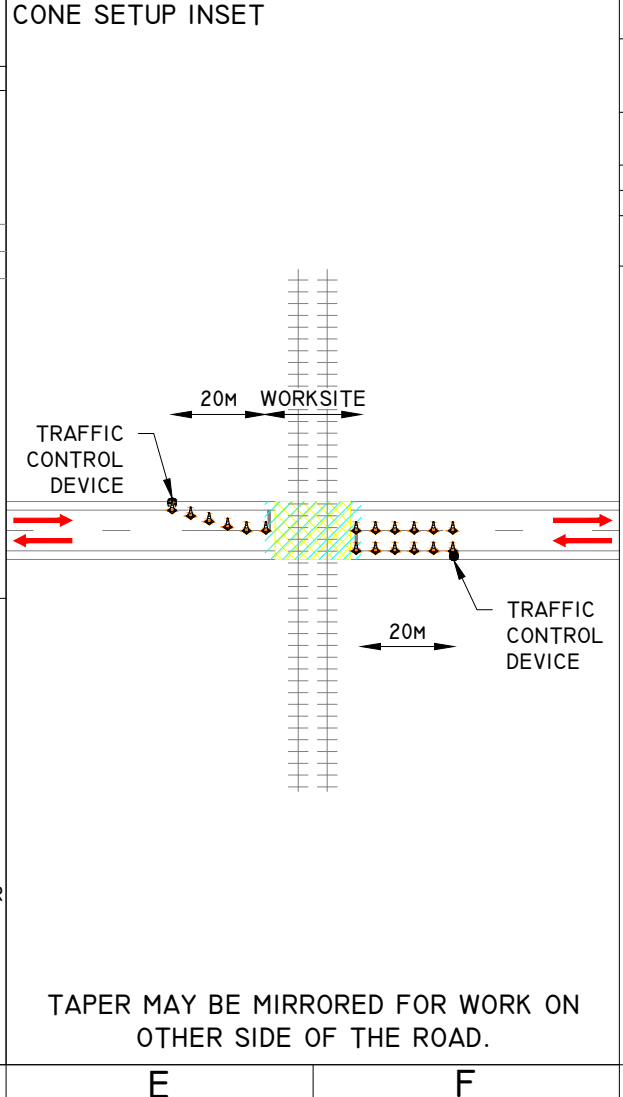

SCENARIO 1:  
EXISTING 70-110km/h  
(60km/h TEMPORARY ZONE)

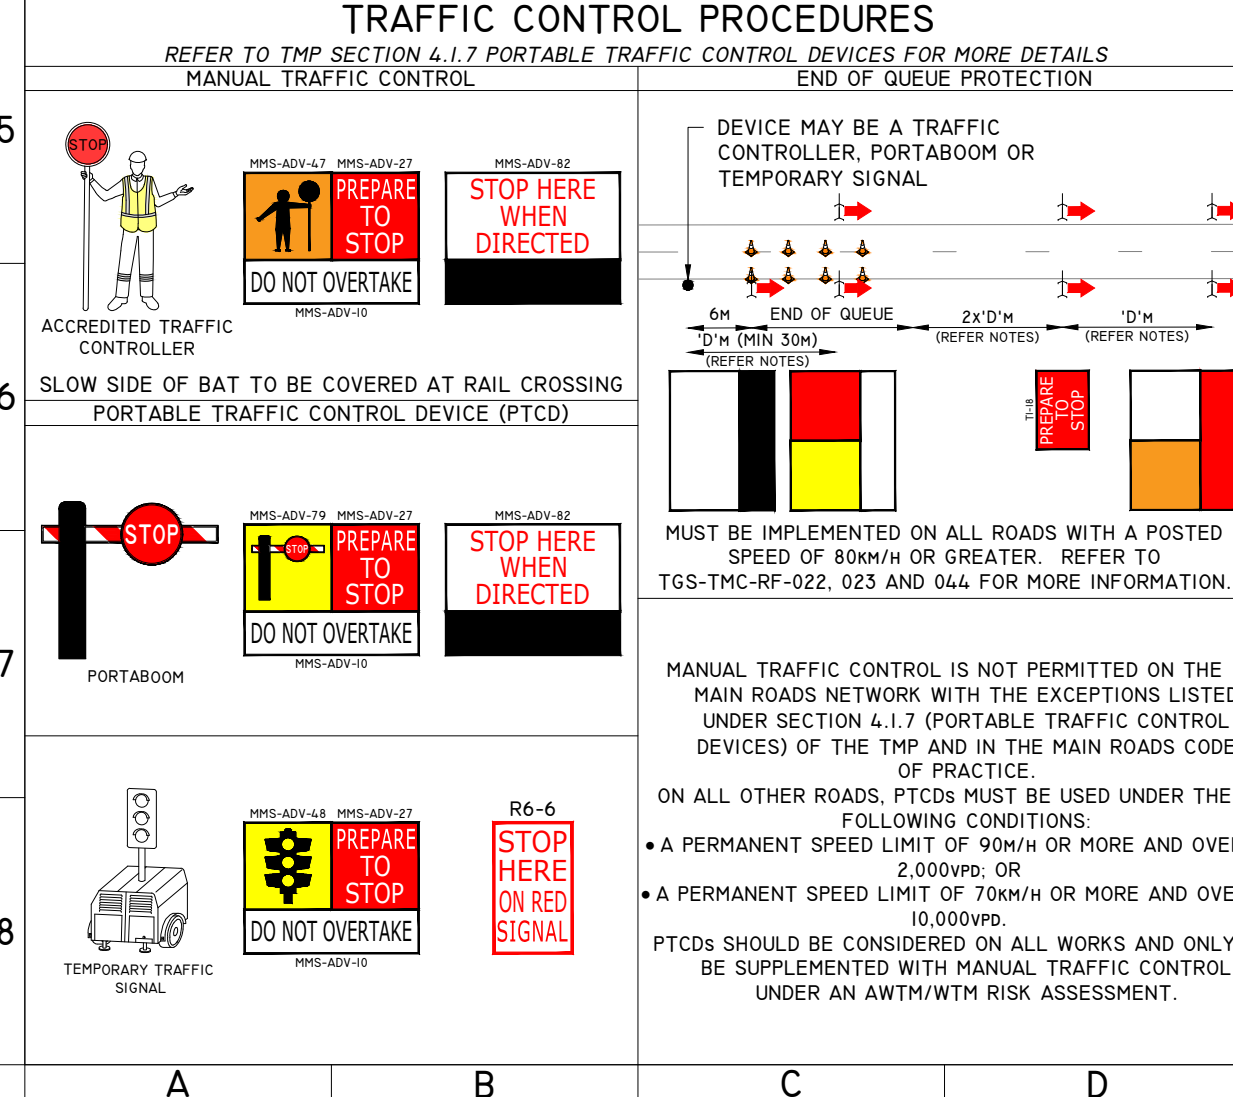

### NOTES

**TOLERANCES**  
POSITION OF SIGNS:  
MINIMUM 10% LESS THAN THE DISTANCE OR LENGTHS GIVEN.  
MAXIMUM 25% MORE THAN THE DISTANCES OR LENGTHS GIVEN.  
SPACING OF DELINEATING DEVICES:  
MAXIMUM 10% MORE THAN THE SPACING GIVEN.  
NO MINIMUM.

AGTTM PART 6 SECTION 6.8.  
**DOCUMENTATION**  
ON-SITE VARIATIONS MUST BE APPROVED BY THE TRAFFIC MANAGEMENT SUPERVISOR, THAN AN ON-SITE VARIATION MADE AND CHANGES RECORDED IN THE DAILY DAIRY. FOR MORE INFORMATION REFER TO SECTION 9.3 OF THE TMP.

- A RISK ASSESSMENT MUST BE CARRIED OUT TO DETERMINE THE REQUIREMENTS OF AFTERCARE.
- ALL SIGN LOCATIONS ARE TO BE CHECKED ON SITE PRIOR TO SETOUT AND POSITIONS ADJUSTED AS PER THE 'TOLERANCES'.
- WHERE WORKERS ARE VISIBLE FROM OTHER APPROACHES, A SYMBOLIC WORKER MUST BE DISPLAYED ON ALL APPROACHES.
- FOR BOX EDGED SIGN ALTERNATIVES, CONSULT AWTM PRIOR TO IMPLEMENTATION.
- WORKERS TO REMAIN 10M CLEAR OF RAILWAY TRACKS AT ALL TIMES.
- ALL CONTRADICTIONARY SIGNS WITHIN THE TM SETUP TO BE COVERED BY SUITABLY OPAQUE MATERIAL.
- REFER TO MANUFACTURING ADVICE FOR SHUNT DISTANCES ON TRUCK MOUNTED ATTENUATORS.
- ACCREDITED FLAG PERSON TO MONITOR AND WARN OF INCOMING TRAINS OVER TWO-WAY RADIO. TCS WILL HOLD ALL TRAFFIC TO ALLOW TRAIN TO PASS.

**PEDESTRIAN MANAGEMENT**

- 'PEDESTRIAN WATCH YOUR STEP' SIGN TO BE INSTALLED ON EACH APPROACH WHERE WORKS MAY ENCROACH ONTO OR ADJACENT TO EXISTING FOOTPATH FACILITIES.
- TM PERSONNEL TO MONITOR AND ESCORT PEDESTRIANS THROUGH THE WORK AREA AS REQUIRED.
- PEDESTRIANS MAY BE HELD ON EITHER END OF THE WORKSITE UNTIL IT IS SAFE TO PASS AS REQUIRED.

**RECOMMENDED CONE SPACING**  
AGTTM PART 3 - TABLE 4.2  
CENTRELINE ON APPROACH TO TC POSITION: 4m  
TAPER AT TRAFFIC CONTROL STATION: 4m  
**RECOMMENDED LANE WIDTHS**  
MAIN ROADS WA CoP SECTION 6.7 - TABLE 9  
SHUTTLE FLOW WITH CONTROL: 3.2m

### LEGEND

EXISTING ROAD  
EXISTING RAILWAY TRACKS  
PROPOSED CONES  
WORKSITE

| TABLES                   |                                   |
|--------------------------|-----------------------------------|
| SIGN SPACING             |                                   |
| AGTTM PART 3 - TABLE 2.2 |                                   |
| SPEED LIMIT (KM/H)       | DISTANCE ('D') (M)                |
| 55 OR LESS               | 15                                |
| 56 TO 65                 | 45                                |
| GREATER THAN 65          | EQUAL TO SPEED OF TRAFFIC IN KM/H |

**mainroads**  
WESTERN AUSTRALIA

METROPOLITAN REGIONS  
TRAFFIC MANAGEMENT BRANCH

WATERLOO CRESCENT  
TELEPHONE (08) 138 138

EAST PERTH 6004

|   |                            |
|---|----------------------------|
| DATE OF DRAWING<br>2025 JULY   | SCALE<br>-                 |
| LOCAL GOVERNMENT AUTHORITY<br>-                                                                                                 | POSTED SPEED<br>70-110km/h |
| ROAD AUTHORITY<br>MAIN ROADS WA                                                                                                 | WORKSITE SPEED<br>60km/h   |
| CHECKED BY<br>TYLER HARTLEY   | SIGNATURE<br>              |
| ACCREDITATION<br>RTM-0066   |                            |
| DESIGNED BY<br>MICHAEL REED   | SIGNATURE<br>              |
| ACCREDITATION<br>AWTM-23-11536-02                                                                                               |                            |
| GENERIC TRAFFIC GUIDANCE SCHEME<br>RAIL APPROACH SETUPS<br>STOP LINE & HATCHING REINSTATEMENT<br>WORKSITE BETWEEN 1.2M AND 3.0M |                            |
| DRAWING NO<br>0922-01531-RA-010                                                                                                 | REVISION<br>6              |