
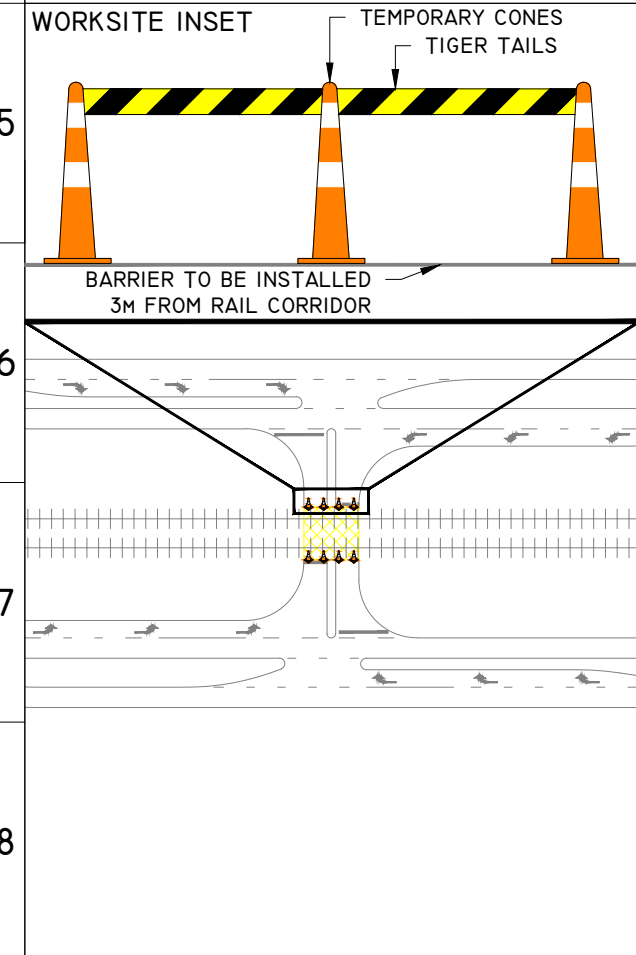


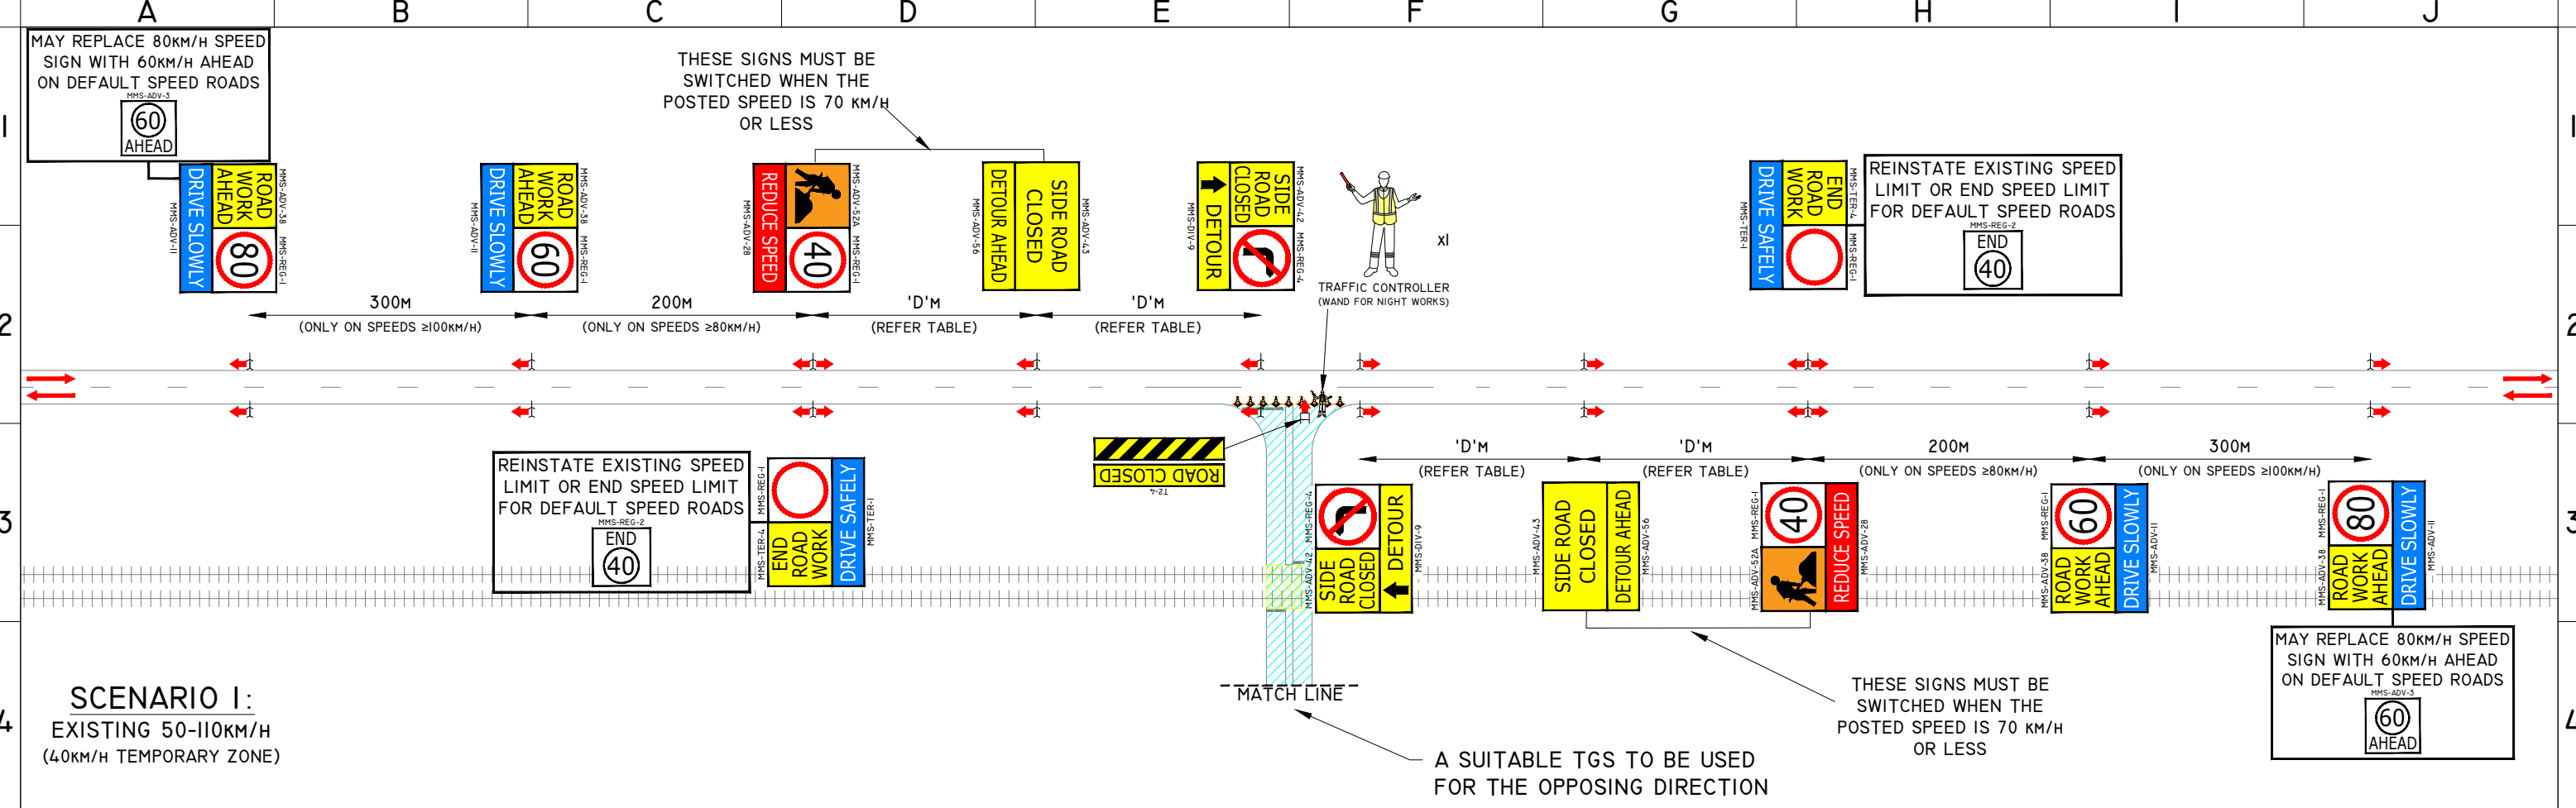

| TABLES                   |                                   |
|--------------------------|-----------------------------------|
| SIGN SPACING             |                                   |
| AGTTM PART 3 - TABLE 2.2 |                                   |
| SPEED LIMIT (KM/H)       | DISTANCE ('D') (M)                |
| 55 OR LESS               | 15                                |
| 56 TO 65                 | 45                                |
| GREATER THAN 65          | EQUAL TO SPEED OF TRAFFIC IN KM/H |

| NOTES   |   |
|---|---|
| <p><b>RECOMMENDED CONE SPACING</b><br/>AGTTM PART 3 - TABLE 5.3<br/>ALL PURPOSES:<br/>(≤ 50KM/H): 4M<br/>PROTECTING FRESHLY PAINTED LINES:<br/>(≤ 70KM/H): 24M</p> <p><b>RECOMMENDED LANE WIDTHS</b><br/>MAIN ROADS WA CoP SECTION 6.7 - TABLE 9<br/>RECOMMENDED LANE WIDTHS:<br/>≤ 60KM/H: 3.2M<br/>MINIMUM LANE WIDTHS:<br/>≤ 60KM/H: 3.0M</p> | <p><b>TOLERANCES</b><br/>POSITION OF SIGNS:<br/>MINIMUM 10% LESS THAN THE DISTANCE OR LENGTHS GIVEN.<br/>MAXIMUM 25% MORE THAN THE DISTANCES OR LENGTHS GIVEN.<br/>SPACING OF DELINEATING DEVICES:<br/>MAXIMUM 10% MORE THAN THE SPACING GIVEN.<br/>NO MINIMUM.</p> <p>AGTTM PART 6 SECTION 6.8.<br/><b>DOCUMENTATION</b><br/>ON-SITE VARIATIONS MUST BE APPROVED BY THE TRAFFIC MANAGEMENT SUPERVISOR, THAN AN ON-SITE VARIATION MADE AND CHANGES RECORDED IN THE DAILY DAIRY. FOR MORE INFORMATION REFER TO SECTION 9.3 OF THE TMP.</p> <ol style="list-style-type: none"><li>A RISK ASSESSMENT MUST BE CARRIED OUT TO DETERMINE THE REQUIREMENTS OF AFTERCARE.</li><li>ALL SIGN LOCATIONS ARE TO BE CHECKED ON SITE PRIOR TO SETOUT AND POSITIONS ADJUSTED AS PER THE 'TOLERANCES'.</li><li>ALL CONTRADICTORY SIGNS WITHIN THE TM SETUP TO BE COVERED BY SUITABLY OPAQUE MATERIAL.</li><li>FOR BOX EDGED SIGN ALTERNATIVES, CONSULT AWTM PRIOR TO IMPLEMENTATION.</li><li>WORKERS TO REMAIN 10m CLEAR OF RAILWAY TRACKS AT ALL TIMES.</li><li>ACCREDITED FLAG PERSON TO MONITOR AND WARN OF INCOMING TRAINS OVER TWO-WAY RADIO. TCs WILL HOLD ALL TRAFFIC TO ALLOW TRAIN TO PASS.</li><li>MAXIMUM LENGTH OF 40km/h TEMPORARY SPEED ZONE MUST BE 500M.</li><li>REFER TO SECTION 4.1.8 OF THE TMP FOR THE MANDATORY USE OF SPEED FEEDBACK SIGNAGE</li></ol> <p><b>PEDESTRIAN MANAGEMENT</b></p> <ol style="list-style-type: none"><li>'PEDESTRIAN WATCH YOUR STEP' SIGN TO BE INSTALLED ON EACH APPROACH WHERE WORKS MAY ENCROACH ONTO OR ADJACENT TO EXISTING FOOTPATH FACILITIES.</li><li>TM PERSONNEL TO MONITOR AND ESCORT PEDESTRIANS THROUGH THE WORK AREA AS REQUIRED.</li><li>PEDESTRIANS MAY BE HELD ON EITHER END OF THE WORKSITE UNTIL IT IS SAFE TO PASS AS REQUIRED.</li></ol> |