
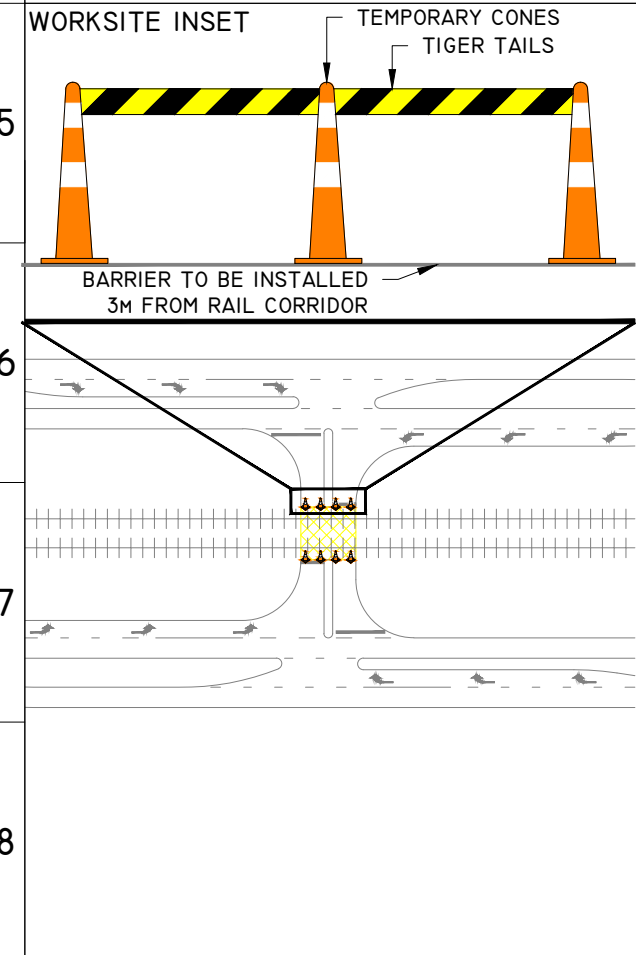


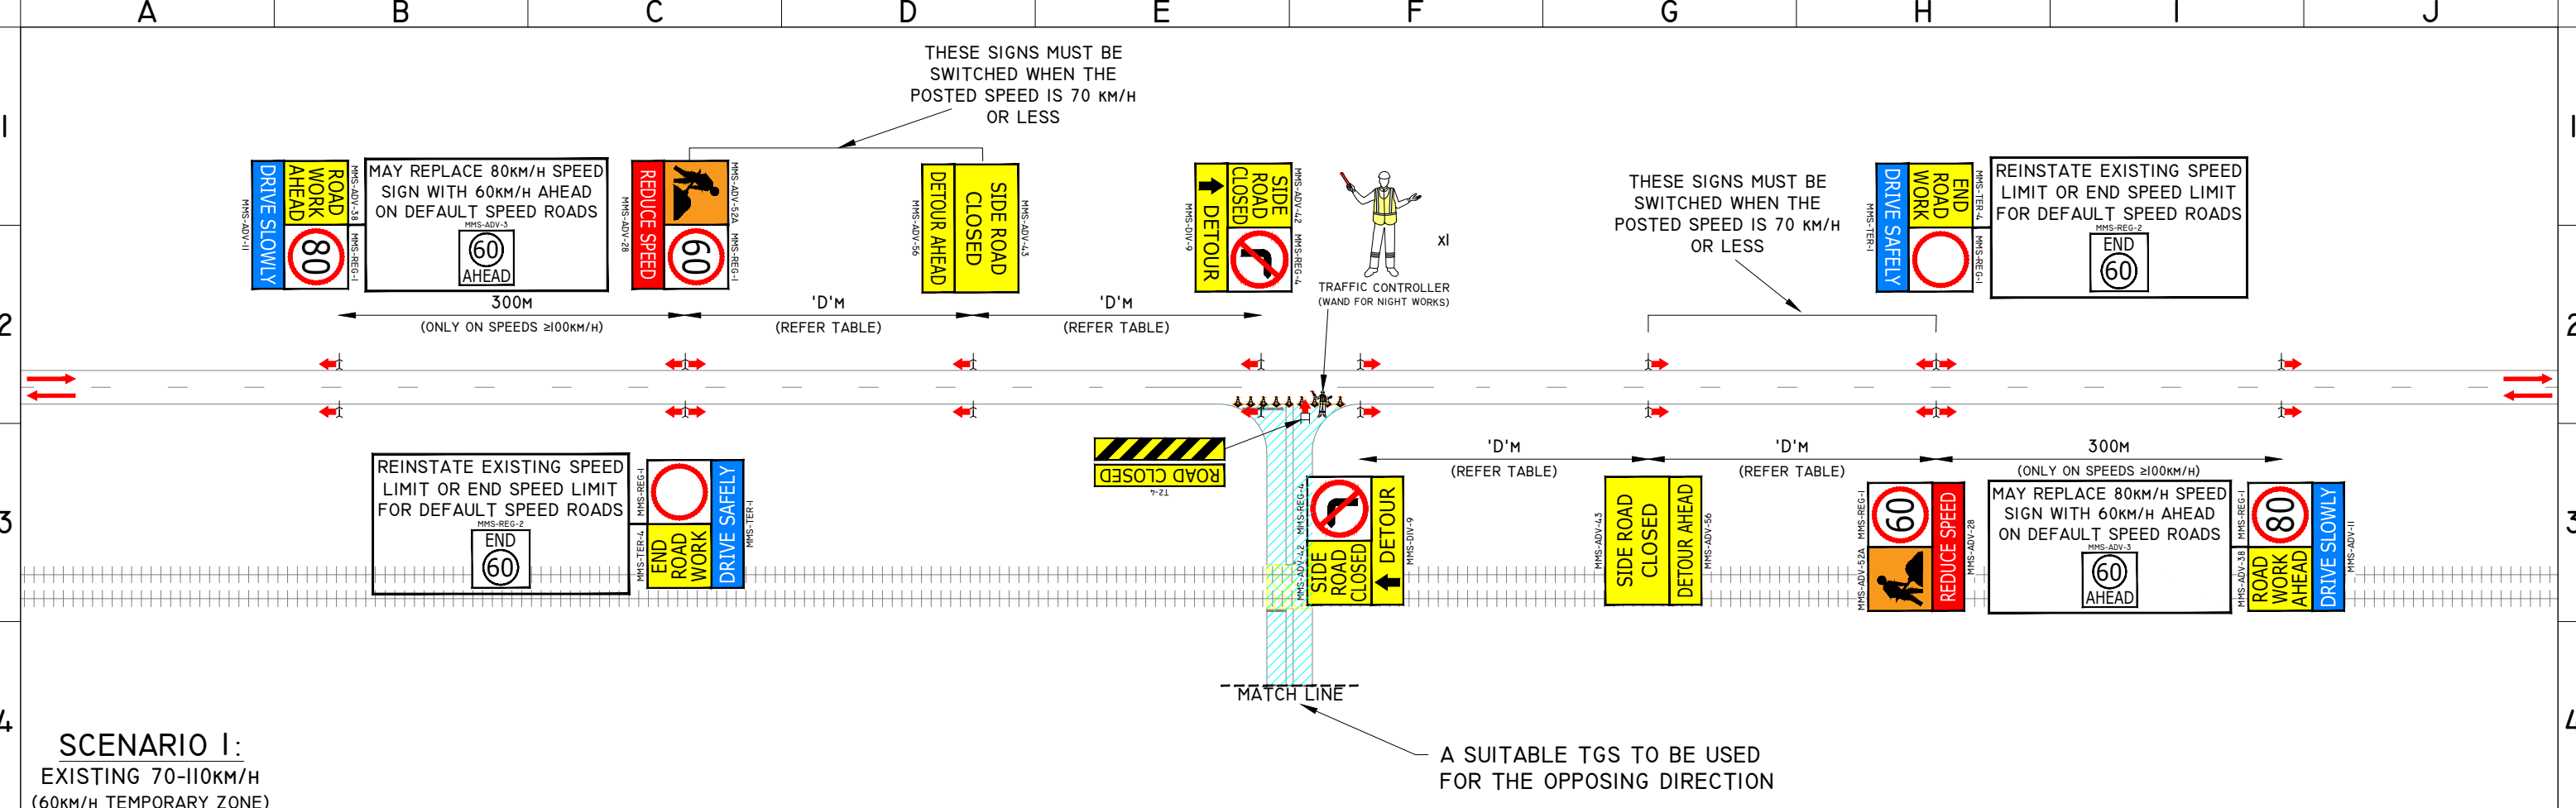

TABLES	
SIGN SPACING	
AGTTM PART 3 - TABLE 2.2	
SPEED LIMIT (KM/H)	DISTANCE ('D') (M)
55 OR LESS	15
56 TO 65	45
GREATER THAN 65	EQUAL TO SPEED OF TRAFFIC IN KM/H

NOTES

RECOMMENDED CONE SPACING
AGTTM PART 3 - TABLE 5.3
ALL PURPOSES:
(60 - 70KM/H): 12M
PROTECTING FRESHLY PAINTED LINES:
(≤ 70KM/H): 24M

RECOMMENDED LANE WIDTHS
MAIN ROADS WA CoP SECTION 6.7 - TABLE 9
RECOMMENDED LANE WIDTHS:
≤ 60KM/H: 3.2M
MINIMUM LANE WIDTHS:
≤ 60KM/H: 3.0M

TOLERANCES
POSITION OF SIGNS:
MINIMUM 10% LESS THAN THE DISTANCE OR LENGTHS GIVEN.
MAXIMUM 25% MORE THAN THE DISTANCES OR LENGTHS GIVEN.
SPACING OF DELINEATING DEVICES:
MAXIMUM 10% MORE THAN THE SPACING GIVEN.
NO MINIMUM.

AGTTM PART 6 SECTION 6.8.
DOCUMENTATION

ON-SITE VARIATIONS MUST BE APPROVED BY THE TRAFFIC MANAGEMENT SUPERVISOR, THAN AN ON-SITE VARIATION MADE AND CHANGES RECORDED IN THE DAILY DAIRY. FOR MORE INFORMATION REFER TO SECTION 9.3 OF THE TMP.

- A RISK ASSESSMENT MUST BE CARRIED OUT TO DETERMINE THE REQUIREMENTS OF AFTERCARE.
- ALL SIGN LOCATIONS ARE TO BE CHECKED ON SITE PRIOR TO SETOUT AND POSITIONS ADJUSTED AS PER THE 'TOLERANCES'.
- ALL CONTRADICTORY SIGNS WITHIN THE TM SETUP TO BE COVERED BY SUITABLY OPAQUE MATERIAL.
- FOR BOX EDGED SIGN ALTERNATIVES, CONSULT AWTM PRIOR TO IMPLEMENTATION.
- WORKERS TO REMAIN 10M CLEAR OF RAILWAY TRACKS AT ALL TIMES.
- ACCREDITED FLAG PERSON TO MONITOR AND WARN OF INCOMING TRAINS OVER TWO-WAY RADIO. TCs WILL HOLD ALL TRAFFIC TO ALLOW TRAIN TO PASS.
- REFER TO SECTION 4.1.8 OF THE TMP FOR THE MANDATORY USE OF SPEED FEEDBACK SIGNAGE

PEDESTRIAN MANAGEMENT

- 'PEDESTRIAN WATCH YOUR STEP' SIGN TO BE INSTALLED ON EACH APPROACH WHERE WORKS MAY ENCROACH ONTO OR ADJACENT TO EXISTING FOOTPATH FACILITIES.
- TM PERSONNEL TO MONITOR AND ESCORT PEDESTRIANS THROUGH THE WORK AREA AS REQUIRED.
- PEDESTRIANS MAY BE HELD ON EITHER END OF THE WORKSITE UNTIL IT IS SAFE TO PASS AS REQUIRED.